


I/16 MLADÁ BOLESLAV - MARTINOVICE
VÝKRES SVODIDEL km 0,000 - 2,500, M 1 : 2000



LEGENDA:

ÚROVEŇ ZADRŽENÍ

- SVODIDLO S ÚROVNÍ ZADRŽENÍ N2
- SVODIDLO S ÚROVNÍ ZADRŽENÍ H1
- SVODIDLO S ÚROVNÍ ZADRŽENÍ H2
- SVODIDLO S ÚROVNÍ ZADRŽENÍ H3

ZNAČKA NA VÝKRESU

- SVODIDLO OCELOVÉ JEDNOSTRANNÉ
- SVODIDLO OCELOVÉ OBOUSTRANNÉ
- SVODIDLO BETONOVÉ JEDNOSTRANNÉ
- SVODIDLO BETONOVÉ OBOUSTRANNÉ
- SVODIDLO DEMONTOVATELNÉ

TYP SVODIDLA

- JSO - JEDNOSTRANNÉ OCELOVÉ
- JSB - JEDNOSTRANNÉ BETONOVÉ
- OSO - OBOUSTRANNÉ OCELOVÉ
- OSB - OBOUSTRANNÉ BETONOVÉ
- JSOM - JEDNOSTRANNÉ OCELOVÉ MOSTNÍ
- JSBM - JEDNOSTRANNÉ BETONOVÉ MOSTNÍ
- OSOM - OBOUSTRANNÉ OCELOVÉ MOSTNÍ
- OSBM - OBOUSTRANNÉ BETONOVÉ MOSTNÍ
- DEM - LEHCE DEMONTOVATELNÉ

120 - VÝŠKA BETONOVÉHO SVODIDLA

Souřadnicový systém: S-JTSK
Výškový systém: Bpv

C Situační výkresy

Objednatel:

Ředitelství silnic a dálnic s. p.
Čerčanská 2023/12, Krč, 140 00 Praha 4

Zhotovitel:

Valbek, spol. s r.o.
Vaňurova 505/17
460 07 Liberec 3

Vypracoval	ING. M. HRUBOŘ	Zak. číslo	21-1113-001
Zodp. projektant	ING. T. KLIMENT	Datum	02/2025
Tech. kontrola	ING. M. HANŽL	Stupeň	PPPS
Akce	I/16 MLADÁ BOLESLAV - MARTINOVICE	Počet formátů	12 x A4
		Měřítko	1:2000
		Č. přílohy	Paré

Zhotovitel:

Valbek, spol. s r.o.
Vaňurova 505/17
460 07 Liberec 3

Příloha

VÝKRES SVODIDEL km 0,000 - 2,500

C.3.1