


I/16 MLADÁ BOLESLAV - MARTINOVICE
VÝKRES SVODIDEL km 5,500 - 8,200, M 1 : 2000

 

LEGENDA:

ÚROVEŇ ZADRŽENÍ

- SVODIDLO S ÚROVNÍ ZADRŽENÍ N2
- SVODIDLO S ÚROVNÍ ZADRŽENÍ H1
- SVODIDLO S ÚROVNÍ ZADRŽENÍ H2
- SVODIDLO S ÚROVNÍ ZADRŽENÍ H3

ZNAČKA NA VÝKRESU

————	SVODIDLO OCELOVÉ JEDNOSTRANNÉ
=====	SVODIDLO OCELOVÉ OBOUSTRANNÉ
- - - - -	SVODIDLO BETONOVÉ JEDNOSTRANNÉ
= = = = =	SVODIDLO BETONOVÉ OBOUSTRANNÉ
~~~~~	SVODIDLO DEMONTOVATELNÉ

**TYP SVODIDLA**


JSO - JEDNOSTRANNÉ OCELOVÉ  
JSB - JEDNOSTRANNÉ BETONOVÉ  
OSO - OBOUSTRANNÉ OCELOVÉ  
OSB - OBOUSTRANNÉ BETONOVÉ  
JSOM - JEDNOSTRANNÉ OCELNOVÉ MOSTN  
JSBM - JEDNOSTRANNÉ BETONOVÉ MOSTN  
OSOM - OBOUSTRANNÉ OCELNOVÉ MOSTN  
OSBM - OBOUSTRANNÉ BETONOVÉ MOSTN

120 - VÝŠKA BETONOVÉHO SVODIDLA

Souřadnicový systém: S-JTSK  
Výškový systém: Bpv

<b>C</b>	Situační výkresy
----------	------------------

Objednatel:

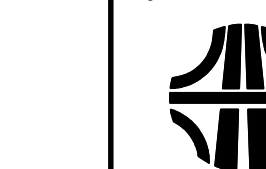

**Ředitelství silnic a dálnic s. p.**  
Čerčanská 2023/12, Krč. 140 00 Praha 4

Zhotovitel:

**Valb**

**Valbek, spol. s r.o.**  
Vaňurova 505/17  
460 07 Liberec 3



Vypracoval	ING. M. HRUBOŇ	
Zodp. projektant	ING. T. KLIMENT	
Tech. kontrola	ING. M. HANŽL	
Akce		
I/16 MLADÁ BOLESLAV - MARTINOV		

Zak. číslo	21-LI13-001
------------	-------------

	Datum	02/2025
--	-------	---------

	Stupeň	PDPS
	1	1

Počet formátů	12 x A4
Měřítko	1 : 2000

Č. přílohy	Paré
------------	------

[illegible]

**C.3.3**

1	2	
---	---	---	---	---	---	---	---	---	----	----	-----	-----	

---