


I/16 MLADÁ BOLESLAV - MARTINOVICE
KOORDINAČNÍ SITUACE km 2,500 - 5,500, M 1:2 000



OCHRANNÁ PÁSMA:
I. ZAKRESY INŽENÝRSKÝCH SÍTÍ:
JSOU PROVÁDĚNY DLE POHLEDU PŘÍSLUŠNÝCH SPRÁVČŮ.
PŘED ZAHAJENÍM STAVEBNÍCH PRACÍ JE NUTNÉ JEJICH OVĚŘENÍ A VYTÝČENÍ
V CELÉM ZÁJMOVÉM ÚZEMÍ DLE STAVBY.

II. OCHRANNÁ A BEZPEČNOSTNÍ PÁSMA:
Ochranná pásma silnic a dálnic jsou dle zákona č. 13/1997 Sb. § 330 následující:
DALNICE, RYCHLOSTNÍ MK: 100 m (od osy přílehlého (jízdního pásu nebo osy vjevu)
SILNICE I. TR., MK I. TRIDY: 50 m (od osy vozovky nebo osy přílehlého (jízdního pásu)
SILNICE II. A III. TR. a MK II. TR.: 15 m (od osy vozovky nebo osy přílehlého (jízdního pásu)

Ochranná pásma drah jsou dle zákona č. 266/1994 Sb. § 88 následující:
CELOSTATNÍ DRAHA, REGIONÁLNÍ: 60 m (od osy krajní koleje)
(nejméně však 30 m od hrane obvodu dráhy)

Ochranná pásma lesa
POZEMEK LESA: 50 m (od okraje lesa)

Ochranná pásma stávajících vedení jsou dle zákona č. 458/2000 Sb. § 46 následující:
Elektro mastrzení vedení
NAPĚTÍ DO 1 kV: 1 m (od krajního vodiče)
- PRO VODIČE BEZ IZOLACE: 7 m (od krajního vodiče)
- PRO VODIČE S IZOLACÍ ZÁKLADNÍ: 2 m (od krajního vodiče)
- PRO ZÁVĚSNÁ KABELOVÁ VEDENÍ: 1 m (od krajního vodiče)
NAPĚTÍ NAD 1 kV DO 35 kV VČETNĚ: 12 m (od krajního vodiče)
- PRO VODIČE BEZ IZOLACE: 5 m (od krajního vodiče)
- PRO VODIČE S IZOLACÍ ZÁKLADNÍ: 15 m (od krajního vodiče)
NAPĚTÍ NAD 110 kV DO 220 kV VČETNĚ: 20 m (od krajního vodiče)
NAPĚTÍ NAD 220 kV DO 400 kV VČETNĚ: 30 m (od krajního vodiče)
NAPĚTÍ NAD 400 kV: 2 m (od krajního vodiče)
U ZÁVĚSNÉHO KABELOVÉHO VEDENÍ 110 kV:
Elektro podzemní vedení: 1,5 m (od krajního kabelu)
SĚLOVACÍ KABELOVÁ VEDENÍ MÍSTNÍ (DÁLKOVÁ): 1 m (po obou stranách krajního kabelu)
SILNOPROUDÁ VEDENÍ DO 110 kV VČETNĚ: 3 m (po obou stranách krajního kabelu)
SILNOPROUDÁ VEDENÍ NAD 110 kV VČETNĚ: 3 m (po obou stranách krajního kabelu)

Ochranná pásma vodovodních řádů a kanalizačních stok jsou dle zákona č. 274/2001 Sb. § 233 následující:
VODOVODNÍ POTRUBÍ DO DN 500 VČETNĚ: 1,5 m (od okraje potrubí)
VODOVODNÍ POTRUBÍ NAD DN 500: 2,5 m (od okraje potrubí)
KANALIZACE DO DN 500 VČETNĚ: 1,5 m (od okraje stoky)
KANALIZACE NAD DN 500: 2,5 m (od okraje stoky)
VODOVODNÍ POTRUBÍ A KANALIZACE NAD DN 200: 2,5 m (od okraje stoky)
ULOŽENÉ V HLUBCE VĚTŠÍ NEŽ 2,5m: ZVĚTŠUJE SE OCHRANNÉ PÁSMA O 1 m

Ochranná pásma plynárenských zařízení jsou dle zákona č. 458/2000 Sb. § 68 následující:
NTL, STL A PŘÍPOJKY PLYNOVODU V ZAST. ÚZEMÍ: 1 m (od podorysu)
OSTATNÍ PLYNOVODY A PŘÍPOJKY: 4 m (od podorysu)
TECHNICKÉ OBJEKTY: 4 m (od podorysu)

LEGENDA:

PLOCHY	NOVÉ IS
VOZOVKA - ASFALTOVÝ KRYT	DEŠŤOVÁ KANALIZACE
VOZOVKA - FRÉZOVANÁ	MELIORACE
VOZOVKA - CYKLISTICKÁ STEZKA	VÝTLAK
VOZOVKA - POLNÍ CESTY	VODOVOD
CHODNÍK	NADZEMNÍ VEDENÍ NN
DLAŽBA VOZOVKY	PODZEMNÍ VEDENÍ NN
SVAHY VÝKOPU	PODZEMNÍ VEDENÍ VN
SVAHY NÁSPYU	NADZEMNÍ VEDENÍ VN
VEGETAČNÍ ÚPRAVY	DEŠŤOVÁ KANALIZACE
	PLYNOVOD - STL
	PODZEMNÍ SĚLOVACÍ VEDENÍ
	PLYNOVOD - STL
	VODOVOD

KATASTR NEMOVITOSTÍ

HRANICE K.Ú.	PODZEMNÍ VEDENÍ NN
HRANICE PARCEL	PODZEMNÍ VEDENÍ VN
TRVALÝ ZÁBOR	NADZEMNÍ VEDENÍ VN
DOČASNÝ ZÁBOR DO 1 ROKU	DEŠŤOVÁ KANALIZACE
	PLYNOVOD - STL
	PODZEMNÍ SĚLOVACÍ VEDENÍ
	VODOVOD

Souřadnicový systém: S-JTSK
Výškový systém: Bpv

C Situační výkresy

Objednatel: ŘEDITELSTVÍ SILNIC A DÁLNIC
Ředitelství silnic a dálnic s. p.
Čerčanská 2023/12, Krč, 140 00 Praha 4

Zhotovitel: Valbek, spol. s r.o.
Valbuřova 505/17
460 07 Liberec 3
HP: ING. T. KLIMENT

Vypracoval: ING. M. HRUBOŠ	Zak. číslo: 21-113-001
Zodp. projektant: ING. T. KLIMENT	Datum: 02/2025
Tech. kontrola: ING. M. HANZL	Stupeň: PDPS
Akce: I/16 MLADÁ BOLESLAV - MARTINOVICE	Počet formátů: 18 x A4
	Měřítko: 1:2 000
	Č. přílohy: Para

Zhotovitel: Valbek, spol. s r.o.
Valbuřova 505/17
460 07 Liberec 3
Příloha: KOORDINAČNÍ SITUACE km 2,500 - 5,500
C.2.2

SEZNAM SO:
SEZNAM SO: 1. Připrava území
SO 020 Připrava území
SO 101 Silnice I/16 Mladá Boleslav - Martinovice
SO 111 Nadjezd MUK Židněves
SO 112 MUK Martinovice
SO 121 Přeložka silnice III/2768 v km 2,200
SO 122 Přeložka silnice III/27612 v km 6,080
SO 123 Přeložka místní komunikace v km 0,228
SO 124 Přeložka místní komunikace km 7,320 i 835 vlevo
SO 125 Napojení původní I/16 do MUK Židněves
SO 126 Napojení původní I/16 do MUK Martinovice
SO 127 Napojení ČSPH na silnici I/16
SO 128 Občanská BUS Martinovice
SO 129 Přeložka místní komunikace v km 1,713
SO 140 Přjezd k DUN v km 0,170
SO 141 Přjezd k DUN v km 0,390
SO 142 Přjezd k DUN v km 0,720
SO 143 Přjezd k DUN v km 1,500
SO 144 Přjezd k DUN v km 2,600
SO 145 Přjezd k DUN v km 2,760
SO 146 Přjezd k DUN v km 4,940
SO 147 Přjezd k DUN v km 5,130
SO 148 Přjezd k DUN v km 5,450
SO 149 Přjezd k DUN v km 5,450
SO 150 Přístup na pozemky v k.ú. Kosmonosy
SO 151 Přístup na pozemky v k.ú. Plázy
SO 152 Přístup na pozemky v k.ú. Židněves
SO 153 Přístup na pozemky v k.ú. Sukorady u Mladé Boleslavi
SO 154 Přeložka polní cesty v km 6,700
SO 171 Provizní přeložka I/16
SO 180 Přeložka dopravní značení
SO 190 Dopravní značení
SO 201 Most na I/16 přes MK a železniční vodotěs v km 0,228
SO 202 Most na I/16 přes Valskou vodotěs v km 2,695
SO 203 Most na I/16 přes přeložku polní cesty v km 3,790
SO 204 Most na I/16 přes Sukoradskou stáku v km 5,048
SO 205 Most na I/16 přes přeložku III/27612 v km 6,080
SO 206 Most na I/16 přes přeložku polní cesty v km 6,700
SO 207 Most na I/16 přes Přeložku potok v km 7,370
SO 221 Nadjezd přeložky III/2768 v km 2,200
SO 222 Nadjezd MUK Židněves v km 4,705
SO 223 Nadjezd MUK Martinovice v km 7,320
SO 230 Nadjezd v km 1,713
SO 301 Odvození I/16
SO 311 Odvození MUK Židněves
SO 312 Odvození MUK Martinovice
SO 320 Úprava vodního toku Ot Stákor
SO 321 Úprava HOZ 1 v km 0,554
SO 322 Úprava HOZ 2 v km 1,480
SO 323 Úprava Valské vodotěs
SO 324 Úprava HOZ 3 v km 3,980
SO 325 Úprava koryta v km 4,210
SO 326 Úprava Sukoradské stáky
SO 327 Úprava HOZ 5A a 6 v km 7,080
SO 328 Úprava HOZ 7 a 8 v km 7,730
SO 329 Úprava Přeložky potoka
SO 341 Přeložka vodovodu PE 110 v km 2,195
SO 342 Přeložka vodovodu PVC 225 v MUK Židněves
SO 343 Přeložka vodovodu PVC 150 v km 6,091
SO 344 Přeložka vodovodu v MUK Martinovice
SO 360 DUK a retenční nádrž na I/16
SO 380 Úpravy meliorací ŽU - KU
SO 390 Zřízení náhradních vodních zdrojů
SO 401 Úprava vedení VVN, km 0,602
SO 410 Přeložka vrchního vedení 22kV km 0,200
SO 411 Přeložka vrchního vedení 22 kV km 0,533
SO 412 Přeložka vrchního vedení 22 kV km 5,560 - 5,885
SO 413 Přeložka síťového transformátoru 22 kV, km 6,060
SO 430 Přeložka kabelových vedení NN km 6,075
SO 431 Přeložka kabelových vedení NN km 7,480 - 7,530
SO 432 Přeložka kabelového vedení NN km 7,845
SO 433 Vělepné osvětlení Martinovice
SO 434 Přeložka NN sdělných zařízení km 7,785
SO 450 Přeložka vedení SEK - DOK CETIN km 2,170
SO 460 Přeložka vedení SEK CETIN km 4,500 - 5,150
SO 461 Přeložka vedení SEK CETIN km 6,080
SO 462 Přeložka vedení SEK CETIN km 7,200 - 7,545
SO 463 Přeložka vedení SEK CETIN km 8,170
SO 466 Automatický sčítací dopravy
SO 500 Přeložka STL, příjezd v km 2,225
SO 760 Protihluková stěna v km 6,100 vlevo
SO 761 Protihluková stěna v km 7,600 vlevo
SO 801 Vegetační úpravy
SO 810 Kámen zelený
SO 830 Rekultivace ploch dočasného záboru
SO 860 Oplotení

POZNÁMKA:
ŠEDOU BARVOU JE VYZNAČEN SEZNAM SOUVISEJÍCÍCH STAVEBNÍCH OBJEKTŮ PROJEKTOVOU DOKUMENTACÍ, INŽENÝRSKOU ČINNOSTÍ PRO STAVEBNÍ ŘÍZENÍ A REALIZACI ZAJIŠTJUE ČEZ DISTRIBUCE, a.s.)