


I/16 MLADÁ BOLESLAV - MARTINOVICE
KOORDINAČNÍ SITUACE km 5,500 - 8,200, M 1:2 000

 

OCHRANNÁ PÁSMA:
I. ZÁKRESY INŽENÝRSKÝCH SÍTÍ:
JEDNÍ PROVĚŘENÝ DLE PODKLADU PŘÍSLUŠNÝCH SPRÁVCŮ.
PŘED ZAHÁJENÍM STAVEBNÍCH PRACÍ JE NUTNÉ JEJICH OVĚŘENÍ A VYTYČENÍ
V CELEM ZÁJMOVÉM ÚZEMÍ DLE STAVBY.
II. OCHRANNÁ A BEZPEČNOSTNÍ PÁSMA:
Ochranná pásma silnic a dálnic jsou dle zákona č. 13/1997 Sb. § 330 následující:
DÁLNIČE, RYCHLOSTNÍ MK: 100 m (od osy přílehleho jízdního pásu nebo osy větvě)
SILNICE I. TR., MK I. TRIDY: 50 m (od osy vozovky nebo osy přílehleho jízdního pásu)
SILNICE II. A III. TR. A MK II. TR.: 15 m (od osy vozovky nebo osy přílehleho jízdního pásu)

Ochranná pásma dráhy jsou dle zákona č. 266/1994 Sb. § 88 následující:
CELOSTÁTNÍ DRÁHA, REGIONÁLNÍ: 60 m (od osy krajní koleje)
(nejméně však 30 m od hranice obvodu dráhy)

Ochranná pásma lesa:
POZEMEK LESÁ: 50 m (od okraje lesa)
Elektro nadzemní vedení:
NAPĚTÍ DO 1 kV: 1 m (od krajního vodiče)
NAPĚTÍ NAD 1 kV DO 35 kV VČETNĚ: 7 m (od krajního vodiče)
PRO VODIČE BEZ IZOLACE: 2 m (od krajního vodiče)
PRO ZÁVĚSNÁ KABELOVÁ VEDENÍ: 1 m (od krajního vodiče)
NAPĚTÍ NAD 35 kV DO 110 kV VČETNĚ: 12 m (od krajního vodiče)
PRO VODIČE BEZ IZOLACE: 5 m (od krajního vodiče)
NAPĚTÍ NAD 110 kV DO 220 kV VČETNĚ: 15 m (od krajního vodiče)
NAPĚTÍ NAD 220 kV DO 400 kV VČETNĚ: 20 m (od krajního vodiče)
NAPĚTÍ NAD 400 kV: 30 m (od krajního vodiče)
U ZÁVĚSNÉHO KABELOVÉHO VEDENÍ 110 kV: 2 m (od krajního vodiče)

Elektro podzemní vedení:
SĚLOVACÍ KABELOVÁ VEDENÍ MÍSTNÍ I DÁLKOVÁ: 1,5 m (od krajního kabelu)
SILNOPROUDÁ VEDENÍ DO 110 kV VČETNĚ: 1 m (po obou stranách krajního kabelu)
SILNOPROUDÁ VEDENÍ NAD 110 kV VČETNĚ: 3 m (po obou stranách krajního kabelu)

Ochranná pásma vodovodních řadů a kanalizačních stok jsou dle zákona č. 274/2001 Sb. § 243 následující:
VODOVODNÍ POTRUBÍ DO DN 500 VČETNĚ: 1,5 m (od okraje potrubí)
VODOVODNÍ POTRUBÍ NAD DN 500: 2,5 m (od okraje potrubí)
KANALIZACE NAD DN 500: 2,5 m (od okraje stoky)
VODOVODNÍ POTRUBÍ A KANALIZACE NAD DN 200: 4 m (od potrubí)
ULOŽENÉ V HLoubCE VĚTŠÍ NEŽ 2,5 m: ZVĚTŠUJE SE OCHRANNÉ PÁSMA O 1 m

Ochranná pásma plynárenských zařízení jsou dle zákona č. 458/2000 Sb. § 68 následující:
NTL, STL A PŘÍPOJKY PLYNOVODŮ V ZAST. ÚZEMÍ: 1 m (od potrubí)
OSTATNÍ PLYNOVODY A PŘÍPOJKY: 4 m (od potrubí)
TECHNOLIGICKÉ OBJEKTY: 4 m (od potrubí)

SEZNAM SO:
SO 001 Demolice autobusové zastávky, Sukorady
SO 020 Příprava území
SO 101 Silnice I/16 Mladá Boleslav - Martinovice
SO 111 MUK Židněves
SO 112 MUK Martinovice
SO 121 Přeložka silnice III/2768 v km 2,200
SO 122 Přeložka silnice III/27612 v km 6,080
SO 123 Přeložka místní komunikace v km 0,228
SO 124 Přeložka místní komunikace km 7,320-7,335 vlevo
SO 125 Napojení povodní I/16 do MUK Židněves
SO 126 Napojení povodní I/16 do MUK Martinovice
SO 127 Napojení ČSPH na silnici I/16
SO 128 Obrátště BUS Martinovice
SO 130 Přeložka místní komunikace v km 1,713
SO 140 Přijezd k DUN v km 0,170
SO 141 Přijezd k DUN v km 0,380
SO 142 Přijezd k DUN v km 0,720
SO 143 Přijezd k DUN v km 1,980
SO 144 Přijezd k DUN v km 2,600
SO 145 Přijezd k DUN v km 2,780
SO 146 Přijezd k DUN v km 4,940
SO 147 Přijezd k DUN v km 5,130
SO 148 Přijezd k DUN v km 7,450
SO 150 Přilupy na pozemky v k.ú. Kosmonosy
SO 151 Přilupy na pozemky v k.ú. Plaz
SO 152 Přilupy na pozemky v k.ú. Židněves
SO 153 Přilupy na pozemky v k.ú. Sukorady u Mladé Boleslavi
SO 154 Přeložka polní cesty v km 6,700
SO 171 Provizorní přeložka I/16
SO 180 Přeložka dopravního zřízení
SO 190 Dopravní zřízení
SO 201 Most na I/16 přes MK a Zašuzanskou vodotěs v km 0,228
SO 202 Most na I/16 přes Váňskou vodotěs v km 2,695
SO 203 Most na I/16 přes přeložku polní cesty v km 3,700
SO 204 Most na I/16 přes Sukoradskou stoku v km 5,048
SO 205 Most na I/16 přes přeložku III/27612 v km 6,080
SO 206 Most na I/16 přes přeložku polní cesty v km 6,700
SO 207 Most na I/16 přes Přepírský potok v km 7,870
SO 221 Nadjezd přeložky III/2768 v km 2,200
SO 222 Nadjezd MUK Židněves v km 4,705
SO 223 Nadjezd MUK Martinovice v km 7,320
SO 230 Nadjezd v km 1,713
SO 301 Odvodnění I/16
SO 311 Odvodnění MUK Židněves
SO 312 Odvodnění MUK Martinovice
SO 320 Úprava vodního toku Od Stákor
SO 321 Úprava HOZ 1 v km 0,854
SO 322 Úprava HOZ 2 v km 1,480
SO 323 Úprava Váňské vodotěs
SO 324 Úprava HOZ 3 v km 3,080
SO 325 Úprava koryta v km 4,210
SO 326 Úprava Sukoradské stoky
SO 327 Úprava HOZ 5A a 6 v km 7,080
SO 328 Úprava HOZ 7 a 8 v km 7,730
SO 329 Úprava Přepírského potoka
SO 341 Přeložka vodotěs PE 110 v km 2,195
SO 342 Přeložka vodotěs PVC 225 v MUK Židněves
SO 343 Přeložka vodotěs PVC 160 v km 6,091
SO 344 Přeložka vodotěs PVC 160 v MUK Martinovice
SO 360 DUN a rekonstrukce nájezdu na I/16
SO 380 Úpravy meliorací ŽU - KU
SO 380 Zřízení nájezdových vodních zábran
SO 401 Úprava vedení VVN, km 0,602
SO 410 Přeložka vnitřního vedení 22 kV km 0,200
SO 411 Přeložka vnitřního vedení 22 kV km 0,333
SO 412 Přeložka vnitřního vedení 22 kV km 5,560 - 5,585
SO 413 Přeložka státního vedení 22 kV km 6,000
SO 430 Přeložka kabelových vedení NN km 6,075
SO 431 Přeložka kabelových vedení NN km 7,480 - 7,530
SO 432 Přeložka kabelových vedení NN km 7,845
SO 433 Vnější osvětlení Martinovice
SO 434 Přilupa NŘ silničního zařízení km 7,785
SO 450 Přeložka vedení SEK - DOK CETIN km 2,170
SO 460 Přeložka vedení SEK CETIN km 5,950 - 5,100
SO 461 Přeložka vedení SEK CETIN km 6,095
SO 462 Přeložka vedení SEK CETIN km 7,250 - 7,545
SO 463 Přeložka vedení SEK CETIN km 2,170
SO 496 Automatický sčítací dopravy
SO 500 Přeložka STL železnice v km 2,205
SO 760 Protihluková stěna v km 6,100 vlevo
SO 761 Protihluková stěna v km 7,600 vlevo
SO 801 Vegetační úpravy
SO 810 Kácení zeleně
SO 830 Rekonstrukce ploch dočasného záboru
SO 860 Osvícení

POZNAMKA:
ŠEDOU BARVOU JE VYZNAČEN SEZNAM SOUVISEJÍCÍCH STAVEBNÍCH OBJEKTŮ (PROJEKTOVOU DOKUMENTACI, INŽENÝRSKOU ČINNOST PRO STAVEBNÍ ŘÍZENÍ A REALIZACI ZAJIŠŤUJE ČEZ DISTRIBUCE, a.s.)

LEGENDA:

PLOCHY

- VOZOVKA - ASFALTOVÝ KRYT
- VOZOVKA - FRÉZOVANÁ
- VOZOVKA - CYKLISTICKÁ STEZKA
- VOZOVKA - POLNÍ CESTY
- CHODNÍK
- DLAŽBA VOZOVKY
- SVAHY VÝKOPU
- SVAHY NÁSPYPU
- VEGETAČNÍ ÚPRAVY

NOVÉ IS

- DEŠŤOVÁ KANALIZACE
- MELIORACE
- VÝTLAK
- VODOVOD
- NADZEMNÍ VEDENÍ NN
- PODZEMNÍ VEDENÍ NN
- PODZEMNÍ SĚLOVACÍ VEDENÍ
- PLYNOVOD - STL

STÁVAJÍCÍ IS - INFORMATIVNÍ ZÁKRES

- PODZEMNÍ VEDENÍ NN
- PODZEMNÍ VEDENÍ NN
- NADZEMNÍ VEDENÍ NN
- NADZEMNÍ VEDENÍ VVN
- DEŠŤOVÁ KANALIZACE
- PLYNOVOD - STL
- PODZEMNÍ SĚLOVACÍ VEDENÍ
- VODOVOD

KATASTR NEMOVITOSTÍ


- HRANICE K.Ú.
- HRANICE PARCEL
- TRVALÝ ZÁBOR
- DOČASNÝ ZÁBOR DO 1 ROKU

Souřadnicový systém: S-JTSK

Výškový systém: Bpv


C Situační výkresy

Objednatel:

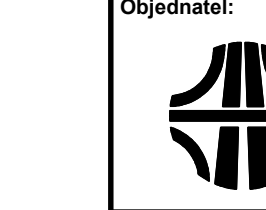

Ředitelství silnic a dálnic s. p.
Čerňanská 2023/12, Krč, 140 00 Praha 4

Zhotovitel:

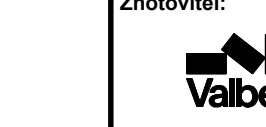

Valbek, spol. s r.o.
Vahurova 505/17
460 07 Liberec 3

HIP: ING. T. KLIMENT

Vypracoval:

Zodp. projektant:

Tech. kontrola:

Akce

I/16 MLADÁ BOLESLAV - MARTINOVICE

KOORDINAČNÍ SITUACE km 5,500 - 8,200

Příloha

Zhotovitel:

Valbek, spol. s r.o.

Vahurova 505/17

460 07 Liberec 3

Zak. číslo

Datum

Stupeň

Počet formátů

Měřítko

C. přílohy

Paré

C.2.3