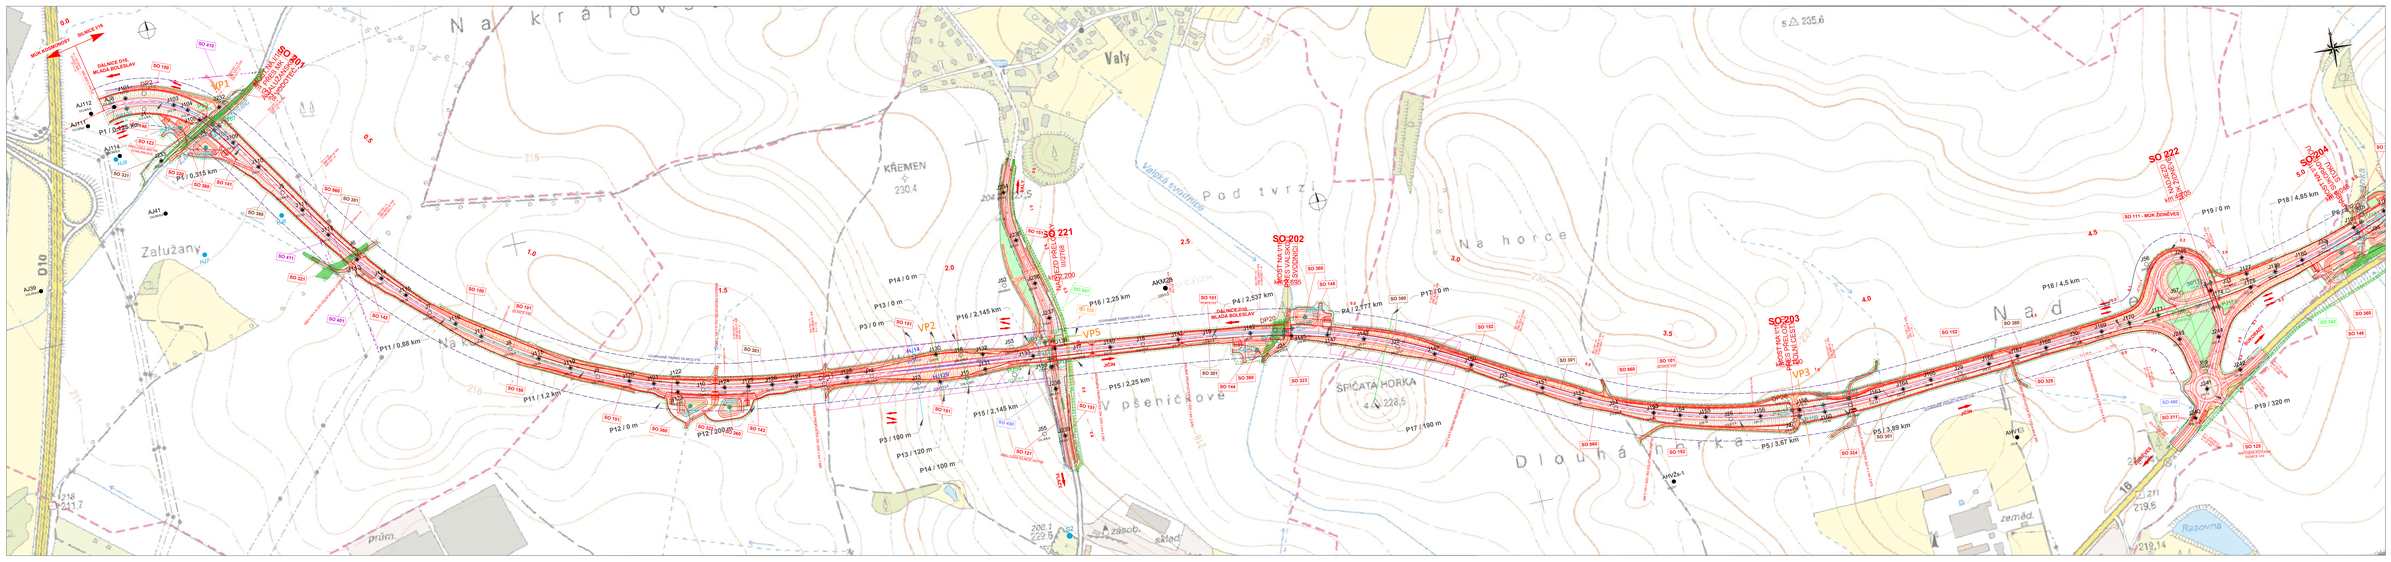

0.0
MÚK KOSMONOSY
SILNICE I/16
DÁLNICE D10, MLADÁ BOLESLAV
SO 150
SO 410
SO 201
MOST NA I/16 PŘES MK ZALUŽANSKOU VODOTEČ
VP1
DP2
AJ8
J101
AJ112
AJ111
J103
J104
J1
SP102
J232
PJ3
J105
PJ107
J4
SP108
J109
P1 / 0,125 km
SO 140
SO 123
PŘELOŽKA MÍSTNÍ KOMUNIKACE
AJ114
HJ9
J233
SO 331
SO 320
P1 / 0,315 km
SO 360
SO 141
J110
J5
SO 860
SO 301
J111
SO 380
HJ6
AJ41
J112
J6
SO 411
J113
J114
SO 321
Zalužany
HJ7
D10
AJ39
0.5
1.0
1.5
Na královské
KŘEMEN 230,4
J116
J7
SO 142
SO 401
P11 / 0,88 km
J117
J8
J118
J119
SO 150
SO 101
P11 / 1,2 km
OCHRANNÉ PÁSMO SILNICE I/16
J9
J120
J121
J122
J10
J123
J124
J125
J126
J127
SO 151
P12 / 0 m
SO 360
SO 322
P12 / 200 m
SO 143
RÁMOVÝ PROPUSTEK 2x2 m v km 1,480
TRUBNÍ PROPUSTEK DN 1200 v km 1,680
DP11
J128
J12
P14 / 0 m
P13 / 0 m
P3 / 0 m
SO 151
VP2
HJ14
J130
J16
J132
J53
J13
HJ129
J15
J131
PJ54
P3 / 100 m
P13 / 120 m
P14 / 100 m
2.0
Valy
J234
VALY
SO 151
SO 221
NÁJEZD PŘELOŽKY III/2768
km 2,200
J235
J236
J52
SO 341
SO 520
VP5
J237
J133
J136
J188
J17
J238
P16 / 2,145 km
P16 / 2,25 km
P15 / 2,145 km
P15 / 2,25 km
SO 450
J55
J239
SO 121
PŘELOŽKA SILNICE III/2768
PLAZY
JIČÍN
MIGRAČNÍ PROPUSTEK DN 1200 v km 2,280
AKM28
J140
J18
J141
J19
J142
DP20
SO 101
SO 301
P4 / 2,537 km
TRUBNÍ PROPUSTEK DN 1200 v km 2,470
V pšeničkové
Valská svodnice
Pod tvrzí
2.5
SO 202
MOST NA I/16 PŘES VALSKOU SVODNICI
km 2,695
SO 360
SO 145
SO 144
SO 323
J145
J21
P4 / 2,777 km
SO 380
P17 / 0 m
P17 / 190 m
J147
J148
J22
J149
J150
ŠPIČATÁ HORKA 228,5
Na horce
3.0
3.5
SO 152
SO 301
SO 860
SO 101
J23
J151
J152
J24
J153
J154
J155
J25
J156
SO 860
SO 152
TRUBNÍ PROPUSTEK DN 800 v km 3,090
TRUBNÍ PROPUSTEK DN 1200 v km 3,490
Dlouhá horka
AHVŽs-1
P5 / 3,67 km
SO 203
MOST NA I/16 PŘES PŘELOŽKU POLNÍ CESTY
km 3,790
VP3
DP26
PJ157
J158
SP159
J27
J160
SP161
SP162
J28
J163
P5 / 3,89 km
SO 301
SO 324
RÁMOVÝ PROPUSTEK 2x2 m v km 3,910
J164
J165
J29
J166
J167
SO 152
SO 380
SO 325
TRUBNÍ PROPUSTEK DN 1200 v km 4,260
TRUBNÍ PROPUSTEK DN 1200 v km 4,410
J168
J30
J169
J170
AHV1
zeměd.
4.0
4.5
Nad
P18 / 4,5 km
5 △ 235,6
SO 222
NÁJEZD MÚK ŽIDNĚVES
km 4,705
SO 111 - MÚK ŽIDNĚVES
P19 / 0 m
J56
J246
J57
SP172
J171
PJ173
J31
J174
SP175
PJ176
J177
J178
J179
J180
J32
J243
J244
J59
J242
J241
J240
SO 460
SO 311
SO 125
NAPOJENÍ PŮVODNÍ SILNICE I/16
P19 / 320 m
ŽIDNĚVES
SUKORADY
SO 342
SO 146
SO 360
VĚTEV 1
VĚTEV 2
VĚTEV 3
VĚTEV 4
OSA 1
OSA 2
SO 204
MOST NA I/16 PŘES SUKORADSKOU STOKU
km 5,048
5.0
P18 / 4,85 km
P6 / 4,93 km
DP33
PJ183
J181
J34
16
219,6
Rasovna
219,14
prům.
zásob.
sklad
S2
208,1 229,6

J101 212.12	Jádrový vrt podrobného GTP 2022 s presiometrickými zkouškami s označením a nadmořskou výškou
HJ129 228,53/11,0	Hydrogeologický jádrový vrt podrobného GTP 2022 s označením a nadmořskou výškou/hloubkou
PJ106 212.37	Jádrový vrt podrobného GTP 2022 s presiometrickými zkouškami s označením a nadmořskou výškou
SP102 212.06	Sonda statické penetrace podrobného GTP 2022 s označením a nadmořskou výškou
KS257 212,24	Jádrový vrt podrobného GTP 2022 pro vsakovací zkoušky s označením a nadmořskou výškou
J1 ○ 212,1/8,0	Jádrový vrt předběžného GTP 2016 s označením a nadmořskou výškou/hloubkou
HJ14 ○ 227,3/11,0	Hydrogeologický jádrový vrt předběžného GTP 2016 s označením a nadmořskou výškou/hloubkou
PJ3 ○ 212,3/15,0	Jádrový vrt předběžného GTP 2016 s presiometrickými zkouškami s označením a nadmořskou výškou/hloubkou
DP2 ○ 212,3/6,0	Sonda dynamické penetrace předběžného GTP 2016 s označením a nadmořskou výškou/hloubkou
AJ8 ● 212,2/6,0	Archivní sonda s označením a nadmořskou výškou/hloubkou
HJ9 ●	Pasportizovaný hydrogeologický objekt
▨	Plošný geofyzikální průzkum metodou DEMP - etapa předběžného GF průzkumu
	Geofyzikální profil - etapa předběžného GT průzkumu
	Geofyzikální profil - etapa podrobného GT průzkumu
	Georadarový profil - etapa podrobného GT průzkumu
VP1	Geotechnický výpočtový profil

KRESLIL:	Mgr: Vlastimil Mužík	ODP. ŘEŠITEL:	Mgr. Vlastimil Mužík	**inset** INSET s.r.o., Lucemburská 1170/7, 130 00 Praha 3 www.inset.com tel. 221 489 111
ZPRACOVAL:	Mgr. Vlastimil Mužík	KONTROLA:	RNDr. Oldřich Levý	
OBJEDNATEL:	ŘSD ČR			
INVESTOR:	ŘSD ČR			Č. ZAKÁZKY: 20020587000
STAVBA ZAKÁZKA:	**I/16 Mladá Boleslav - Martinovice Podrobný geotechnický průzkum**			ÚČEL: ZZ
OBSAH PŘÍLOHY:	**Situace průzkumných prací část 1, km 0,000 až 5,000**			FORMÁT: 594x2720 DATUM: 02/2022 ČÍS. ZPRÁVY: 01
				MĚŘÍTKO: 1:2000 ČÍSLO PŘÍLOHY: A1.1