VĚTEV 1 MÚK ŽIDNĚVES

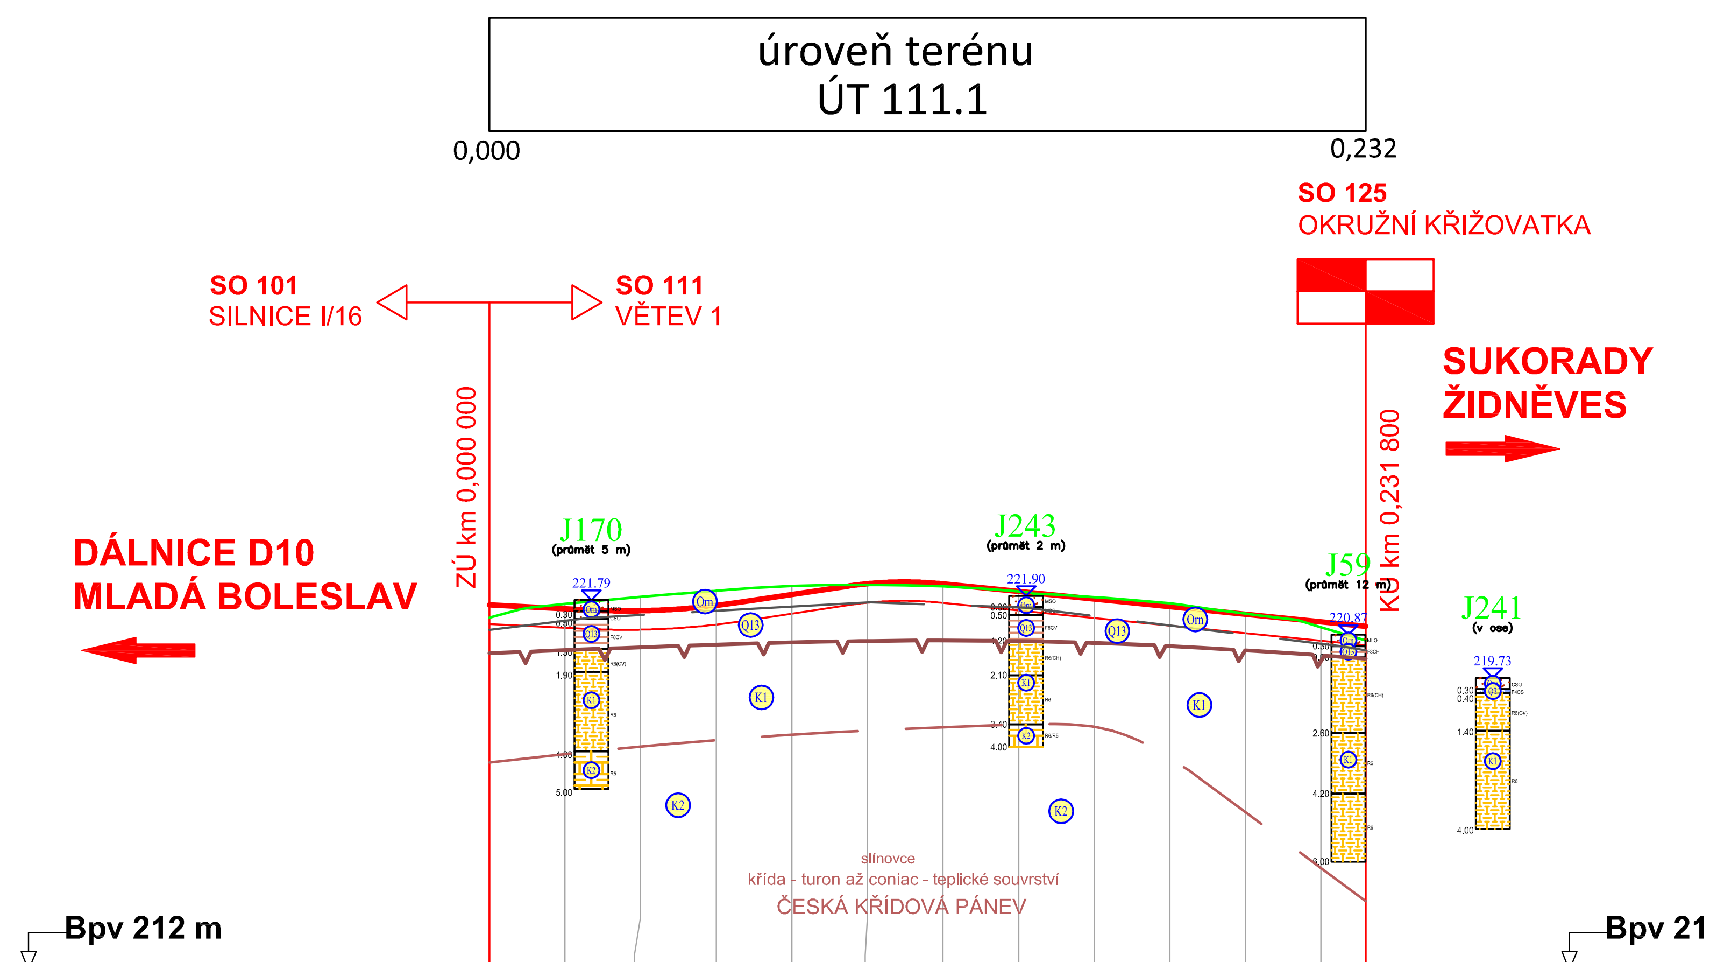
úroveň terénu
ÚT 111.1
0,000
0,232
SO 101
SILNICE I/16
SO 111
VĚTEV 1
SO 125
OKRUŽNÍ KŘIŽOVATKA
DÁLNICE D10
MLADÁ BOLESLAV
SUKORADY
ŽIDNĚVES
ZÚ km 0,000 000
KÚ km 0,231 800
J170
J243
J59
J241
K1
K2
křída - turon až coniac - teplické souvrství
slínovce
ČESKÁ KŘÍDOVÁ PÁNEV
Bpv 212 m

KÓTY NIVELETY	221,66	221,56	221,50	221,64	221,93	222,22	222,21	222,01	221,81	221,61	221,41	221,21	221,10
KÓTY TERÉNU	221,32	221,68	221,87	222,03	222,16	222,19	222,15	222,02	221,86	221,70	221,43	221,07	220,72
STANIČENÍ	0,00	20,00	40,00	60,00	80,00	100,00	120,00	140,00	160,00	180,00	200,00	220,00	231,80

km 0.0 0.1 0.2

VĚTEV 2 MÚK ŽIDNĚVES

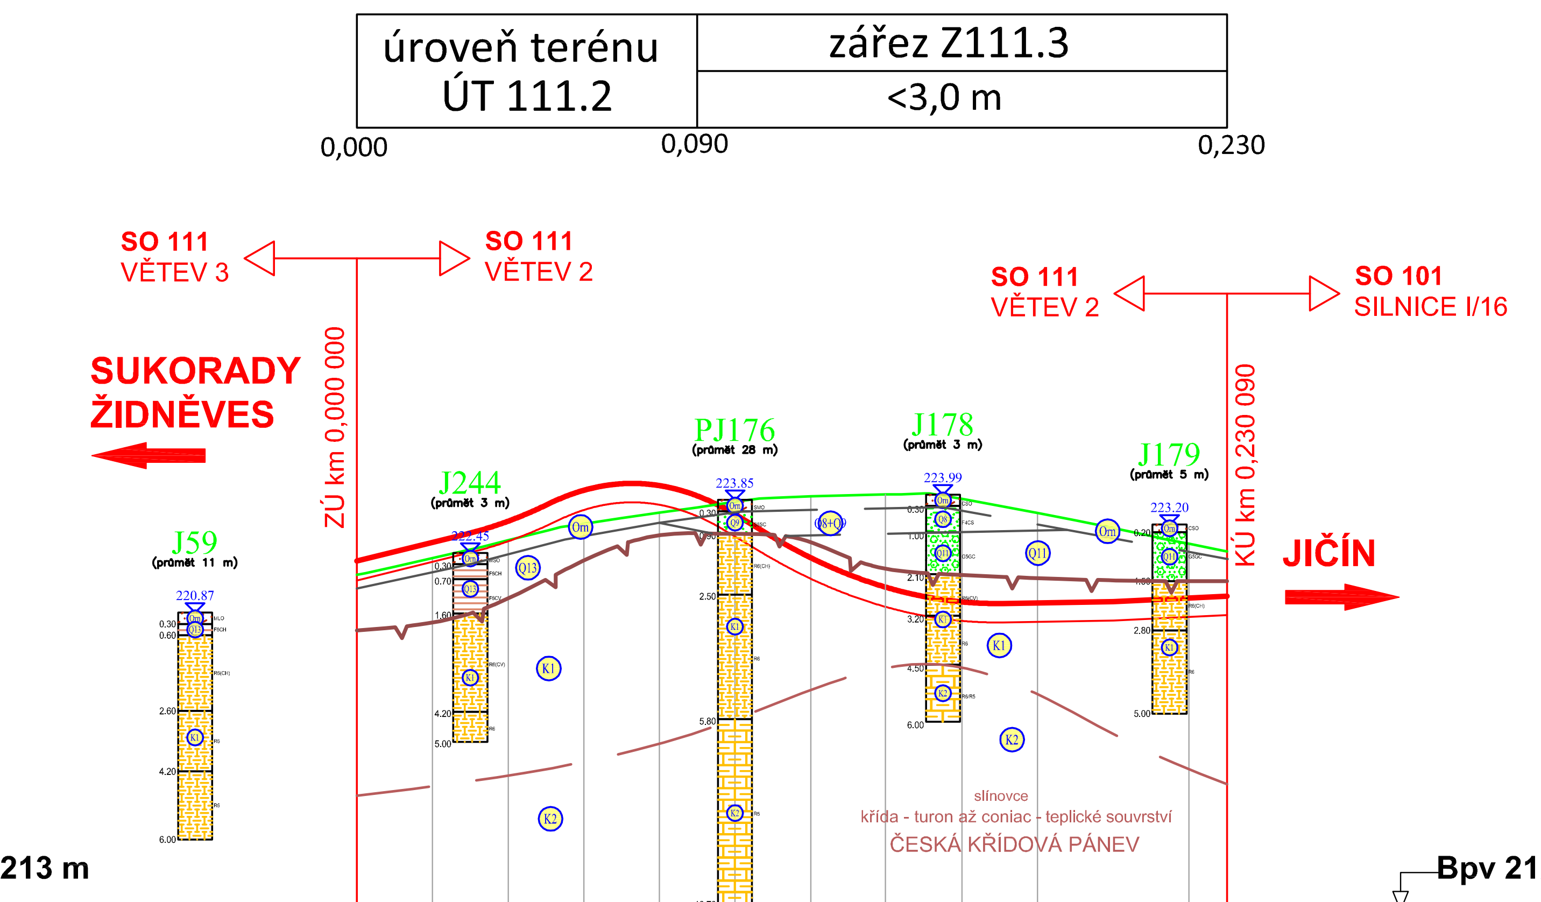
úroveň terénu
ÚT 111.2
zářez Z111.3
<3,0 m
0,000
0,090
0,230
SO 111
VĚTEV 3
SO 111
VĚTEV 2
SO 111
VĚTEV 2
SO 101
SILNICE I/16
SUKORADY
ŽIDNĚVES
JIČÍN
ZÚ km 0,000 000
KÚ km 0,230 090
J59
J244
PJ176
J178
J179
K1
K2
křída - turon až coniac - teplické souvrství
slínovce
ČESKÁ KŘÍDOVÁ PÁNEV
Bpv 213 m

KÓTY NIVELETY	222,24	222,73	223,29	224,11	224,23	223,46	222,32	221,54	221,15	221,13	221,16	221,26	221,31
KÓTY TERÉNU	221,87	222,31	222,78	223,22	223,51	223,80	223,95	224,00	223,88	223,50	223,11	222,69	222,49
STANIČENÍ	0,00	20,00	40,00	60,00	80,00	100,00	120,00	140,00	160,00	180,00	200,00	220,00	230,09

km 0.0 0.1 0.2

VĚTEV 3 MÚK ŽIDNĚVES

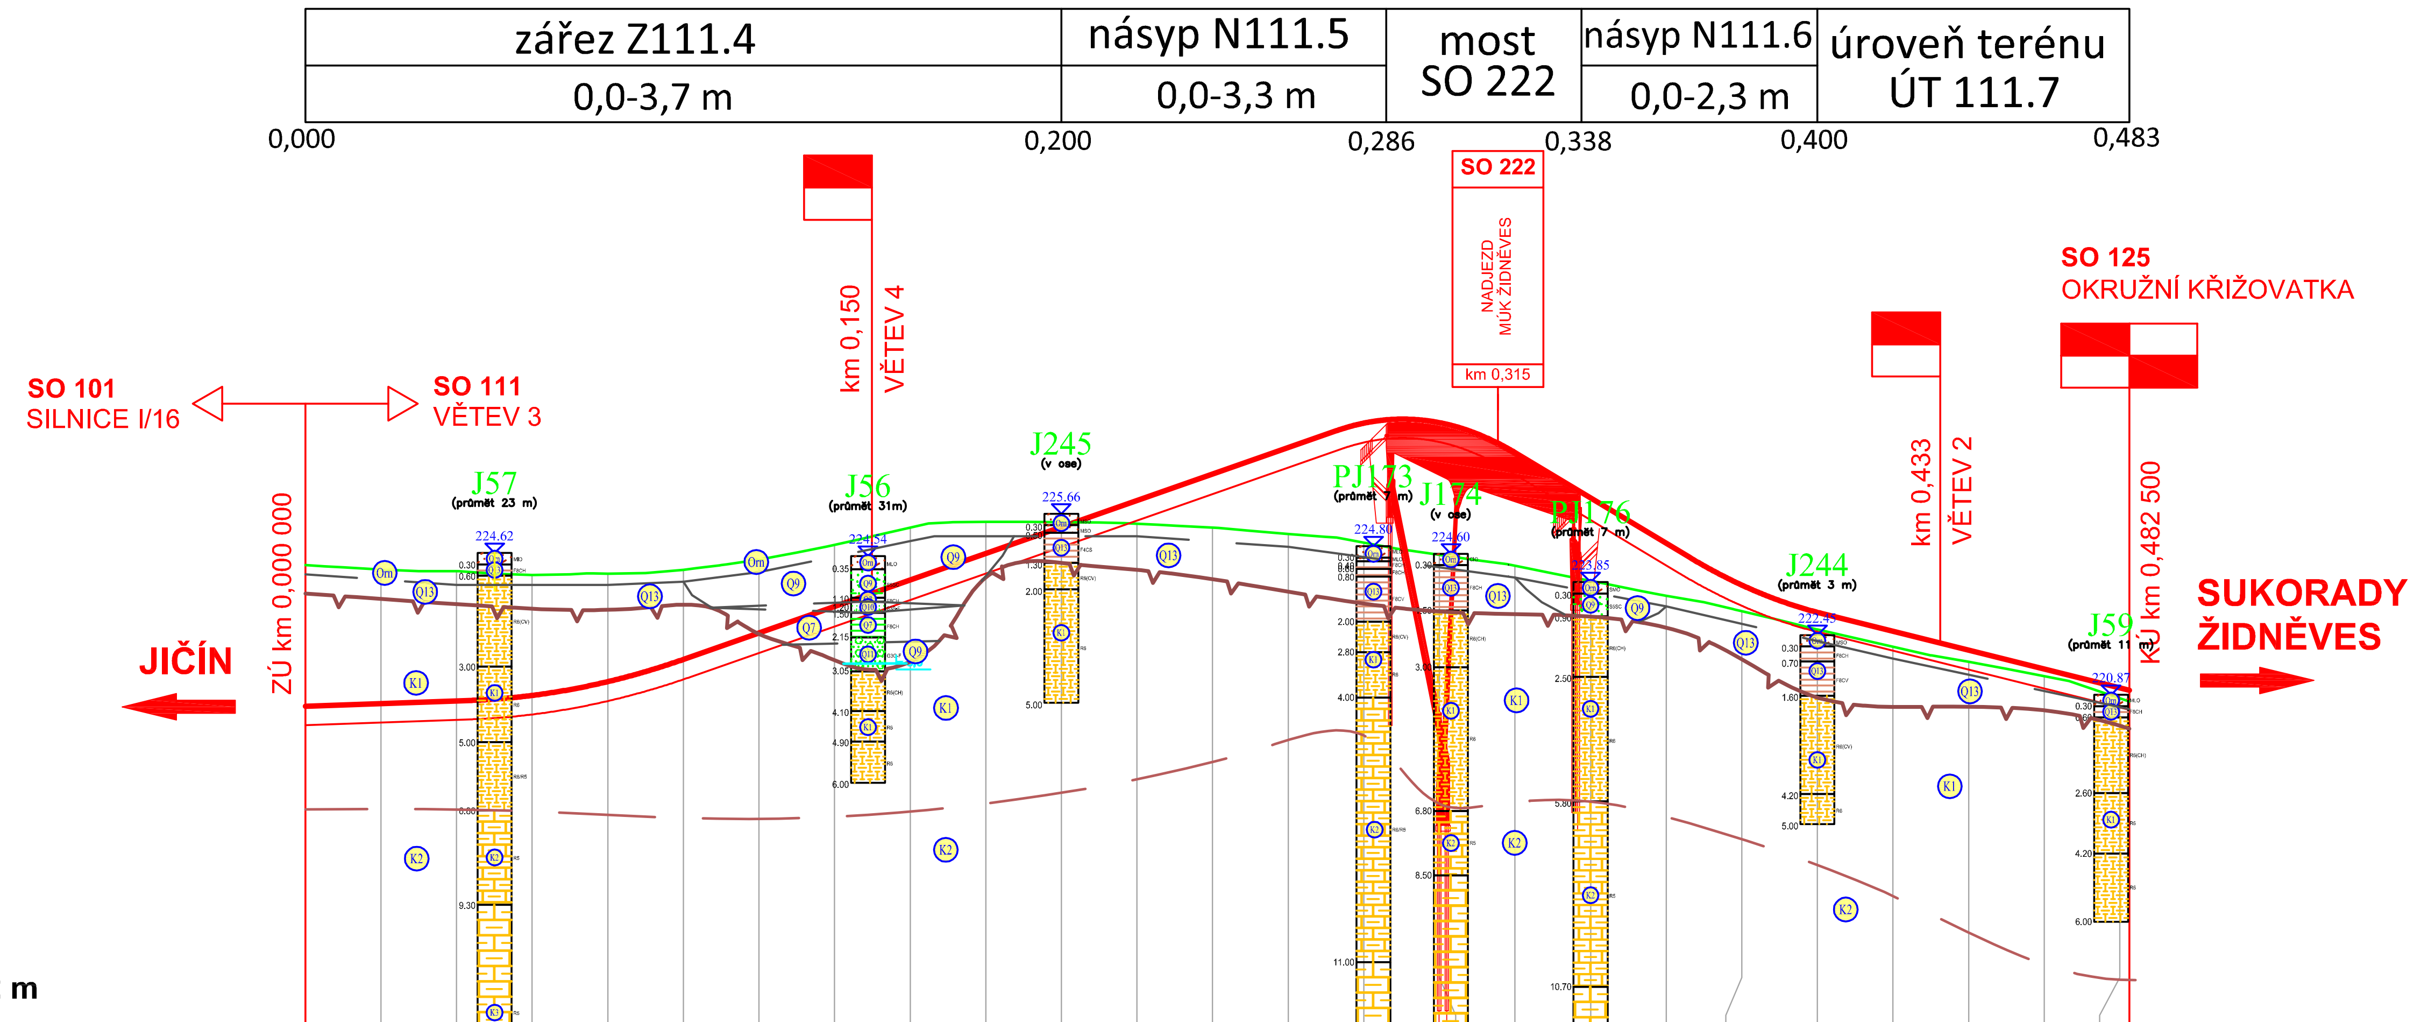
zářez Z111.4
0,0-3,7 m
násyp N111.5
0,0-3,3 m
most
SO 222
násyp N111.6
0,0-2,3 m
úroveň terénu
ÚT 111.7
0,000
0,200
0,286
0,338
0,400
0,483
SO 101
SILNICE I/16
SO 111
VĚTEV 3
km 0,150
VĚTEV 4
SO 222
NADJEZD
MÚK ŽIDNĚVES
km 0,315
km 0,433
VĚTEV 2
SO 125
OKRUŽNÍ KŘIŽOVATKA
JIČÍN
SUKORADY
ŽIDNĚVES
ZÚ km 0,000 000
KÚ km 0,482 500
J57
J56
J245
PJ173
J174
PJ175
J244
J59
K1
K2
K3
14.0
17.4
Bpv 212 m

KÓTY NIVELETY	220,57	220,64	220,71	220,85	221,22	221,81	222,51	223,21	223,91	224,61	225,31	226,01	226,71	227,41	228,05	228,12	228,06	227,28	226,08	224,88	223,77	223,61	223,05	222,55	222,05	221,55	221,05	220,99
KÓTY TERÉNU	224,30	224,18	224,14	224,04	224,07	224,17	224,45	224,83	225,29	225,44	225,44	225,40	225,29	225,12	224,89	224,62	224,57	224,28	223,88	223,49	223,08	223,00	222,60	222,14	221,74	221,36	220,78	220,70
STANIČENÍ	0,00	20,00	40,00	60,00	80,00	100,00	120,00	140,00	160,00	180,00	200,00	220,00	240,00	260,00	280,00	296,53	300,00	320,00	340,00	360,00	380,00	383,60	400,00	420,00	440,00	460,00	480,00	482,50

km 0.0 0.1 0.2 0.3 0.4

VĚTEV 4 MÚK ŽIDNĚVES

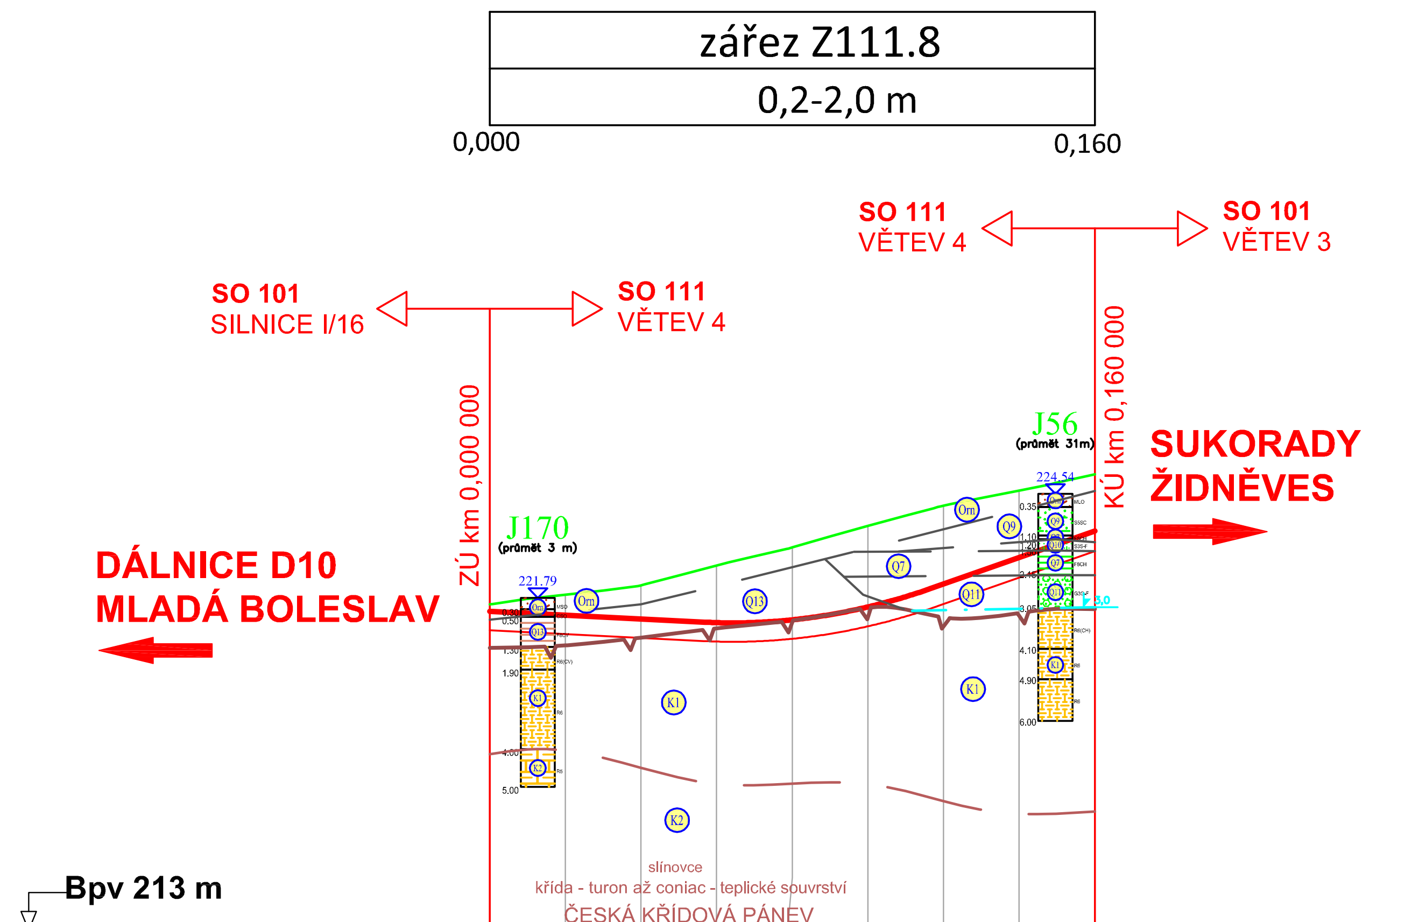
zářez Z111.8
0,2-2,0 m
0,000
0,160
SO 101
SILNICE I/16
SO 111
VĚTEV 4
SO 111
VĚTEV 4
SO 101
VĚTEV 3
DÁLNICE D10
MLADÁ BOLESLAV
SUKORADY
ŽIDNĚVES
ZÚ km 0,000 000
KÚ km 0,160 000
J170
J56
K1
K2
křída - turon až coniac - teplické souvrství
slínovce
ČESKÁ KŘÍDOVÁ PÁNEV
Bpv 213 m

KÓTY NIVELETY	221,43	221,33	221,23	221,13	221,21	221,55	222,15	222,85	223,55
KÓTY TERÉNU	221,62	221,87	222,12	222,64	223,12	223,69	224,23	224,62	225,06
STANIČENÍ	0,00	20,00	40,00	60,00	80,00	100,00	120,00	140,00	160,00

km 0.0 0.1

LEGENDA

genetický původ zemin a stratigrafické zařazení hornin			litologická charakteristika	zatřídění dle ČSN 73 6133	geotechnický typ – šrafa	
kvartér	antropogenní sedimenty		Navážky, tělesa stávajících komunikací	Y	A	▨
	kulturní vrstvy		Organogenní zeminy	O	Orn	▨
	fluviální sedimenty	holocenní sedimenty	Jíly s nízkou až střední plasticitou	F6	Q1	▨
			Jíly s vysokou a velmi vysokou plasticitou	F8	Q2	▨
			Štěrkovité a písčité jíly	F2, F4	Q3	▨
			Hlinité a jílovité písky	S5, S4	Q4	▨
			Písky s jemnozrnnou příměsí	S3 (S1,S2)	Q5	▨
			Hlinité a jílovité štěrky	G4, G5	Q6	▨
		pleistocenní terasové sedimenty	Jíly s vysokou až extrémní plasticitou	F8	Q7	▨
			Štěrkovité a písčité jíly	F2, F4	Q8	▨
			Hlinité a jílovité písky	S4, S5	Q9	▨
			Písky s jemnozrnnou příměsí	S3 (S1, S2)	Q10	▨
			Štěrky s proměnlivým obsahem jemnozrnné frakce	G3, G4, G5	Q11	▨
	deluviální, deluviofluviální a soliflukční sedimenty		Jíly s nízkou až střední plasticitou	F6	Q12	▨
			Jíly s vysokou a velmi vysokou plasticitou	F8	Q13	▨
			Štěrkovité a písčité jíly	F2, F4 (S5)	Q14	▨
mesozoikum	svrchní turon až coniac	teplické souvrství	Slínovec zcela až velmi zvětralý	R6	K1	▨
			Slínovec mírně zvětralý	R6/R5, R5	K2	▨
			Slínovec slabě zvětralý až zdravý	R5	K3	▨

LEGENDA ZNAČEK A ČAR

J101-J999 (průmět 10m vpravo)	jádrový vrt podrobného průzkumu 2022
PJ101-PJ999 (průmět 10m vpravo)	jádrový vrt podrobného průzkumu 2022, s presiometrickými zkouškami
HJ101-HJ999 (průmět 10m vpravo)	jádrový vrt podrobného průzkumu 2022, vystrojený pro hydrogeologické měření
SP101-SP999 (průmět 10m vpravo)	sonda statické penetrace podrobného průzkumu 2022
J1-J99 (průmět 10m vpravo)	jádrový vrt předběžného průzkumu 2016
PJ1-PJ99 (průmět 10m vpravo)	jádrový vrt předběžného průzkumu 2016 s presiometrickými zkouškami
HJ1-HJ99 (průmět 10m vpravo)	jádrový vrt předběžného průzkumu 2016 vystrojený pro hydrogeologické měření
DP1-DP99 (průmět 10m vpravo)	sonda dynamická penetrace předběžného průzkumu 2016
AJX-AJXXX (průmět 10m vpravo)	archivní jádrový vrt

— — —	rozhraní mezi vrstvami kvartéru
⌇	povrch předkvartérního podloží
— — —	rozhraní míry zvětrání v podloží
δ	tektonika
- · - · -	hladina podzemní vody
2.35	hloubka ustálené hladiny podzemní vody ve vrtu
3.40	hloubka naražené hladiny podzemní vody ve vrtu
Q1	geotechnický typ

KRESLIL:	Mgr: Vlastimil Mužík	ODP. ŘEŠITEL:	Mgr. Vlastimil Mužík
ZPRACOVAL:	Mgr. Vlastimil Mužík	KONTROLA:	RNDr. Oldřich Levý
OBJEDNATEL:	ŘSD ČR		
INVESTOR:	ŘSD ČR		
STAVBA ZAKÁZKA:	**I/16 Mladá Boleslav - Martinovice** **Podrobný geotechnický průzkum**		
OBSAH PŘÍLOHY:	**Podélné IG profily SO111** **větve 1 až 4**		

inset
INSET s.r.o.,
Lucemburská 1170/7, 130 00 Praha 3
www.inset.com tel. 221 489 111

Č. ZAKÁZKY:	20020587000		
ÚČEL:	ZZ		
FORMÁT:	297x1360	DATUM:	02/2022
		ČÍS. ZPRÁVY:	01
MĚŘÍTKO:	1:2000/200	ČÍSLO PŘÍLOHY:	A2.3