


I/16 MLADÁ BOLESLAV - m MARTINOVICE
KOORDINAČNÍ SITUACE km 2,500 - 5,500, M 1:2 000



LEGENDA:

PLOCHY

- VOZOVKA - ASFALTOVÝ KRYT
- VOZOVKA - FRÉZOVANÁ
- VOZOVKA - CYKLISTICKÁ STEZKA
- VOZOVKA - POLNÍ CESTY
- CHODNÍK
- DLAŽBA VOZOVKY
- SVAHY VÝKOPY
- SVAHY NÁSPY
- VEGETAČNÍ ÚPRAVY

NOVÉ IS

- DEŠŤOVÁ KANALIZACE
- MELIORACE
- VÝTLAK
- VODOVOD
- NADZEMNÍ VEDENÍ NN
- PODZEMNÍ VEDENÍ NN
- PODZEMNÍ SĎELOVACÍ VEDENÍ
- PLYNOVOD - STL

STÁVAJÍCÍ IS - INFORMATIVNÍ ZÁKRES

- PODZEMNÍ VEDENÍ NN
- PODZEMNÍ VEDENÍ VN
- NADZEMNÍ VEDENÍ VN
- NADZEMNÍ VEDENÍ VVN
- DEŠŤOVÁ KANALIZACE
- PLYNOVOD - STL
- PODZEMNÍ SĎELOVACÍ VEDENÍ
- VODOVOD

KATASTR NEMOVITOSTÍ

- HRANICE K.Ú.
- HRANICE PARCEL
- TRVALÝ ZÁBOR
- DOČASNÝ ZÁBOR DO 1 ROKU

Souřadnicový systém: S-JTSK
Výškový systém: Bpv

C Situační výkresy

Objednatel:

ŘEDITELSTVÍ SILNIC A DÁLNIC

Ředitelství silnic a dálnic s. p.
Čerčanská 2023/12, Krč, 140 00 Praha 4

Zhotovitel:

Valbek, spol. s r.o.
Vaňurova 505/17
460 07 Liberec 3

HIP:

ING. T. KLIMENT

Valbek

Vypracoval: ING. M. HRUBÝ
Zodp. projektant: ING. T. KLIMENT
Tech. kontrola: ING. M. HANZL

Akce: I/16 MLADÁ BOLESLAV - MARTINOVICE

Přiloška: KOORDINAČNÍ SITUACE km 2,500 - 5,500

Zak. číslo: 21-113-001
Datum: 02/2025
Stupeň: PDPS
Počet formátů: 18 x A4
Měřítko: 1:2 000
Č. přílohy: Para

C.2.2

SEZNAM SO:

- SO 001 Příprava území
- SO 002 Silnice I/16 Mladá Boleslav - Martinovice
- SO 003 Přeložka silnice III/2768 v km 2,200
- SO 004 Přeložka silnice III/27612 v km 6,080
- SO 005 Přeložka místní komunikace v km 0,228
- SO 006 Přeložka místní komunikace v km 7,320 / 835 vlevo
- SO 007 Napojení původní I/16 do MUK Židněves
- SO 008 Napojení původní I/16 do MUK Martinovic
- SO 009 Napojení ČSPH na silnici I/16
- SO 010 Oprávnění BUS Martinovic
- SO 011 Přeložka místní komunikace v km 1,713
- SO 012 Přístup k DUN v km 0,170
- SO 013 Přístup k DUN v km 0,390
- SO 014 Přístup k DUN v km 0,720
- SO 015 Přístup k DUN v km 1,500
- SO 016 Přístup k DUN v km 2,760
- SO 017 Přístup k DUN v km 4,940
- SO 018 Přístup k DUN v km 5,130
- SO 019 Přístup k DUN v km 5,450
- SO 020 Přístup na pozemky v k.ú. Kosmonosy
- SO 021 Přístup na pozemky v k.ú. Židněves
- SO 022 Přístup na pozemky v k.ú. Sukorady u Mladé Boleslavi
- SO 023 Přeložka polní cesty v km 6,700
- SO 024 Provozovní přeložka I/16
- SO 025 Přeložka dopravního značení
- SO 026 Most na I/16 přes MK a železniční vodotěs v km 0,228
- SO 027 Most na I/16 přes Valskou vodotěs v km 2,695
- SO 028 Most na I/16 přes přeložku polní cesty v km 3,790
- SO 029 Most na I/16 přes Sukoradskou stávkou v km 5,048
- SO 030 Most na I/16 přes přeložku III/27612 v km 6,080
- SO 031 Most na I/16 přes přeložku polní cesty v km 6,700
- SO 032 Most na I/16 přes Přeloučský potok v km 7,870
- SO 033 Nadjezd přeložky III/2768 v km 2,200
- SO 034 Nadjezd MUK Židněves v km 4,705
- SO 035 Nadjezd MUK Martinovic v km 7,320
- SO 036 Nadjezd v km 1,713
- SO 037 Odvození I/16
- SO 038 Odvození MUK Martinovic
- SO 039 Úprava vodního toku Ot Stákor
- SO 040 Úprava HOZ 1 v km 0,554
- SO 041 Úprava HOZ 2 v km 1,480
- SO 042 Úprava Valské vodotěs
- SO 043 Úprava HOZ 3 v km 3,980
- SO 044 Úprava koryta v km 4,210
- SO 045 Úprava Sukoradské stávkou
- SO 046 Úprava HOZ 5A a 6 v km 7,080
- SO 047 Úprava HOZ 7 a 8 v km 7,730
- SO 048 Úprava Přeloučského potoka
- SO 049 Přeložka vodovodu PE 110 v km 2,195
- SO 050 Přeložka vodovodu PVC 225 v MUK Židněves
- SO 051 Přeložka vodovodu PVC 150 v km 6,091
- SO 052 Přeložka vodovodu v MUK Martinovic
- SO 053 DUK a retenční nádrž na I/16
- SO 054 Úpravy meliorací ŽU - KU
- SO 055 Zřízení nádrží vodních zdrojů
- SO 056 Úprava vedení VVN, km 0,602
- SO 057 Přeložka vřchového vedení 22kV km 0,200
- SO 058 Přeložka vřchového vedení 22 kV km 0,533
- SO 059 Přeložka vřchového vedení 22 kV km 5,560 - 5,885
- SO 060 Přeložka sítě napájecího vedení 22 kV, km 6,060
- SO 061 Přeložka kabelových vedení NN km 6,075
- SO 062 Přeložka kabelových vedení NN km 7,480 - 7,530
- SO 063 Přeložka kabelového vedení NN km 7,845
- SO 064 Velkoplošná sítě napájecího vedení 7,785
- SO 065 Přeložka vedení SEK - DOK CETIN km 2,170
- SO 066 Přeložka vedení SEK CETIN km 4,500 - 5,150
- SO 067 Přeložka vedení SEK CETIN km 6,080
- SO 068 Přeložka vedení SEK CETIN km 7,200 - 7,545
- SO 069 Přeložka vedení SEK CETIN km 8,170
- SO 070 Automatická sítě napájecího vedení
- SO 071 Přeložka STL, příjezd v km 2,225
- SO 072 Protiukozová stěna v km 6,100 vlevo
- SO 073 Protiukozová stěna v km 7,600 vlevo
- SO 074 Vegetační úpravy
- SO 075 Kvalitní zeleň
- SO 076 Rekultivace ploch dočasného záboru
- SO 077 Odpojení

POZNÁMKA:

ŠEDOU BARVOU JE VYZNAČEN SEZNAM SOUVISEJÍCÍCH STAVEBNÍCH OBJEKTŮ PROJEKTOVOU DOKUMENTACÍ, INŽENÝRSKOU ČINNOSTÍ PRO STAVEBNÍ ŘÍZENÍ A REALIZACI ZAJIŠŤUJE ČEZ DISTRIBUCE, a.s.)