
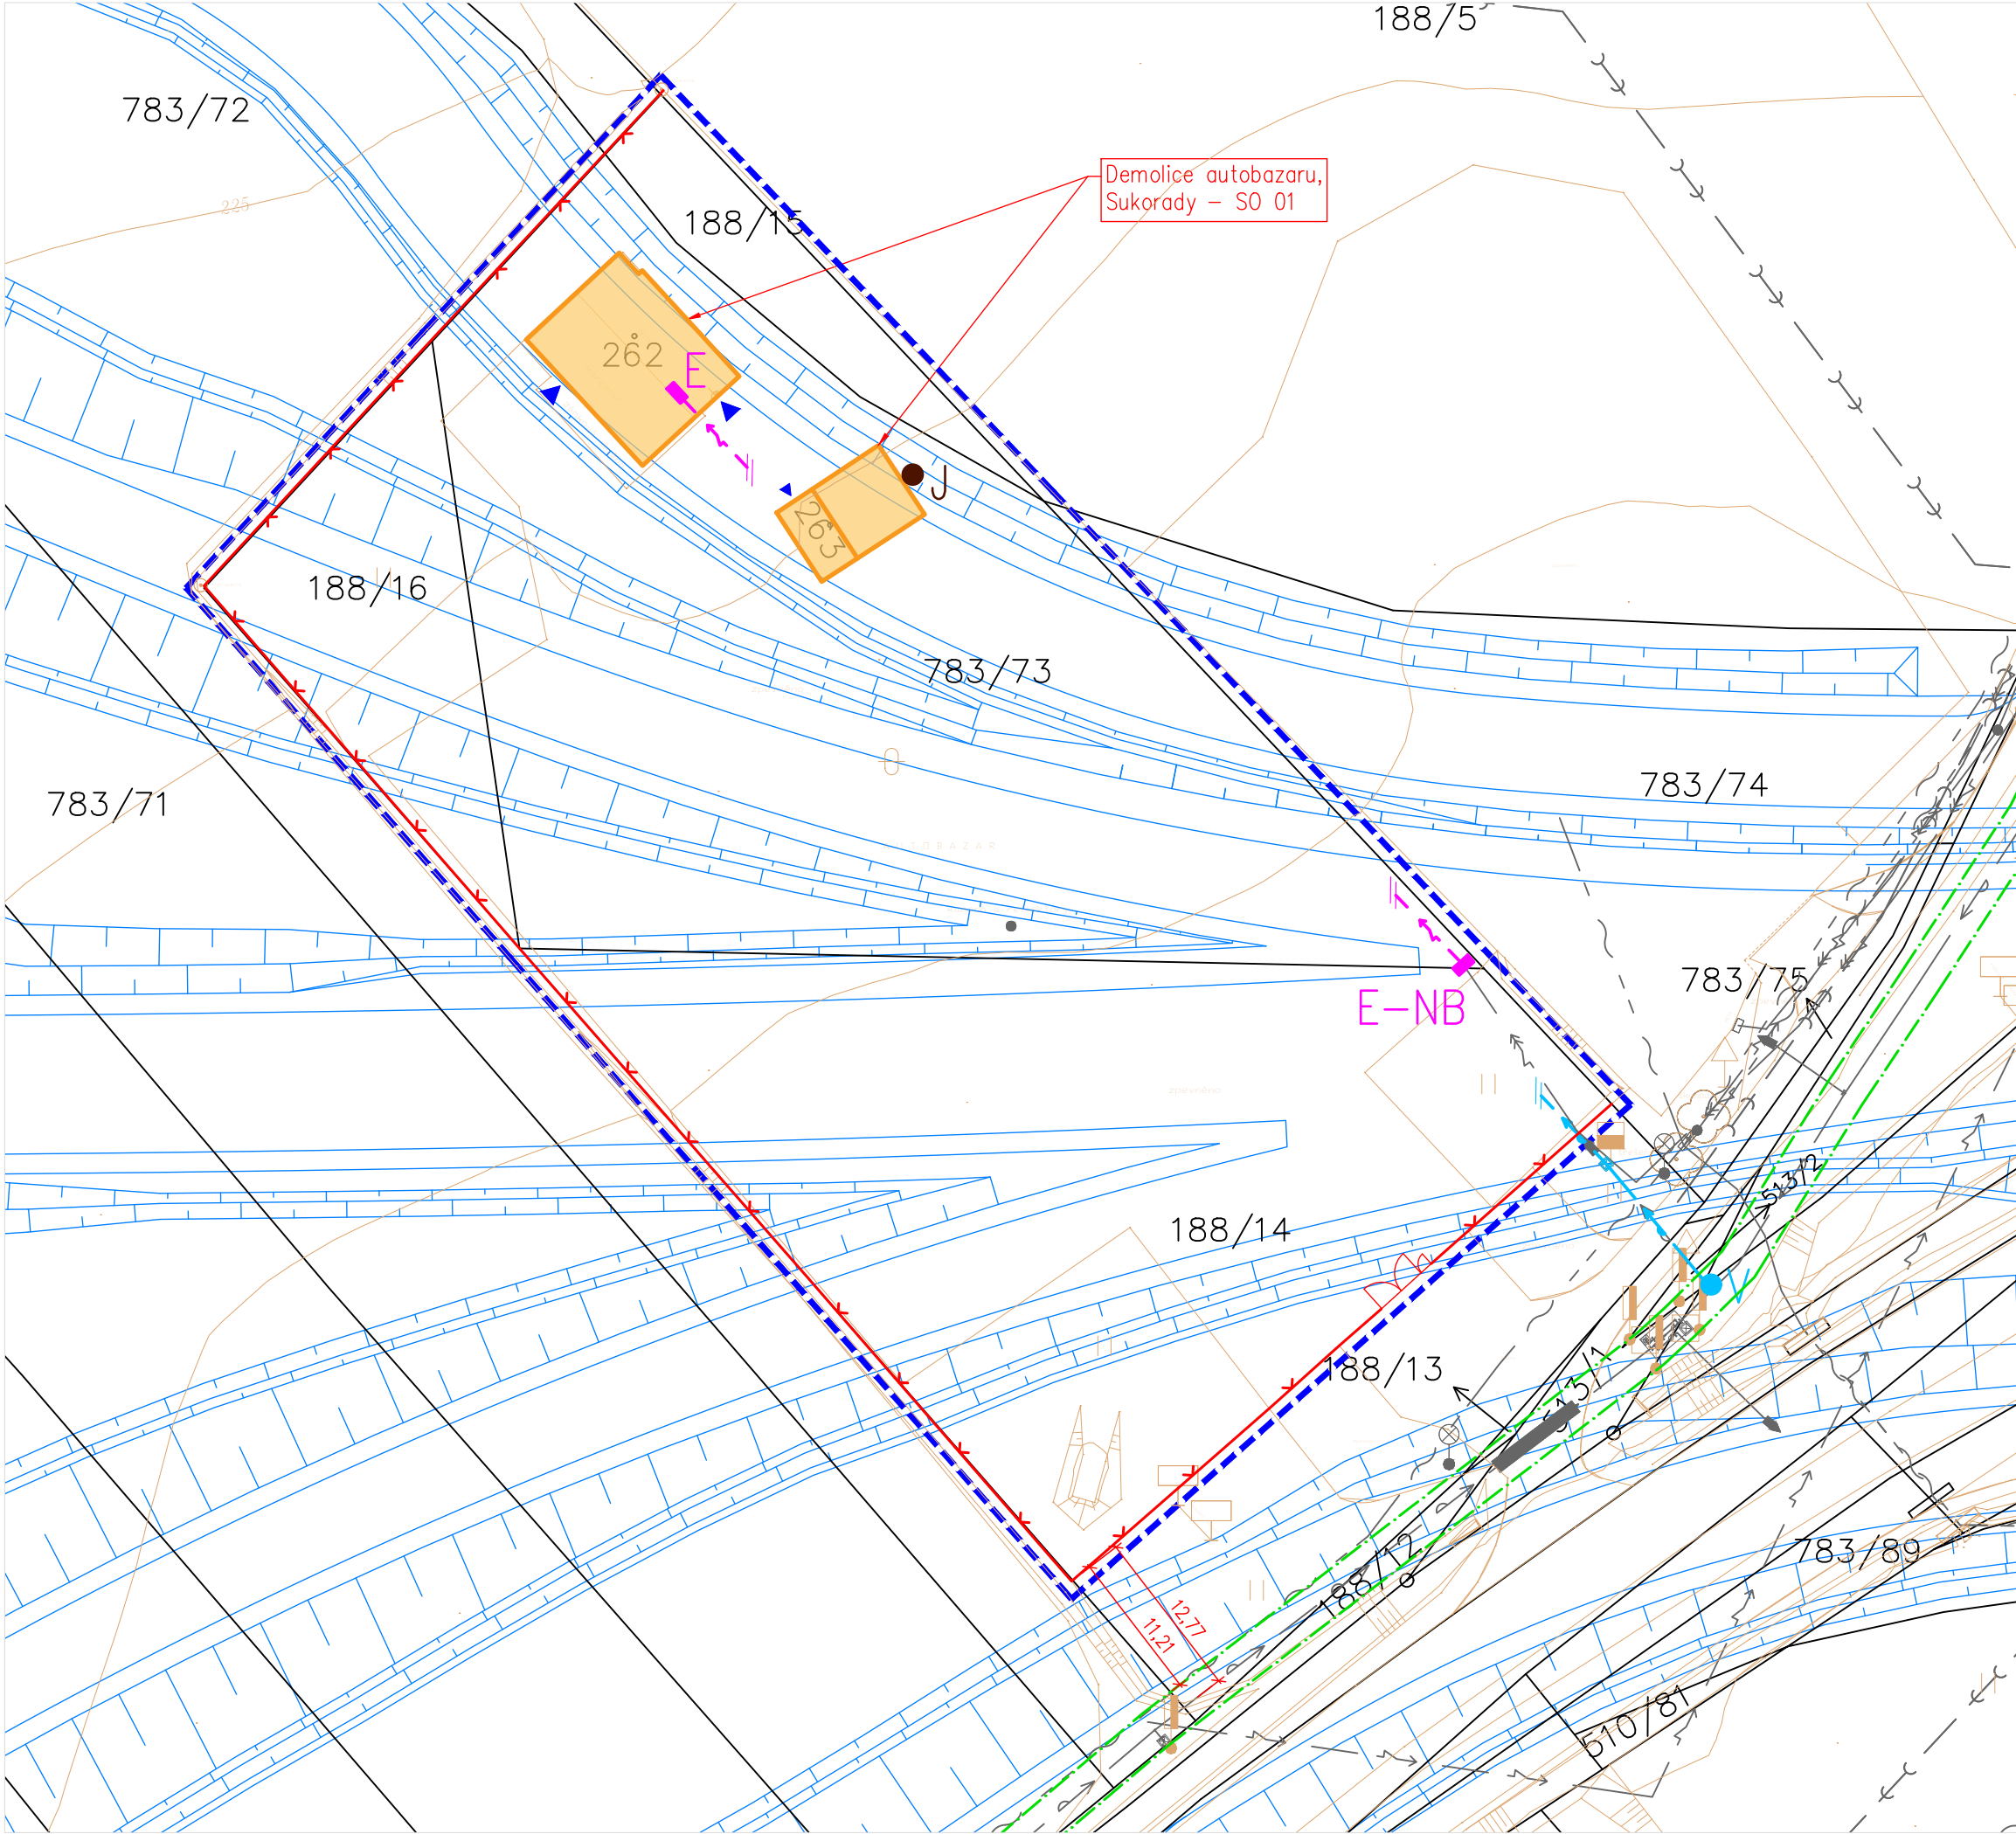
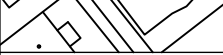
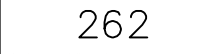


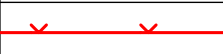

SEZNAM DOTČENÝCH POZEMKŮ				
katastrální území	č. poz.	LV	vlastník	Druh pozemku
Sukorady	st. 262	575	Česká republika, Ředitelství silnic a dálnic s. p., Na Pankráci 546/56, Nusle, 14000 Praha 4	zastavěná plocha a nádvoří
Sukorady	st. 263	575	Česká republika, Ředitelství silnic a dálnic s. p., Na Pankráci 546/56, Nusle, 14000 Praha 4	zastavěná plocha a nádvoří
Sukorady	188/14	575	Česká republika, Ředitelství silnic a dálnic s. p., Na Pankráci 546/56, Nusle, 14000 Praha 4	orná půda
Sukorady	188/15	575	Česká republika, Ředitelství silnic a dálnic s. p., Na Pankráci 546/56, Nusle, 14000 Praha 4	ostatní plocha
Sukorady	188/16	575	Česká republika, Ředitelství silnic a dálnic s. p., Na Pankráci 546/56, Nusle, 14000 Praha 4	orná půda
Sukorady	783/73	575	Česká republika, Ředitelství silnic a dálnic s. p., Na Pankráci 546/56, Nusle, 14000 Praha 4	ostatní plocha

LEGENDA		
PLOCHY, PRVKY		Demolice autobazaru, Strakov – SO 01
		Hranice zájmového území
		Digitalizovaná katastrální mapa
		Parcelní čísla
		Geodetické zaměření
		I/16 Mladá Boleslav – Martinovice (nová trasa)
		Hlavní a vedlejší vstupy do objektů
		Stávající oplocení – demontovat

NAPOJOVACÍ BODY

- E-NB ELEKTRO – napojovací bod
- E ELEKTRO – elektroměrová skříň
- V VODA – napojovací bod
- S SEPTIK
- ELEKTRO – přípojka (neověřená trasa)
- VODA – přípojka
- ochranné pásmo vodovodu

STÁVAJÍCÍ INŽENÝRSKÉ SÍTĚ

- Stávající vedení elektro NN
- Stávající vedení elektro VN
- Kanalizace splašková (budoucí)
- Stávající vodovod
- Stávající sdělovací kabely

Souřadnicový systém: S-JTSK
Výškový systém: Bpv

SO 01

Demolice autobazaru, Sukorady

Objednatel:

Ředitelství
silnic
a dálnic

Ředitelství silnic a dálnic s. p.
Čerčanská 2023/12, Krč, 140 00 Praha 4

Zhotovitel:

Valbek

Valbek, spol. s r.o.

Vaňurova 505/17
460 07 Liberec 3

	Vypracoval	Bc. Ivana Rajdlová	Zak. číslo	21-LI13-001
	Zodp. projektant	Bc. Ivana Rajdlová	Datum	02/2025
	Tech. kontrola	Ing. Jiří Švarc	Stupeň	PDPS
	Akce		Počet formátů	4 x A4
Zhotovitel: Valbek, spol. s r.o. Vaňurova 505/17 460 07 Liberec 3	Příloha KATASTRÁLNÍ SITUAČNÍ VÝKRES		Měřítko	1 : 500
			Č. přílohy	Paré
			C.2	