ŘEZ A-A´
MĚŘÍTKO 1:100

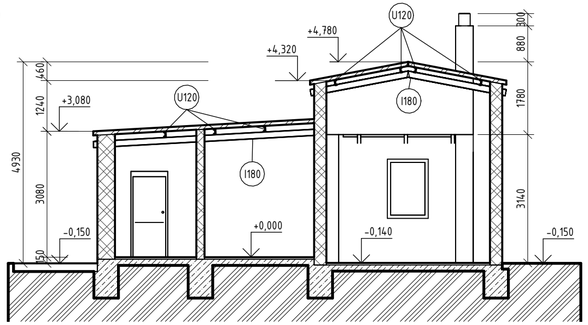

PŮDORYS 1.NP
MĚŘÍTKO 1:100

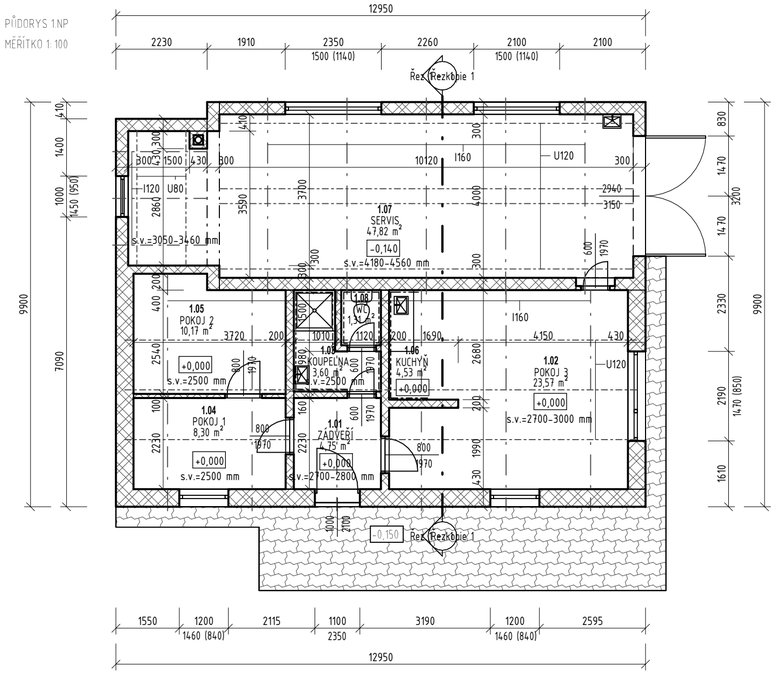

LEGENDA MATERIÁLŮ

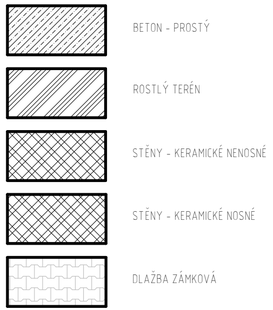

POHLED Z JIHOVÝCHODU

POHLED Z JIHOZÁPADU

POHLED ZE SEVEROVÝCHODU

POHLED ZE SEVERU

Souřadnicový systém: S-JTSK
Výškový systém: Bpv

± 0,000 = 224,75 m.n.m.

SO 01 Demolice autobazaru, Sukorady

Objednatel:

ŘEDITELSTVÍ SILNIC A DÁLNIC

Ředitelství silnic a dálnic s. p

Čerčanská 2023/12, Krč, 140 00 Praha 4

Valbek

Valbek, spol. s r.o.
Vaňurova 505/17
460 07 Liberec 3

Valbek

Vypracoval	Josef Vendl		**Zak. číslo**	**21-LI13-001**
Zodp. projektant	Bc. Ivana Rajdlová		**Datum**	**02/2025**
Tech. kontrola	Ing. Jiří Švarc		**Stupeň**	**PDPS**
Akce	**I/16 MLADÁ BOLESLAV - MARTINOVICE**		**Počet formátů**	**3 x A4**
			Měřítko	**1 : 100**
			Č. přílohy	**Paré**
Zhotovitel: Valbek, spol. s r.o. Vaňurova 505/17 460 07 Liberec 3	**Příloha** PŮDORYS 1.NP, ŘEZ A-A´, POHLEDY		**D.2**	