
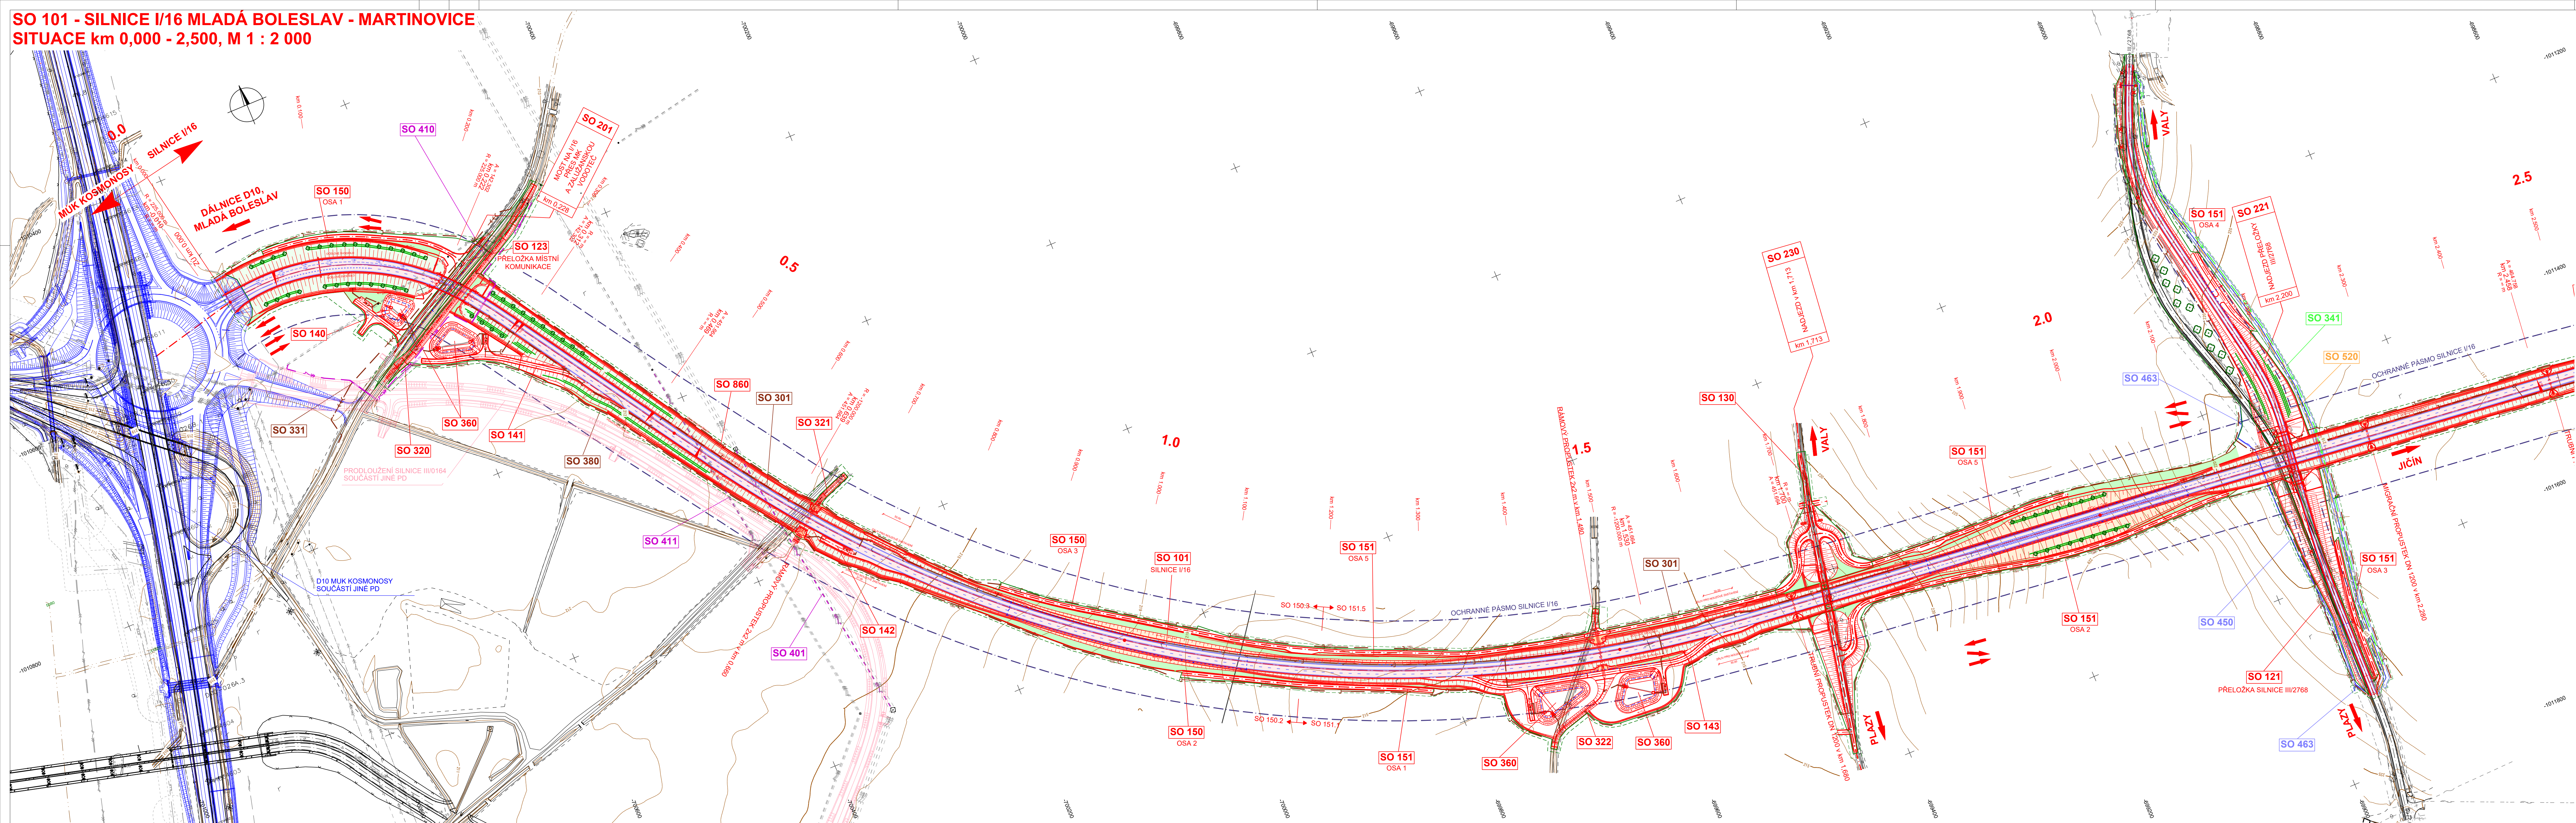
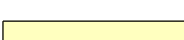
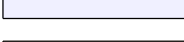


SO 101 - SILNICE I/16 MLADÁ BOLESLAV - MARTINOVICE
SITUACE km 0,000 - 2,500, M 1 : 2 000

 

LEGENDA:

POLOHY	NOVÉ IS	
		DEŠŤOVÁ KANALIZACE
		MELIORACE
		VÝTLAK
		VODOVOD
		NADZEMNÍ VEDENÍ NN
		NADZEMNÍ VEDENÍ VN
		PODZEMNÍ VEDENÍ NN
		PODZEMNÍ SDĚLOVACÍ VEDENÍ
		PLYNOVOD - STL
		STÁVAJÍCÍ IS - INFORMATIVNÍ ZÁKRES
		PODZEMNÍ VEDENÍ NN
		PODZEMNÍ VEDENÍ VN
		NADZEMNÍ VEDENÍ NN
		NADZEMNÍ VEDENÍ VN
		NADZEMNÍ VEDENÍ VVN
		DEŠŤOVÁ KANALIZACE
		PLYNOVOD - STL
		PODZEMNÍ SDĚLOVACÍ VEDENÍ
		VODOVOD
KATASTR NEMOVITOSTÍ		
		HRANICE K.Ú.
		HRANICE PARCEL
		TRVALÝ ZÁBOR
		DOČASNÝ ZÁBOR DO 1 ROKU

Souřadnicový systém: S-JTSK

Výškový systém: Bpv

SO 101 Silnice I/16 Mladá Boleslav - Martinovice

Objednatel:



Ředitelství silnic a dálnic s. p.
Čerčanská 2023/12, Krč, 140 00 Praha 4

Zhotovitel:



Valbek, spol. s r.o.
Vaňurova 505/17
460 07 Liberec 3

	Výpracoval	ING. M. HRUBOŠ		Dat. číslo	21-113-001
	Zodp. projektant	ING. T. KLIMENT		Zak.	02/2026
	Tech. kontrola	ING. M. HANZL		Stupeň	PDPS
	Akce	I/16 MLADÁ BOLESLAV - MARTINOVICE			Počet formátů
Zhotovitel: Valbek, spol. s r.o. Valbeřov 500/17 460 07 Liberec 3	Příloha SITUACE km 0,000 - 2,500			Měřítko	1 : 2 000
				Č. přílohy	Paré
				2.1	