
 
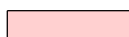
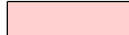
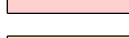


SO 101 - SILNICE I/16 MLADÁ BOLESLAV - MARTINOVICE
SITUACE km 2,500 - 5,500, M 1 : 2 000

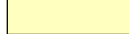

LEGENDA

POLOHY	NOVÉ IS
	VOZOVKA - ASFALTOVÝ KRYT
	VOZOVKA - FRÉZOVANÁ
	VOZOVKA - CYKLISTICKÁ STEZKA
	VOZOVKA - POLNÍ CESTY
	CHODNÍK
	DLAŽBA VOZOVKY
	SVAHY VÝKOPU
	SVAHY NÁSYPU
	VEGETAČNÍ ÚPRAVY
	DEŠŤOVÁ KANALIZACE
	MELIORACE
	VÝTLAK
	VODOVOD
	NADZEMNÍ VEDENÍ NN
	NADZEMNÍ VEDENÍ VN
	PODZEMNÍ VEDENÍ NN
	PODZEMNÍ SĐELOVACÍ VEDE
	PLYNOVOD - STL
	STÁVAJÍCÍ IS - INFORMATIVNÍ ZÁKRES
	PODZEMNÍ VEDENÍ NN
	PODZEMNÍ VEDENÍ VN
	NADZEMNÍ VEDENÍ NN
	NADZEMNÍ VEDENÍ VN
	NADZEMNÍ VEDENÍ VVN
	DEŠŤOVÁ KANALIZACE
	PLYNOVOD - STL
	PODZEMNÍ SĐELOVACÍ VEDE
	VODOVOD

Souřadnicový systém: S-JTSK
Výškový systém: Bpv

SO 101 Silnice I/16 Mladá Boleslav - Martinovice

Objednatel:

	ŘEDITELSTVÍ SILNIC A DÁLNIC
---	--

Ředitelství silnic a dálnic s. p.
Čerčanská 2023/12, Krč, 140 00 Praha 4

Zhotovitel: 	Valbek, spol. s r.o. Vaňurova 505/17 460 07 Liberec 3
--	--

	Ypracoval	ING. M. HRUBŮŇ	Zak. číslo	21-113-001
	Zodp. projektant	ING. T. KLIMENT	Datum	02/2025
	Tech. kontrola	ING. M. HANŽL	Stupeň	PDPŠ
	Akce		Počet fórmátů	18 x A4
I/16 MLADÁ BOLESLAV - MARTINOVICE			Měřítko	1 : 2 000
			C. přílohy	Pare
Zhotovitel: Valbek, spol. s r.o. Vytváření SdG17 460 017 Šternberk 3	Příloha	SITUACE km 2,500 - 5,500	2.2	