


SO 101 - SILNICE I/16 MLADÁ BOLESLAV - MARTINOVICE
SITUACE km 5,500 - 8,200, M 1 : 2 000



LEGENDA:

PLOCHY

- VOZOVKA - ASFALTOVÝ KRYT
- VOZOVKA - FRÉZOVANÁ
- VOZOVKA - CYKLISTICKÁ STEZKA
- VOZOVKA - POLNÍ CESTY
- CHODNÍK
- DLAŽBA VOZOVKY
- SVAHY VÝKOPU
- SVAHY NÁSPY
- VEGETAČNÍ ÚPRAVY

NOVÉ IS

- DEŠŤOVÁ KANALIZACE
- MELIORACE
- VÝTLAK
- VODOVOD
- NADZEMNÍ VEDENÍ NN
- NADZEMNÍ VEDENÍ VN
- PODZEMNÍ VEDENÍ NN
- PODZEMNÍ SDĚLOVACÍ VEDENÍ
- PLYNOVOD - STL

STÁVAJÍCÍ IS - INFORMATIVNÍ ZÁKRES

- PODZEMNÍ VEDENÍ NN
- PODZEMNÍ VEDENÍ VN
- NADZEMNÍ VEDENÍ NN
- NADZEMNÍ VEDENÍ VN
- NADZEMNÍ VEDENÍ VVN
- DEŠŤOVÁ KANALIZACE
- PLYNOVOD - STL
- PODZEMNÍ SDĚLOVACÍ VEDENÍ
- VODOVOD

KATASTR NEMOVITOSTÍ

- HRANICE K.Ú.
- HRANICE PARCEL
- TRVALÝ ZÁBOR
- DOČASNÝ ZÁBOR DO 1 ROKU

Souřadnicový systém: S-JTSK
Výškový systém: Bpv

SO 101 Silnice I/16 Mladá Boleslav - Martinovice

Objednatel: Ředitelství silnic a dálnic
Ředitelství silnic a dálnic s. p.
Čerňanská 2023/12, Krč, 140 00 Praha 4

Zhotovitel: Valbek
Valbek, spol. s r.o.
Vaňurova 505/17
460 07 Liberec 3

Vypracoval	ING. M. HRUBOŇ	Zak. číslo	21-L113-001
Zodp. projektant	ING. T. KLIMENT	Datum	02/2025
Tech. kontrola	ING. M. HANŽL	Stupeň	PPPS
Akce	I/16 MLADÁ BOLESLAV - MARTINOVICE	Počet formátů	16 x A4
		Měřítko	1 : 2 000
		C. přílohy	Paré

Zhotovitel: Valbek, spol. s r.o.
Vaňurova 505/17
460 07 Liberec 3

Příloha: SITUACE km 5,500 - 8,200

2.3