
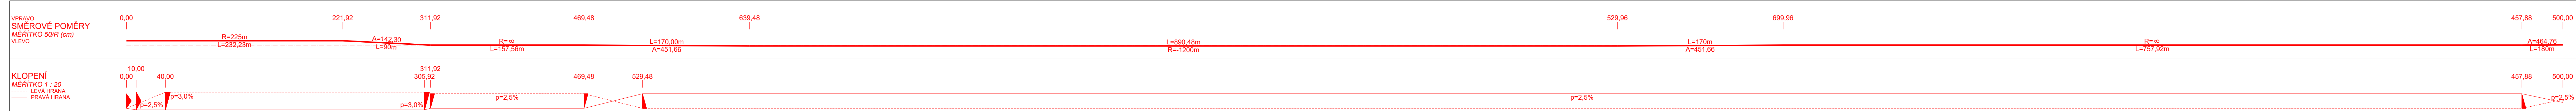


SO 101 - SILNICE I/16 MLADÁ BOLESLAV - MARTINOVICE  
PODÉLNÝ PROFIL km 0,000 - 2,500, M 1 : 2 000 / 200

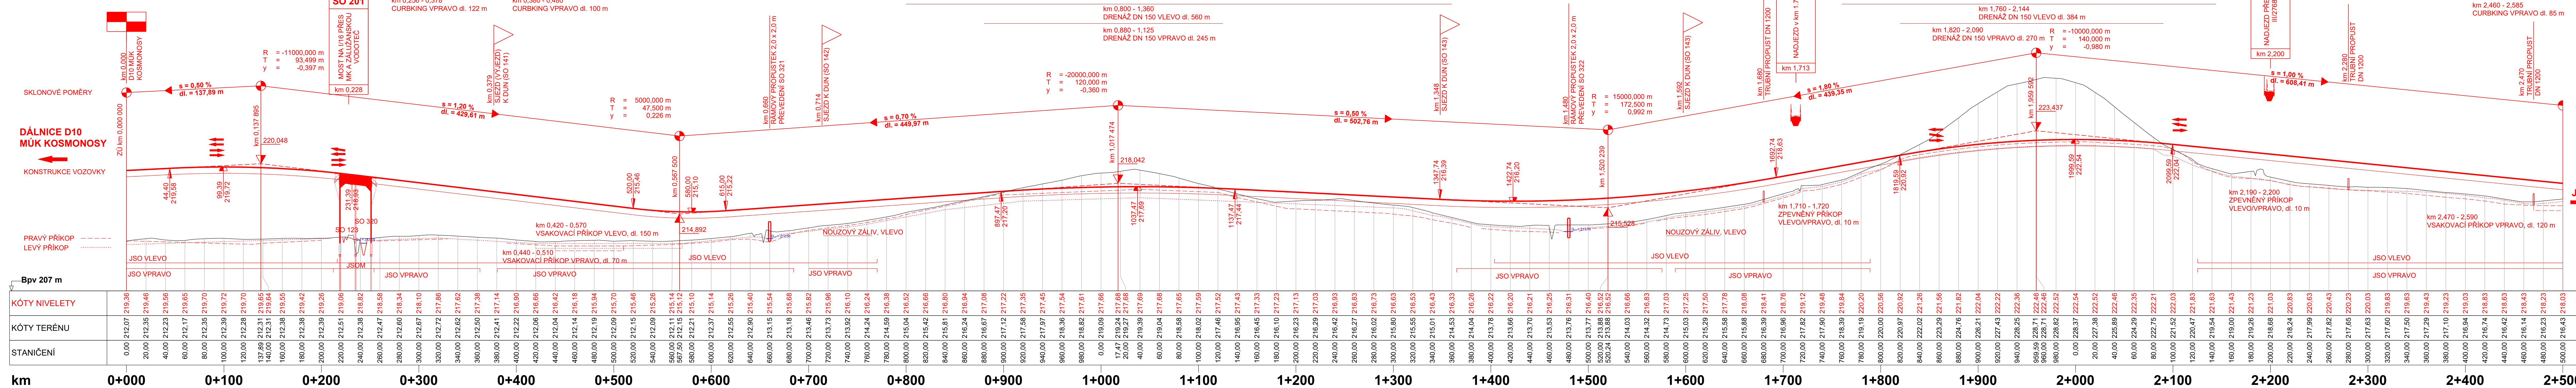

Výškový systém: Bpv

SO 101 Silnice I/16 Mladá Boleslav - Martinovice

Objednatel:

**ŘEDITELSTVÍ SILNIC A DÁLNIC**

Ředitelství silnic a dálnic s. p.  
Čerčanská 2023/12, Krč, 140 00 Praha 4

Zhotovitel:

**Valbek**

Valbek, spol. s r.o.  
Vaňurova 505/17  
460 07 Liberec 3

Vypracoval: ING. M. HRUBOŇ  
Zodp. projektant: ING. T. KLIMENT  
Tech. kontrola: ING. M. HANŽL  
Akce: I/16 MLADÁ BOLESLAV - MARTINOVICE  
Zhotovitel: Valbek, spol. s r.o.  
Vaňurova 505/17  
460 07 Liberec 3

Zak. číslo: 21-L113-001  
Datum: 02/2025  
Stupeň: PDPS  
Počet formátů: 8 x A4  
Měřítko: 1 : 2000 / 200  
Č. přílohy: Paré

3.1