


SO 101 - SILNICE I/16 MLADÁ BOLESLAV - MARTINOVICE
PODÉLNÝ PROFIL km 2,500 - 5,500, M 1 : 2 000 / 200



Výškový systém: Bpv

SO 101

Silnice I/16 Mladá Boleslav - Martinovice

Objednatel:



Ředitelství silnic a dálnic s. p.
Čerčanská 2023/12, Krč, 140 00 Praha 4

Zhotovitel:



Valbek, spol. s r.o.
Vaňurova 505/17
460 07 Liberec 3

	Vypracoval	ING. M. HRUBÝ	Zak. číslo	21-L113-001
	Zodp. projektant	ING. T. KLIMENT	Datum	02/2025
	Tech. kontrola	ING. M. HANŽL	Stupeň	PDP3
	Akce	I/16 MLADÁ BOLESLAV - MARTINOVICE		
Zhotovitel: Valbek, spol. s r.o. Vaňurova 505/17 460 07 Liberec 3	Příloha			3.2
	PODÉLNÝ PROFIL km 2,500 - 5,500			