


SO 101 - SILNICE I/16 MLADÁ BOLESLAV - MARTINOVICE
PODÉLNÝ PROFIL km 5,500 - 8,200, M 1 : 2 000 / 200



Výškový systém: Bpv

SO 101 Silnice I/16 Mladá Boleslav - Martinovice

ŘEDITELSTVÍ SILNIC A DÁLNIC

Ředitelství silnic a dálnic s. p.
Čerťanská 2023/12, Křč, 140 00 Praha 4

Valbek

Valbek, spol. s r.o.
Vaňurova 505/17
460 07 Liberec 3

Valbek

I/16 MLADÁ BOLESLAV - MARTINOVICE

PODÉLNÝ PROFIL km 5,500 - 8,200

Zak. číslo 21-L113-001

Datum 02/2025

Stupeň PDPS

Počet formátů 16 x A4

Měřítko 1 : 2000 / 200

Č. přílohy Paré

3.3