


SO 101 - SILNICE I/16 MLADÁ BOLESLAV - MARTINOVICE
VZOROVÉ PŘÍČNÉ ŘEZY, M 1 : 100

NÁVRHOVÁ KATEGORIE S 13,5/90
USPOŘÁDÁNÍ 2+1 V NÁSYPU


TRÍDA DOPRAVNÍHO ZATÍŽENÍ I
NÁVRHOVÁ ÚROVEŇ PORUŠENÍ DO
D0-A-3 PIII

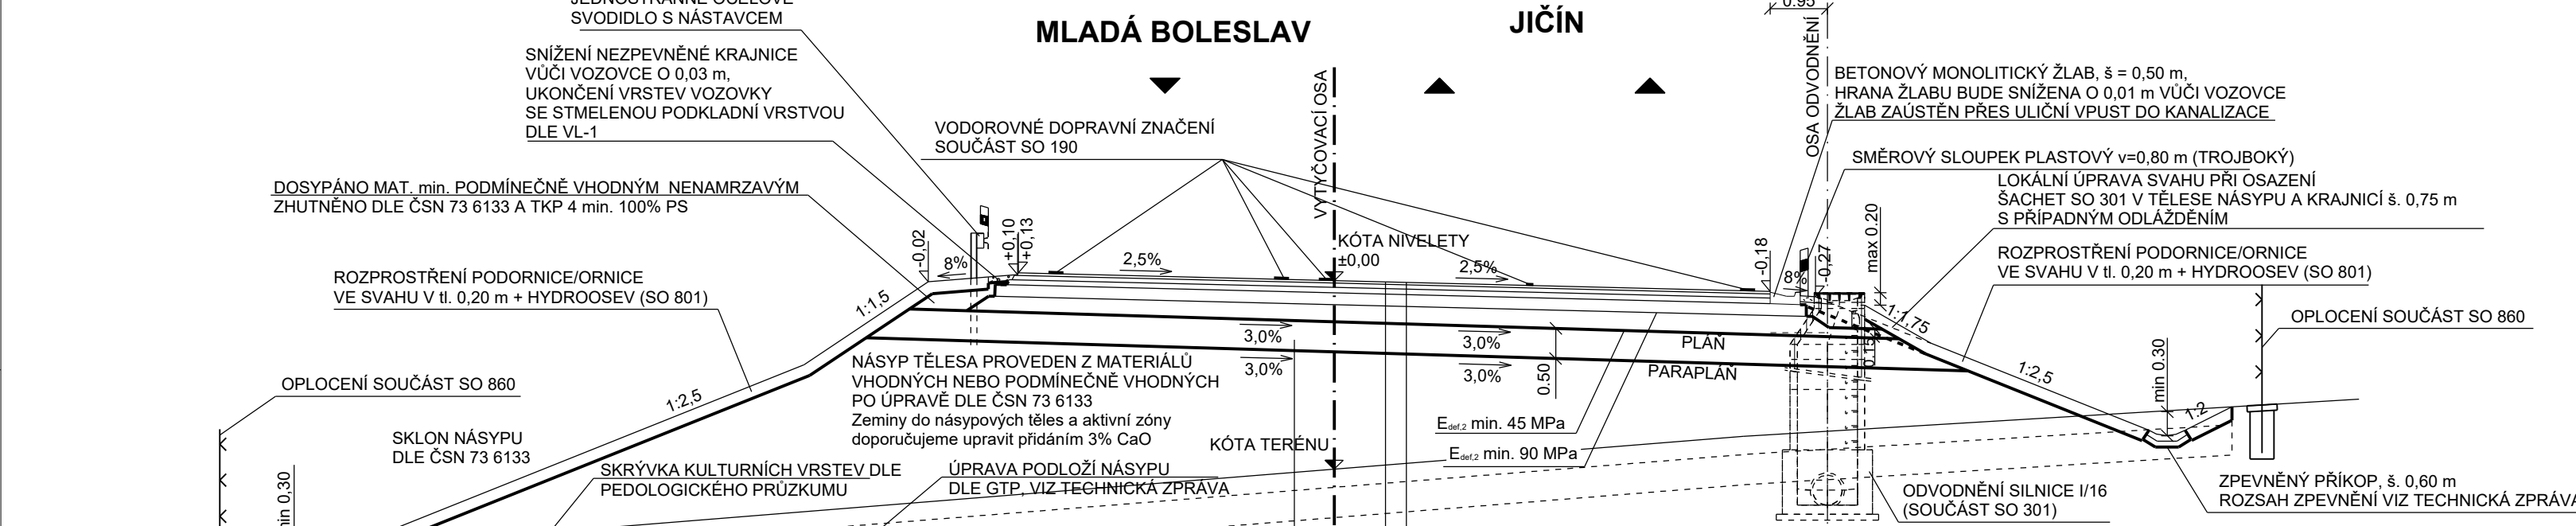

SO 101 - SILNICE I/16 MLADÁ BOLESLAV - MARTINOVICE - NÁPOJENÍ NA MÚK KOSMONOSY (km 0,050 - KÚ)			
ASFALTOVÝ KOBEREK MASTIXOVÝ MODIFIKOVANÝ S PODRCENÍM POVRCHU KAMENIVO fr. 2/4 V MNOŽSTVÍ 1,5 kg/2	SMA 11 S PMB 45/80-65	40 mm	ČSN EN 13 108-5, ČSN 73 6121
SPOJOVACÍ POSTŘIK EMULZNÍ STŘEDNĚŠTĚPNÝ S MODIFIKOVANÝM ASFALTEM	PS-CP	0,35 kg/m ²	ČSN EN 13 808, ČSN 73 6129, ČSN 73 6132
ASFALTOVÝ BETON MODIFIKOVANÝ PRO LOŽNÍ VRSTVU	ACL 22 S PMB 25/55-60	80 mm	ČSN EN 13 108-1, ČSN 73 6121
SPOJOVACÍ POSTŘIK EMULZNÍ STŘEDNĚŠTĚPNÝ S MODIFIKOVANÝM ASFALTEM	PS-CP	0,35 kg/m ²	ČSN EN 13 808, ČSN 73 6129, ČSN 73 6132
ASFALTOVÝ BETON PRO PODKLADNÍ VRSTVU	ACP 22 S 50/70	80 mm	ČSN EN 13 108-1, ČSN 73 6121
SMĚS Z KAMENIVA STMELENÁ CEMENTEM	SC 0/32 C ₄₀	190 mm	ČSN EN 14 227-1, ČSN 73 6124-1
ŠTERKODRT fr. A	ŠD, 0/32 G ₄	min. 250 mm	ČSN EN 13 285, ČSN 73 6126-1
CELKEM		min. 640 mm	
POZN. NA PODKLADNÍCH VRSTVÁCH Z SC PROVĚST OPATŘENÍ K VÝVOJI REFLEXNÍCH TRHLIN DLE TP 170, ČSN 73 6124-1. POZN. OŠETŘENÍ OKRAJOVÝCH HRAN, PRACOVNÍCH SPOJŮ A PRACOVNÍCH STYKŮ VOZOVKY BUDE PROVEDENO V SOULADU S ČSN 73 6101, KAP. 5.7			

NÁVRHOVÁ KATEGORIE S 13,5/90
USPOŘÁDÁNÍ 2+1 V ZÁŘEZU


TRÍDA DOPRAVNÍHO ZATÍŽENÍ I
NÁVRHOVÁ ÚROVEŇ PORUŠENÍ DO
D0-A-3 PIII

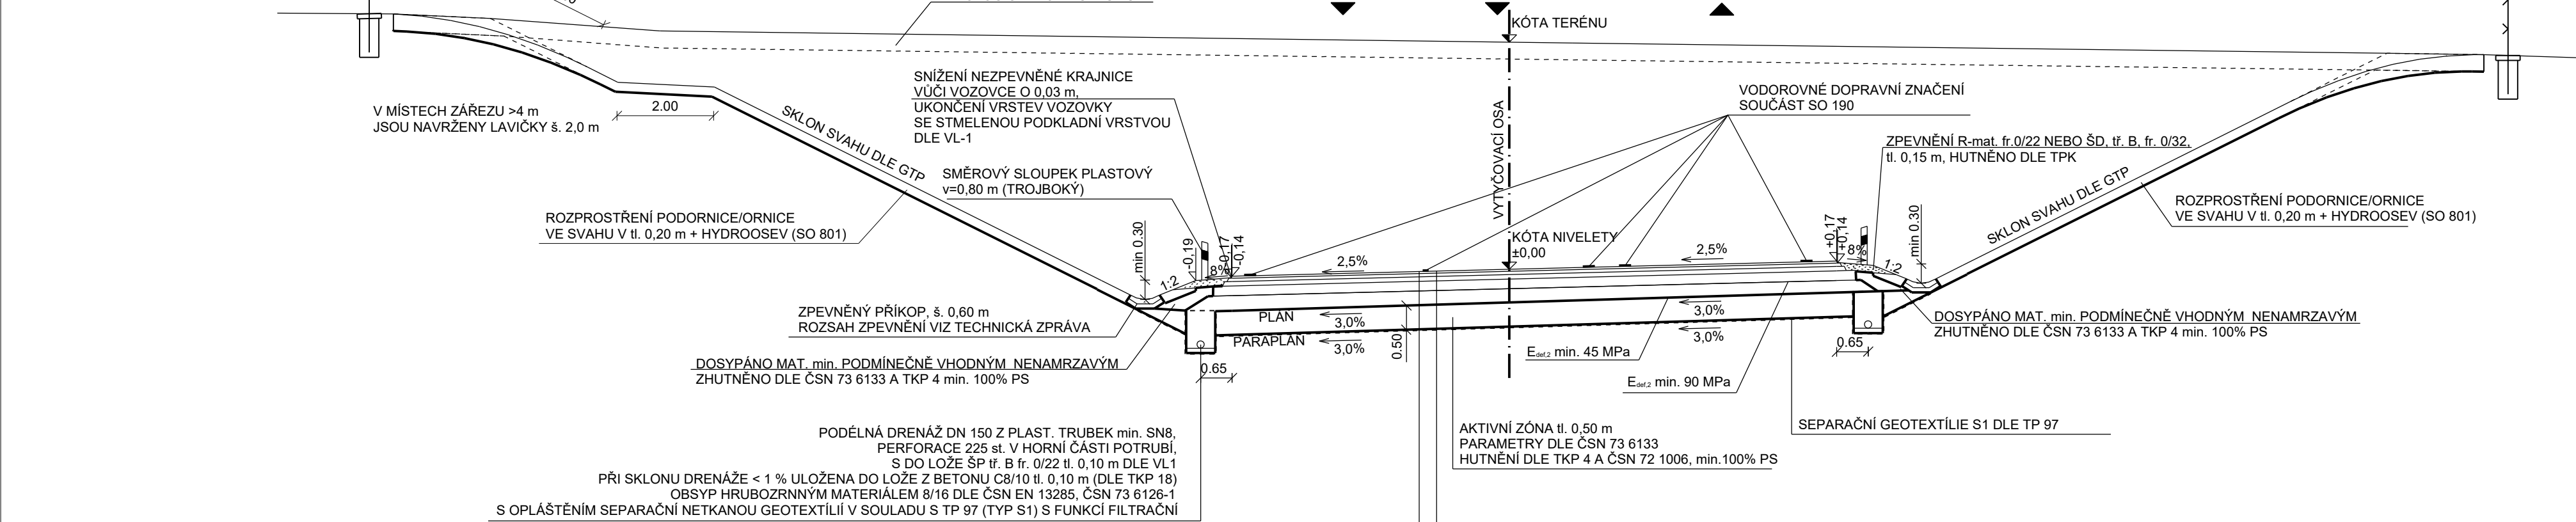


SO 101 - SILNICE I/16 MLADÁ BOLESLAV - MARTINOVICE - NÁPOJENÍ NA MÚK KOSMONOSY (km 0,050 - KÚ)			
ASFALTOVÝ KOBEREK MASTIXOVÝ MODIFIKOVANÝ S PODRCENÍM POVRCHU KAMENIVO fr. 2/4 V MNOŽSTVÍ 1,5 kg/2	SMA 11 S PMB 45/80-65	40 mm	ČSN EN 13 108-5, ČSN 73 6121
SPOJOVACÍ POSTŘIK EMULZNÍ STŘEDNĚŠTĚPNÝ S MODIFIKOVANÝM ASFALTEM	PS-CP	0,35 kg/m ²	ČSN EN 13 808, ČSN 73 6129, ČSN 73 6132
ASFALTOVÝ BETON MODIFIKOVANÝ PRO LOŽNÍ VRSTVU	ACL 22 S PMB 25/55-60	80 mm	ČSN EN 13 108-1, ČSN 73 6121
SPOJOVACÍ POSTŘIK EMULZNÍ STŘEDNĚŠTĚPNÝ S MODIFIKOVANÝM ASFALTEM	PS-CP	0,35 kg/m ²	ČSN EN 13 808, ČSN 73 6129, ČSN 73 6132
ASFALTOVÝ BETON PRO PODKLADNÍ VRSTVU	ACP 22 S 50/70	80 mm	ČSN EN 13 108-1, ČSN 73 6121
SMĚS Z KAMENIVA STMELENÁ CEMENTEM	SC 0/32 C ₄₀	190 mm	ČSN EN 14 227-1, ČSN 73 6124-1
ŠTERKODRT fr. A	ŠD, 0/32 G ₄	min. 250 mm	ČSN EN 13 285, ČSN 73 6126-1
CELKEM		min. 640 mm	
POZN. NA PODKLADNÍCH VRSTVÁCH Z SC PROVĚST OPATŘENÍ K VÝVOJI REFLEXNÍCH TRHLIN DLE TP 170, ČSN 73 6124-1. POZN. OŠETŘENÍ OKRAJOVÝCH HRAN, PRACOVNÍCH SPOJŮ A PRACOVNÍCH STYKŮ VOZOVKY BUDE PROVEDENO V SOULADU S ČSN 73 6101, KAP. 5.7			

SO 101 - SILNICE I/16 MLADÁ BOLESLAV - MARTINOVICE - NÁPOJENÍ NA MÚK KOSMONOSY (km 0,000 - 0,050)			
ASFALTOVÝ KOBEREK MASTIXOVÝ MODIFIKOVANÝ S PODRCENÍM POVRCHU KAMENIVO fr. 2/4 V MNOŽSTVÍ 1,5 kg/2	SMA 11 S PMB 45/80-65	40 mm	ČSN EN 13 108-5, ČSN 73 6121
SPOJOVACÍ POSTŘIK EMULZNÍ STŘEDNĚŠTĚPNÝ S MODIFIKOVANÝM ASFALTEM	PS-CP	0,35 kg/m ²	ČSN EN 13 808, ČSN 73 6129, ČSN 73 6132
ASFALTOVÝ BETON MODIFIKOVANÝ PRO LOŽNÍ VRSTVU	ACL 22 S PMB 25/55-60	80 mm	ČSN EN 13 108-1, ČSN 73 6121
SPOJOVACÍ POSTŘIK EMULZNÍ STŘEDNĚŠTĚPNÝ S MODIFIKOVANÝM ASFALTEM	PS-CP	0,35 kg/m ²	ČSN EN 13 808, ČSN 73 6129, ČSN 73 6132
ASFALTOVÝ BETON PRO PODKLADNÍ VRSTVU	ACP 22 S 50/70	80 mm	ČSN EN 13 108-1, ČSN 73 6121
SMĚS Z KAMENIVA STMELENÁ CEMENTEM	SC 0/32 C ₄₀	170 mm	ČSN EN 14 227-1, ČSN 73 6124-1
ŠTERKODRT fr. A	ŠD, 0/32 G ₄	min. 250 mm	ČSN EN 13 285, ČSN 73 6126-1
CELKEM		min. 660 mm	
POZN. NA PODKLADNÍCH VRSTVÁCH Z SC PROVĚST OPATŘENÍ K VÝVOJI REFLEXNÍCH TRHLIN DLE TP 170, ČSN 73 6124-1. POZN. OŠETŘENÍ OKRAJOVÝCH HRAN, PRACOVNÍCH SPOJŮ A PRACOVNÍCH STYKŮ VOZOVKY BUDE PROVEDENO V SOULADU S ČSN 73 6101, KAP. 5.7			


DETAIL V MÍSTĚ PHS

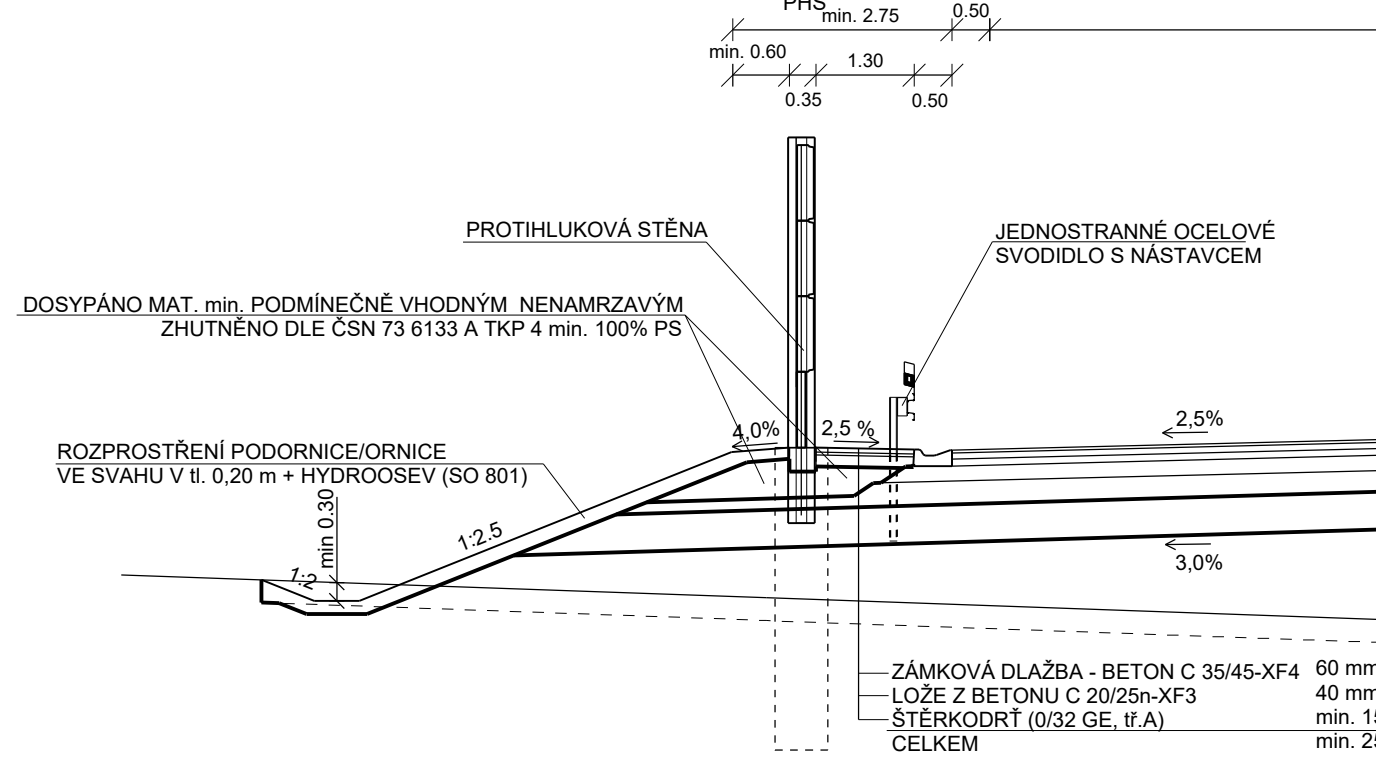


DETAIL PŘÍKOPU V MÍSTĚ VSAKOVÁNÍ

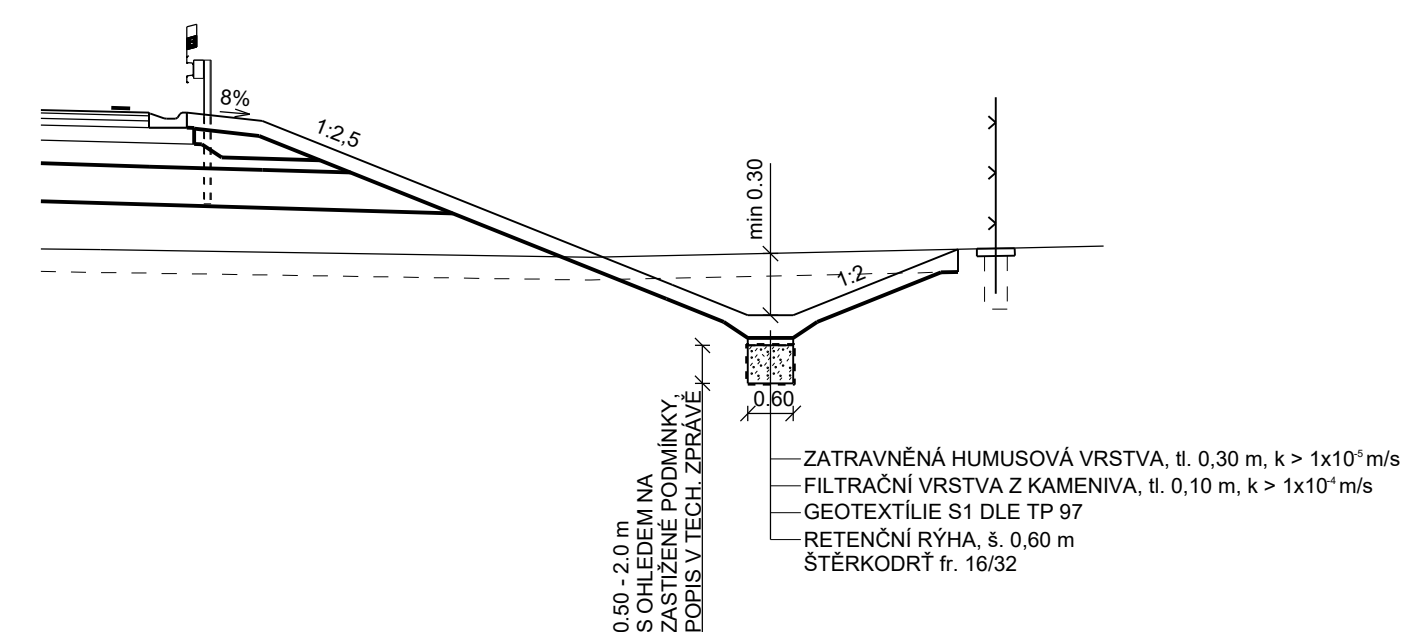


DETAIL NÁPOJENÍ NOVÉ
KONSTRUKCE NA STÁVAJÍCÍ
V PŘÍČNÉM SMĚRU

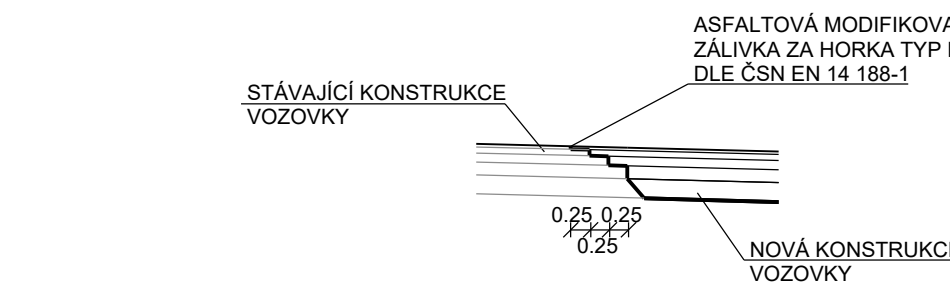


DETAIL NÁPOJENÍ NOVÉ
KONSTRUKCE NA STÁVAJÍCÍ
V PODÉLNÉM SMĚRU

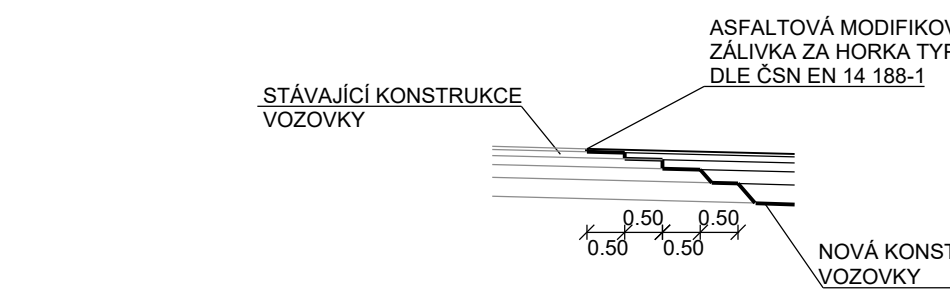


POZNÁMKA:
PŘI SKLONU STÁVAJÍCÍHO TERÉNU, KOLMĚHO NA OSU NÁSYPU, VĚTŠÍHO NEŽ 10 %, MUSÍ BÝT
ZŘÍZENY V PODLOŽÍ NÁSYPU STUPNĚ V S VL 1 32-02

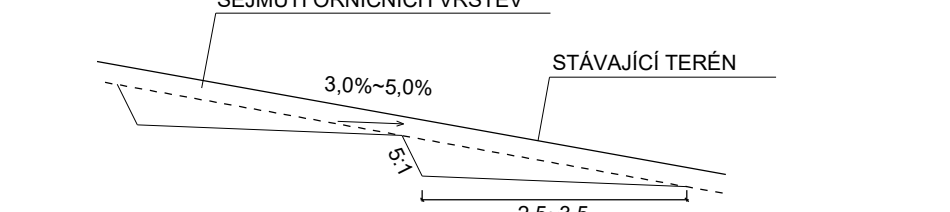


DETAIL DRENÁŽNÍHO PŘÍKOPU
km 1,380 - 1,470 VLEVO
km 3,620 - 3,750 VLEVO
-DLE VL1 54-01

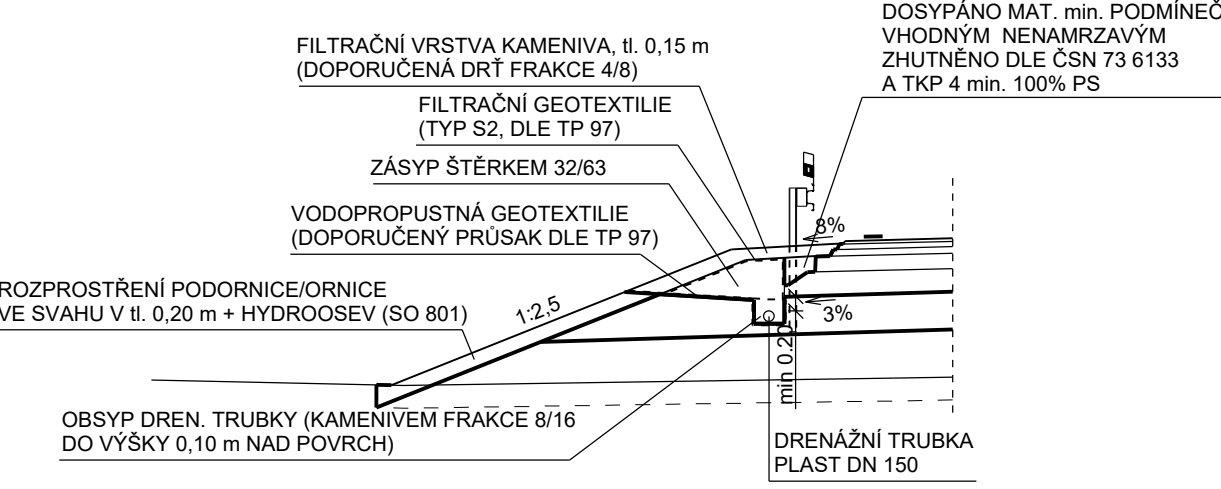


DETAIL VYÚSTĚNÍ DRENÁŽE

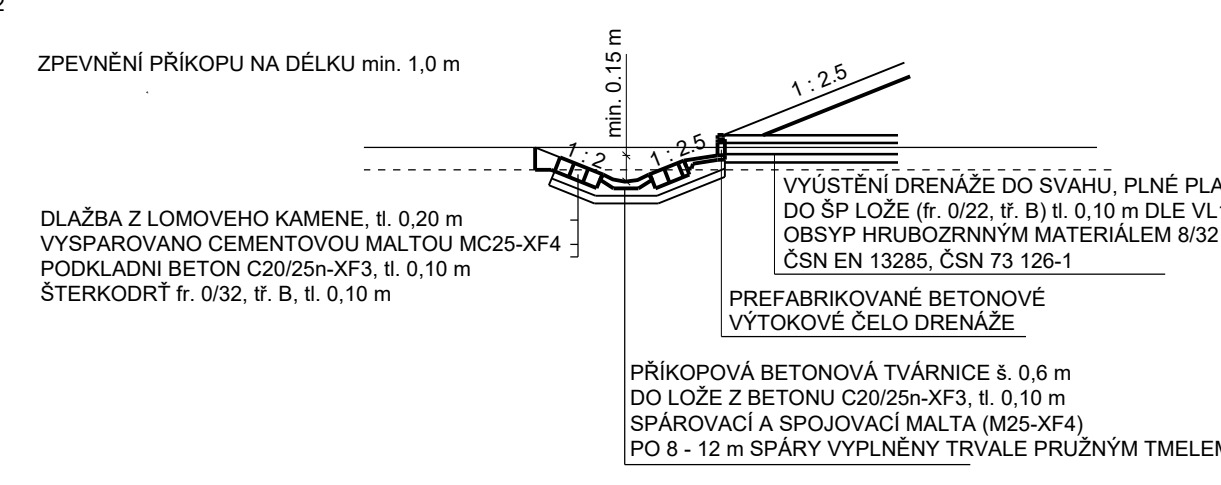

DETAIL STYKU VOZOVKY S MONOLITICKÝM BETONOVÝM ŽLABEM

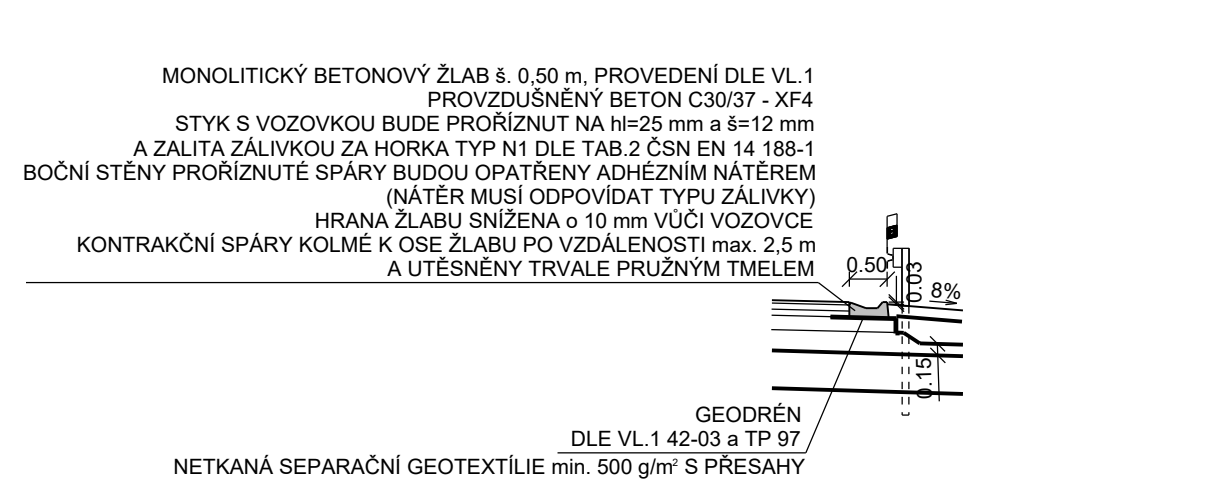


DETAIL ZPEV. PŘÍKOPŮ

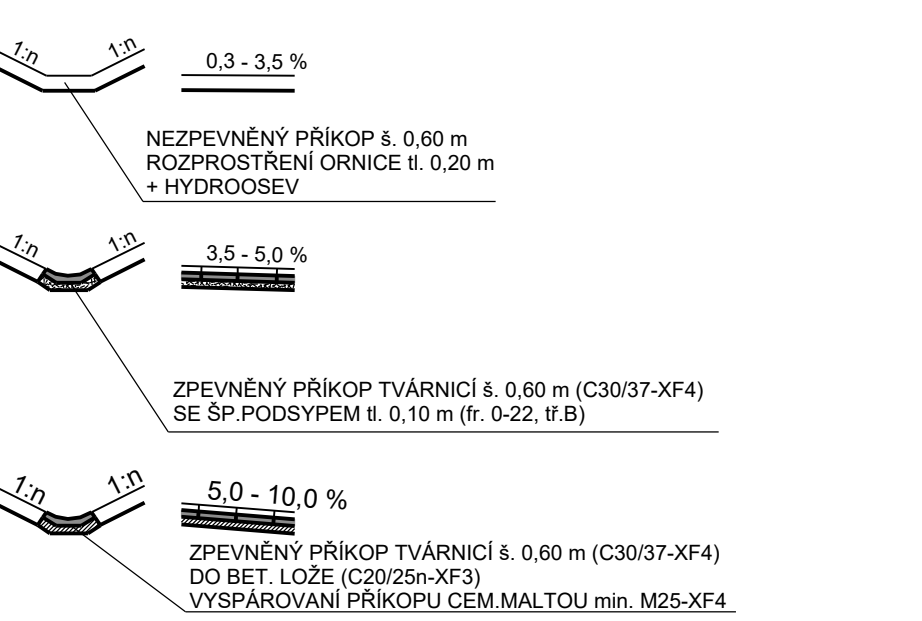


POZNÁMKA:
STŘIDÁNÍ SMĚRU DOPRAVY VE STŘEDNÍM PRUHU V USPOŘÁDÁNÍ 2+1 BUDE PROVEDENO DLE VL 1 15-06,
ÚSEKY VE KTERÝCH BUDE TOTO PROVEDENO JSOU PATRNY Z OBJEKTU SO 190

SNÍŽENÍ POČTU JÍZDNÍCH PRUHŮ V KONCI ÚSEKU BUDE PROVEDENO DLE VL 1 15-05

DETAIL OPĚVNĚNÍ SVAHU
OPEVNĚNÍ POMOCÍ GEOBUNĚK
km 5,000 - 5,080 (MIMO SO 204)
DLE VL1 32-05

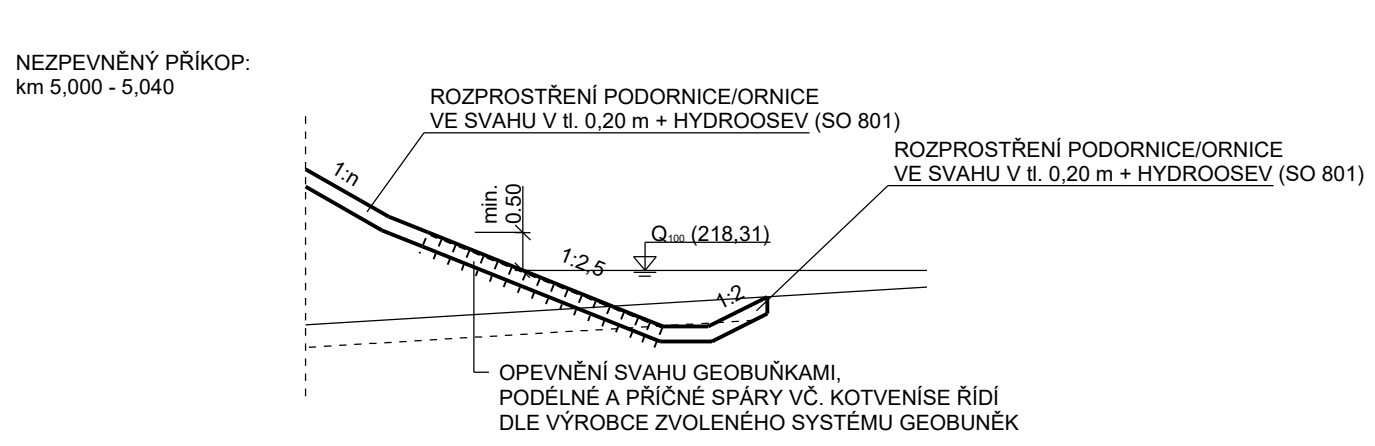

PŘÍKOP ZPEVNĚNÝ ŽLABOVKOU:

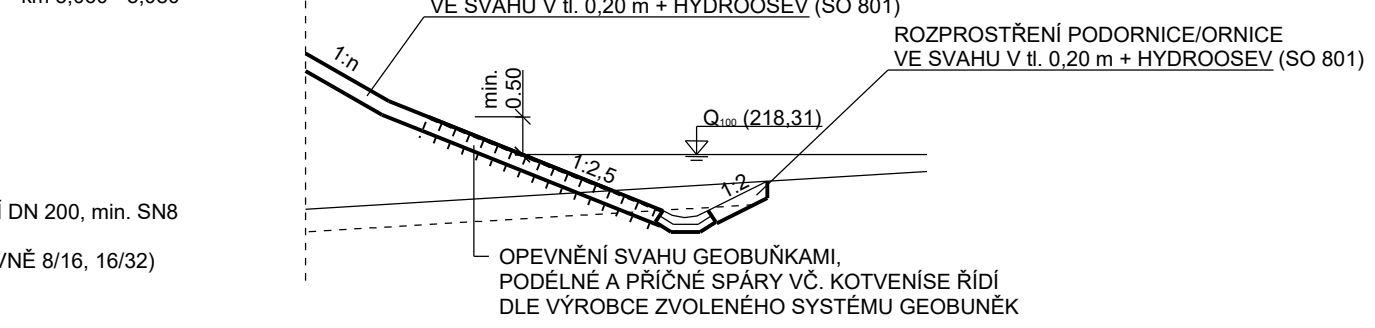

Výškový systém: BpV

SO 101 Silnice I/16 Mladá Boleslav - Martinovice

Objednatel:



Ředitelství silnic a dálnic s. p.
Čerčanská 2023/12, Krč, 140 00 Praha 4

Zhotovitel:



Valbek, spol. s r.o.
Vaňurova 505/17
460 07 Liberec 3



Vypracoval	ING. M. HRUBOŇ	Zak. číslo	21-L113-001
Zodp. projektant	ING. T. KLIMENT	Datum	02/2025
Tech. kontrola	ING. M. HANŽL	Stupeň	PDPs
Akce		Počet formátů	12 x A4
I/16 MLADÁ BOLESLAV - MARTINOVICE		Měřítko	1 : 100
Příloha		Č. přílohy	Paré
Zhotovitel:		4	
Valbek, spol. s r.o. Vaňurova 505/17 460 07 Liberec 3			
VZOROVÉ PŘÍČNÉ ŘEZY			