SO 101 - SILNICE I/16 MLADÁ BOLESLAV - MARTINOVICE
PŘÍČNÉ ŘEZY km 0,100 - 1,800, M 1 : 200

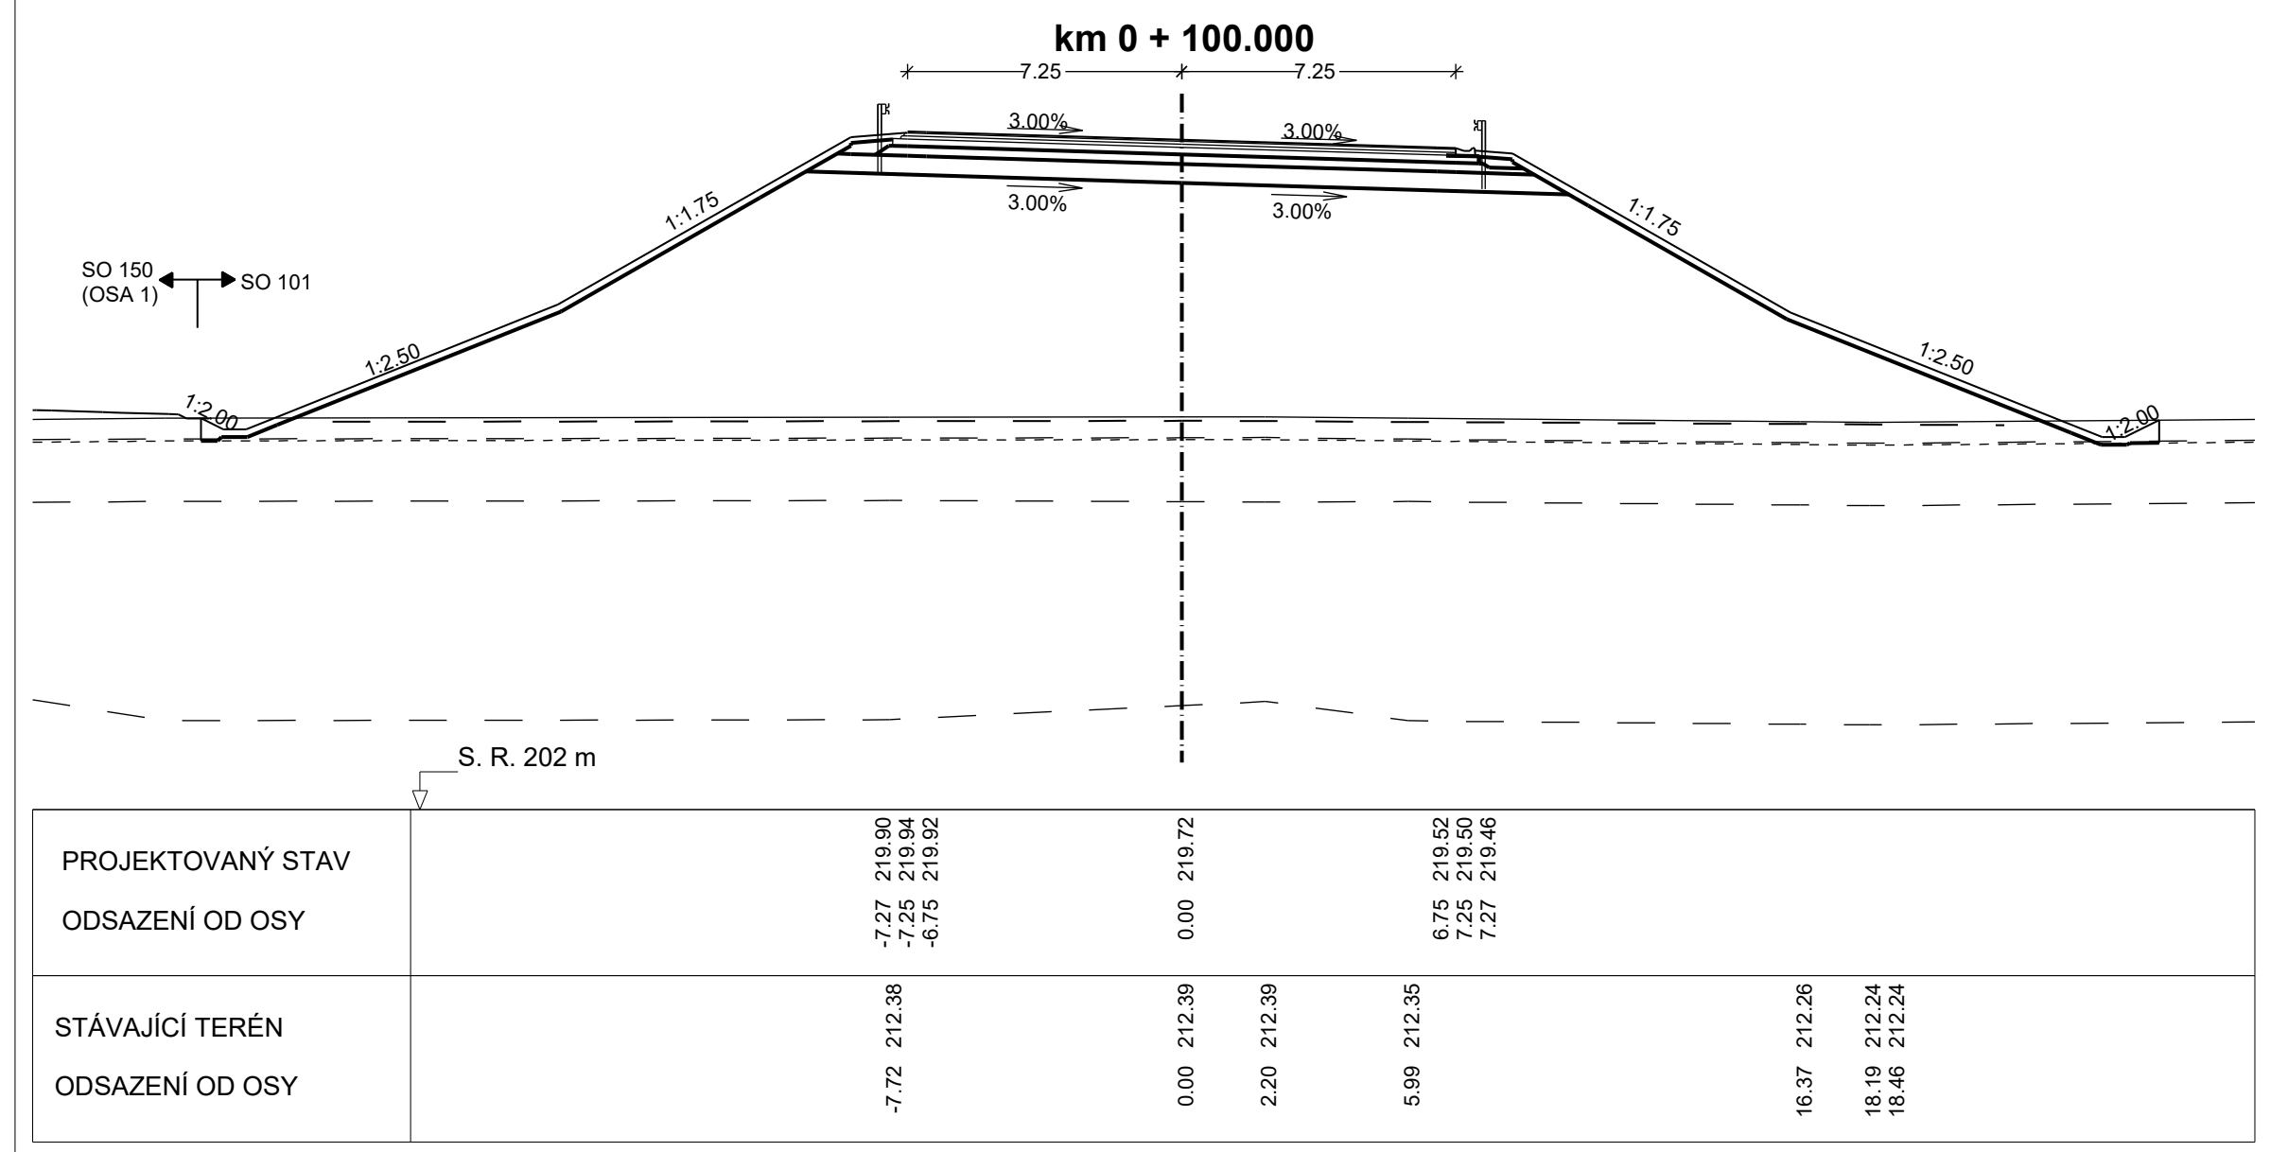

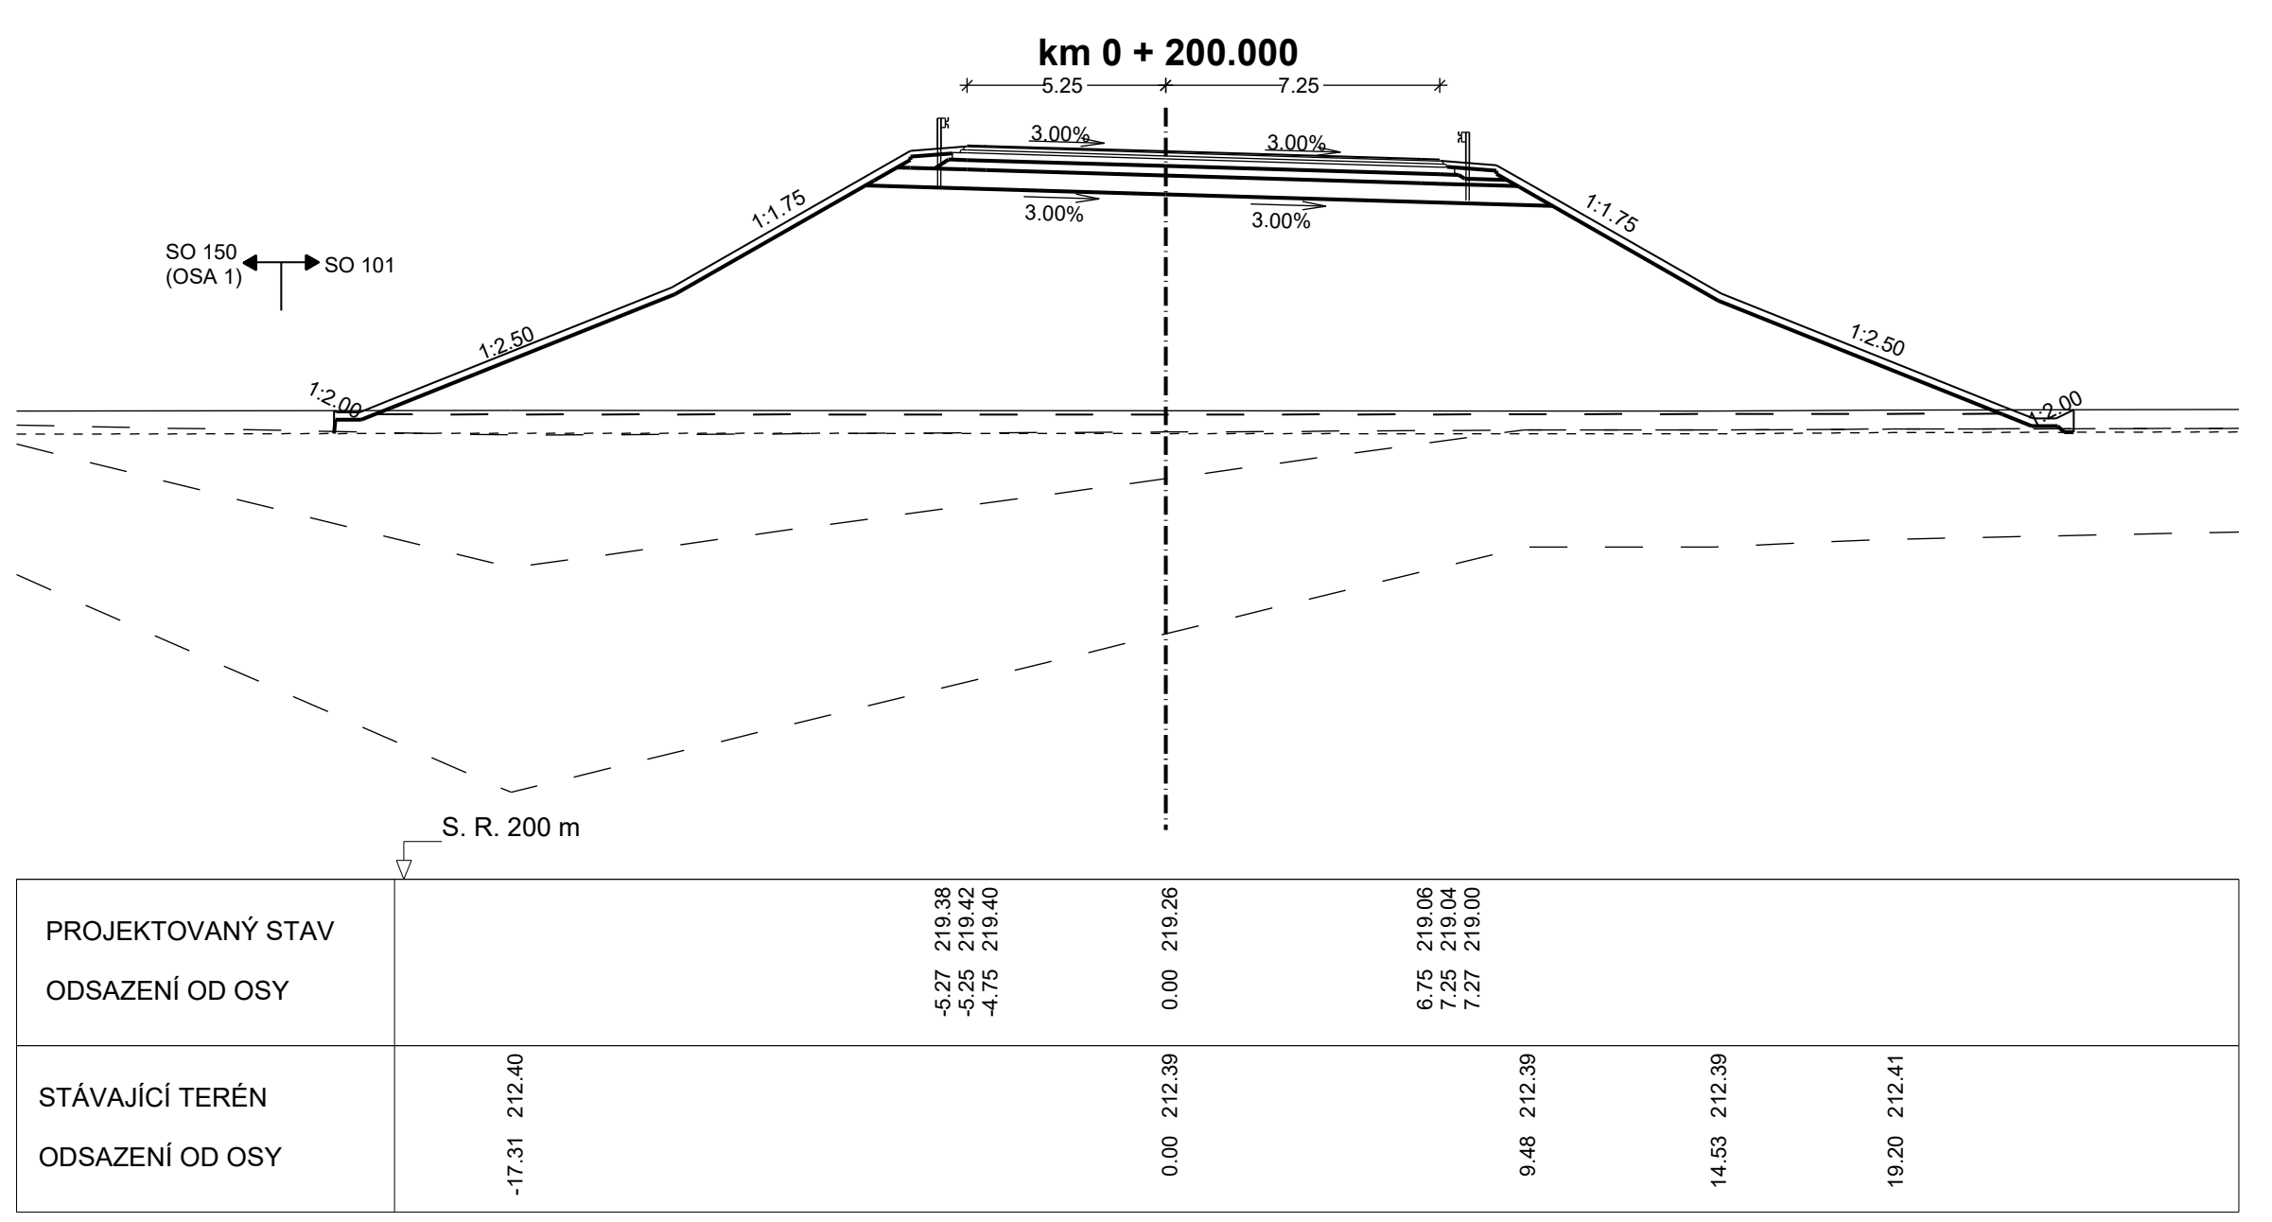

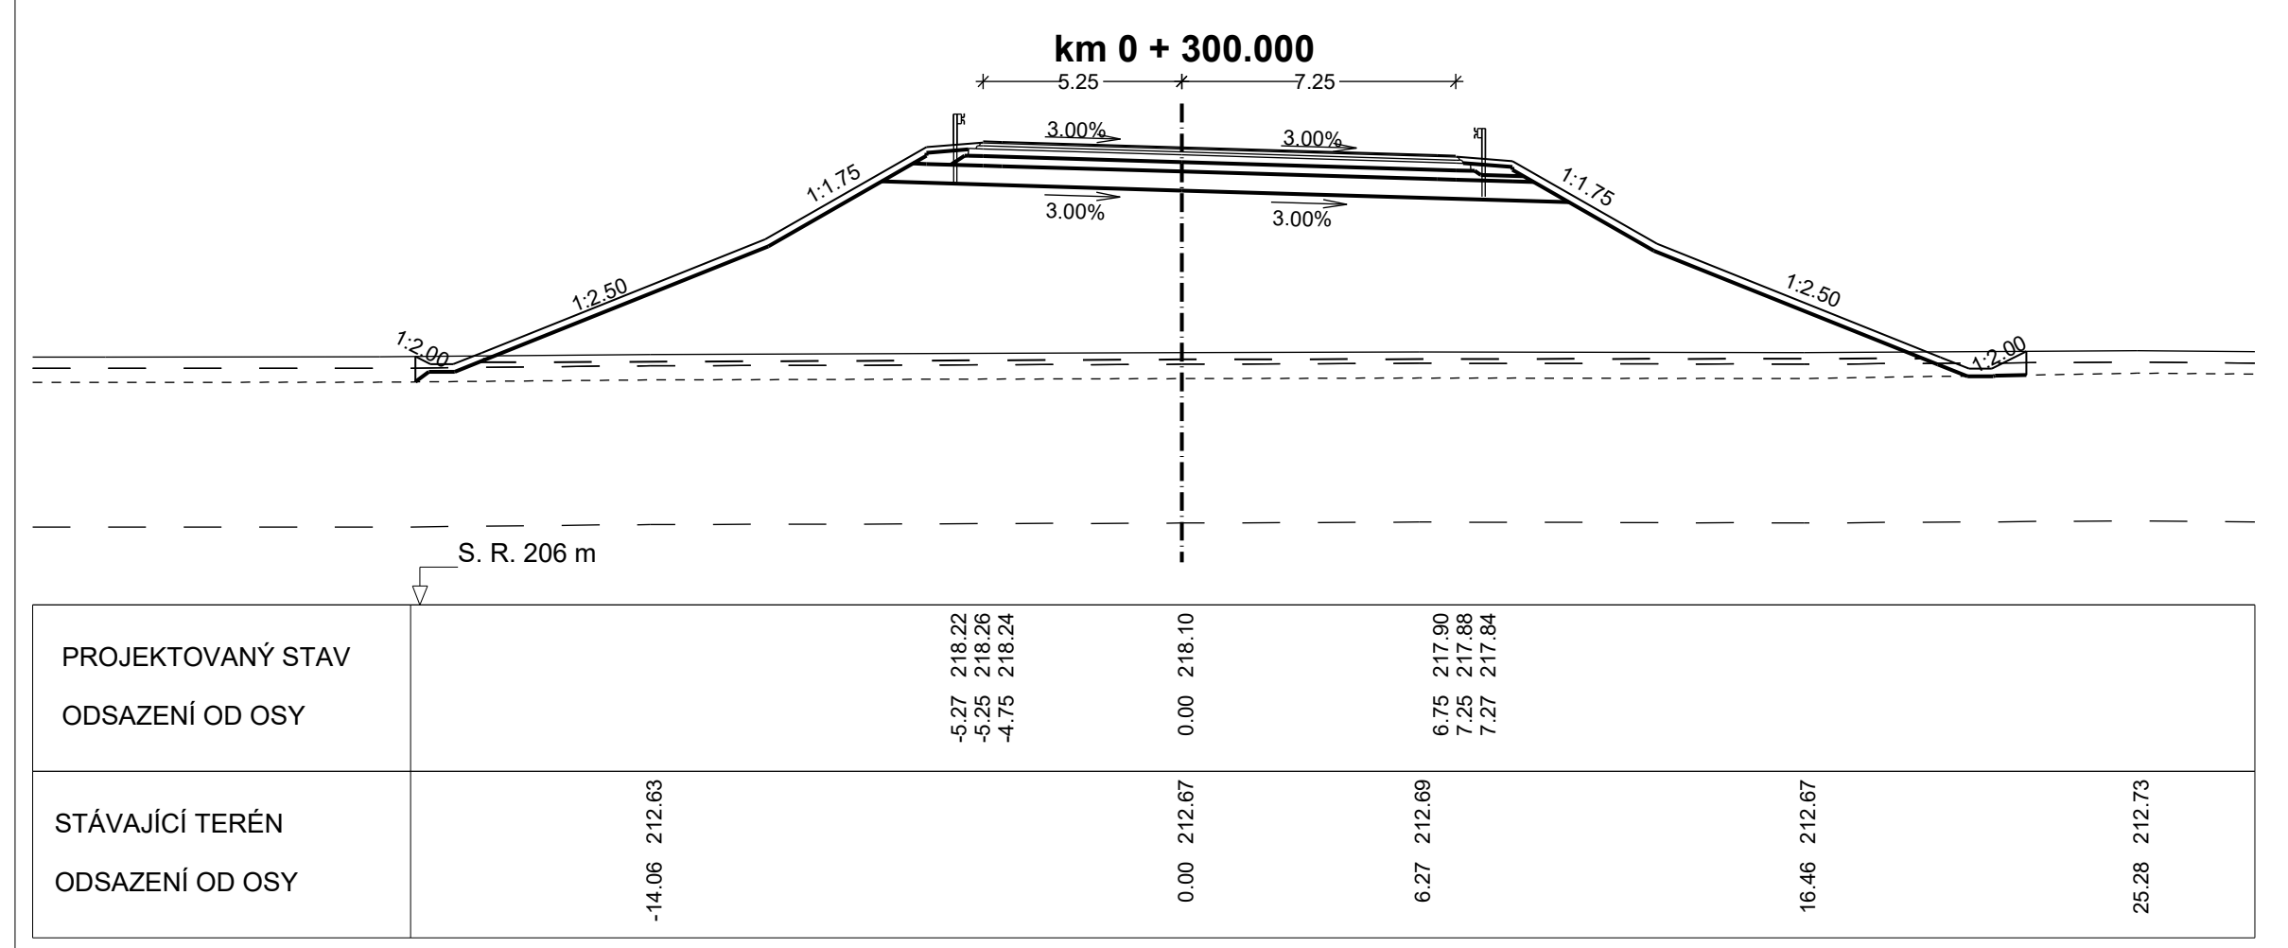

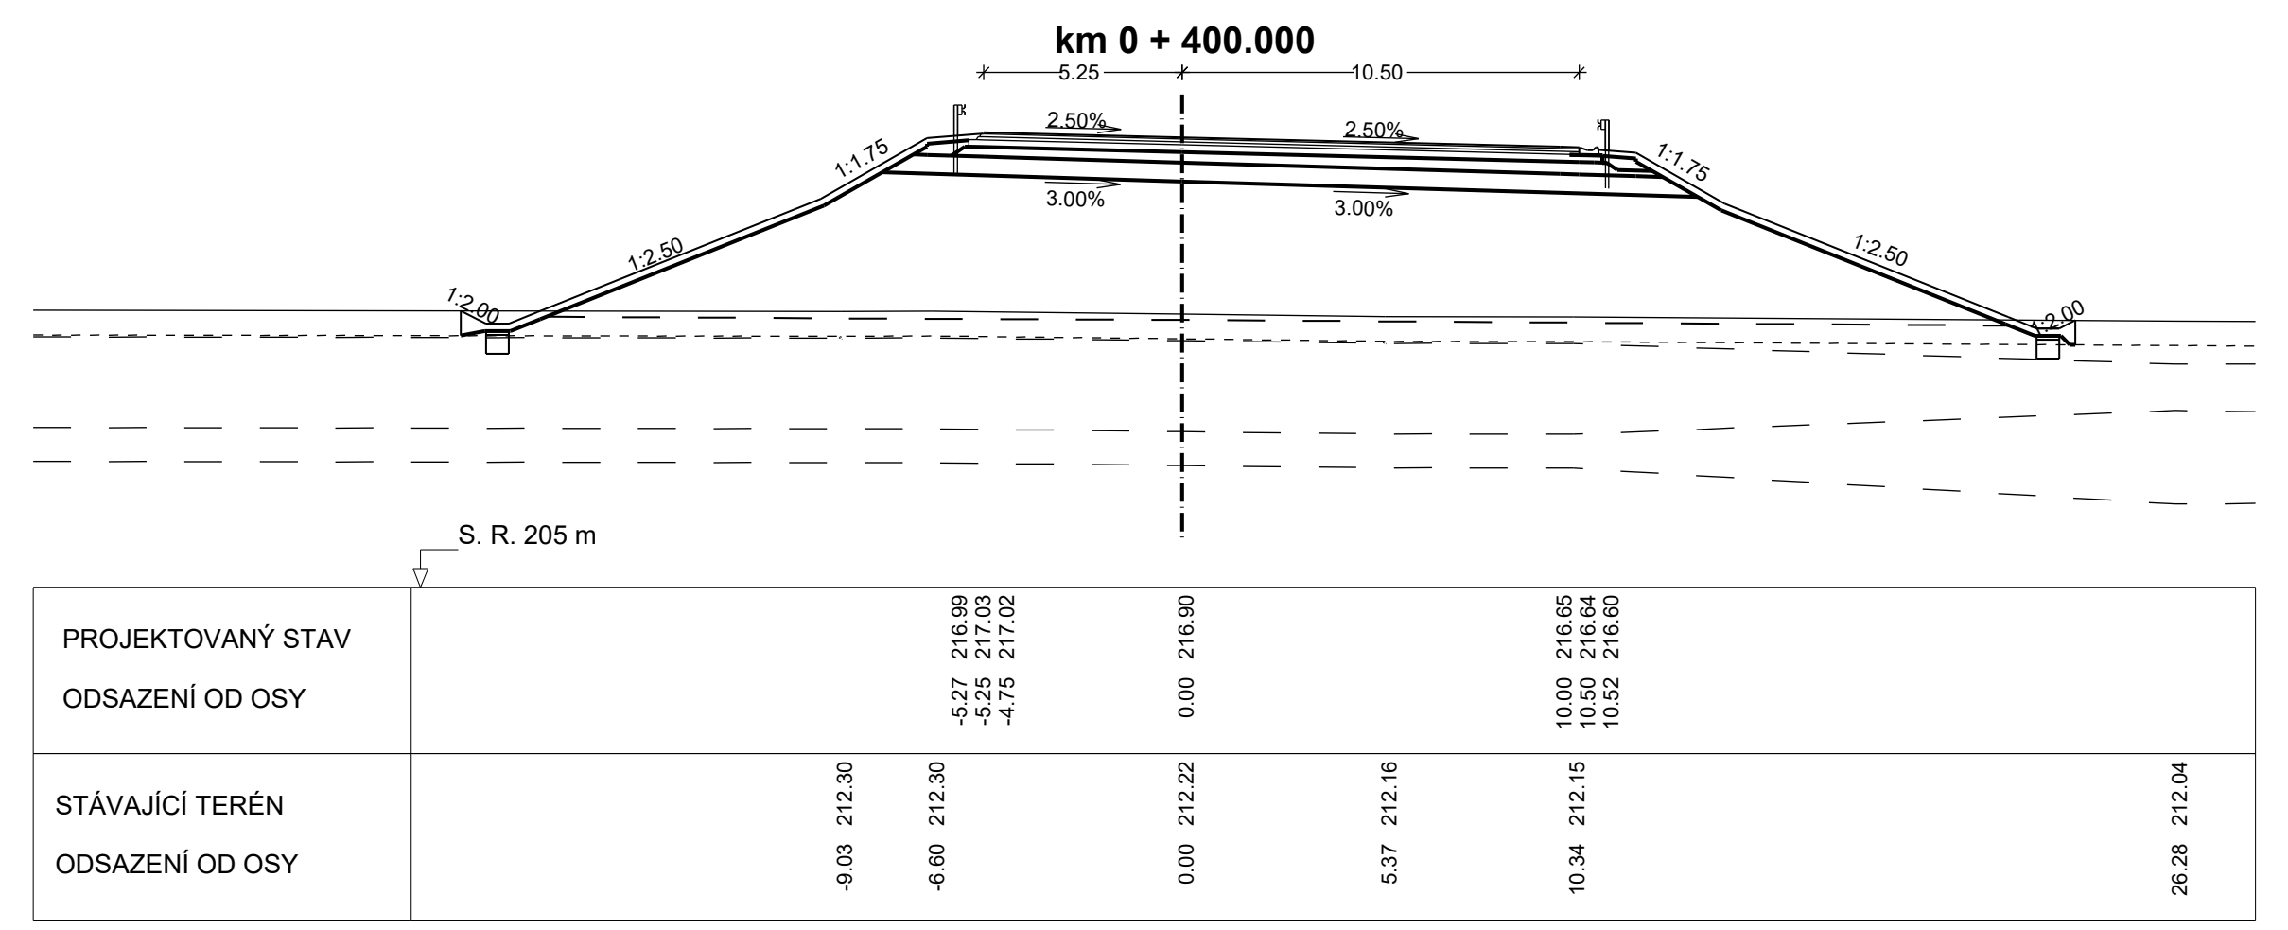

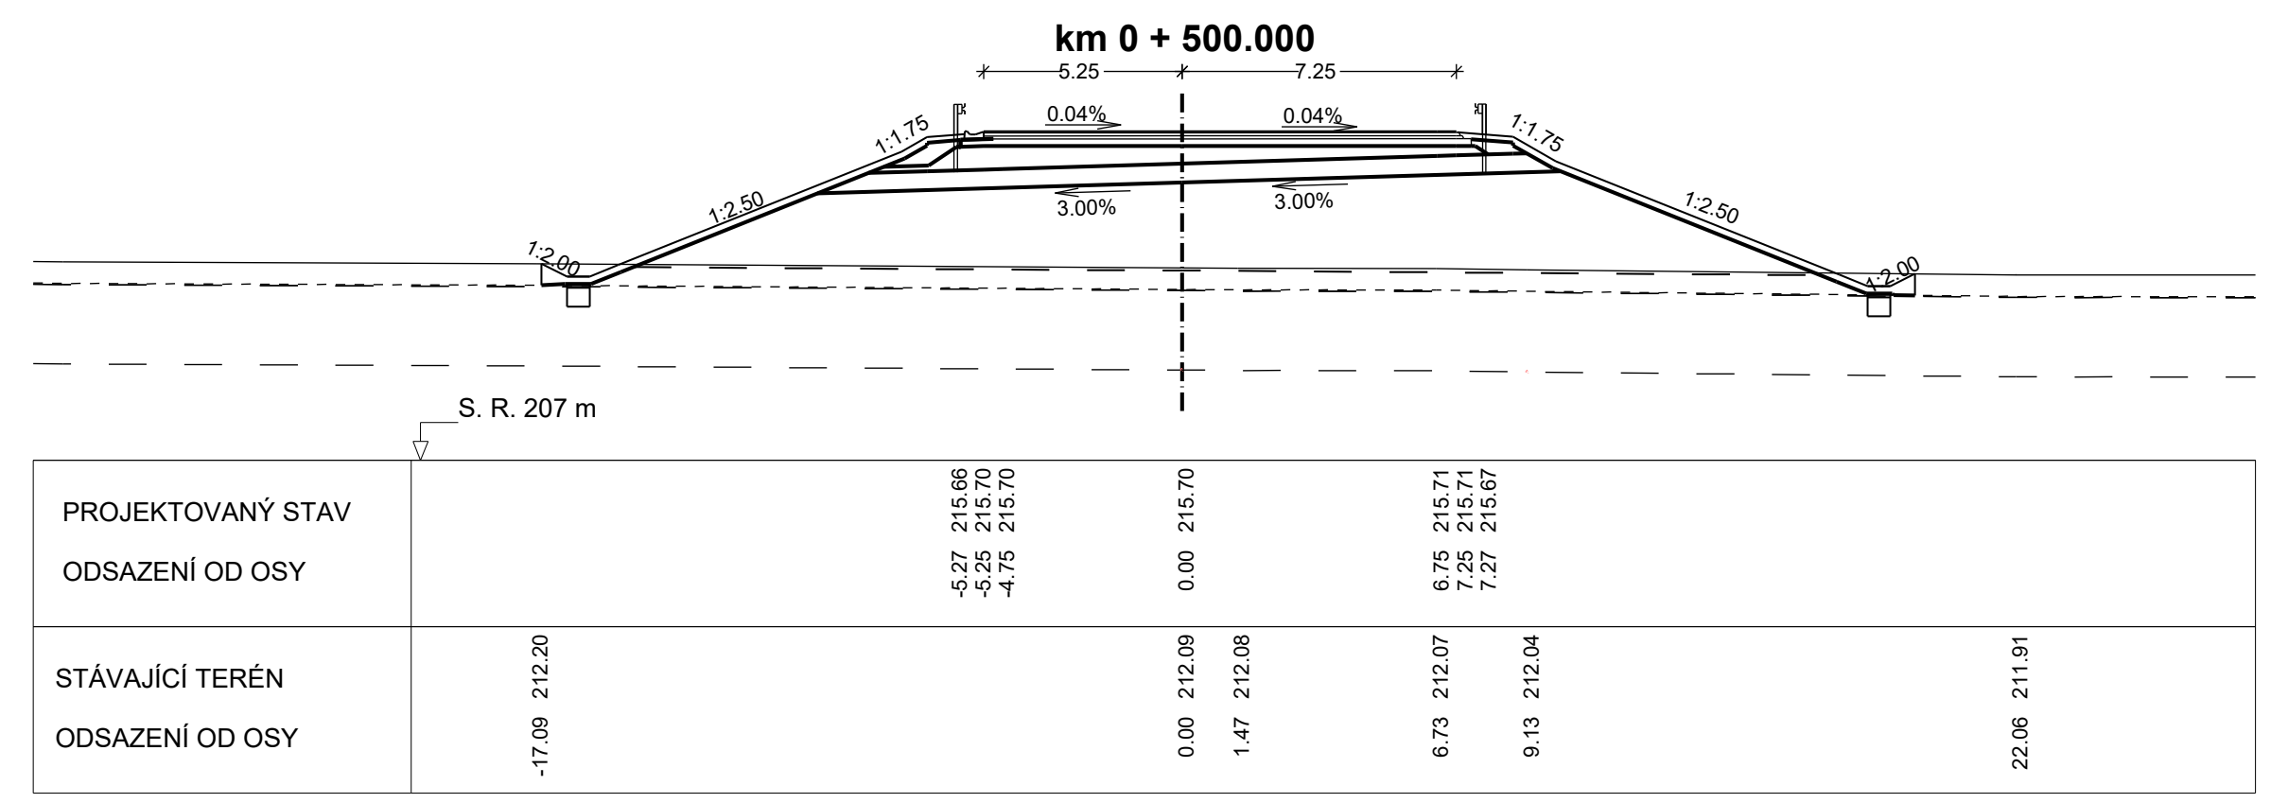

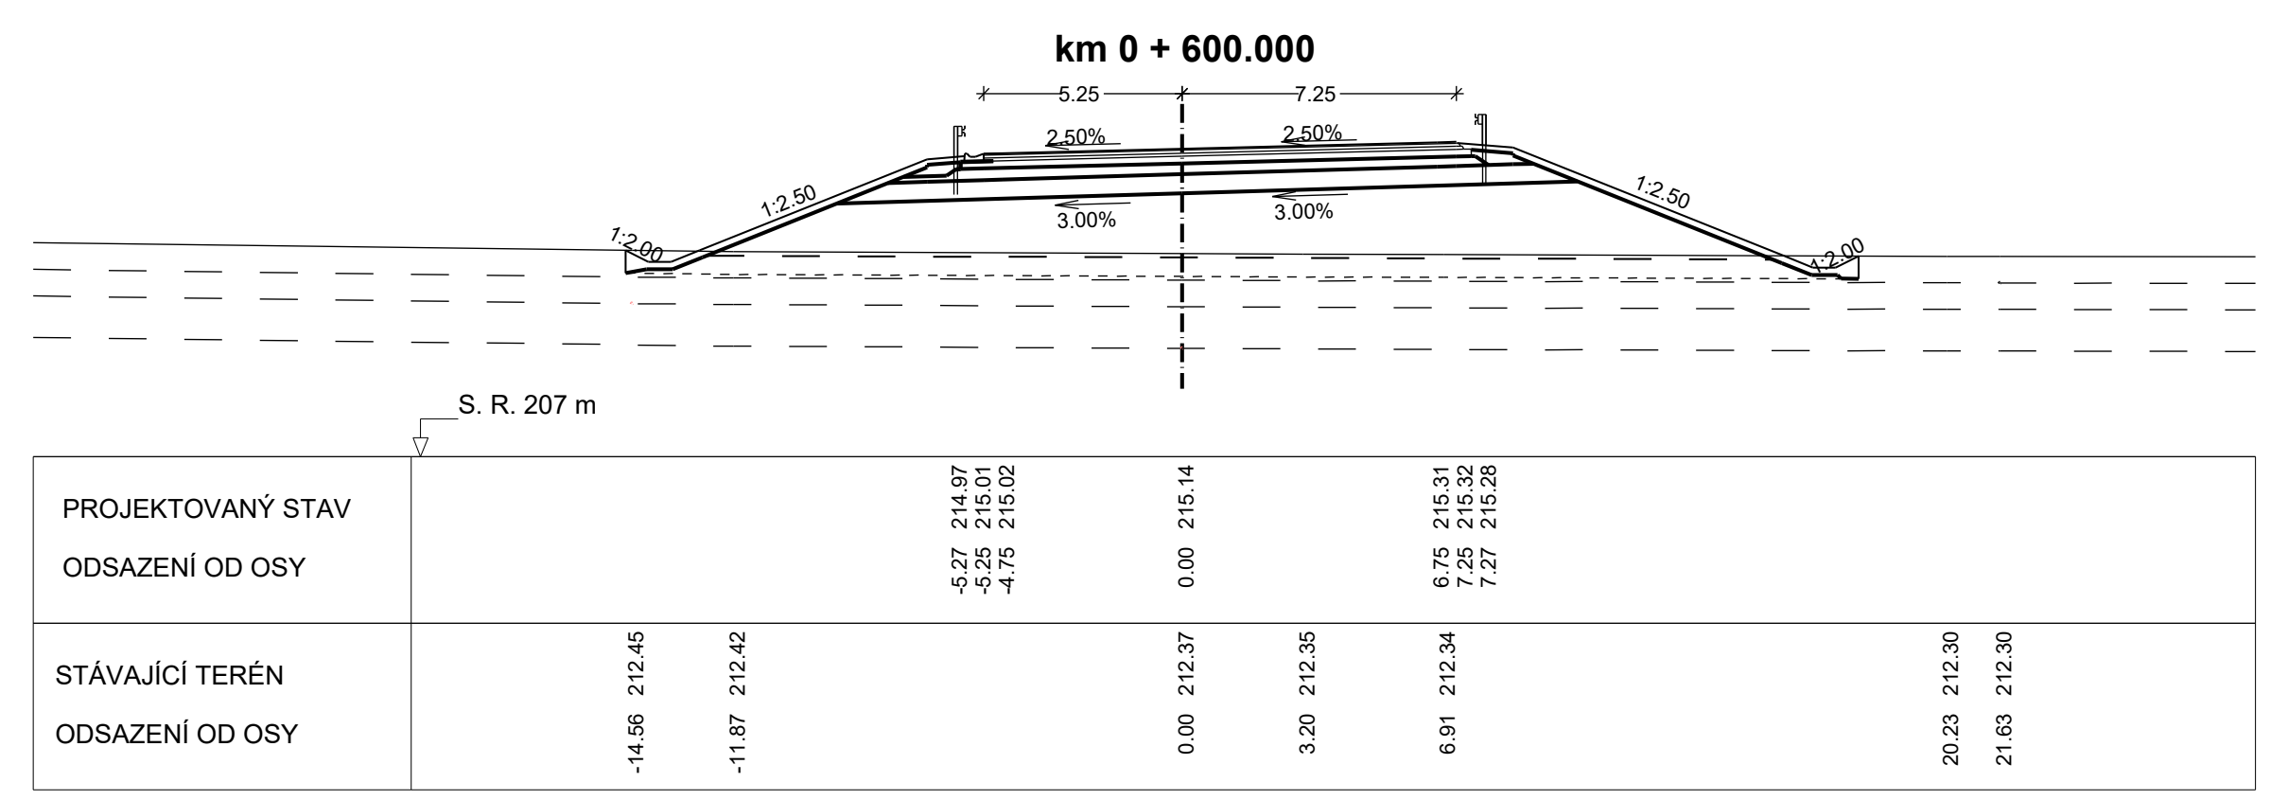

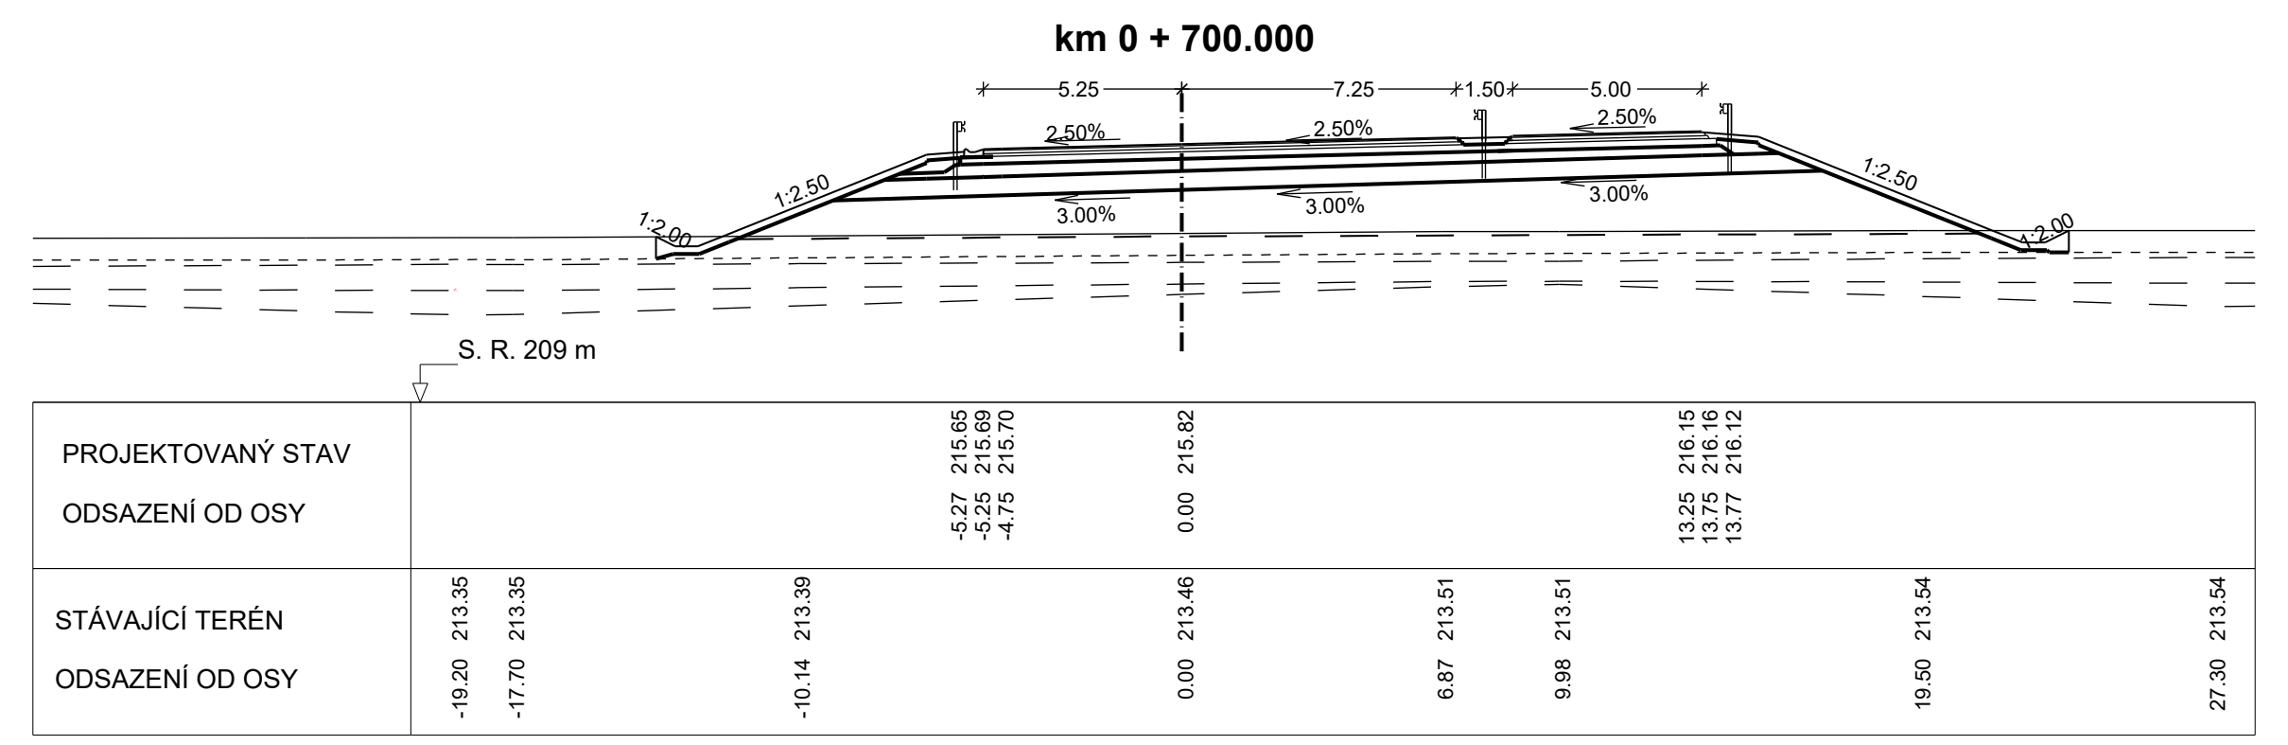

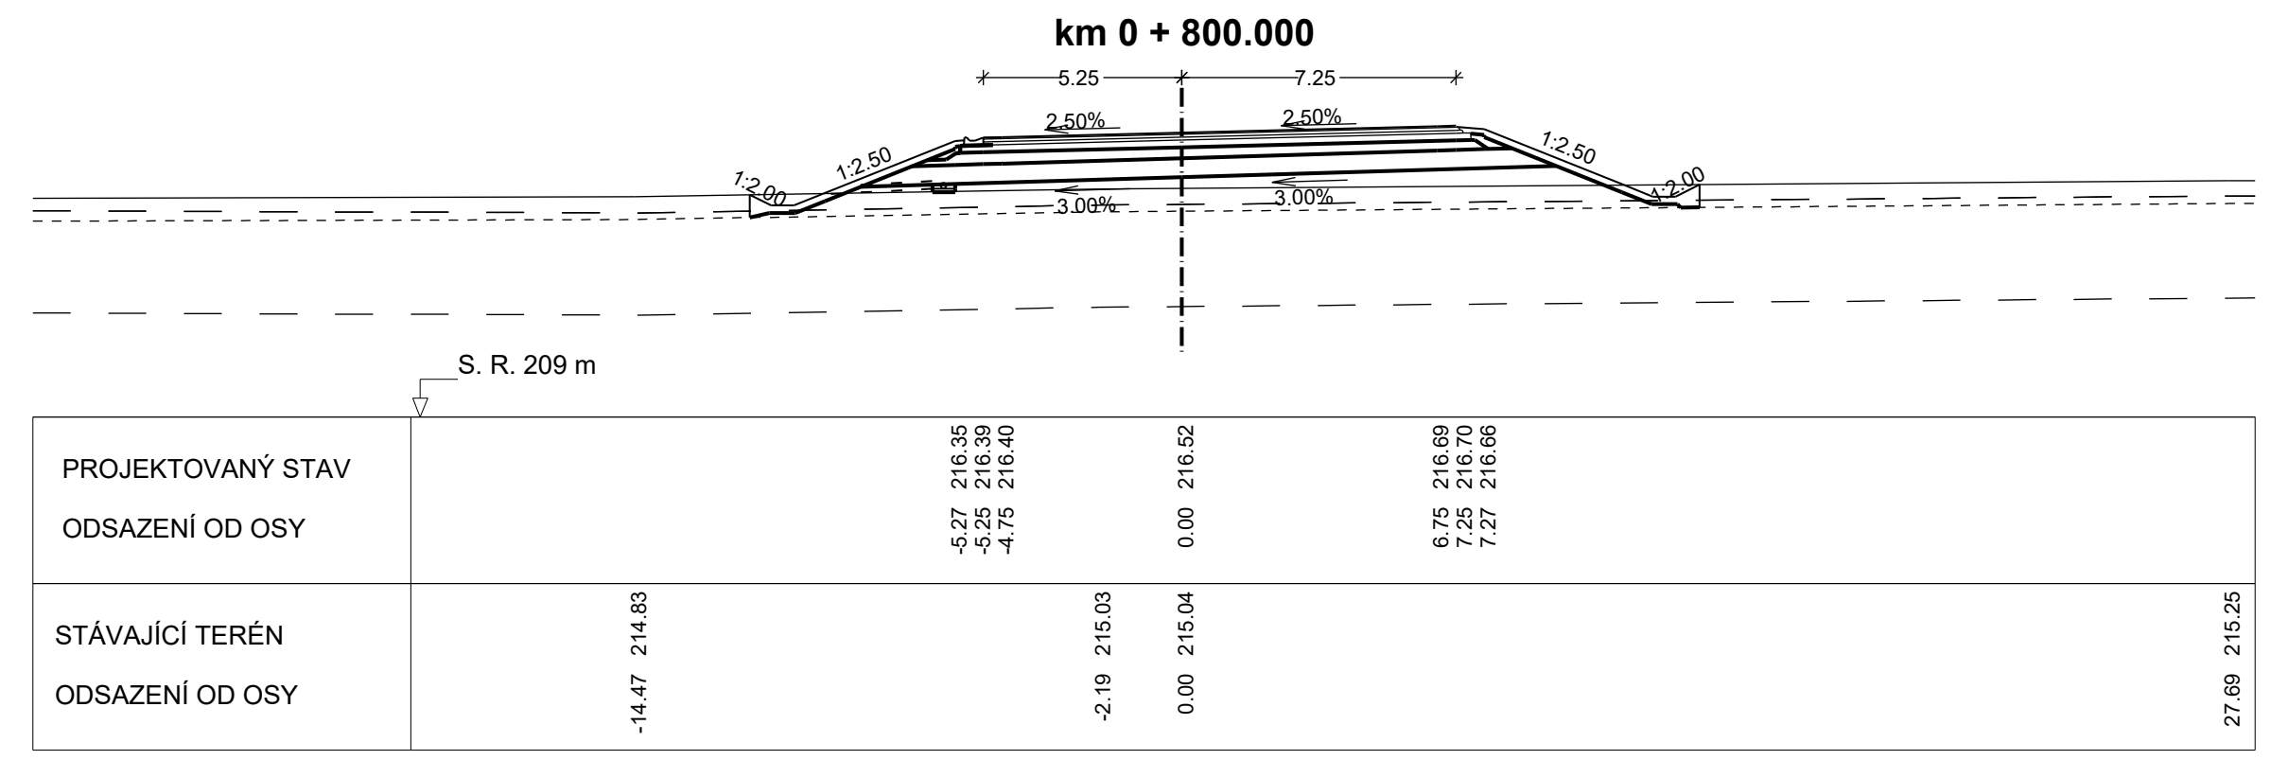

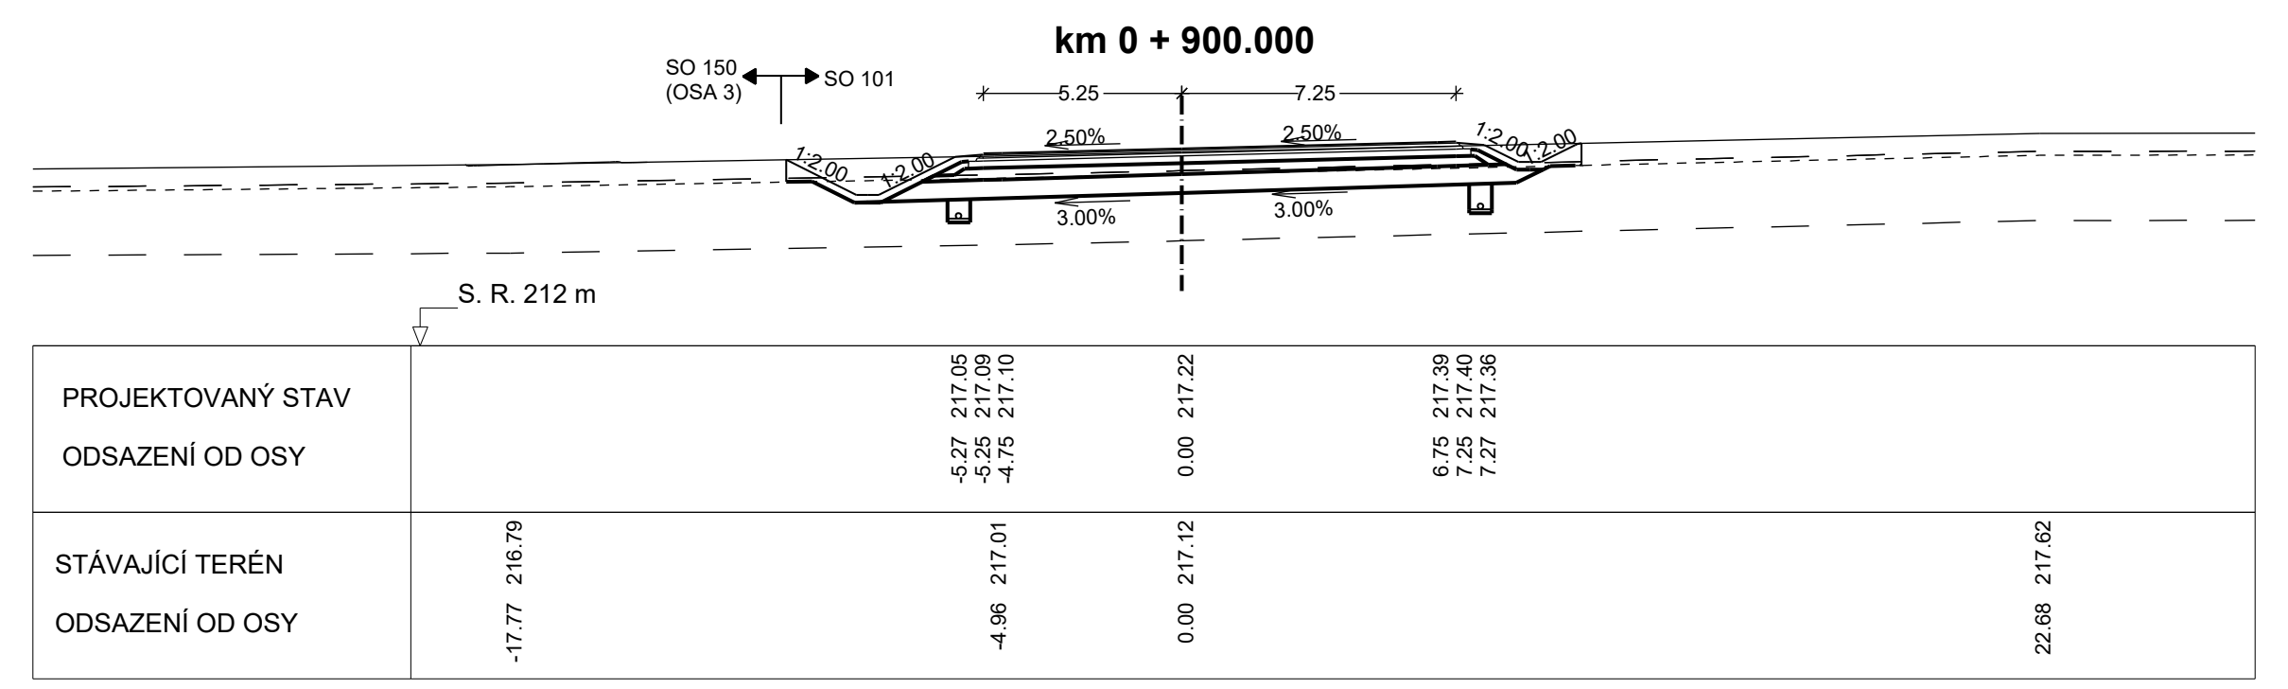

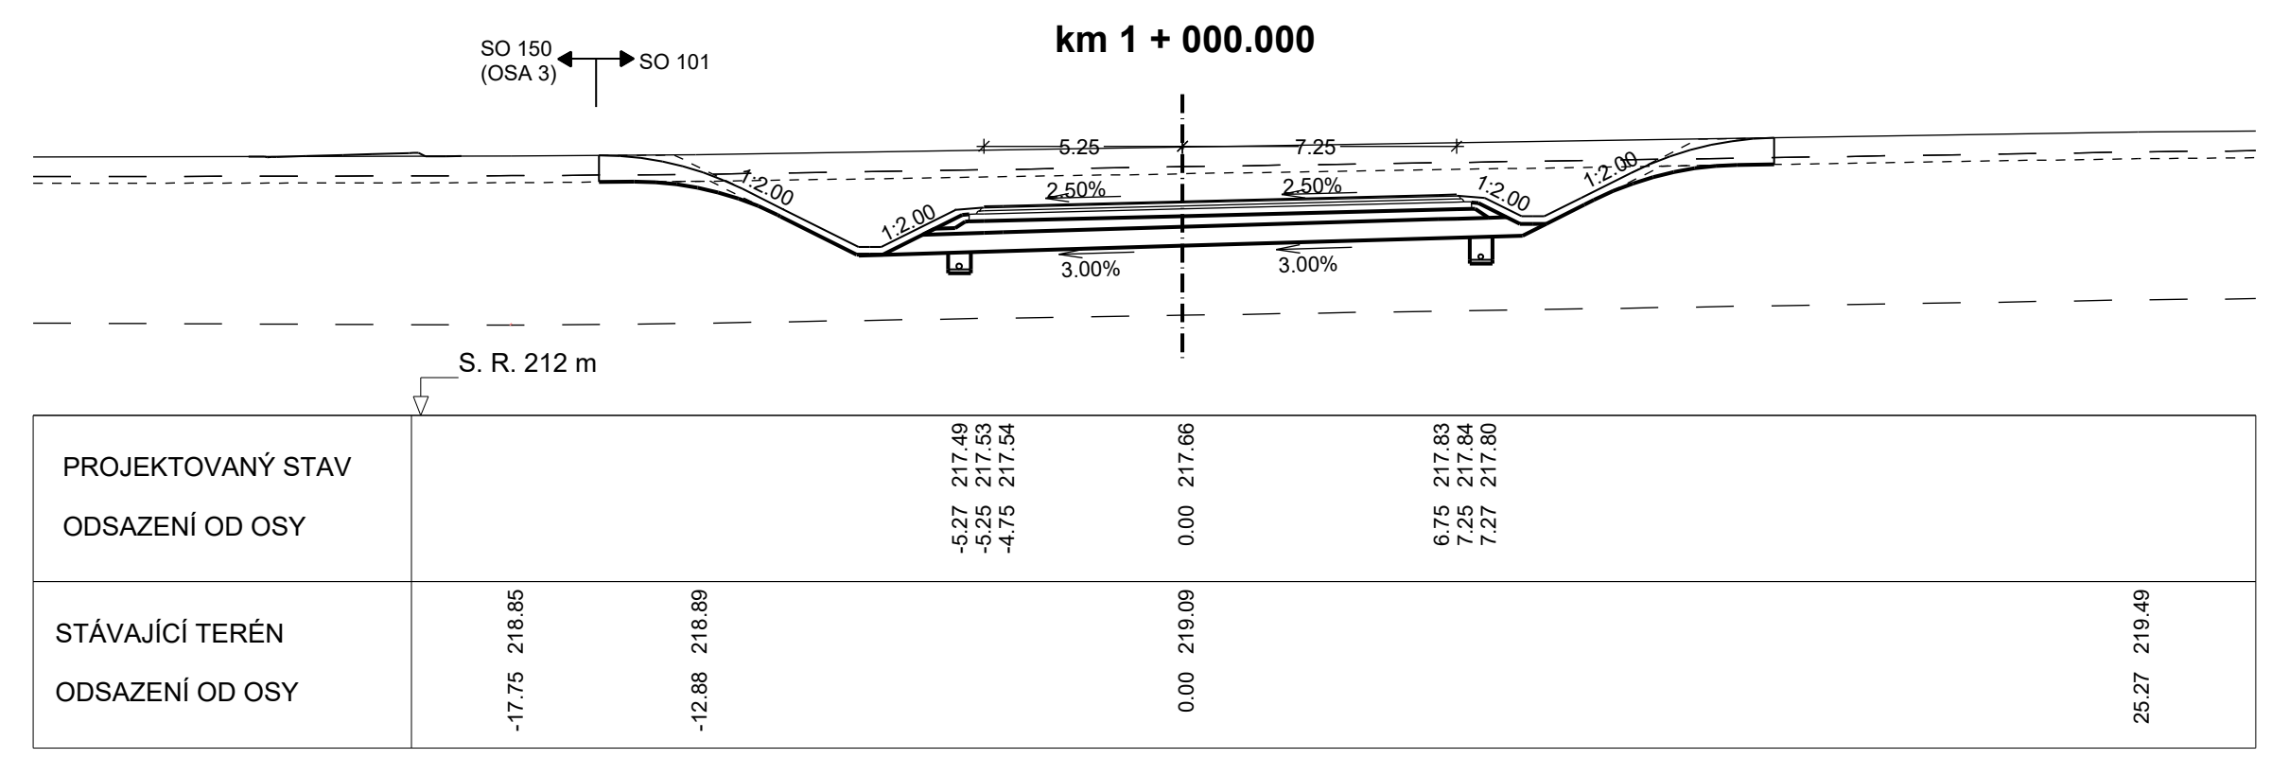

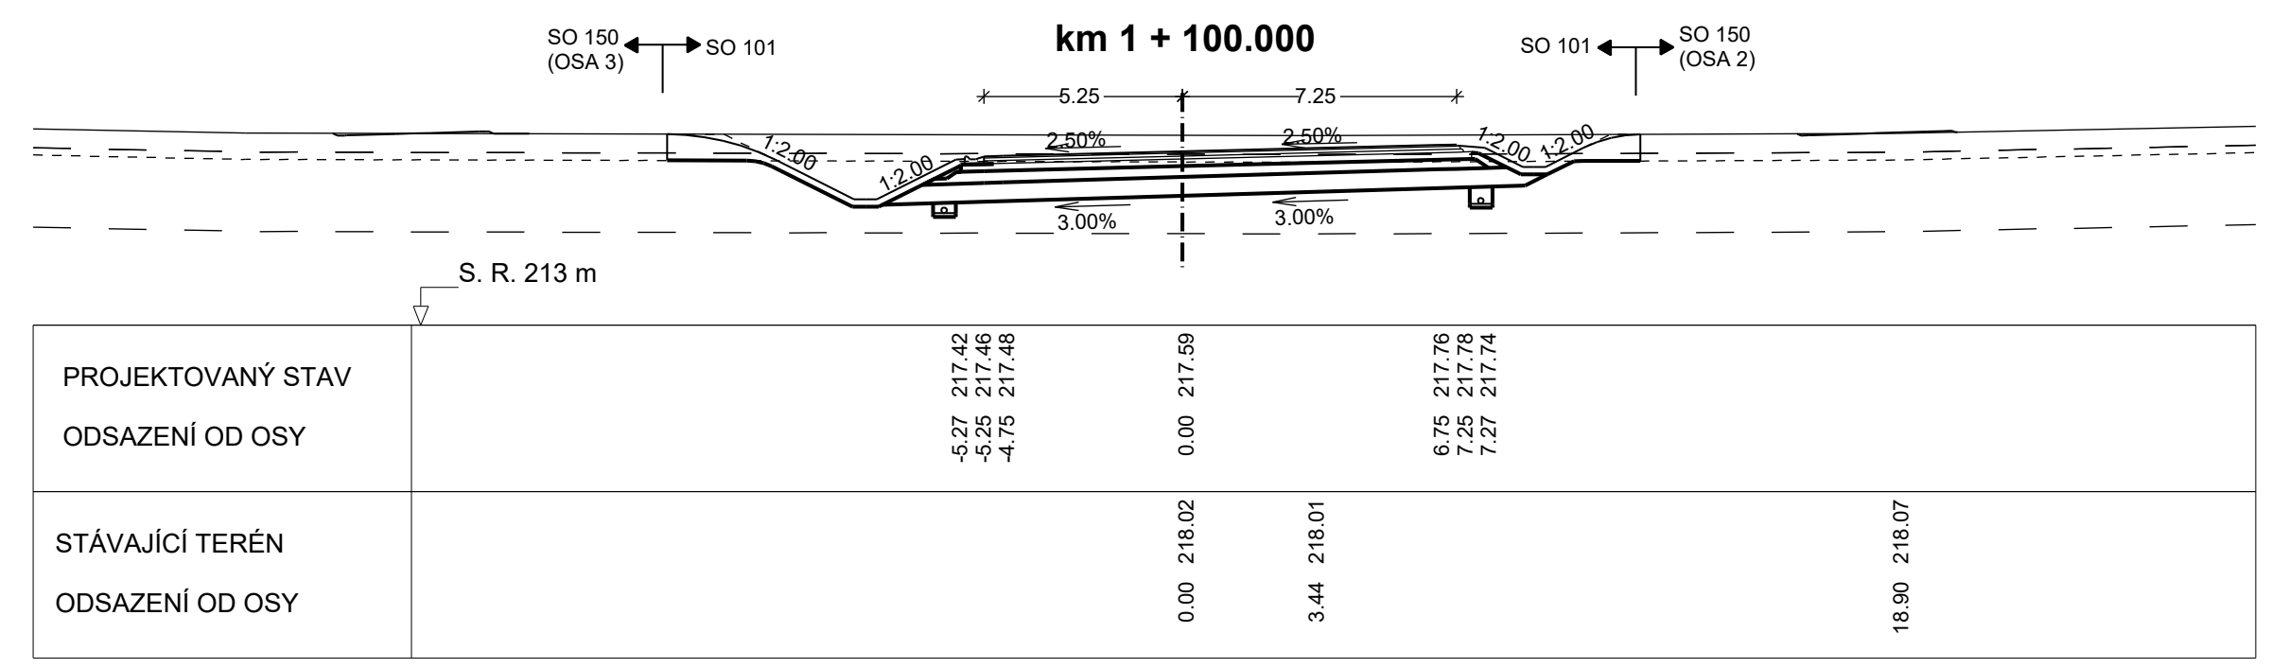

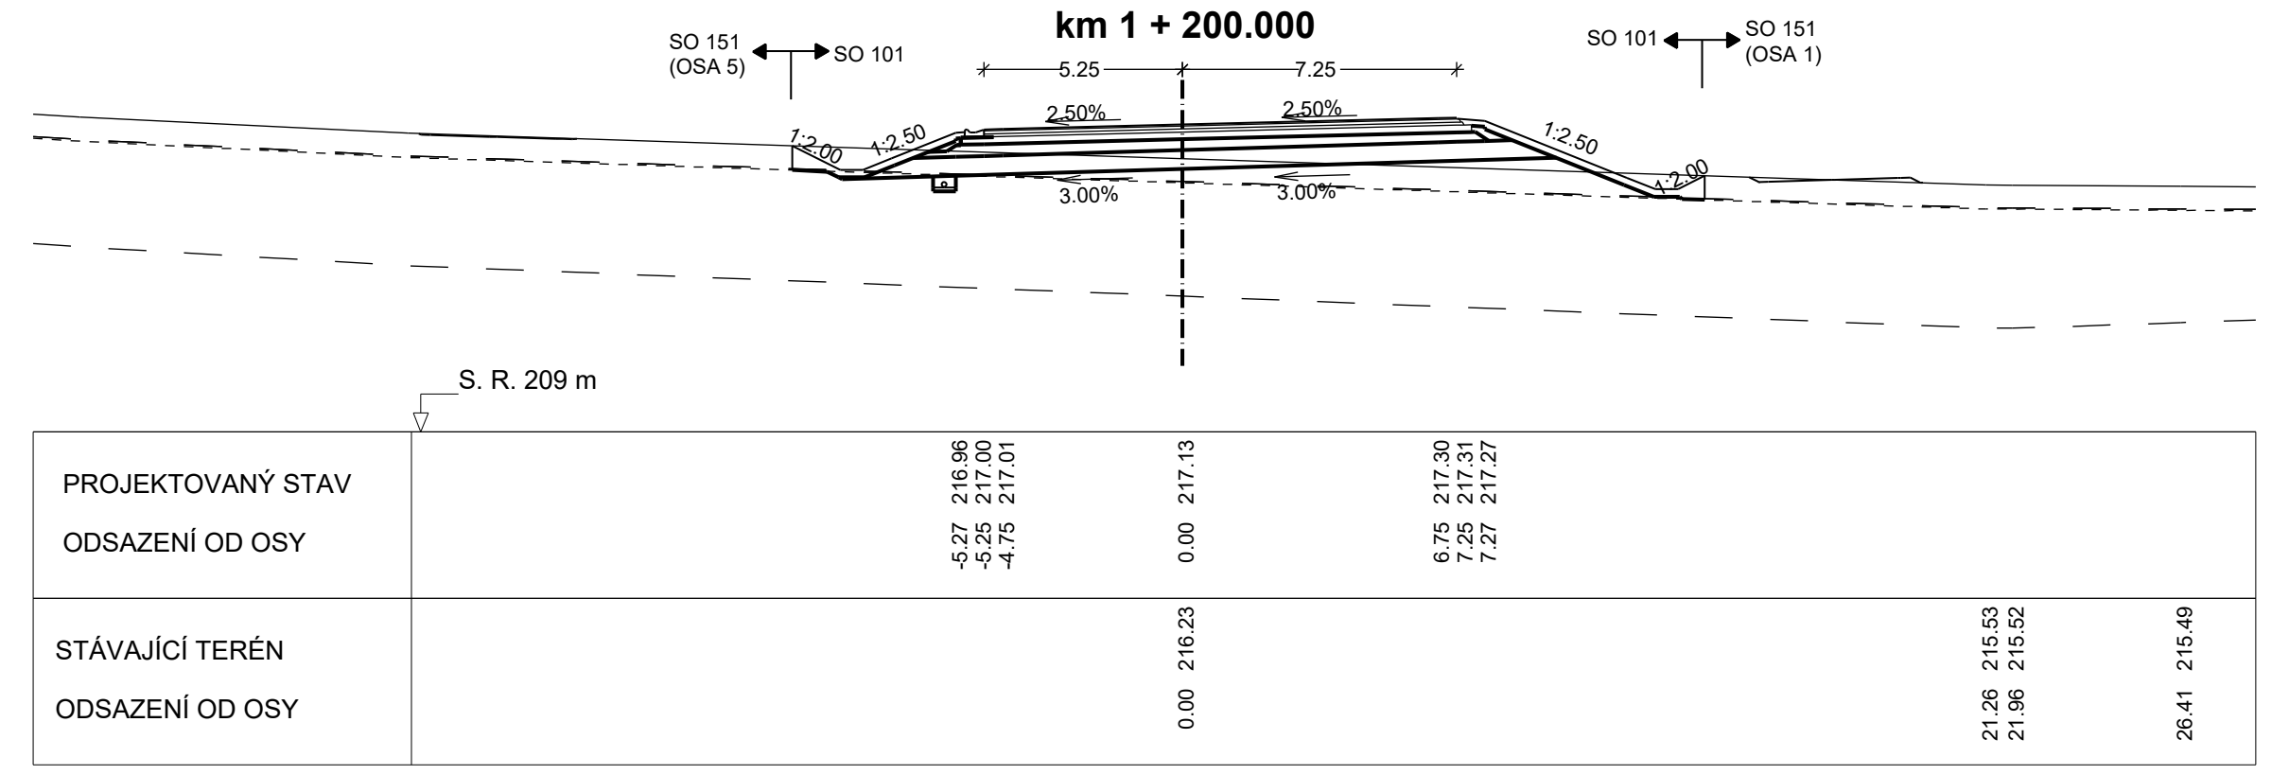

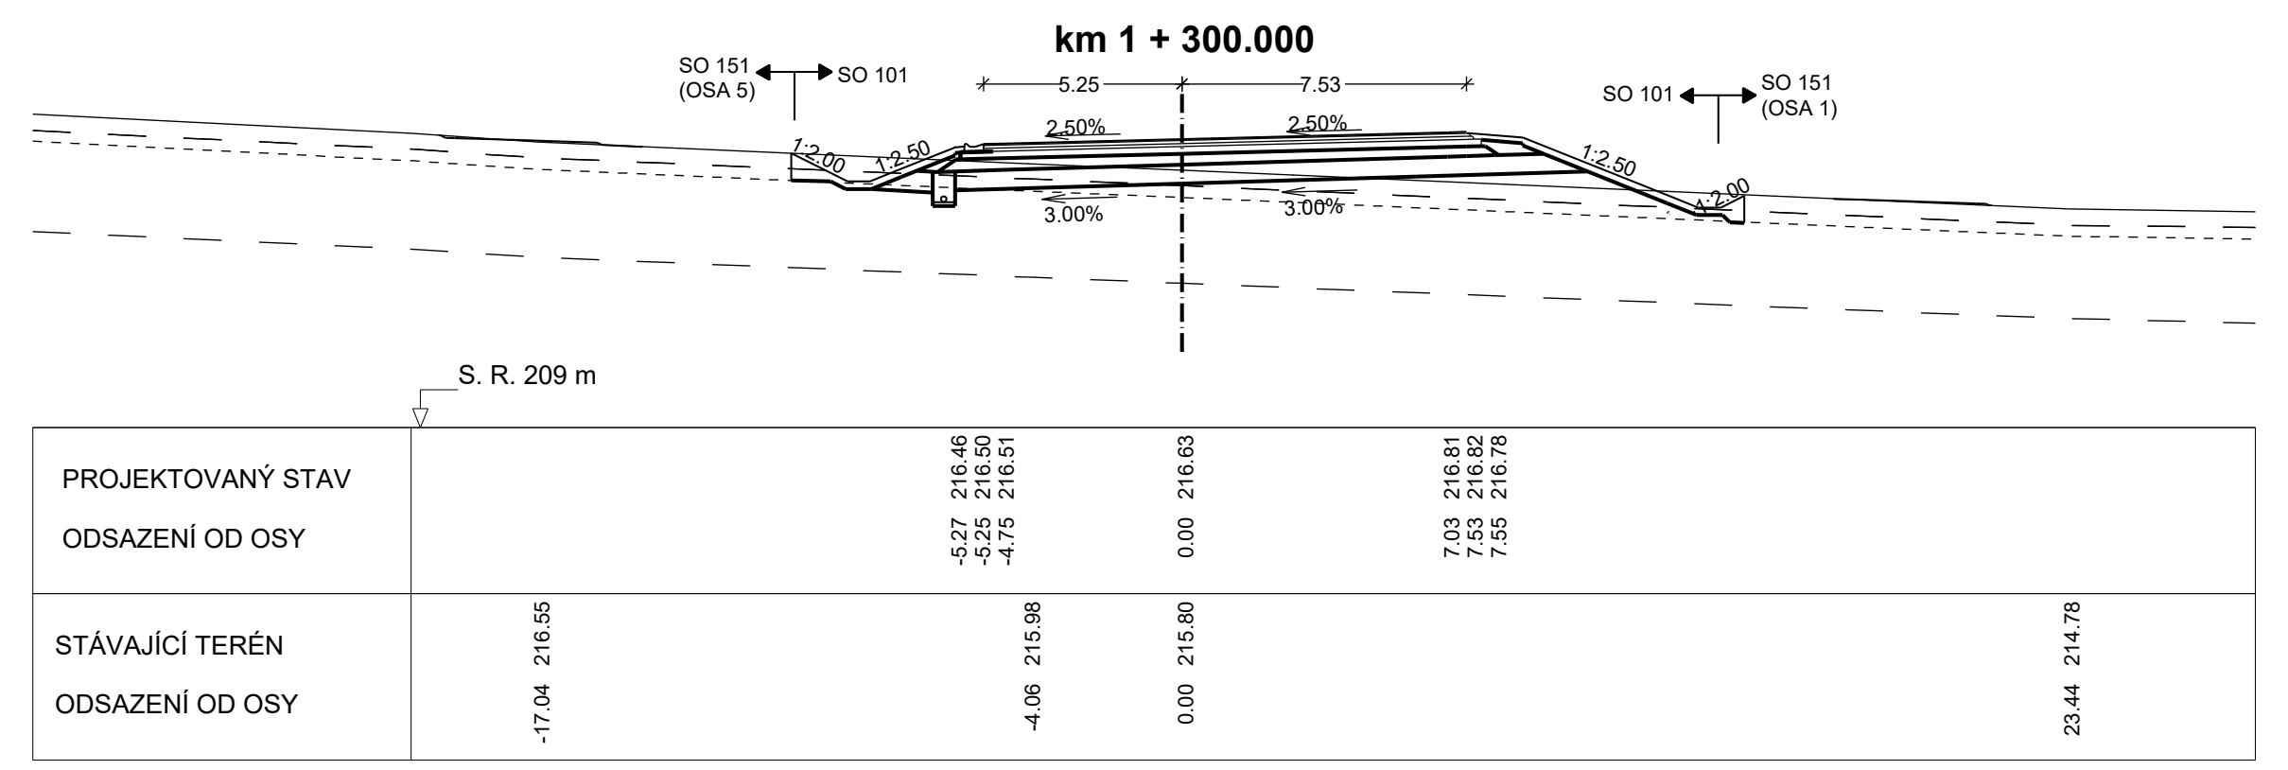

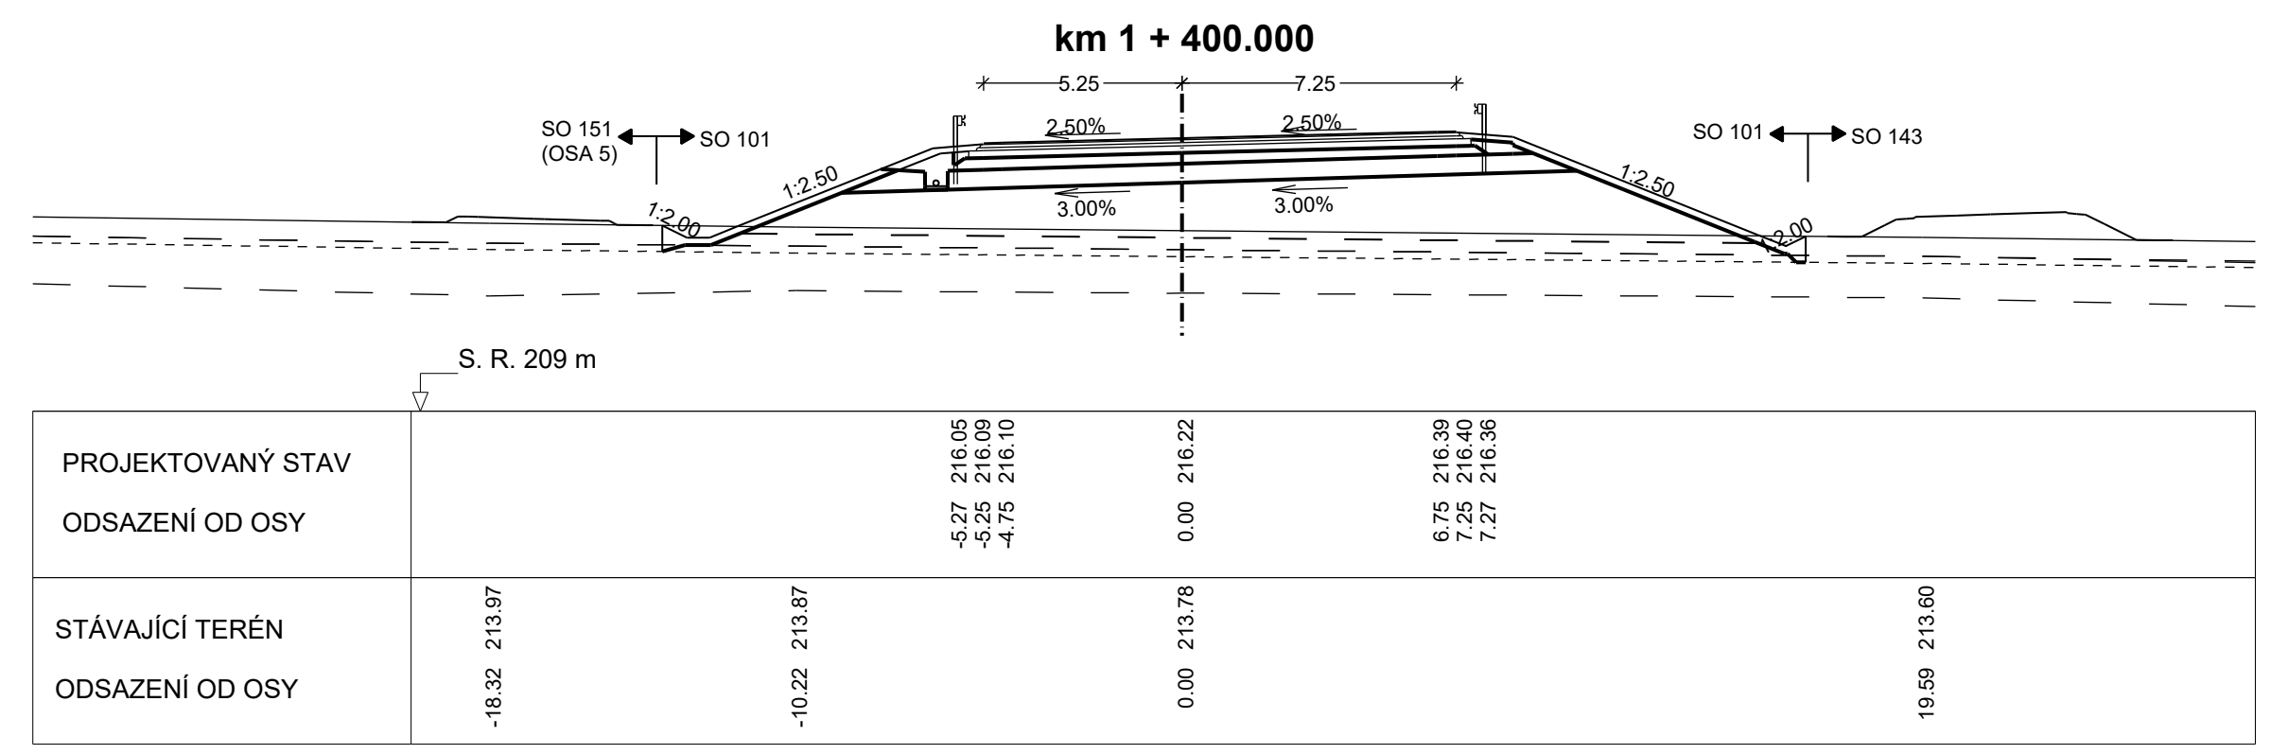

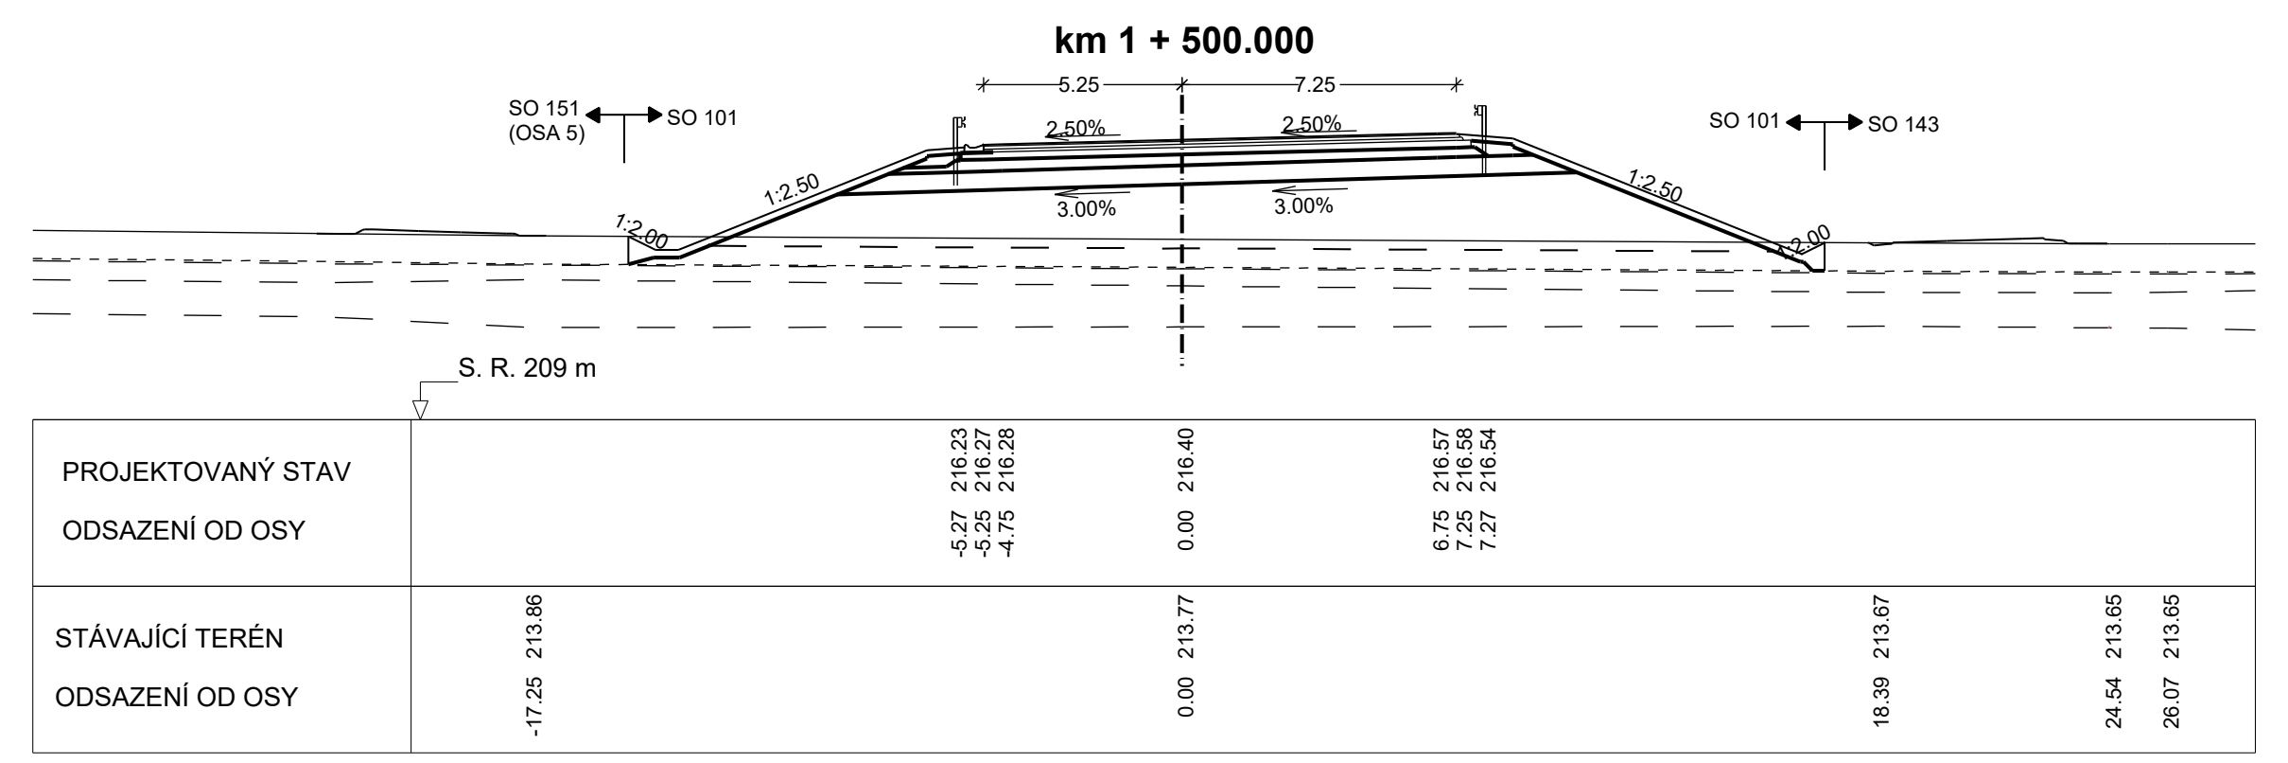

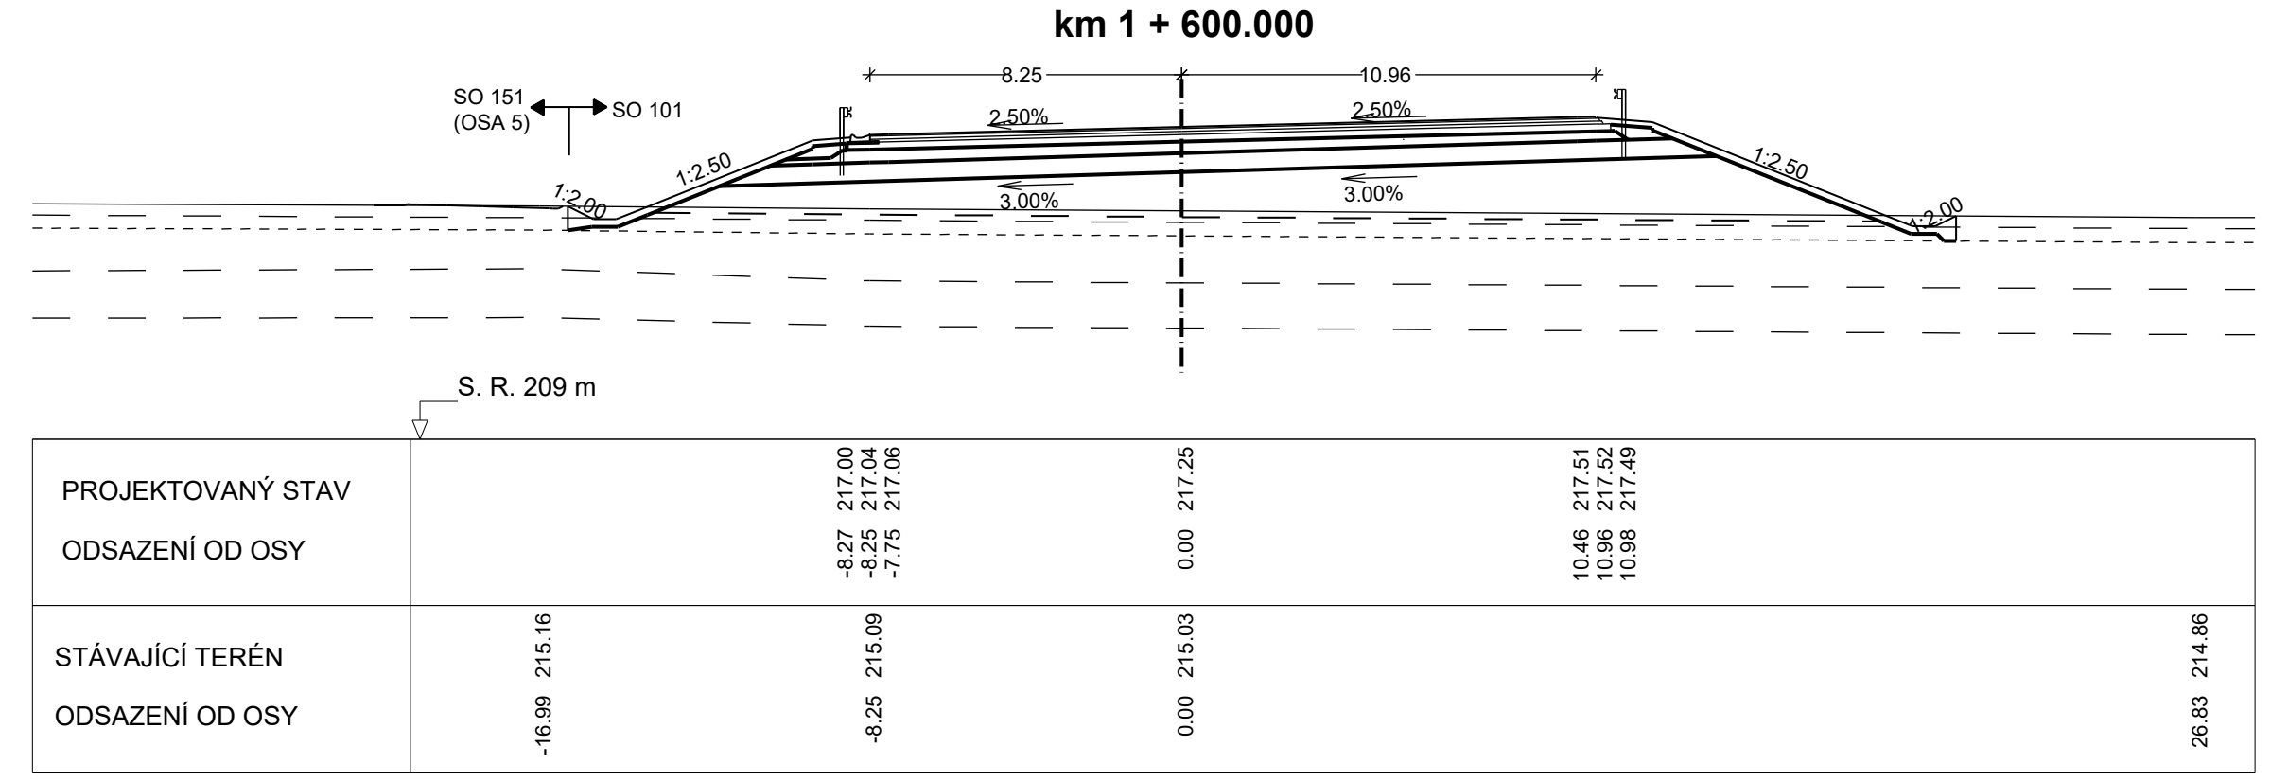

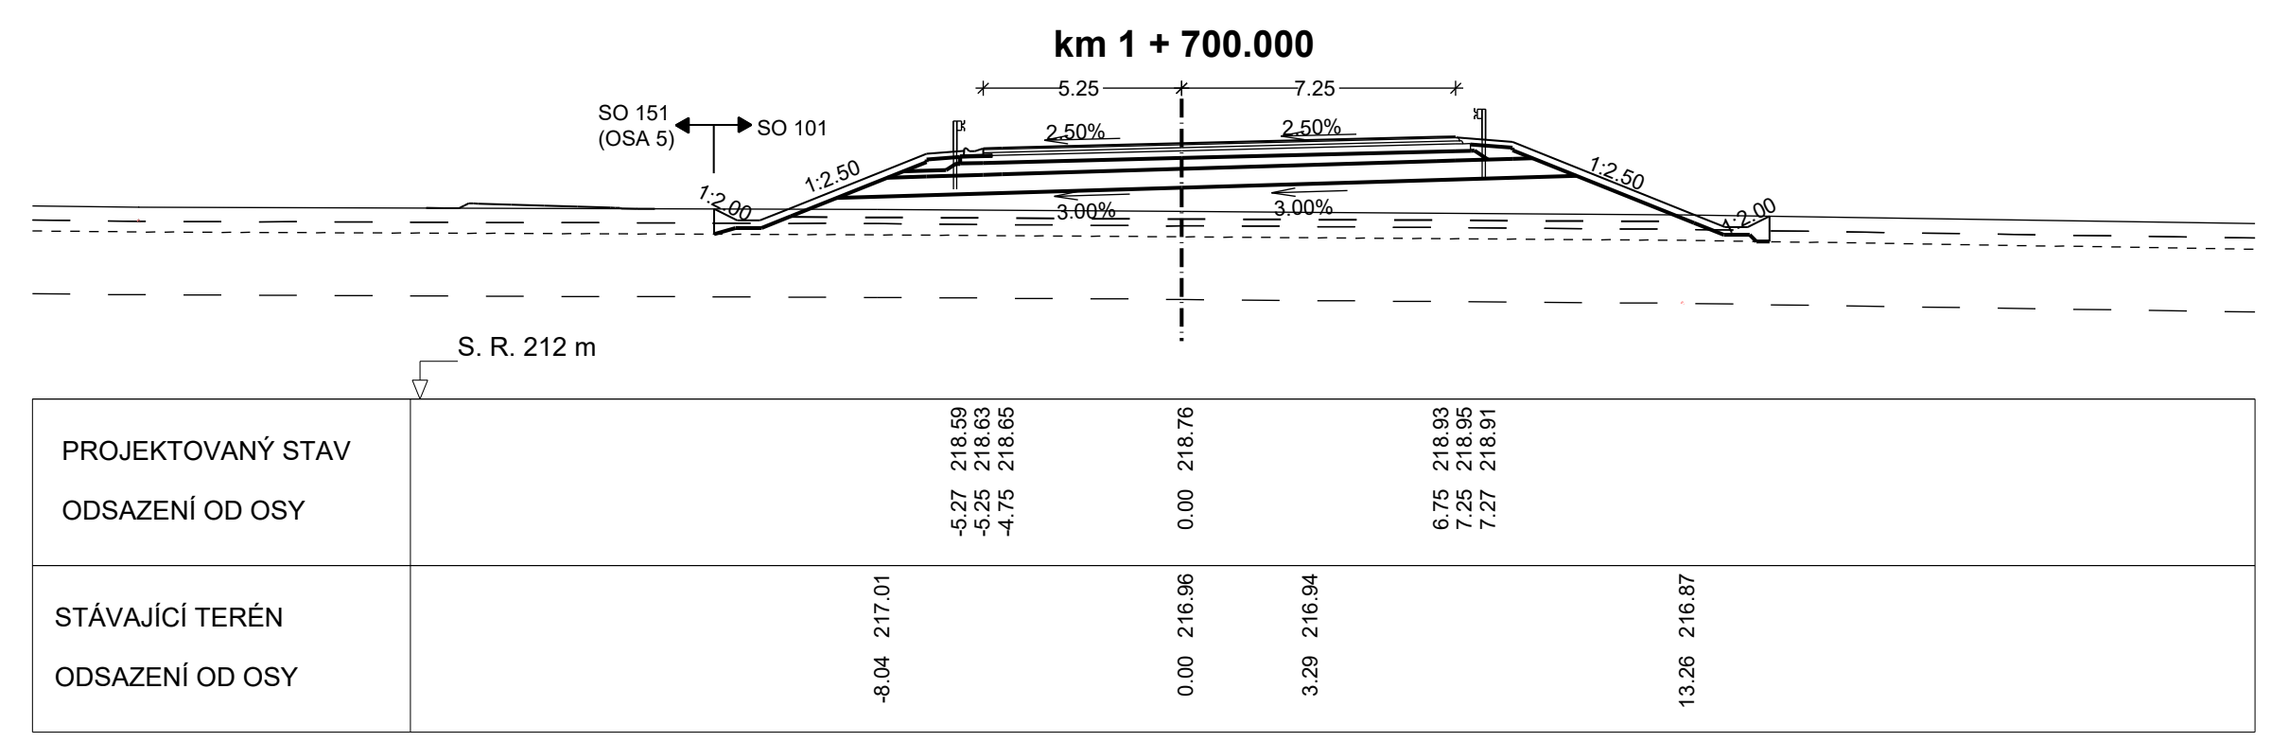

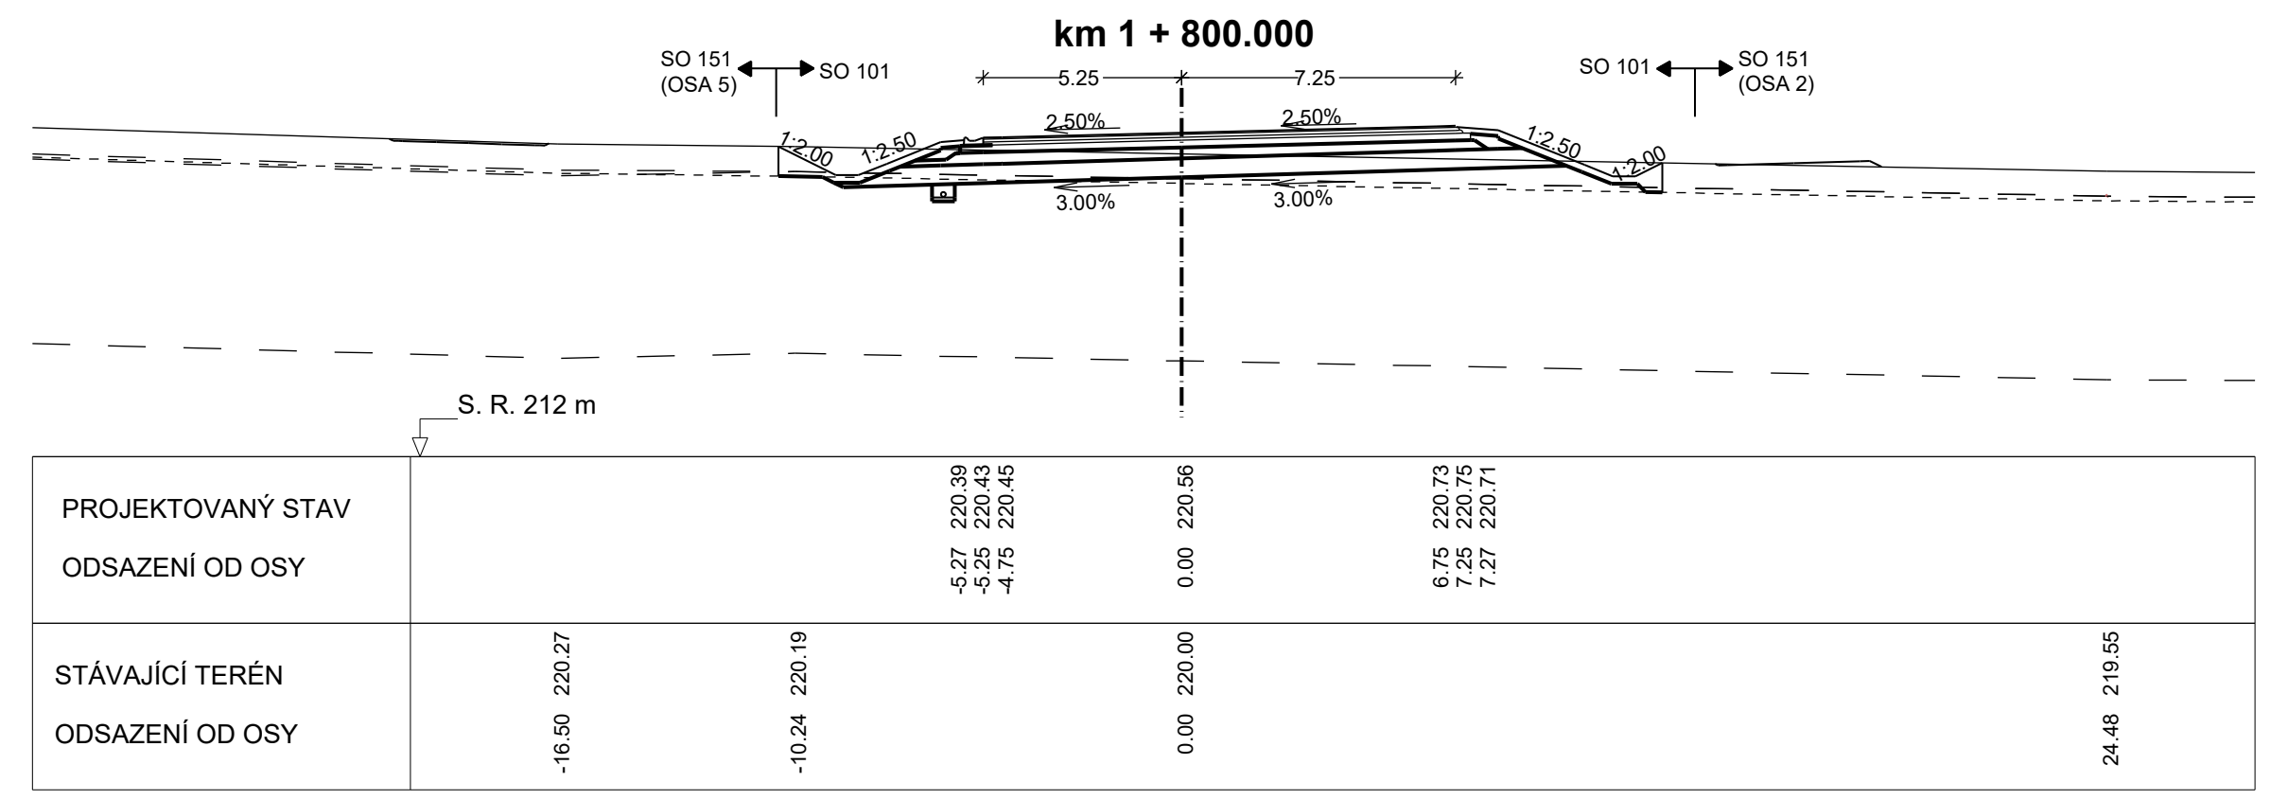

Výškový systém: Bpv

SO 101 Silnice I/16 Mladá Boleslav - Martinovice

Objednatel:

Ředitelství silnic a dálnic s. p.
Čerčanská 2023/12, Krč, 140 00 Praha 4

Zhotovitel:

Valbek, spol. s r.o.
Vaňurova 505/17
460 07 Liberec 3

Vypracoval	A. BARTONÍČKOVÁ	**Zak. číslo**	**21-LI13-001**
Zodp. projektant	ING. T. KLIMENT	**Datum**	**02/2025**
Tech. kontrola	ING. M. HANŽL	**Stupeň**	**PDPS**
Akce	**I/16 MLADÁ BOLESLAV - MARTINOVICE**	**Počet formátů**	**20 x A4**
		Měřítko	**1 : 200**
Příloha	PŘÍČNÉ ŘEZY km 0,100 - 1,800	**Č. přílohy** **5.1**	**Paré**

Zhotovitel:
Valbek, spol. s r.o.
Vaňurova 505/17
460 07 Liberec 3