

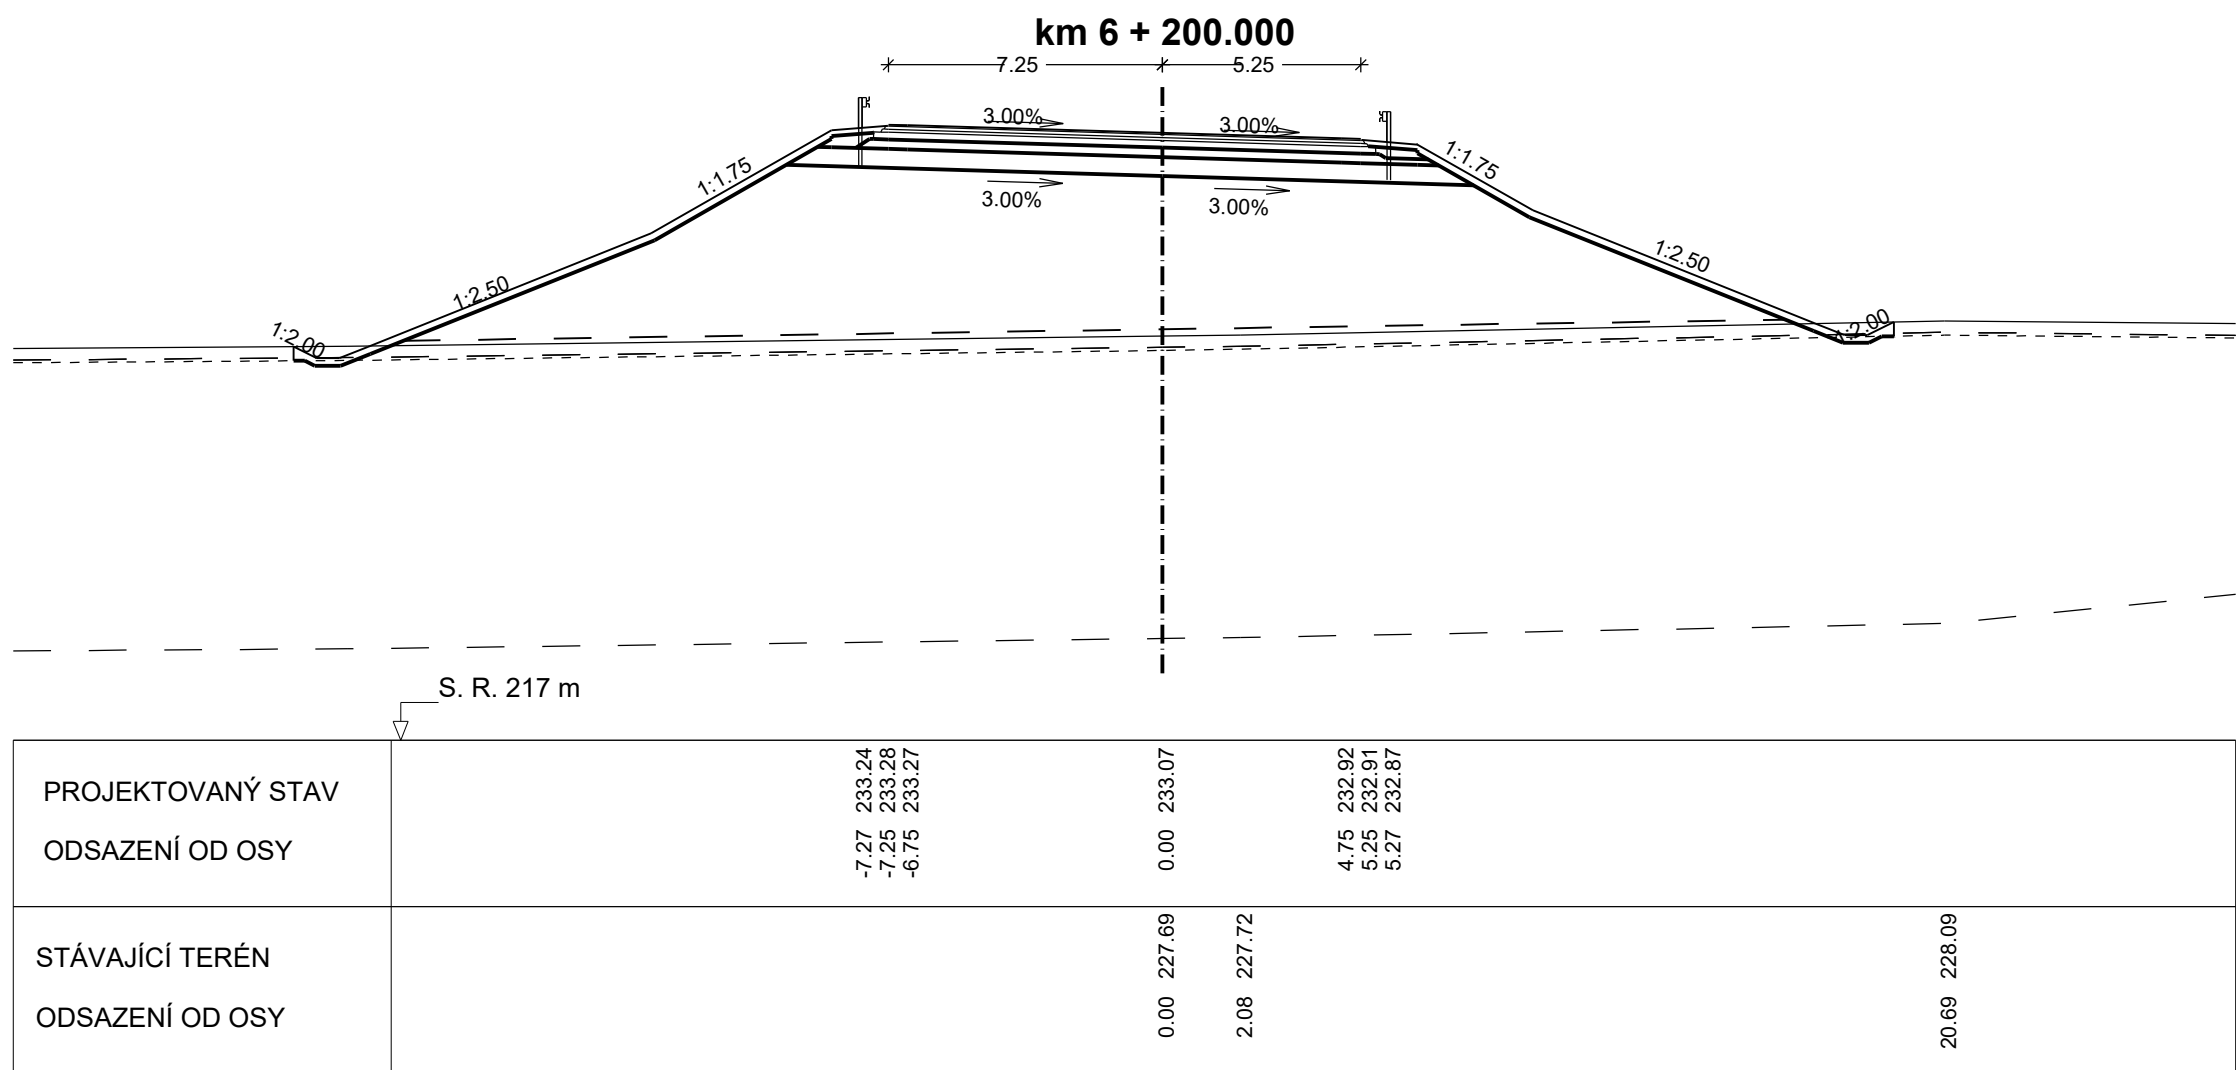
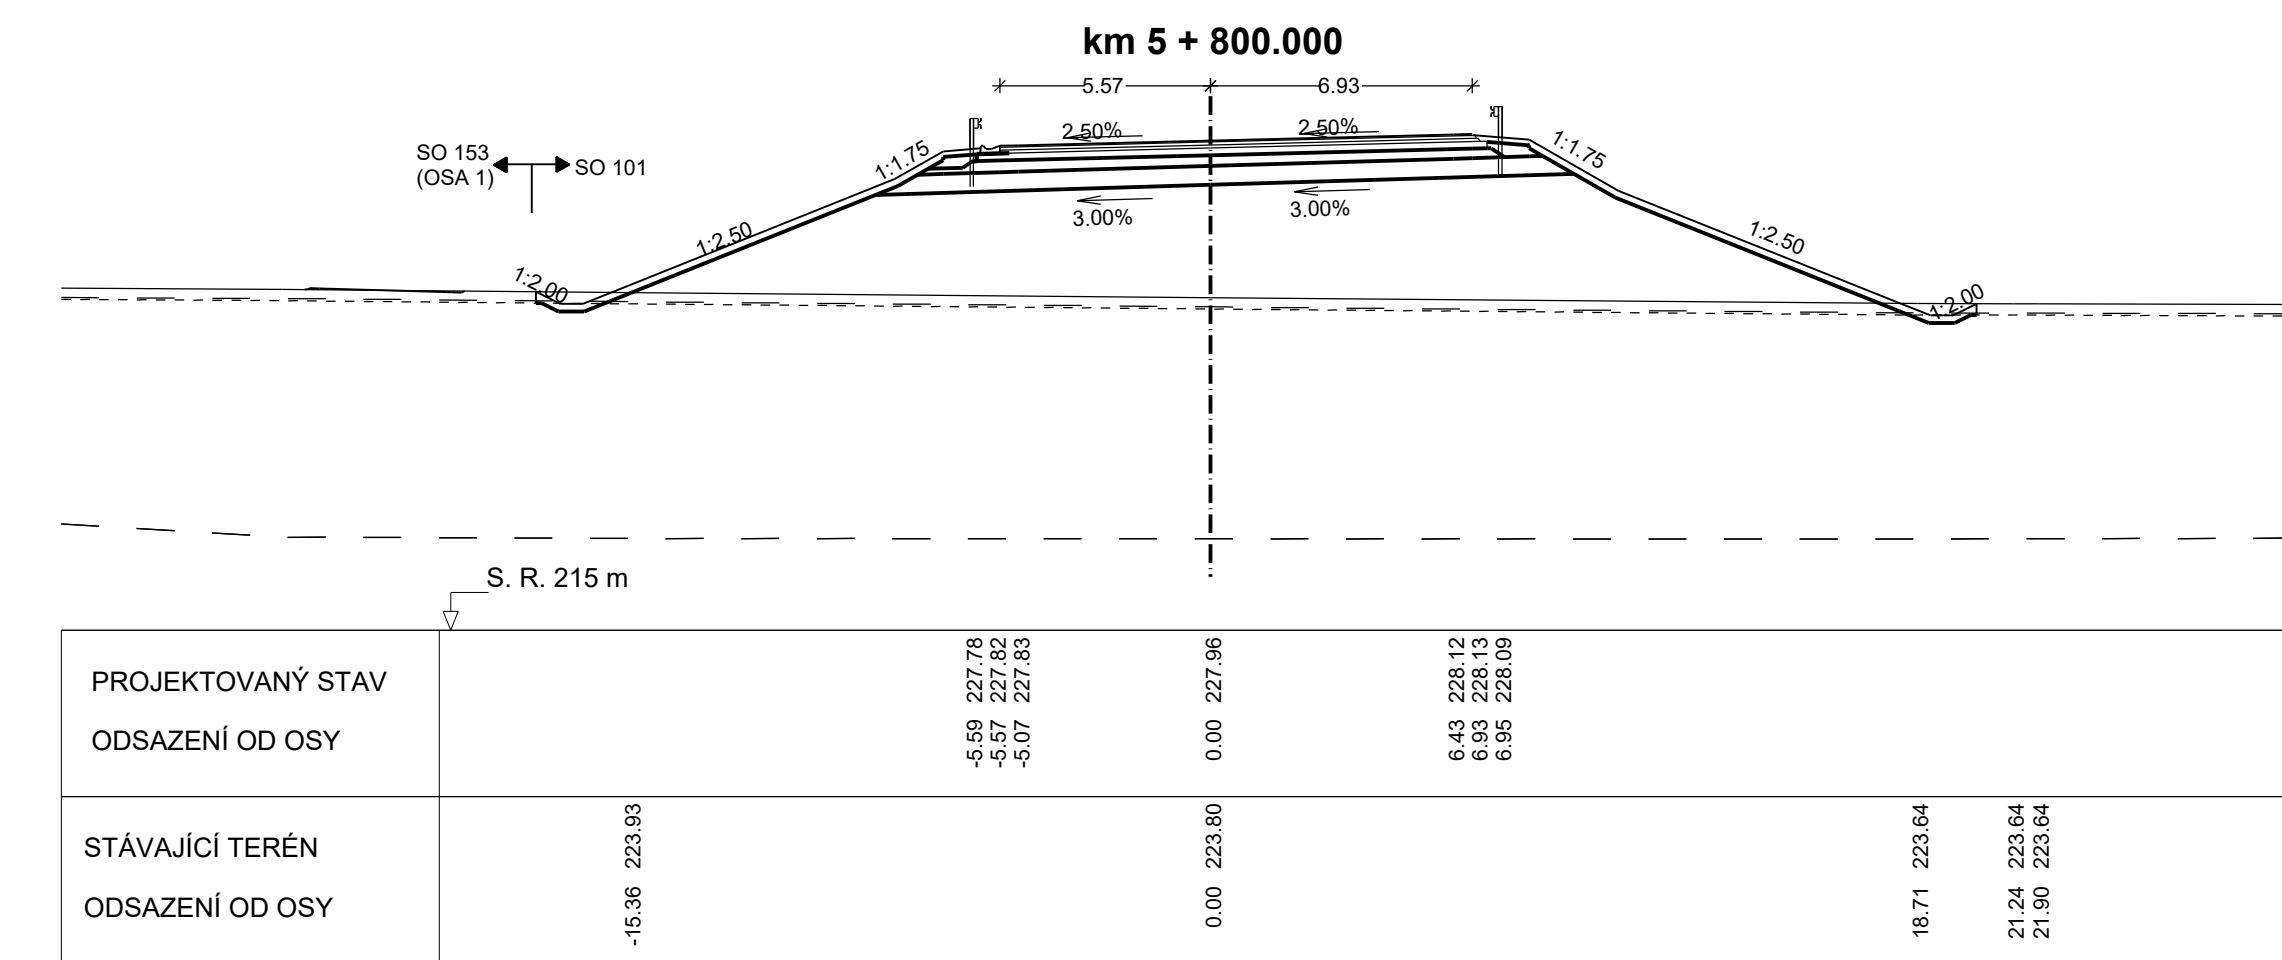
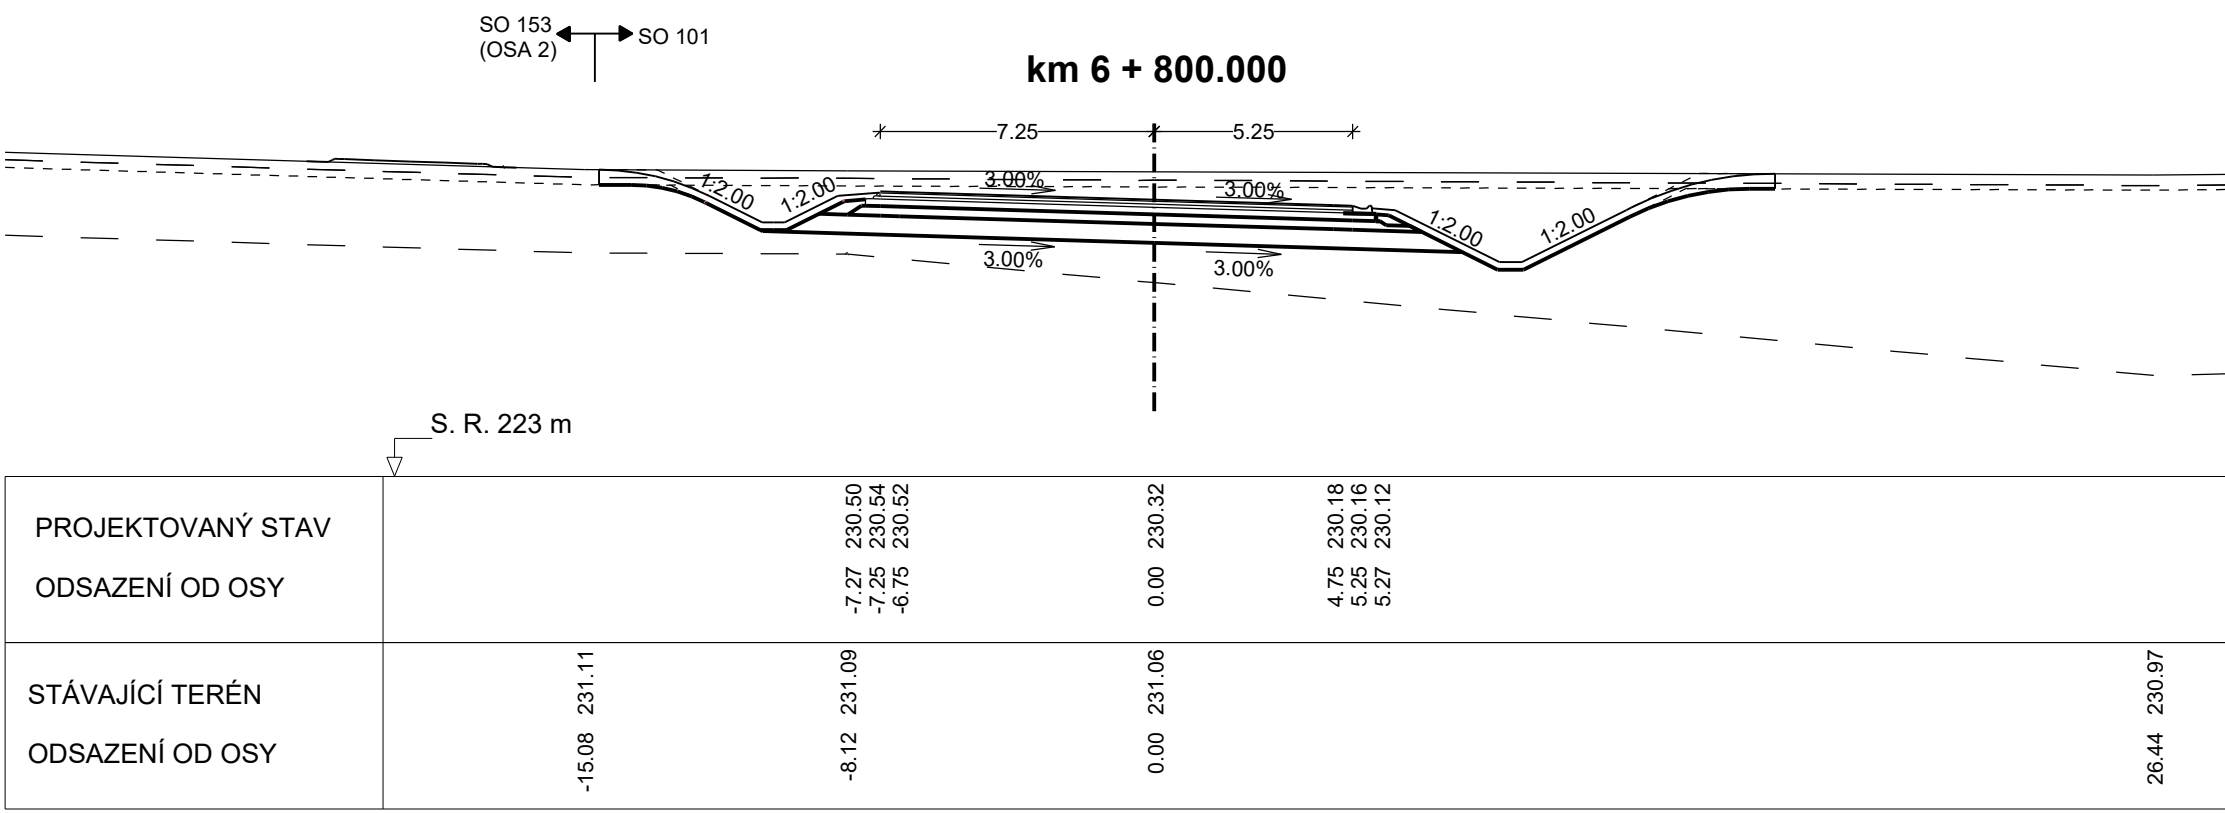
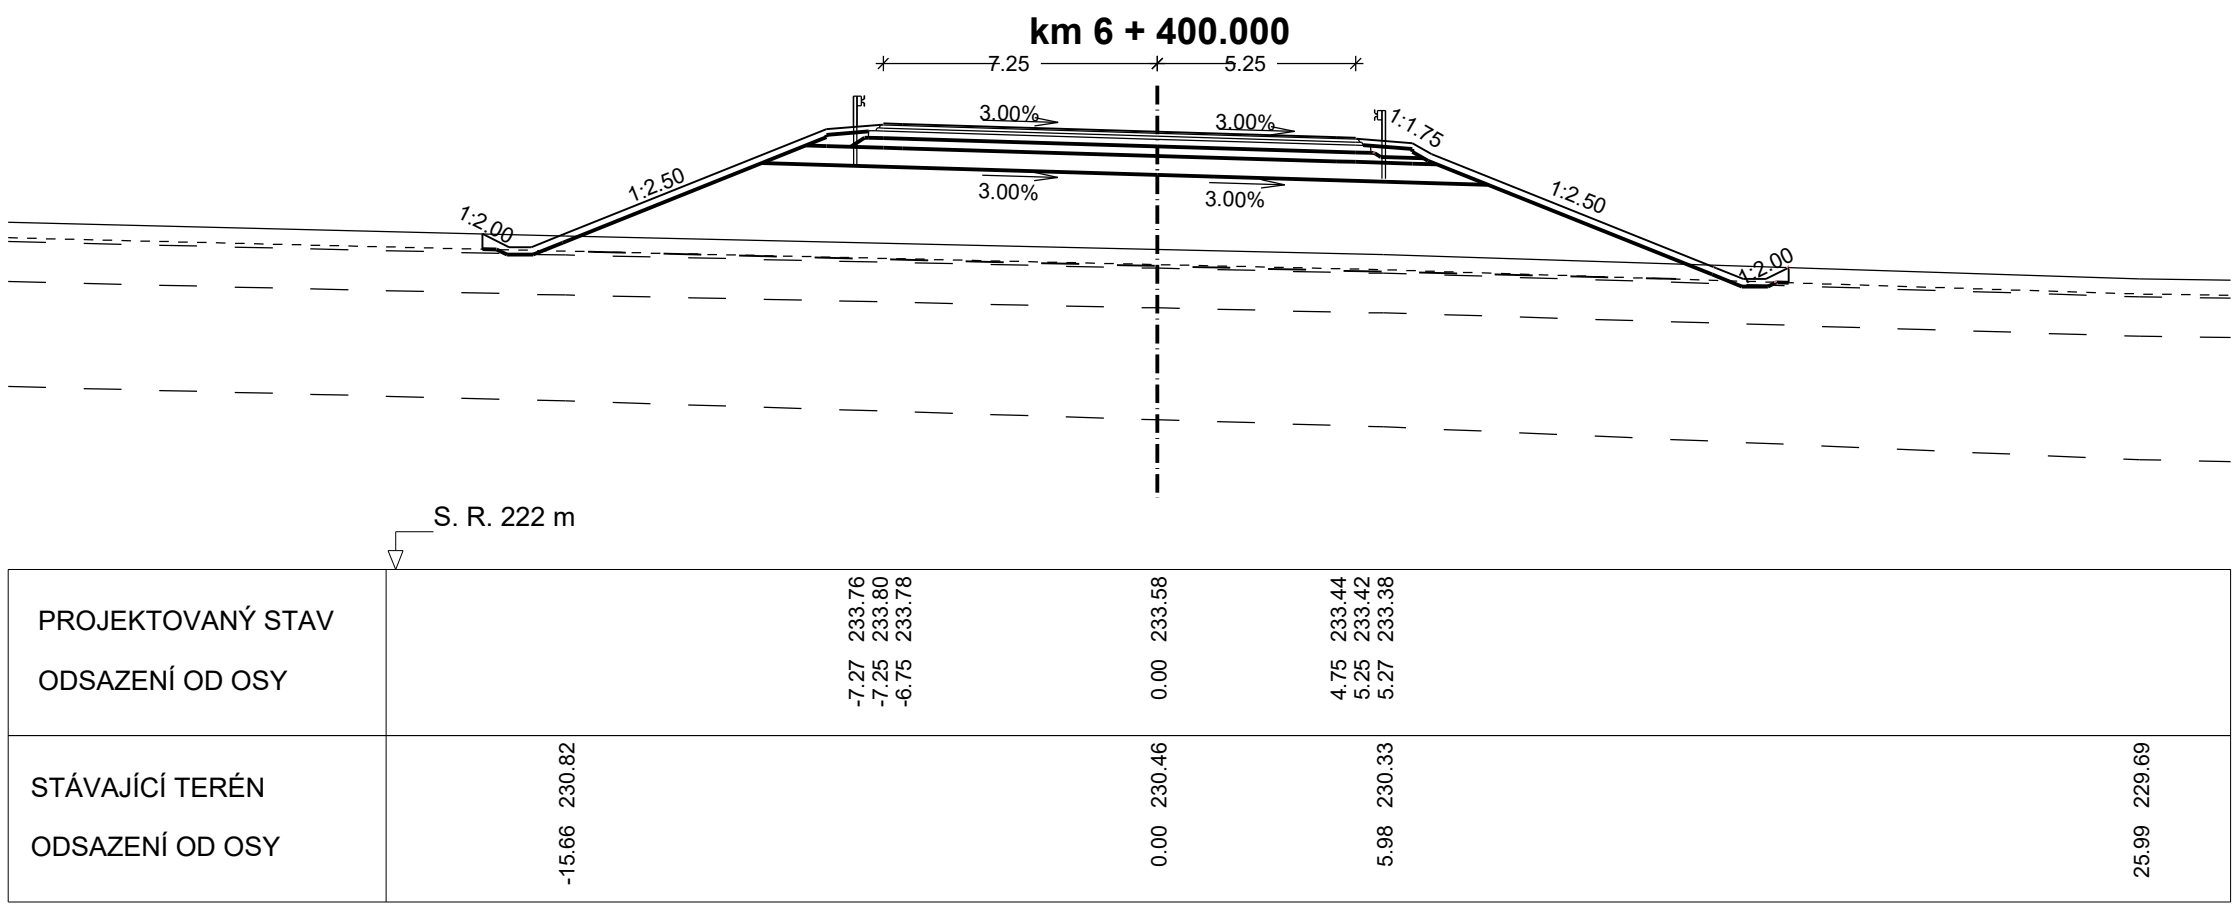
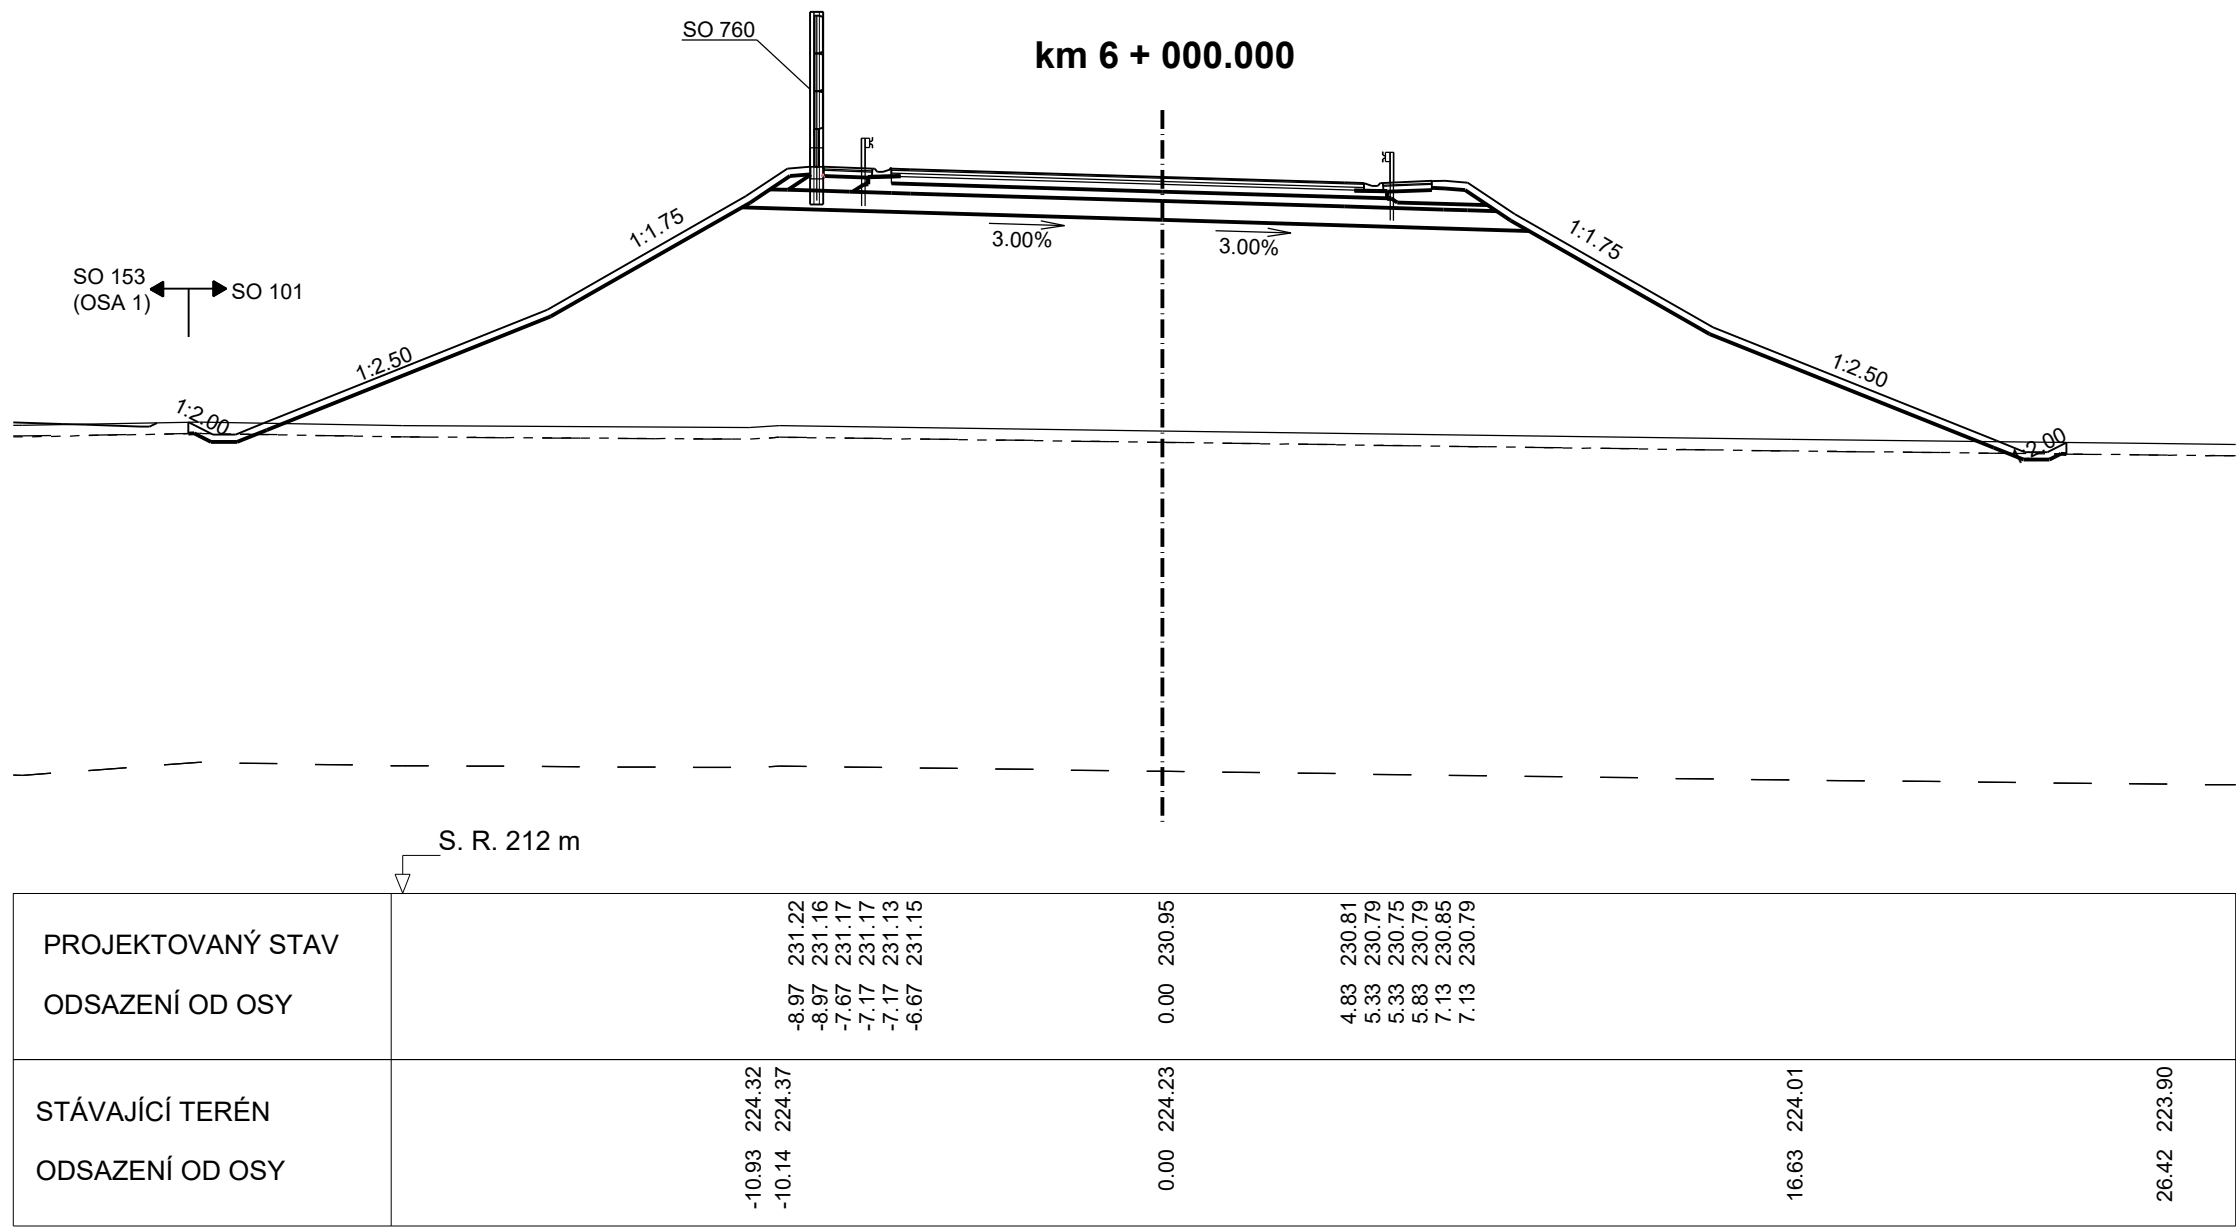
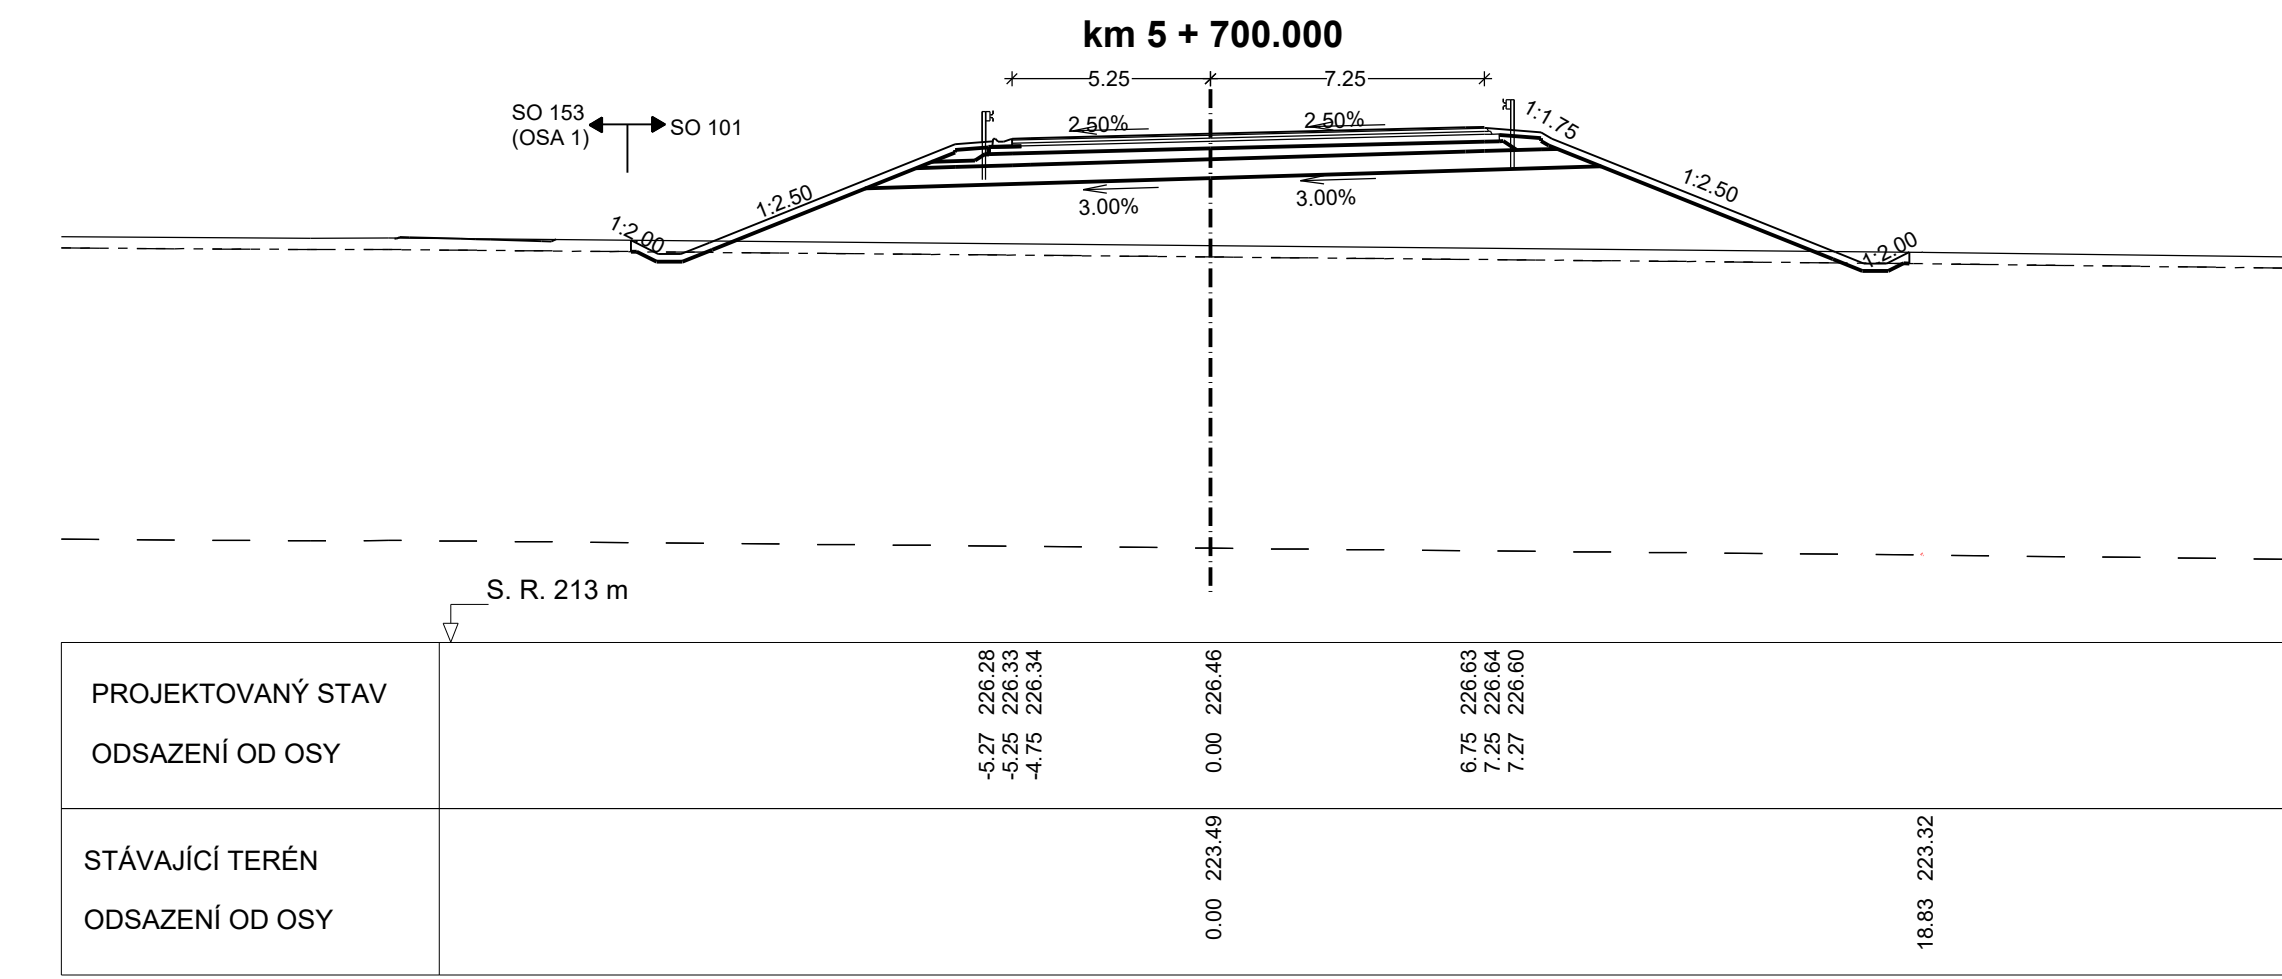
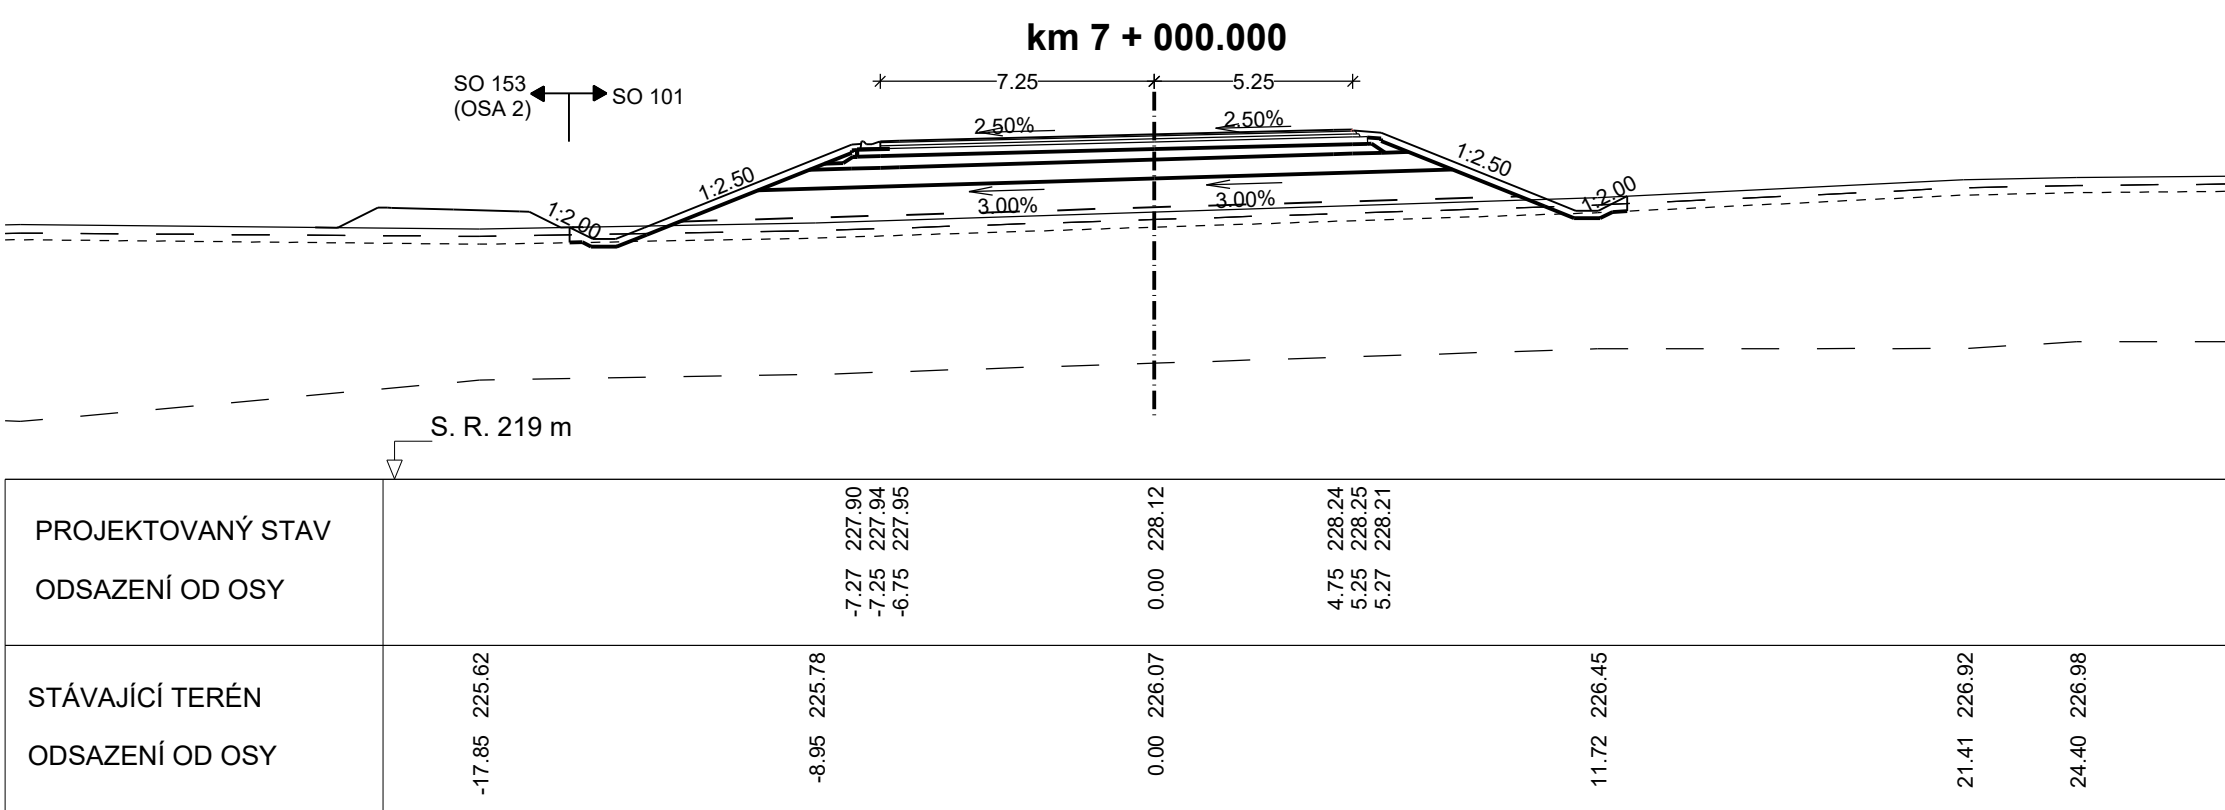
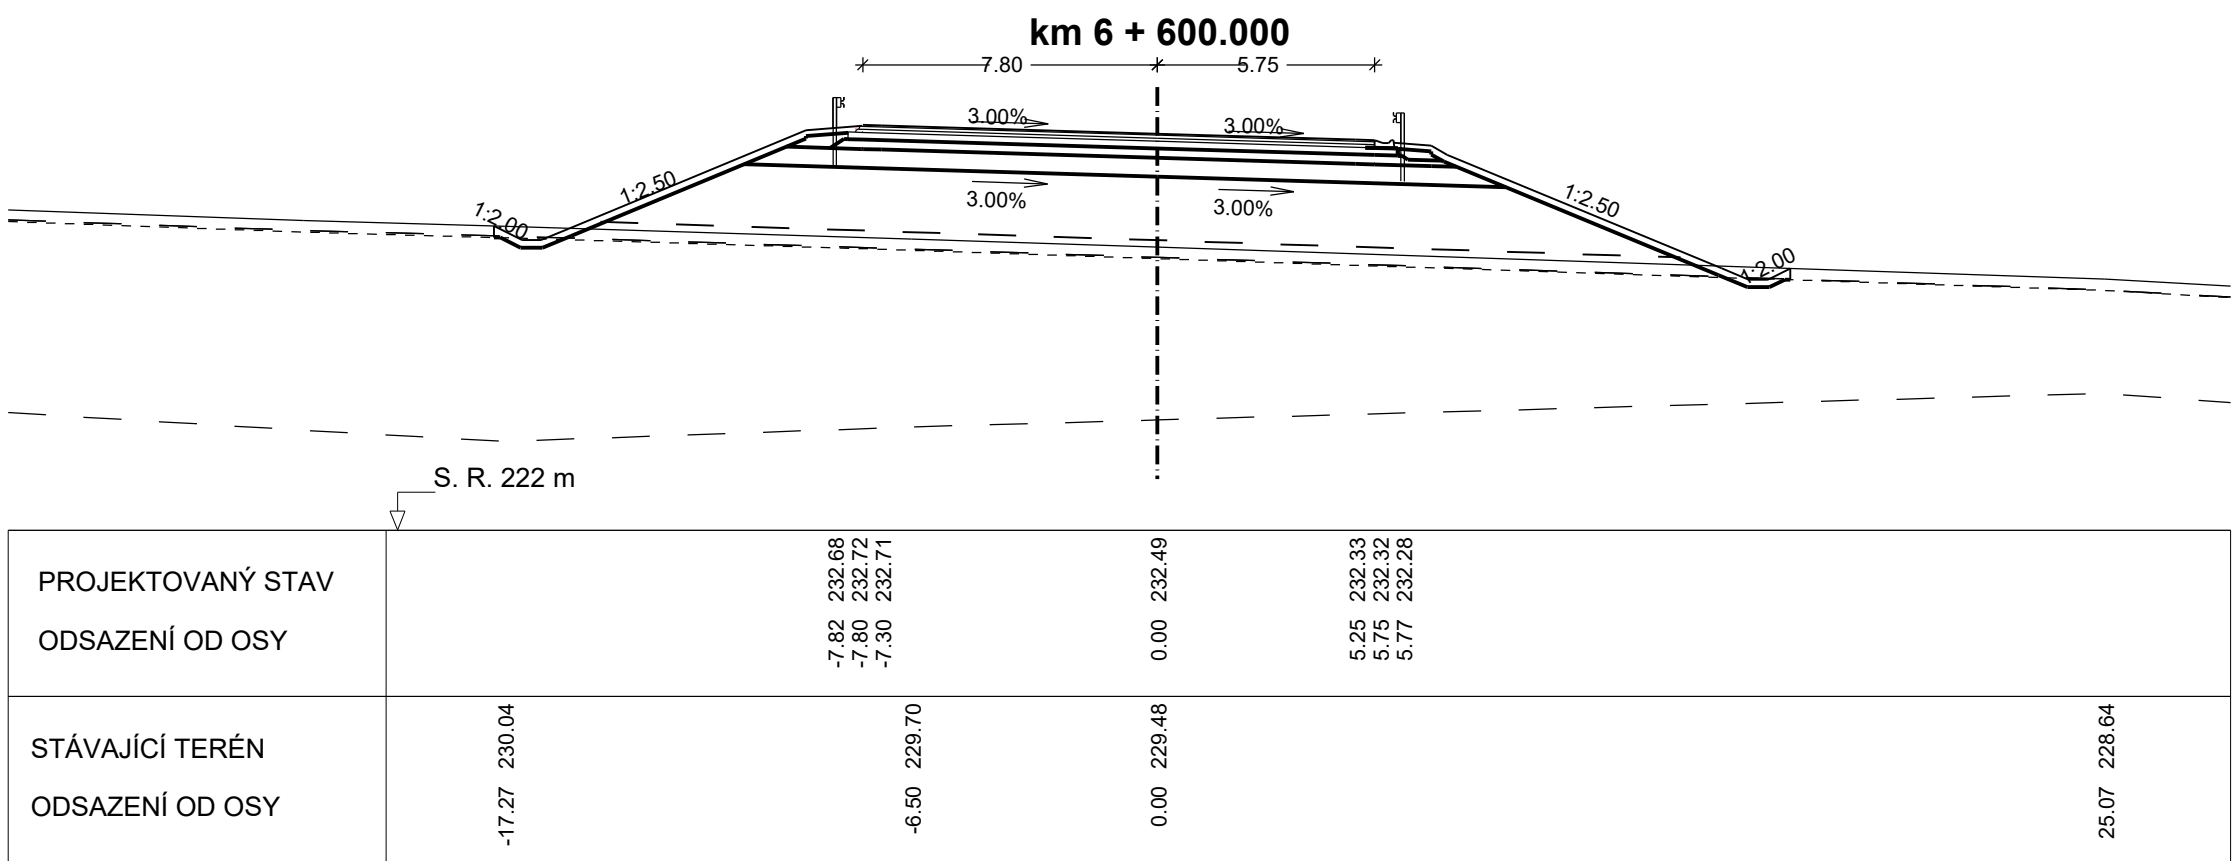
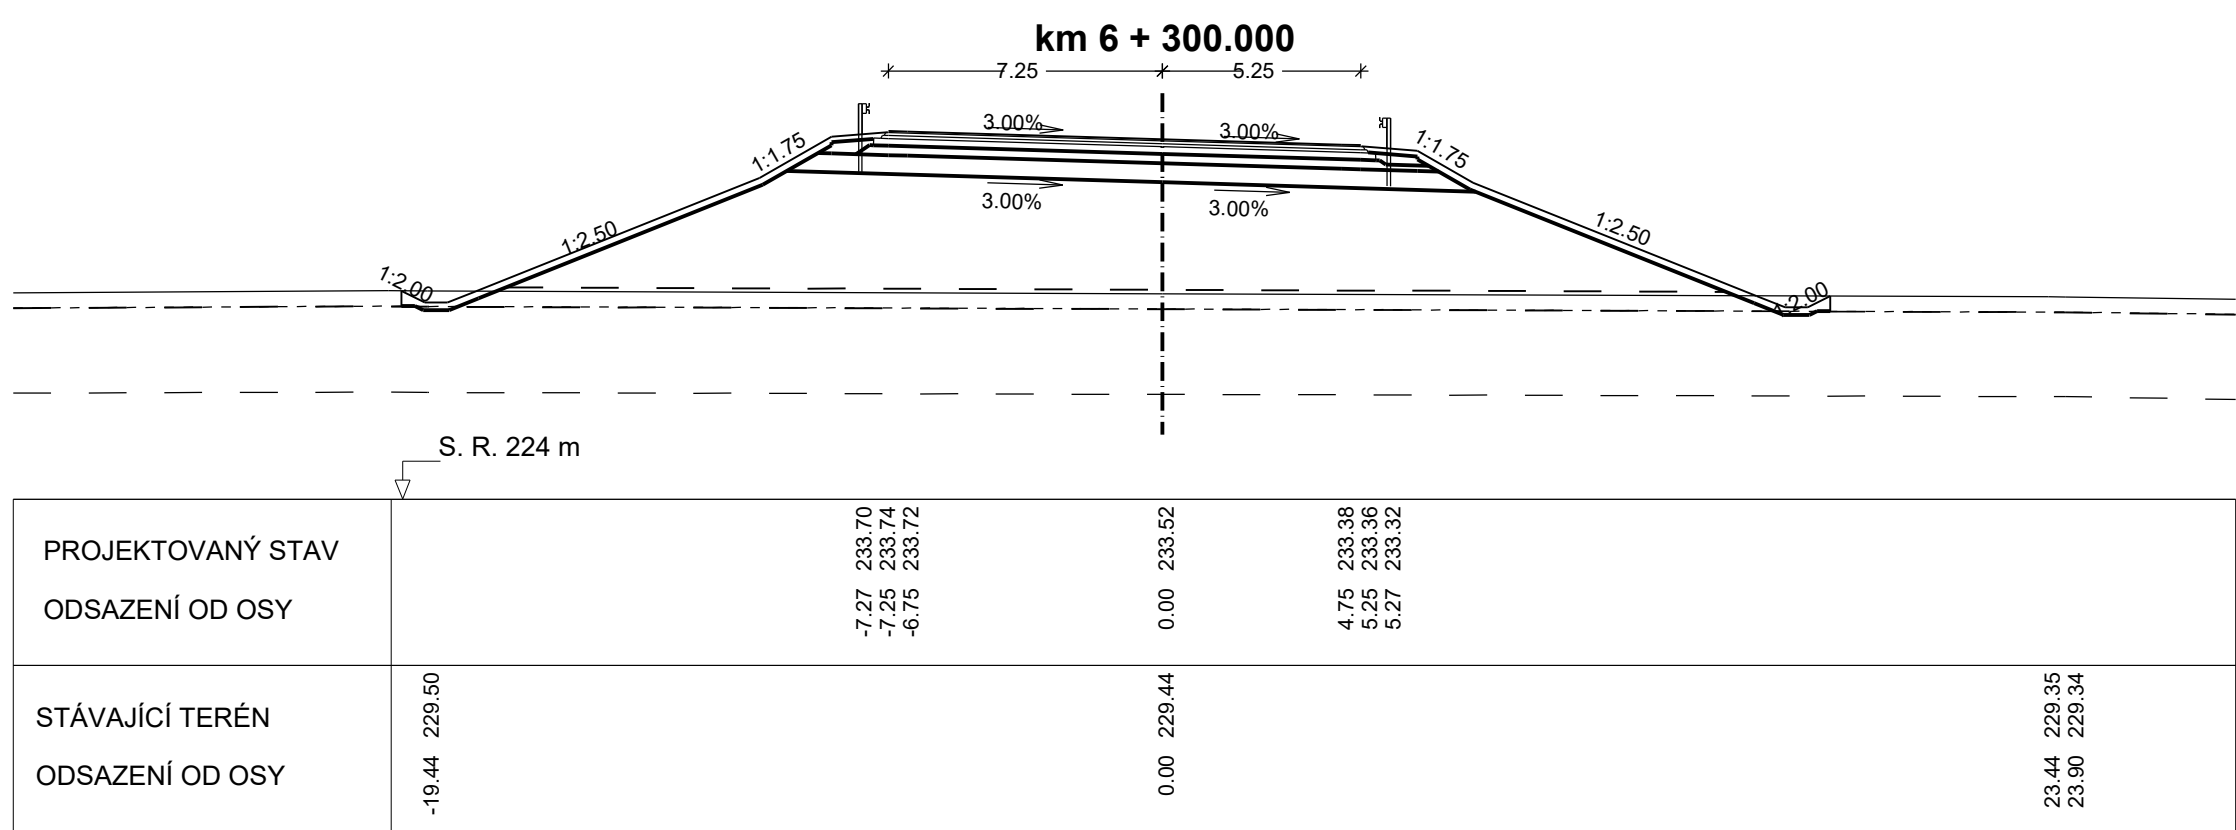


SO 101 - SILNICE I/16 MLADÁ BOLESLAV - MARTINOVICE
PŘÍČNÉ ŘEZY km 5,700 - 7,000, M 1 : 200

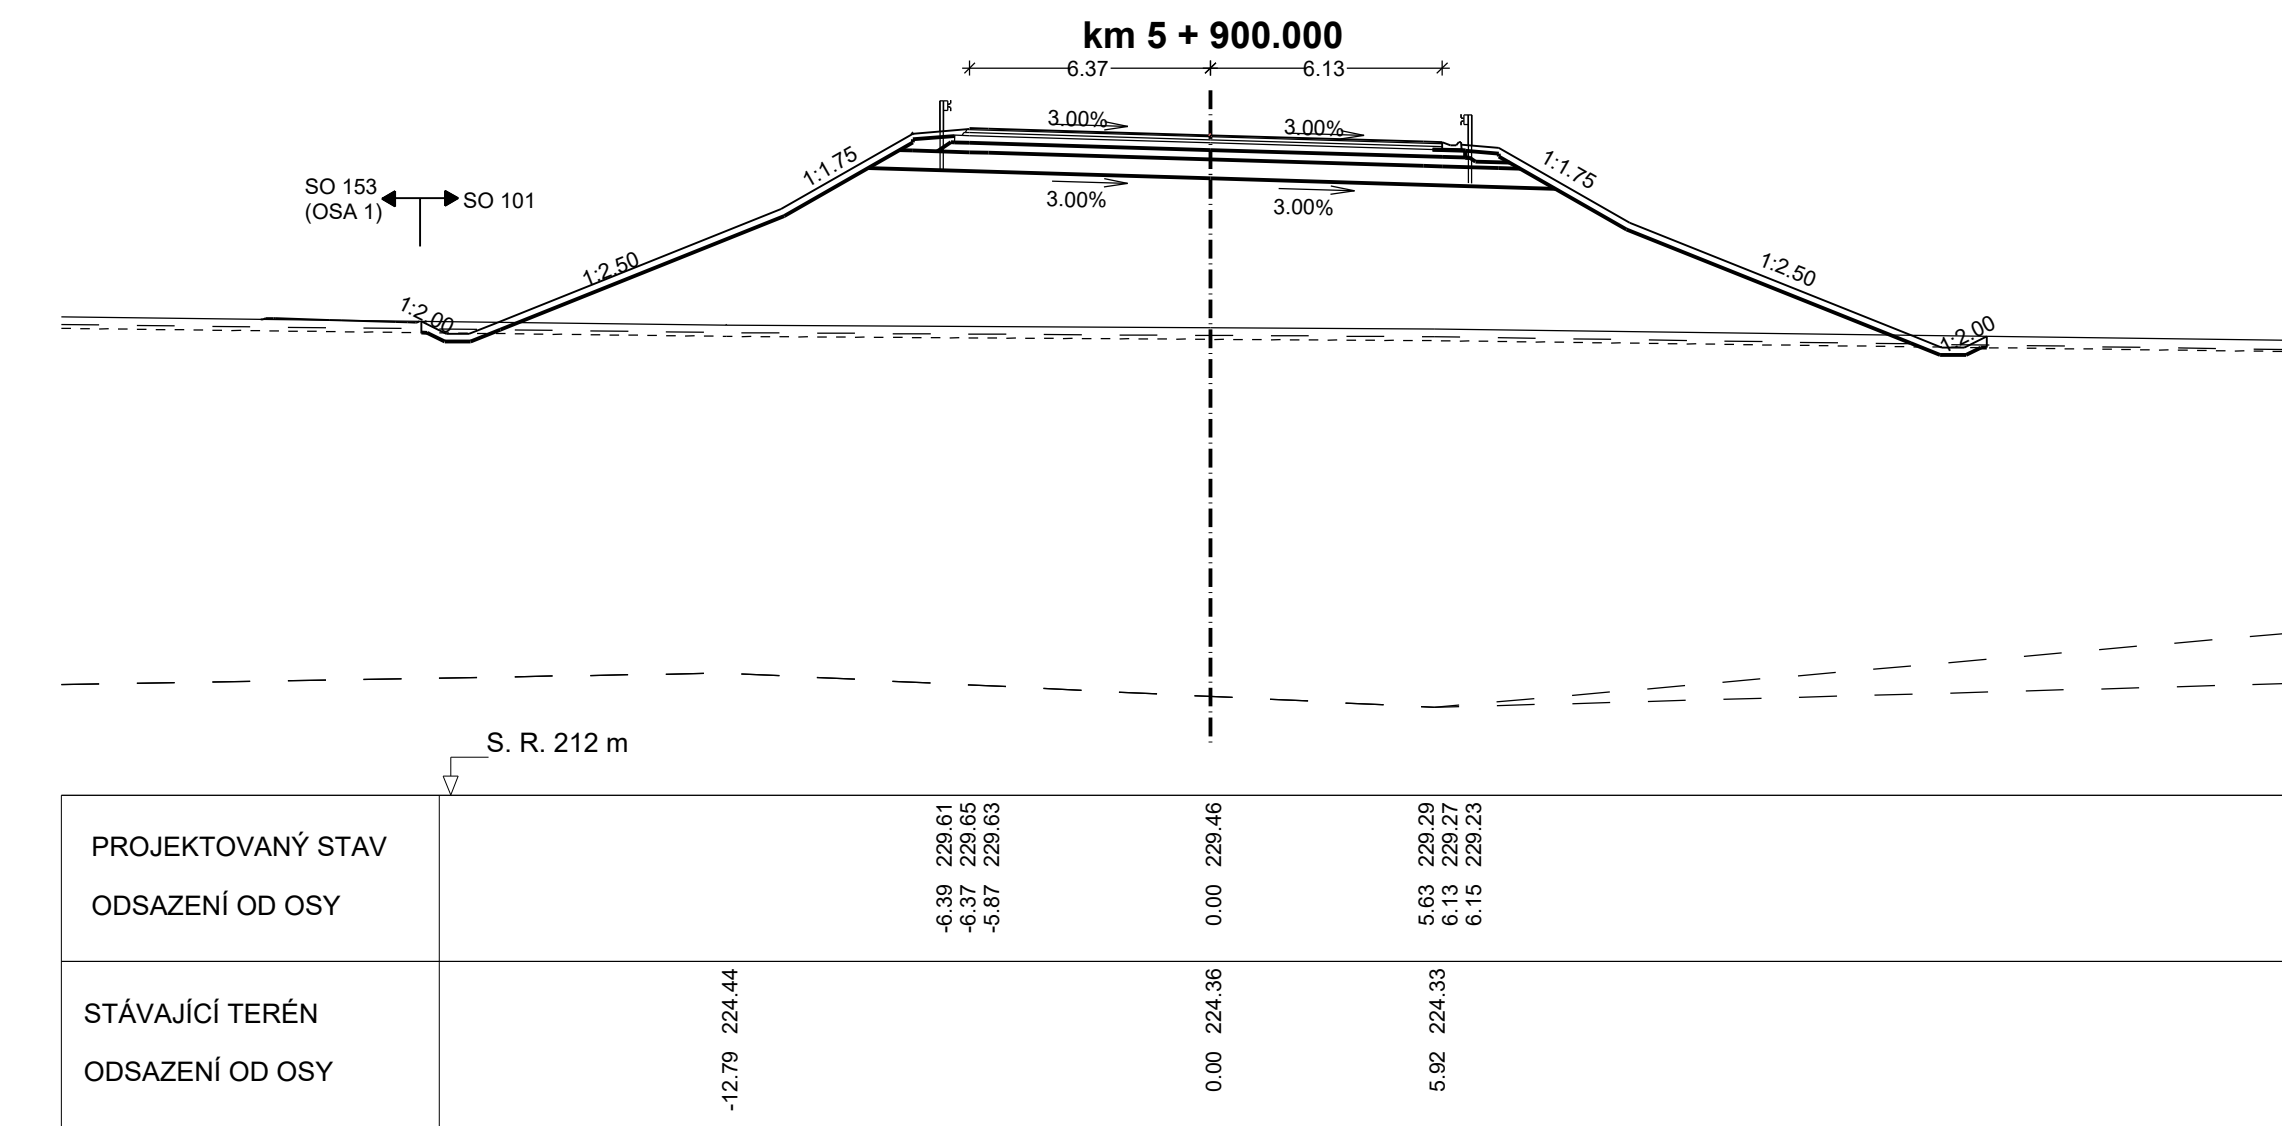

km 6 + 500.000

Viz 6.14 - RÁMOVÝ PROPUSTEK 2.0 x 2.0 m
V km 6.500

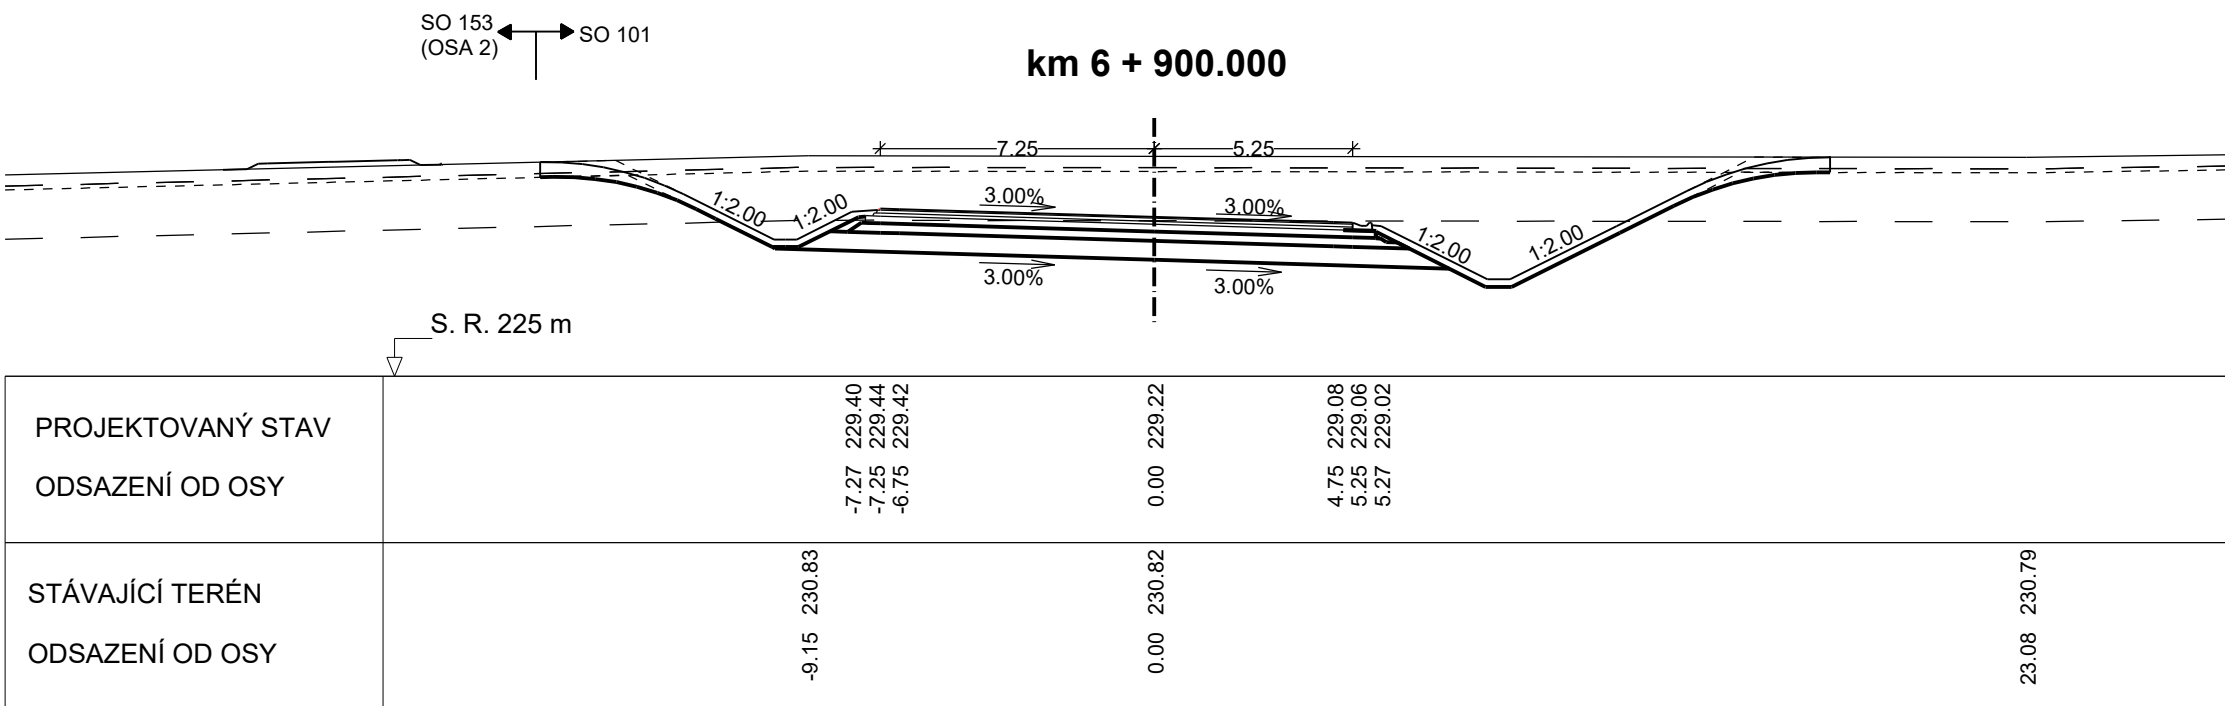

Výškový systém: BpV

SO 101 Silnice I/16 Mladá Boleslav - Martinovice

Objednatel: Ředitelství silnic a dálnic s. p.
Čerčanská 2023/12, Křt, 140 00 Praha 4

Zhotovitel: Valbek, spol. s r.o.
Vahurova 505/17
460 07 Liberec 3

Valbek
I/16 MLADÁ BOLESLAV - MARTINOVICE
Příloha PŘÍČNÉ ŘEZY km 5.700 - 7.000
5.4