SO 101 - SILNICE I/16 MLADÁ BOLESLAV - MARTINOVICE
PŘÍČNÉ ŘEZY km 7,100 - 8,200, M 1 : 200

km 7 + 100.000

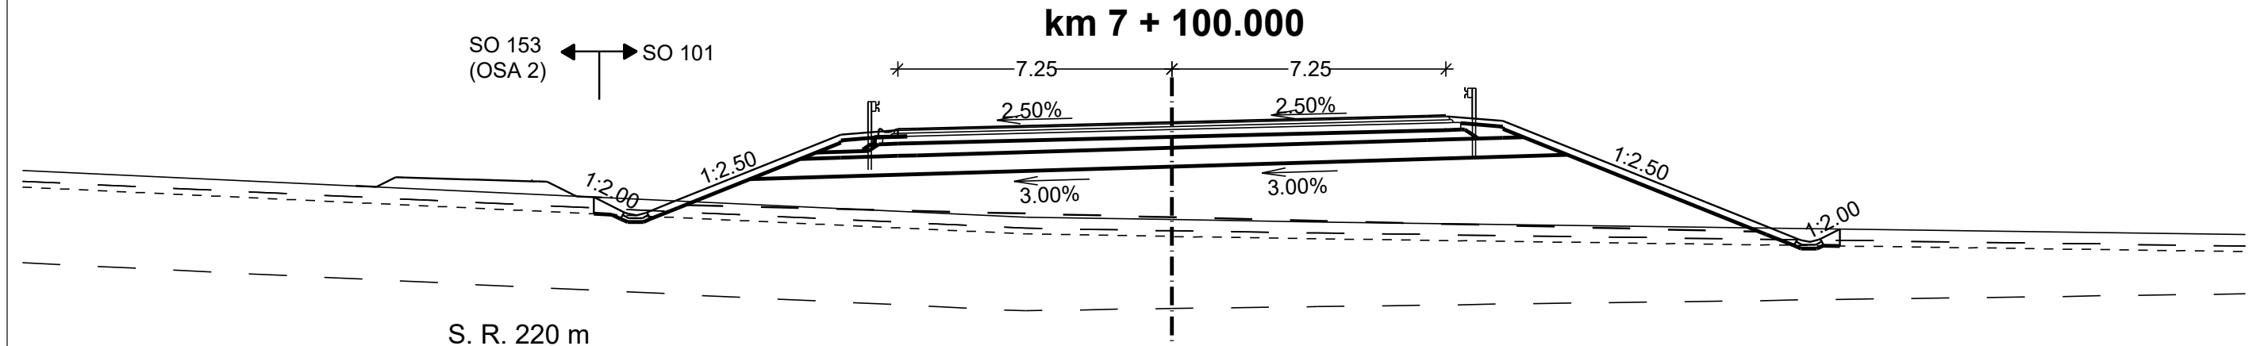
SO 153 (OSA 2)
SO 101
7.25
7.25
2.50%
2.50%
3.00%
3.00%
1:2.00
1:2.50
1:2.50
1:2.00
S. R. 220 m

ODSAZENÍ OD OSY	PROJEKTOVANÝ STAV
-7.27	226.80
-7.25	226.84
-6.75	226.85
0.00	227.02
6.75	227.19
7.25	227.20
7.27	227.16

ODSAZENÍ OD OSY	STÁVAJÍCÍ TERÉN
-3.87	224.50
0.00	224.44
3.86	224.38

km 7 + 200.000

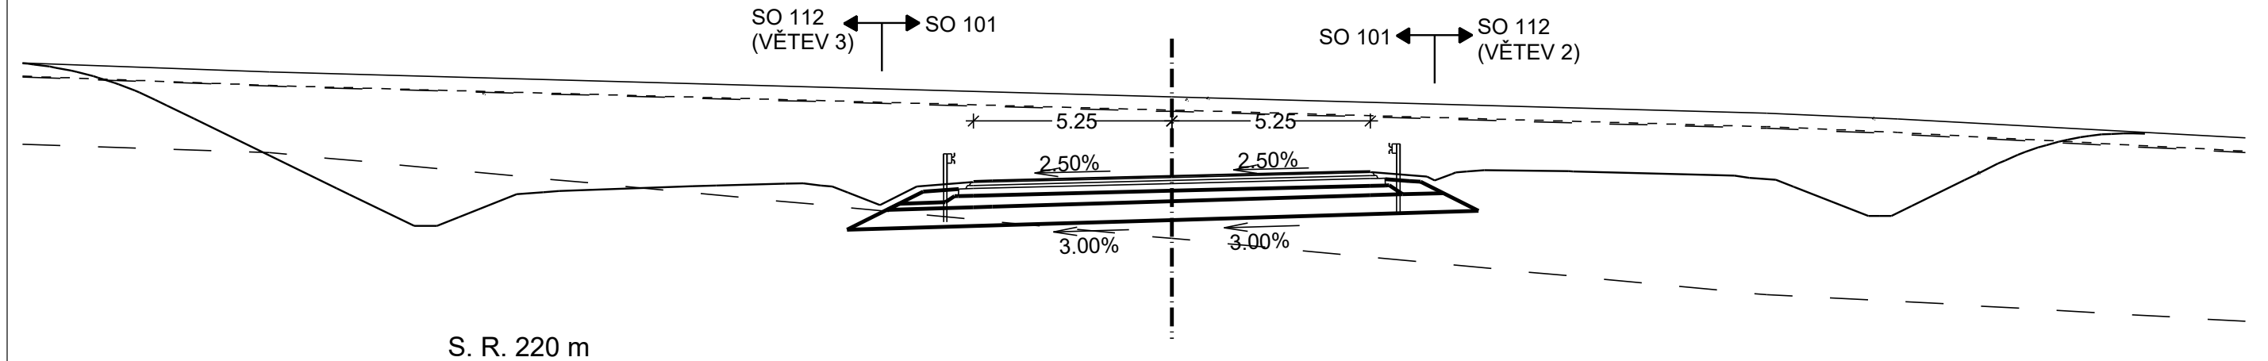
SO 112 (VĚTEV 3)
SO 101
SO 101
SO 112 (VĚTEV 2)
5.25
5.25
2.50%
2.50%
3.00%
3.00%
S. R. 220 m

ODSAZENÍ OD OSY	PROJEKTOVANÝ STAV
-5.27	225.75
-5.25	225.79
-4.75	225.80
0.00	225.92
4.75	226.04
5.25	226.05
5.27	226.01

ODSAZENÍ OD OSY	STÁVAJÍCÍ TERÉN
0.00	228.01
15.74	227.58
19.20	227.43

km 7 + 300.000

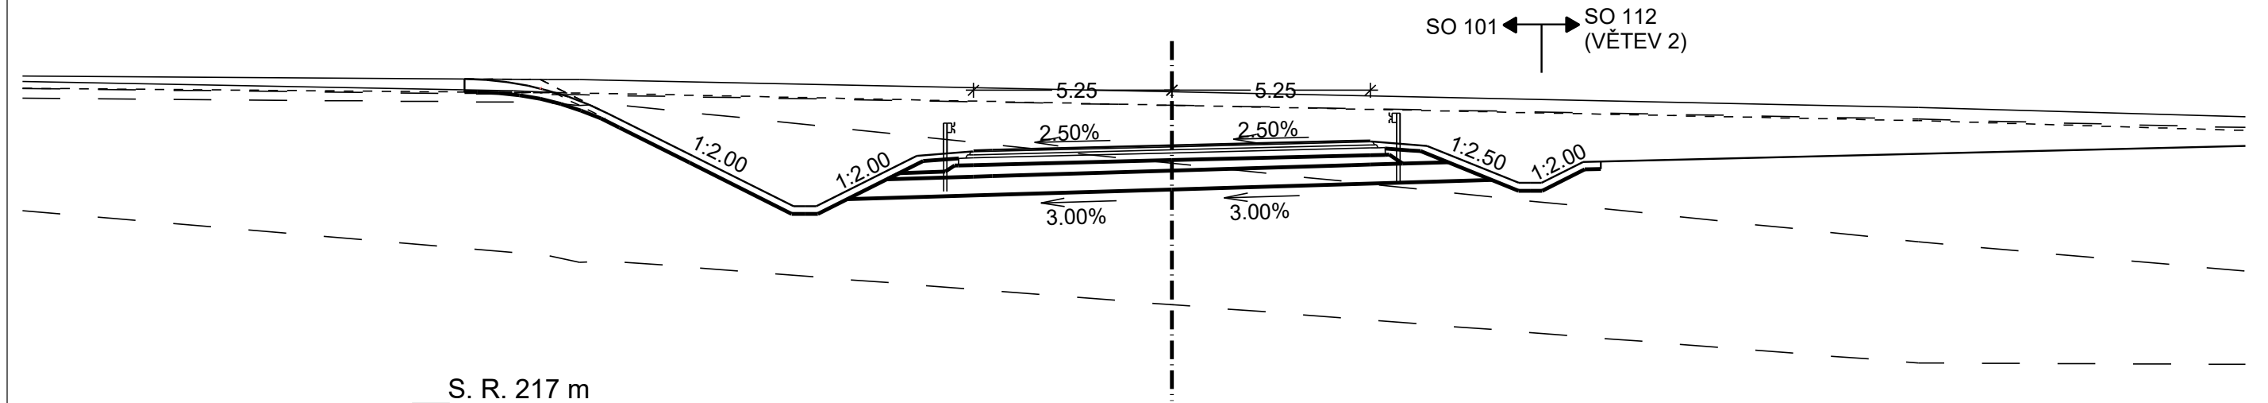
SO 101
SO 112 (VĚTEV 2)
5.25
5.25
2.50%
2.50%
3.00%
3.00%
1:2.00
1:2.00
1:2.50
1:2.00
S. R. 217 m

ODSAZENÍ OD OSY	PROJEKTOVANÝ STAV
-5.27	224.65
-5.25	224.69
-4.75	224.70
0.00	224.82
4.75	224.94
5.25	224.95
5.27	224.91

ODSAZENÍ OD OSY	STÁVAJÍCÍ TERÉN
-16.51	226.56
-15.67	226.55
-14.92	226.54
0.00	226.23
19.75	225.82

km 7 + 400.000

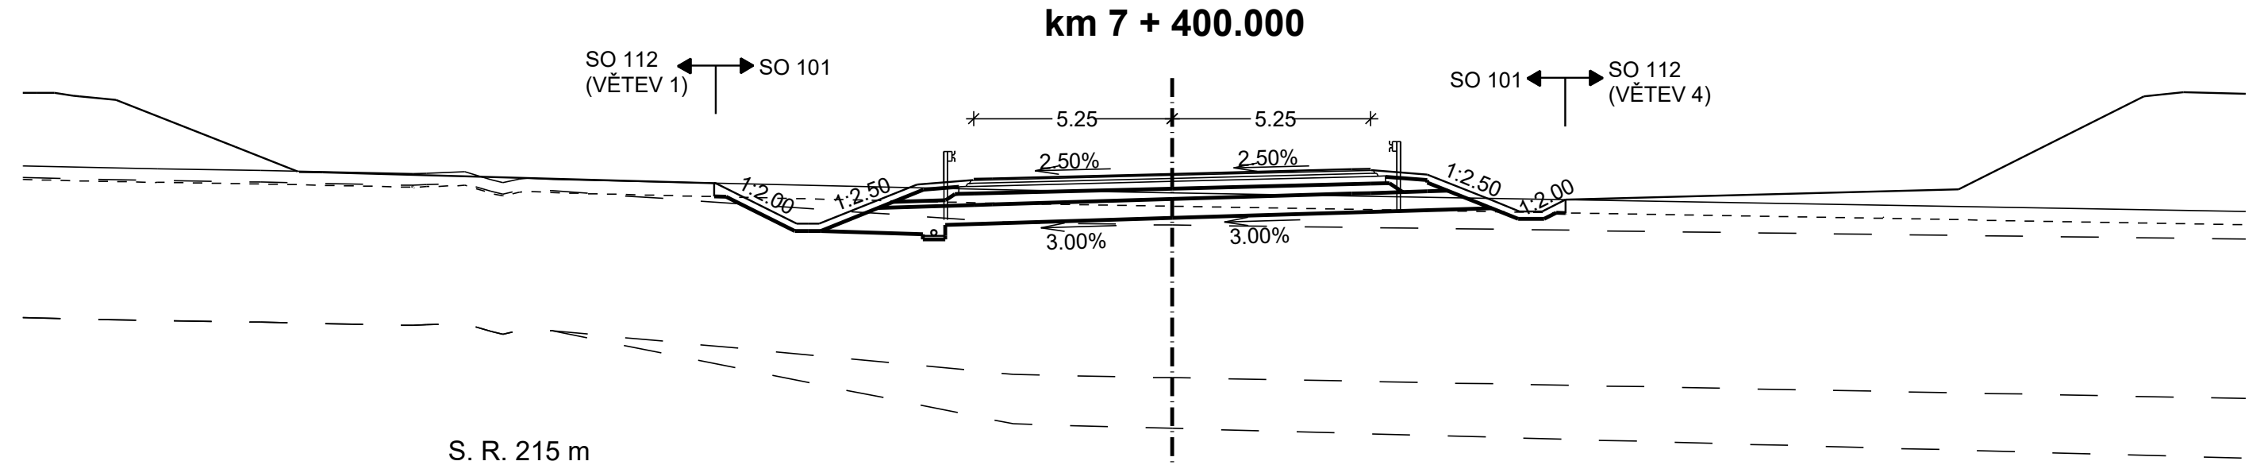
SO 112 (VĚTEV 1)
SO 101
SO 101
SO 112 (VĚTEV 4)
5.25
5.25
2.50%
2.50%
3.00%
3.00%
1:2.00
1:2.50
1:2.50
1:2.00
S. R. 215 m

ODSAZENÍ OD OSY	PROJEKTOVANÝ STAV
-5.27	223.55
-5.25	223.59
-4.75	223.61
0.00	223.72
4.75	223.84
5.25	223.86
5.27	223.82

ODSAZENÍ OD OSY	STÁVAJÍCÍ TERÉN
-19.72	223.74
-18.71	223.78
-18.02	223.57
-17.71	223.49
-17.27	223.59
-17.05	223.61
-16.40	223.58
-4.20	223.29
0.00	223.22

km 7 + 500.000

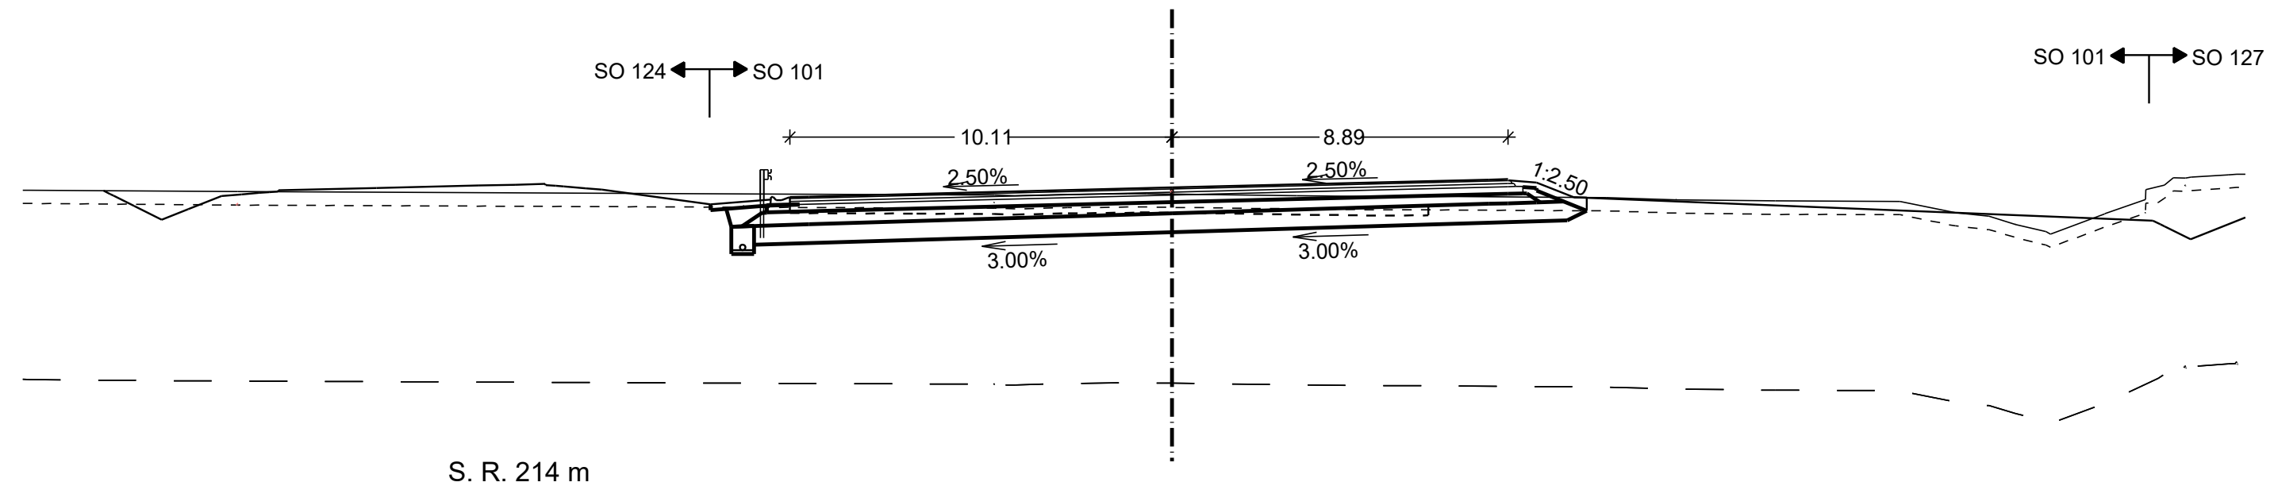
SO 124
SO 101
SO 101
SO 127
10.11
8.89
2.50%
2.50%
3.00%
3.00%
1:2.50
S. R. 214 m

ODSAZENÍ OD OSY	PROJEKTOVANÝ STAV
-10.13	222.62
-10.11	222.66
-9.61	222.68
0.00	222.92
8.39	223.13
8.89	223.14
8.91	223.10

ODSAZENÍ OD OSY	STÁVAJÍCÍ TERÉN
-6.76	222.73
-4.70	222.72
-4.16	222.70
-2.76	222.73
-1.17	222.75
-0.66	222.75
0.00	222.74
3.30	222.70
5.59	222.68
6.78	222.68
11.50	222.65
13.34	222.59
15.96	222.56
19.26	222.55
20.72	222.25
21.61	222.15
22.32	221.94
23.12	221.75
23.24	221.68
24.67	222.22
24.68	222.22
25.75	222.60
25.76	222.86
26.25	222.98
26.49	223.18

km 7 + 600.000

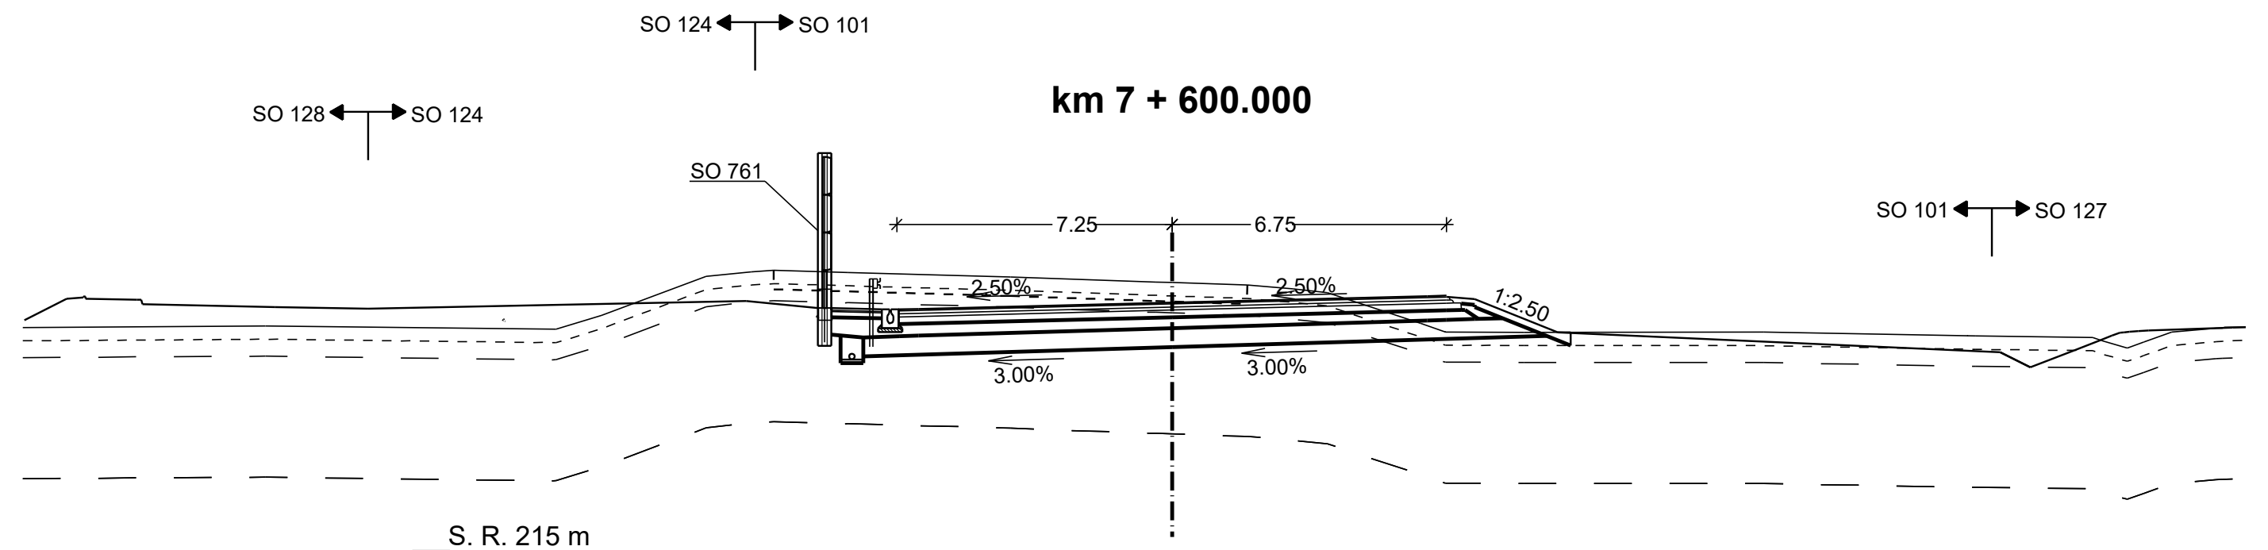
SO 124
SO 101
SO 128
SO 124
SO 761
SO 101
SO 127
7.25
6.75
2.50%
2.50%
3.00%
3.00%
1:2.50
S. R. 215 m

ODSAZENÍ OD OSY	PROJEKTOVANÝ STAV
-7.25	222.38
-7.25	222.34
-6.75	222.39
0.00	222.56
6.75	222.73
7.25	222.74
7.27	222.70

ODSAZENÍ OD OSY	STÁVAJÍCÍ TERÉN
-16.30	221.85
-15.10	222.22
-12.32	223.25
-11.14	223.37
-10.54	223.41
-8.59	223.36
-4.27	223.24
-0.43	223.10
0.00	223.09
1.99	223.02
3.19	222.92
4.10	222.82
6.57	222.01
7.23	221.78
9.31	221.77
15.65	221.78
21.24	221.68
24.35	221.64
24.59	221.55
25.26	221.36
25.70	221.51
26.44	221.78
27.62	221.88

km 7 + 700.000

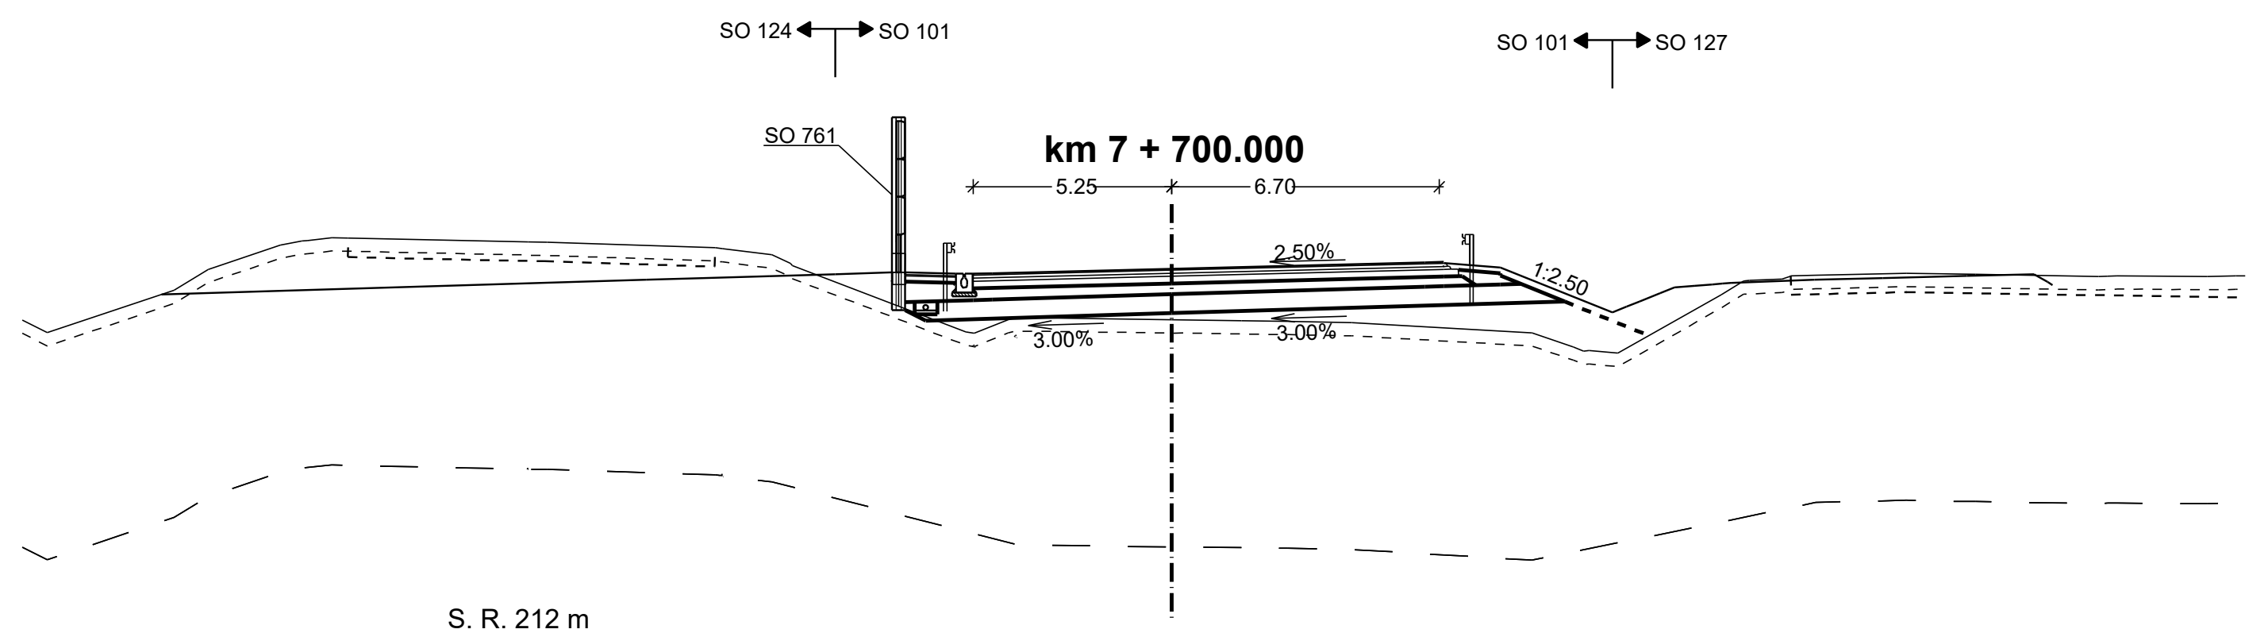
SO 124
SO 101
SO 101
SO 127
SO 761
5.25
6.70
2.50%
3.00%
3.00%
1:2.50
S. R. 212 m

ODSAZENÍ OD OSY	PROJEKTOVANÝ STAV
-7.05	222.56
-7.05	222.50
-5.75	222.53
-5.25	222.53
-5.25	222.49
-4.75	222.54
0.00	222.66
6.70	222.83
7.20	222.84
7.22	222.80

ODSAZENÍ OD OSY	STÁVAJÍCÍ TERÉN
-17.02	223.37
-16.52	223.36
-12.07	223.22
-11.89	223.19
-10.58	223.03
-10.09	222.80
-10.03	222.74
-5.45	220.99
-5.23	220.96
-4.33	221.31
-4.12	221.37
0.00	221.31
1.84	221.29
3.07	221.27
4.77	221.24
9.53	220.97
10.62	220.60
10.90	220.48
11.03	220.50
11.80	220.43
14.53	221.97
15.12	222.34
15.28	222.35
16.14	222.39
16.35	222.46
16.37	222.47
17.03	222.49
19.43	222.54
21.26	222.51
24.51	222.45
24.75	222.47
25.00	222.47
27.39	222.46

km 7 + 800.000

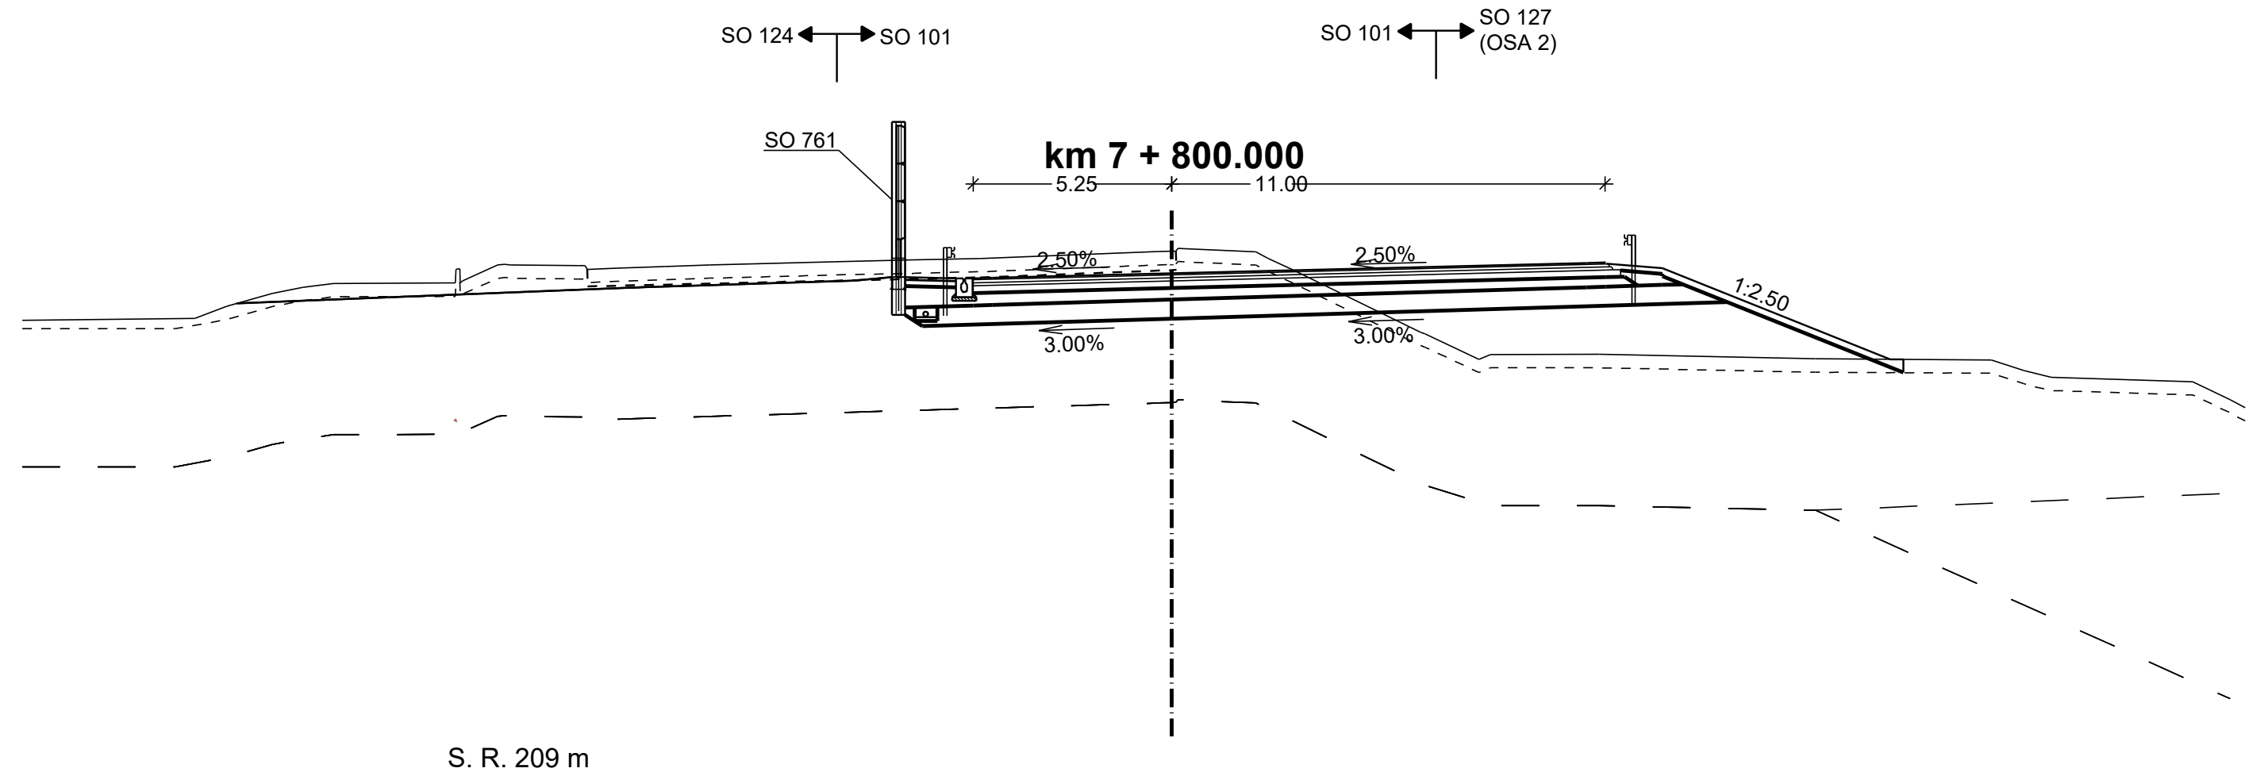
SO 124
SO 101
SO 101
SO 127 (OSA 2)
SO 761
5.25
11.00
2.50%
2.50%
3.00%
3.00%
1:2.50
S. R. 209 m

ODSAZENÍ OD OSY	PROJEKTOVANÝ STAV
-7.05	223.12
-7.05	223.06
-5.75	223.09
-5.25	223.09
-5.25	223.05
-4.75	223.10
0.00	223.22
11.00	223.49
11.50	223.50
11.52	223.47

ODSAZENÍ OD OSY	STÁVAJÍCÍ TERÉN
-18.77	223.02
-17.83	223.43
-17.65	223.45
-17.49	223.44
-15.70	223.42
-15.52	223.42
-15.46	223.33
-15.45	223.32
-14.67	223.35
-13.42	223.40
-12.22	223.44
-8.92	223.52
-6.81	223.57
-5.09	223.61
-0.36	223.79
0.00	223.80
0.11	223.80
0.16	223.88
0.17	223.88
0.30	223.87
2.23	223.79
2.54	223.62
3.20	223.31
6.59	221.65
6.69	221.62
8.12	220.94
8.43	221.07
11.31	221.07
17.03	220.96
21.68	220.93
22.55	220.65
23.26	220.47
27.00	220.35
27.99	219.88

km 7 + 900.000

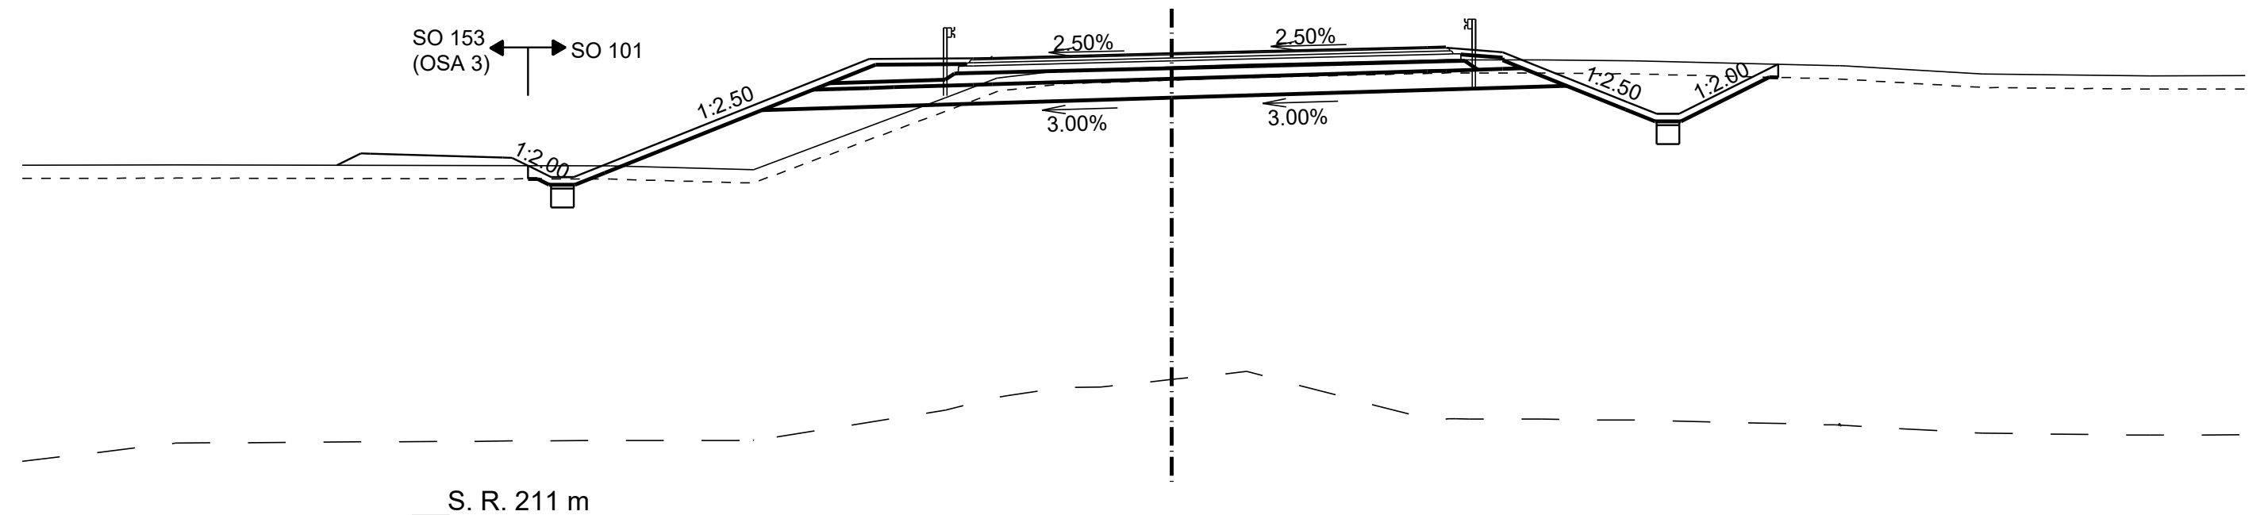
SO 153 (OSA 3)
SO 101
5.25
7.25
2.50%
2.50%
3.00%
3.00%
1:2.00
1:2.50
1:2.50
1:2.00
S. R. 211 m

ODSAZENÍ OD OSY	PROJEKTOVANÝ STAV
-7.05	224.13
-7.05	224.07
-5.75	224.10
-5.25	224.10
-5.25	224.06
-4.75	224.11
0.00	224.23
6.75	224.40
7.25	224.41
7.27	224.37

ODSAZENÍ OD OSY	STÁVAJÍCÍ TERÉN
-14.85	221.25
-11.06	221.15
-5.98	223.05
-4.62	223.57
-4.36	223.60
-2.82	223.78
-1.88	223.80
0.00	223.87
1.98	223.94
6.81	224.05
7.34	224.06
7.51	224.06
7.87	224.05
9.78	224.06
12.27	224.03
17.54	223.91
17.68	223.90
17.84	223.89
21.44	223.68
25.88	223.63

km 8 + 000.000

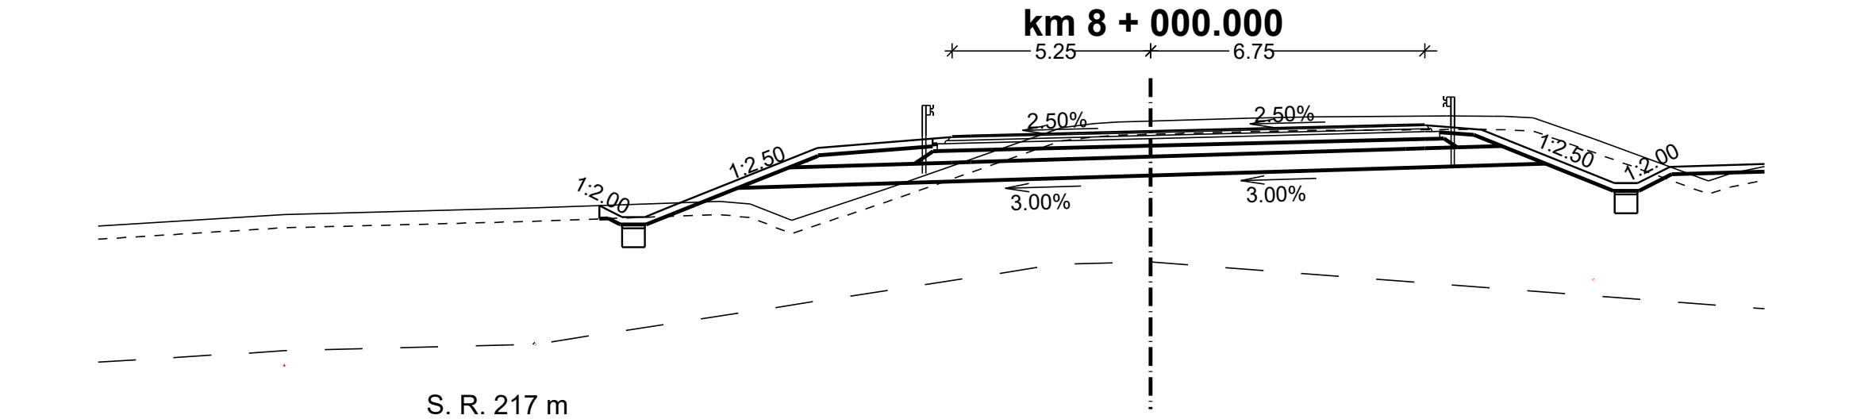
5.25
6.75
2.50%
2.50%
3.00%
3.00%
1:2.00
1:2.50
1:2.50
1:2.00
S. R. 217 m

ODSAZENÍ OD OSY	PROJEKTOVANÝ STAV
-5.75	225.52
-5.25	225.52
-5.25	225.48
0.00	225.65
6.75	225.82
7.25	225.83
7.27	225.79

ODSAZENÍ OD OSY	STÁVAJÍCÍ TERÉN
-16.29	223.62
-11.40	223.79
-10.59	223.72
-9.49	223.29
-6.97	224.13
-2.36	225.74
-1.51	225.84
-0.88	225.89
0.00	225.92
2.59	225.99
4.20	226.02
7.84	226.05
9.08	226.04
9.33	226.04
10.12	226.00
11.73	225.44
14.75	224.33
15.33	224.52
16.24	224.71

km 8 + 100.000

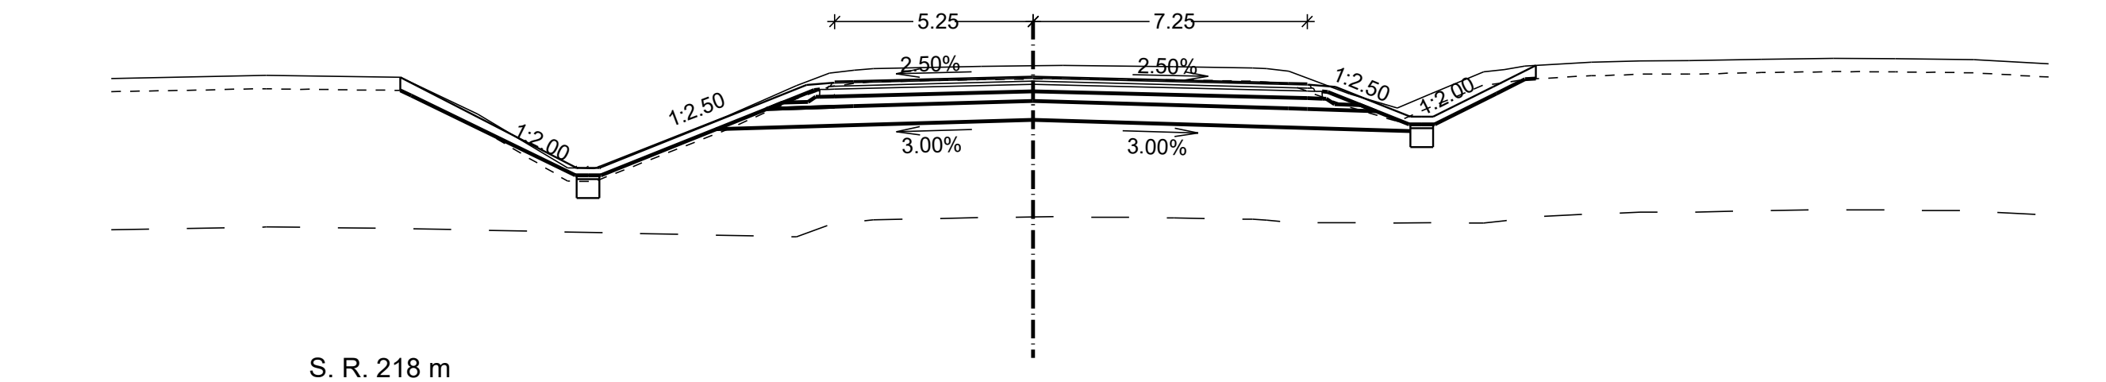
5.25
7.25
2.50%
2.50%
3.00%
3.00%
1:2.00
1:2.50
1:2.50
1:2.00
S. R. 218 m

ODSAZENÍ OD OSY	PROJEKTOVANÝ STAV
-5.27	226.93
-5.25	226.97
-4.75	226.98
0.00	227.10
6.75	226.93
7.25	226.92
7.27	226.88

ODSAZENÍ OD OSY	STÁVAJÍCÍ TERÉN
-16.74	227.08
-14.69	226.11
-12.31	224.69
-12.03	224.69
-11.62	224.67
-8.07	226.06
-6.26	226.86
-5.39	227.19
-4.74	227.27
-4.23	227.31
-1.37	227.37
0.00	227.39
0.79	227.40
3.73	227.36
5.80	227.33
6.17	227.31
6.76	227.24
8.37	226.64
9.63	226.27
10.51	226.64
11.91	227.22
12.47	227.28
13.01	227.38
14.76	227.48
16.06	227.51
17.35	227.52
19.26	227.56
21.16	227.58
22.81	227.57
24.89	227.55
26.86	227.44

km 8 + 200.000

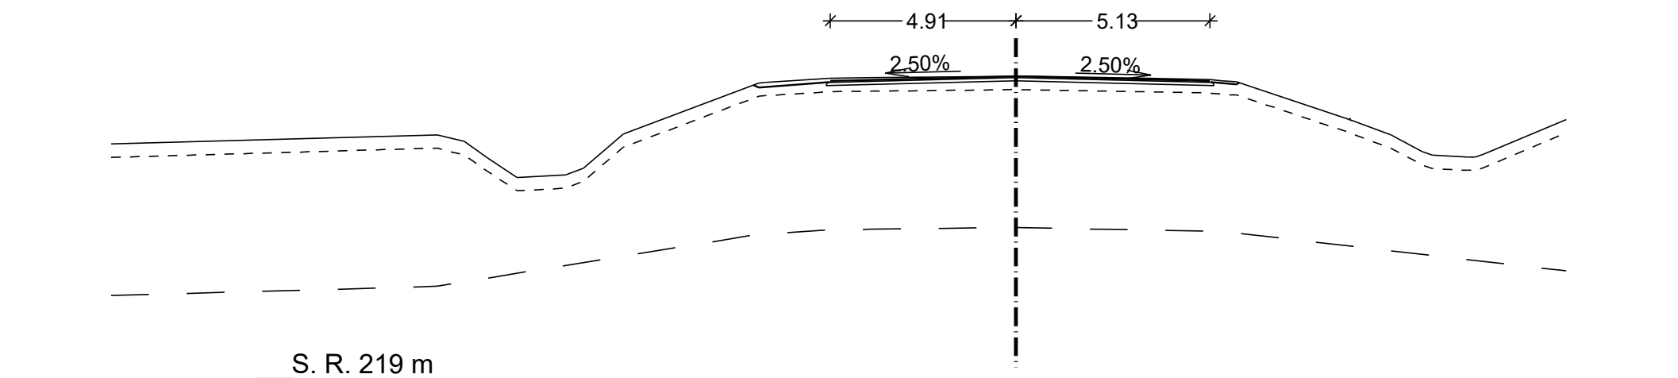
4.91
5.13
2.50%
2.50%
S. R. 219 m

ODSAZENÍ OD OSY	PROJEKTOVANÝ STAV
-4.93	227.83
-4.91	227.87
-4.41	227.88
0.00	227.99
4.63	227.88
5.13	227.87
5.15	227.83

ODSAZENÍ OD OSY	STÁVAJÍCÍ TERÉN
-15.30	226.44
-14.59	226.27
-13.97	225.83
-13.20	225.32
-11.96	225.38
-11.92	225.38
-11.44	225.56
-10.38	226.47
-6.80	227.81
-6.63	227.83
-4.91	227.94
-3.81	227.95
0.00	227.99
0.08	227.99
3.43	227.94
5.13	227.90
5.44	227.87
5.83	227.85
8.84	226.84
9.92	226.44
10.74	226.00
11.01	225.91
11.93	225.86
12.15	225.86
12.37	225.93
14.55	226.85

Výškový systém: Bpv

SO 101 Silnice I/16 Mladá Boleslav - Martinovice

Objednatel:

Ředitelství silnic a dálnic s. p.
Čerčanská 2023/12, Krč, 140 00 Praha 4

Zhotovitel:

Valbek, spol. s r.o.
Vaňurova 505/17
460 07 Liberec 3

Vypracoval	A. BARTONÍČKOVÁ		**Zak. číslo**	**21-LI13-001**
Zodp. projektant	ING. T. KLIMENT		**Datum**	**02/2025**
Tech. kontrola	ING. M. HANŽL		**Stupeň**	**PDPS**
Akce	**I/16 MLADÁ BOLESLAV - MARTINOVICE**		**Počet formátů**	**14 x A4**
			Měřítko	**1 : 200**
			Č. přílohy	**Paré**
Příloha	PŘÍČNÉ ŘEZY km 7,100 - 8,200		**5.5**	

Zhotovitel:
Valbek, spol. s r.o.
Vaňurova 505/17
460 07 Liberec 3