



SO 101 - SILNICE I/16 MLADÁ BOLESLAV - MARTINOVICE
RÁMOVÝ PROPUSTEK 2,0 x 2,0 m V km 0,660, M 1 : 100


PŮDORYS

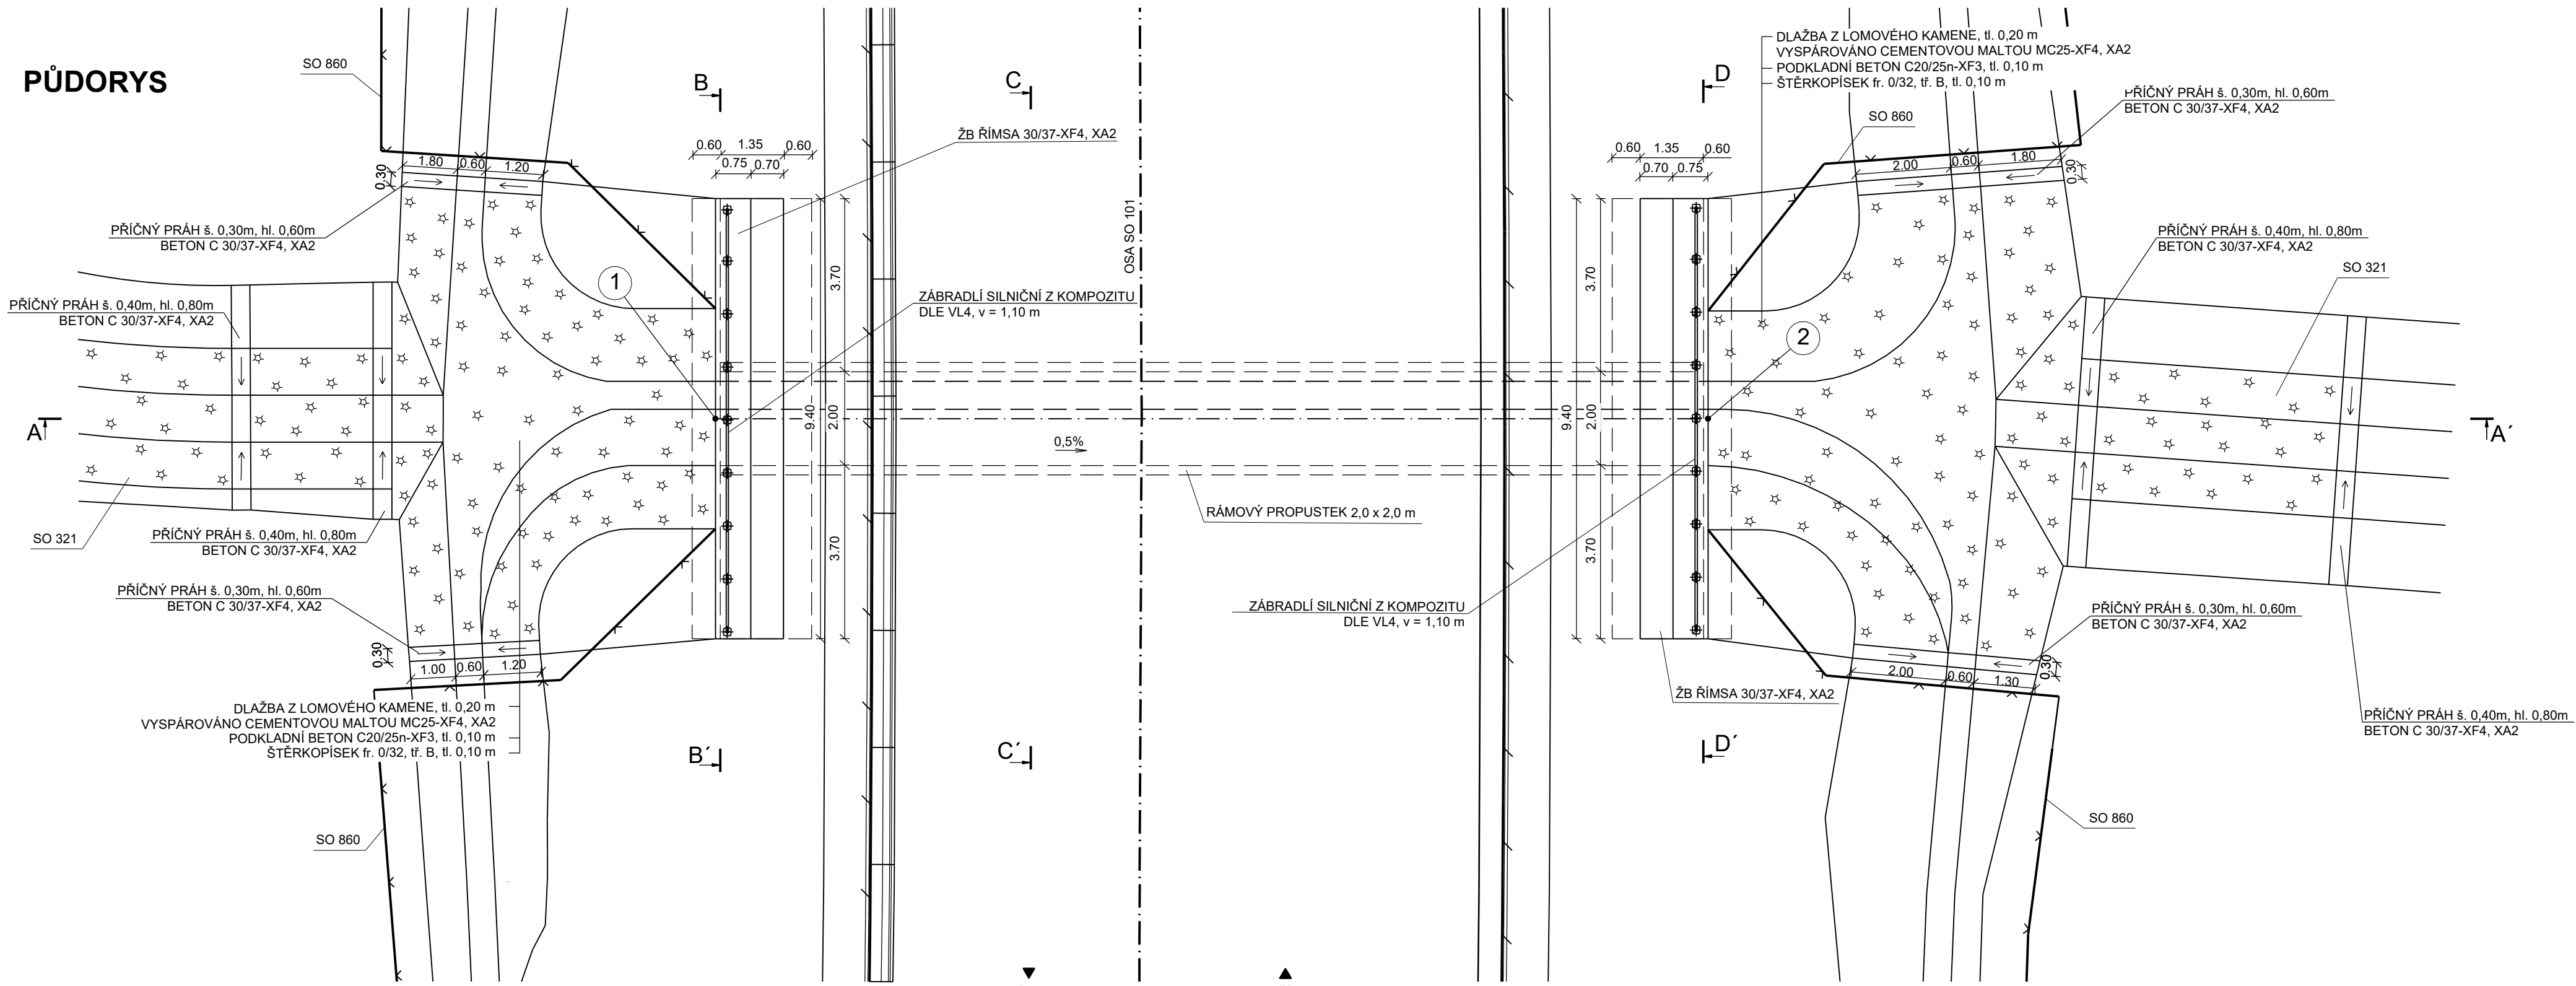


PODÉLNÝ ŘEZ A-A'

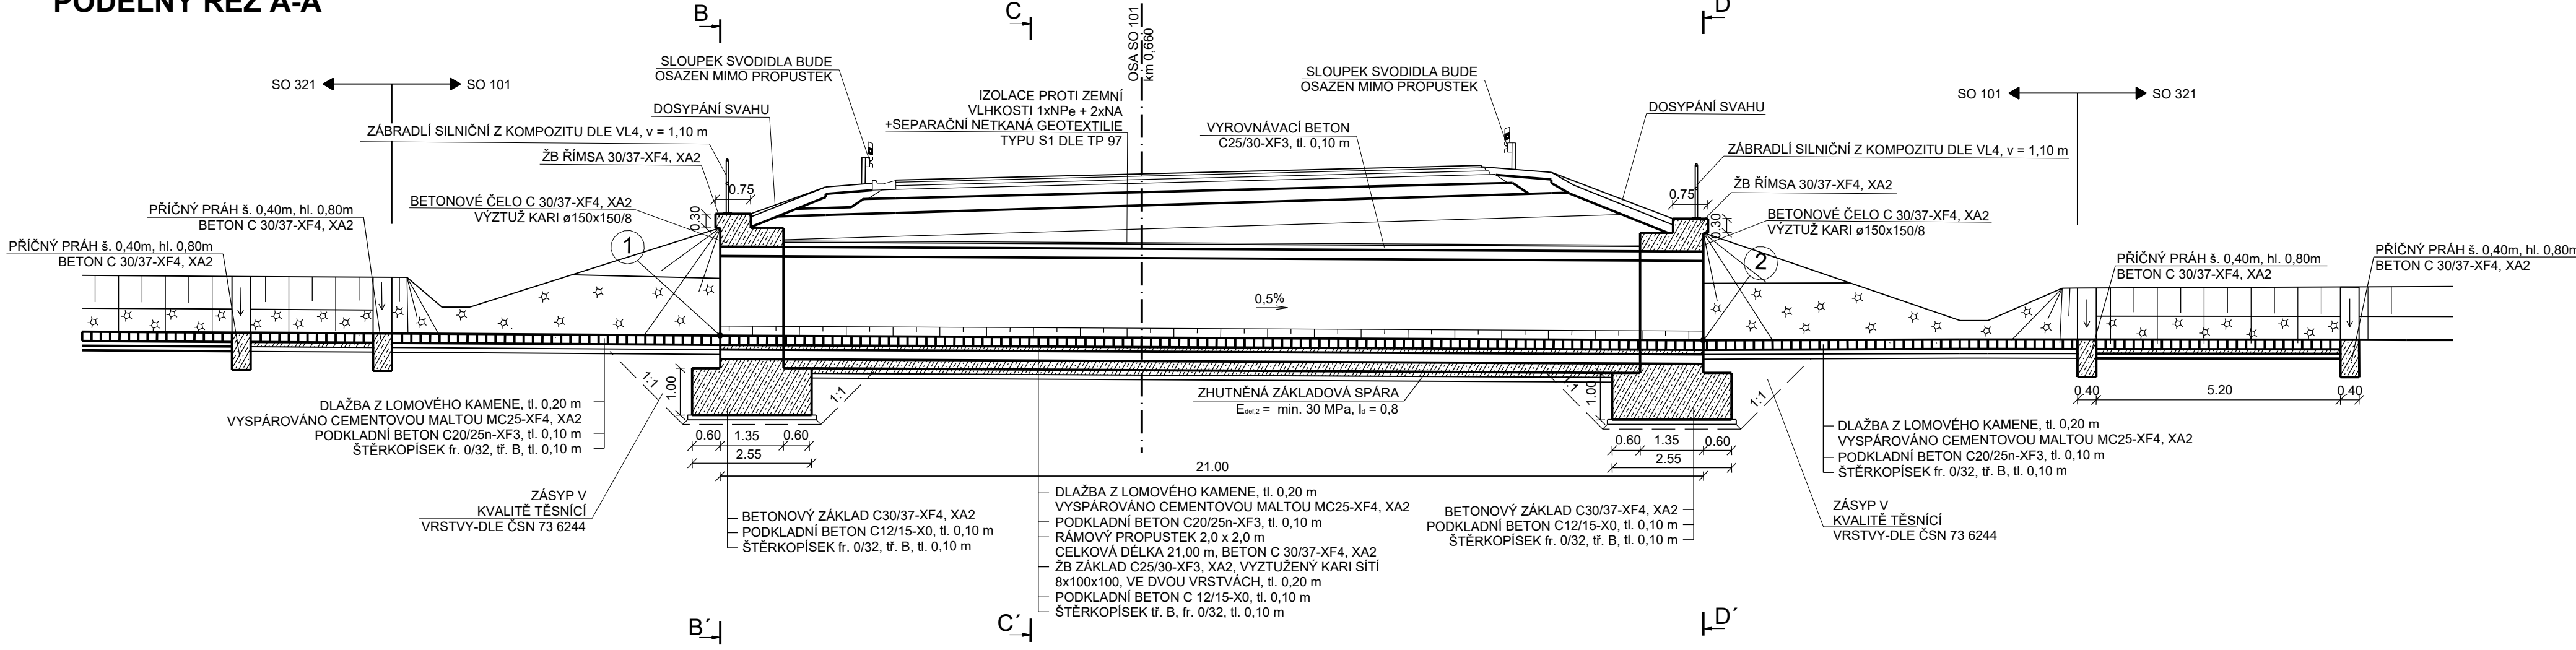


POHLED NA VÝTOK
ŘEZ D-D'

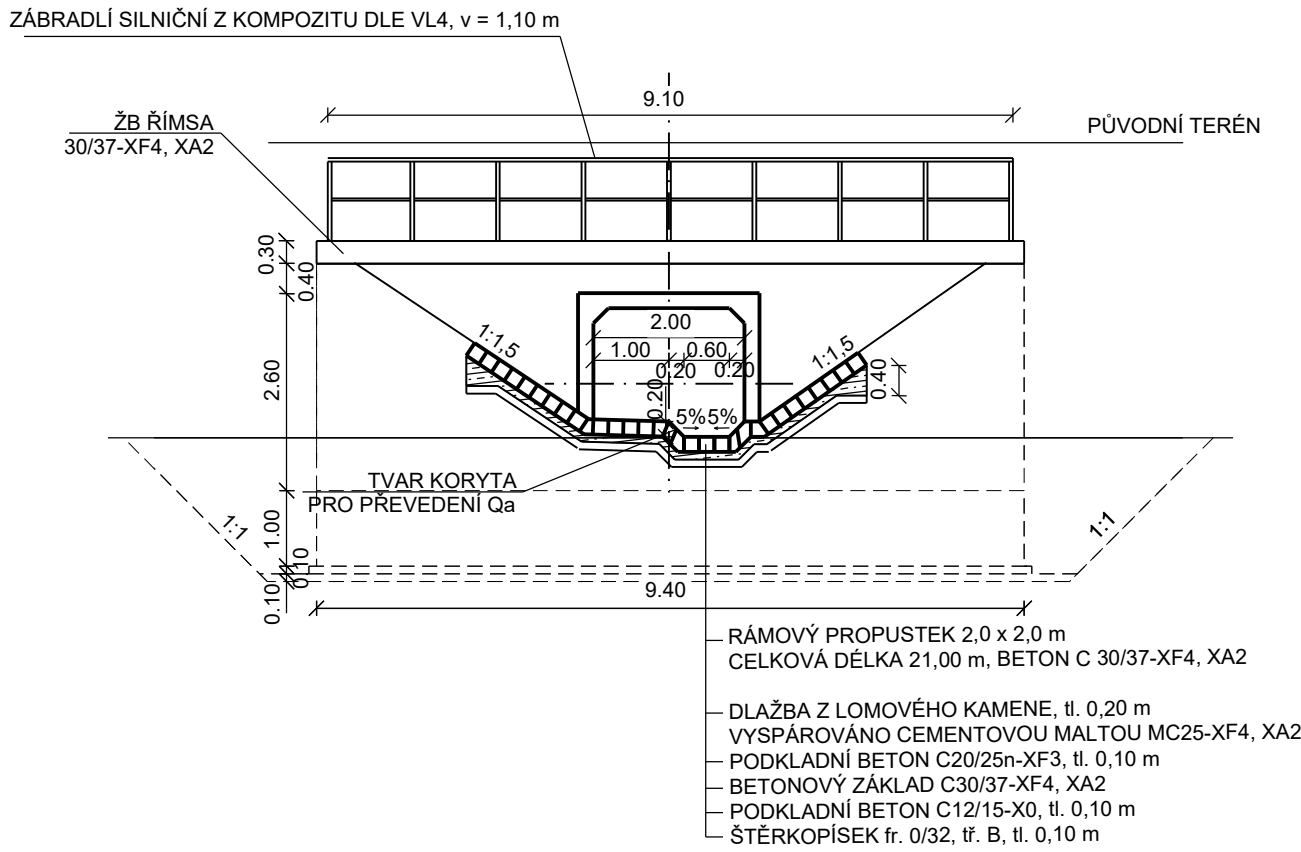

POHLED NA VTOK
ŘEZ B-B'

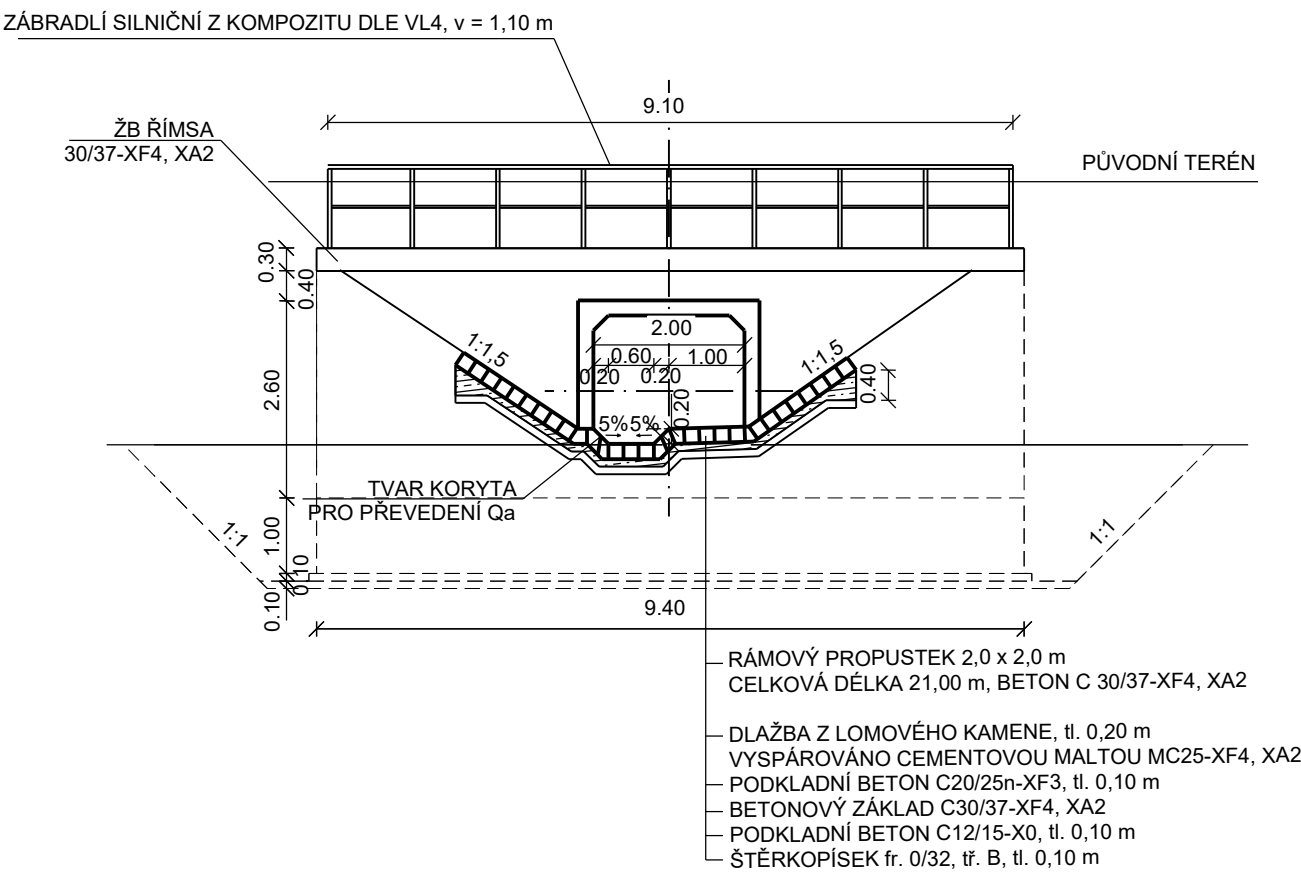


PŘÍČNÝ ŘEZ C-C'

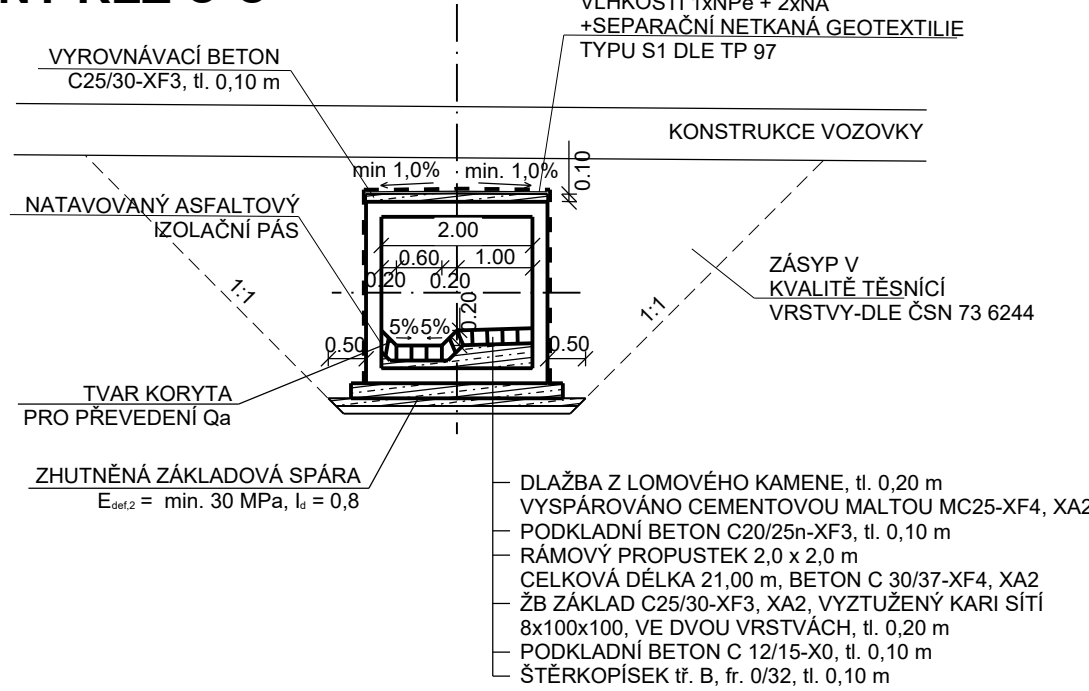


POZNÁMKA:

- SPÁROVÁNÍ DLAŽBY Z LOMOVÉHO KAMENE BUDE VYPLNĚNÉ CEMENTOVOU MALTOU M25 S ODOLNOSTÍ XF4, tl. min. 200 mm
- VŠECHNY BETONOVÉ PRVKY, KTERÉ PŘÍJÍŠ DO STYKY SE ZEMINOU MUSÍ BYT OPATŘENY NÁTĚRY: 1x NPc A 2x NA
- VYTÝČENÍ BUDE PROVEDENO DLE TKP 1 A SOUVISEJÍCÍCH PŘEDPISŮ
- SKLONY SVAHŮ JSOU URČENY SKLONEM SILNIČNÍHO TĚLESA A PŘÍLEHLÝCH PŘÍKOPŮ
- DETAILY JSOU KÓTOVÁNY V MILIMETRECH
- KORYTO BUDE VYTVAROVÁNO DO STŘELKY

DETAIL UKOTEVNÍ, M 1:10

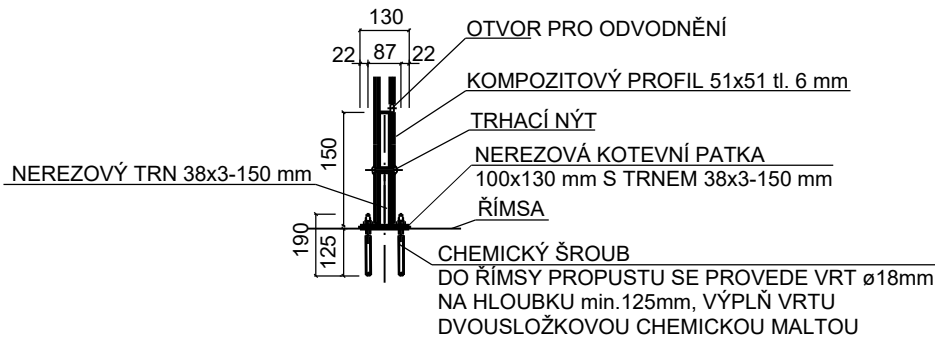

DETAIL KOTEVNÍ PATKY, M 1:10

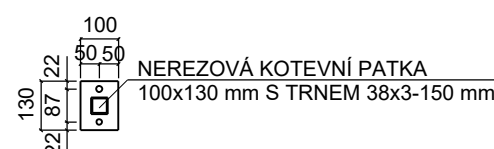

PARAMETRY PROPUSTKŮ					VYTÝČOVANÉ BODY	
STANIČENÍ [km]	DN [m]	DĚLKA DL [m]	SKLON S [‰]	ÚHEL α [°]	VTOK - 01 Y / X [S-JTSK] / Z [Bpv]	VÝTOK - 02 Y / X [S-JTSK] / Z [Bpv]
0,660	2 x 2	21,00	0,50	90	700321,303/1010956,173/212,09	700338,410/1010968,395/211,95

Souřadnicový systém: S-JTSK
Výškový systém: Bpv

SO 101 Silnice I/16 Mladá Boleslav - Martinovice

Objednatel:



Ředitelství silnic a dálnic s. p.
Čerčanská 2023/12, Krč, 140 00 Praha 4

Zhotovitel:



Valbek, spol. s r.o.
Vaňurova 505/17
460 07 Liberec 3

	Vypracoval	A. BARTOŇKOVÁ	Zak. číslo	21-L113-001
	Zodp. projektant	ING. T. KLIMENT	Datum	02/2025
	Tech. kontrola	ING. M. HANŽL	Stupeň	PDPS
	I/16 MLADÁ BOLESLAV - MARTINOVICE		Počet formátů	10 x A4
Zhotovitel: Valbek, spol. s r.o. Vaňurova 505/17 460 07 Liberec 3	Příloha RÁMOVÝ PROPUSTEK 2,0 x 2,0 m V km 0,660		Měřítko Č. přílohy	1 : 100 Paré
				6.1