



SO 101 - SILNICE I/16 MLADÁ BOLESLAV - MARTINOVICE
RÁMOVÝ PROPUSTEK 2,0 x 2,0 m V km 1,480, M 1 : 100

PARAMETRY PROPUSTKŮ					VYTÝČOVANÉ BODY	
STANIČENÍ [km]	DN	DĚLKA DL [m]	SKLON S. [‰]	ÚHEL α [°]	VTKO - 01 Y / X [S-JTSK] / Z [Bpv]	VÝTKO - 02 Y / X [S-JTSK] / Z [Bpv]
1,480	2 x 2	23,00	0,50	90	699646,062/1011379,316/212,42	699651,117/1011401,754/212,31


PŪDORYS

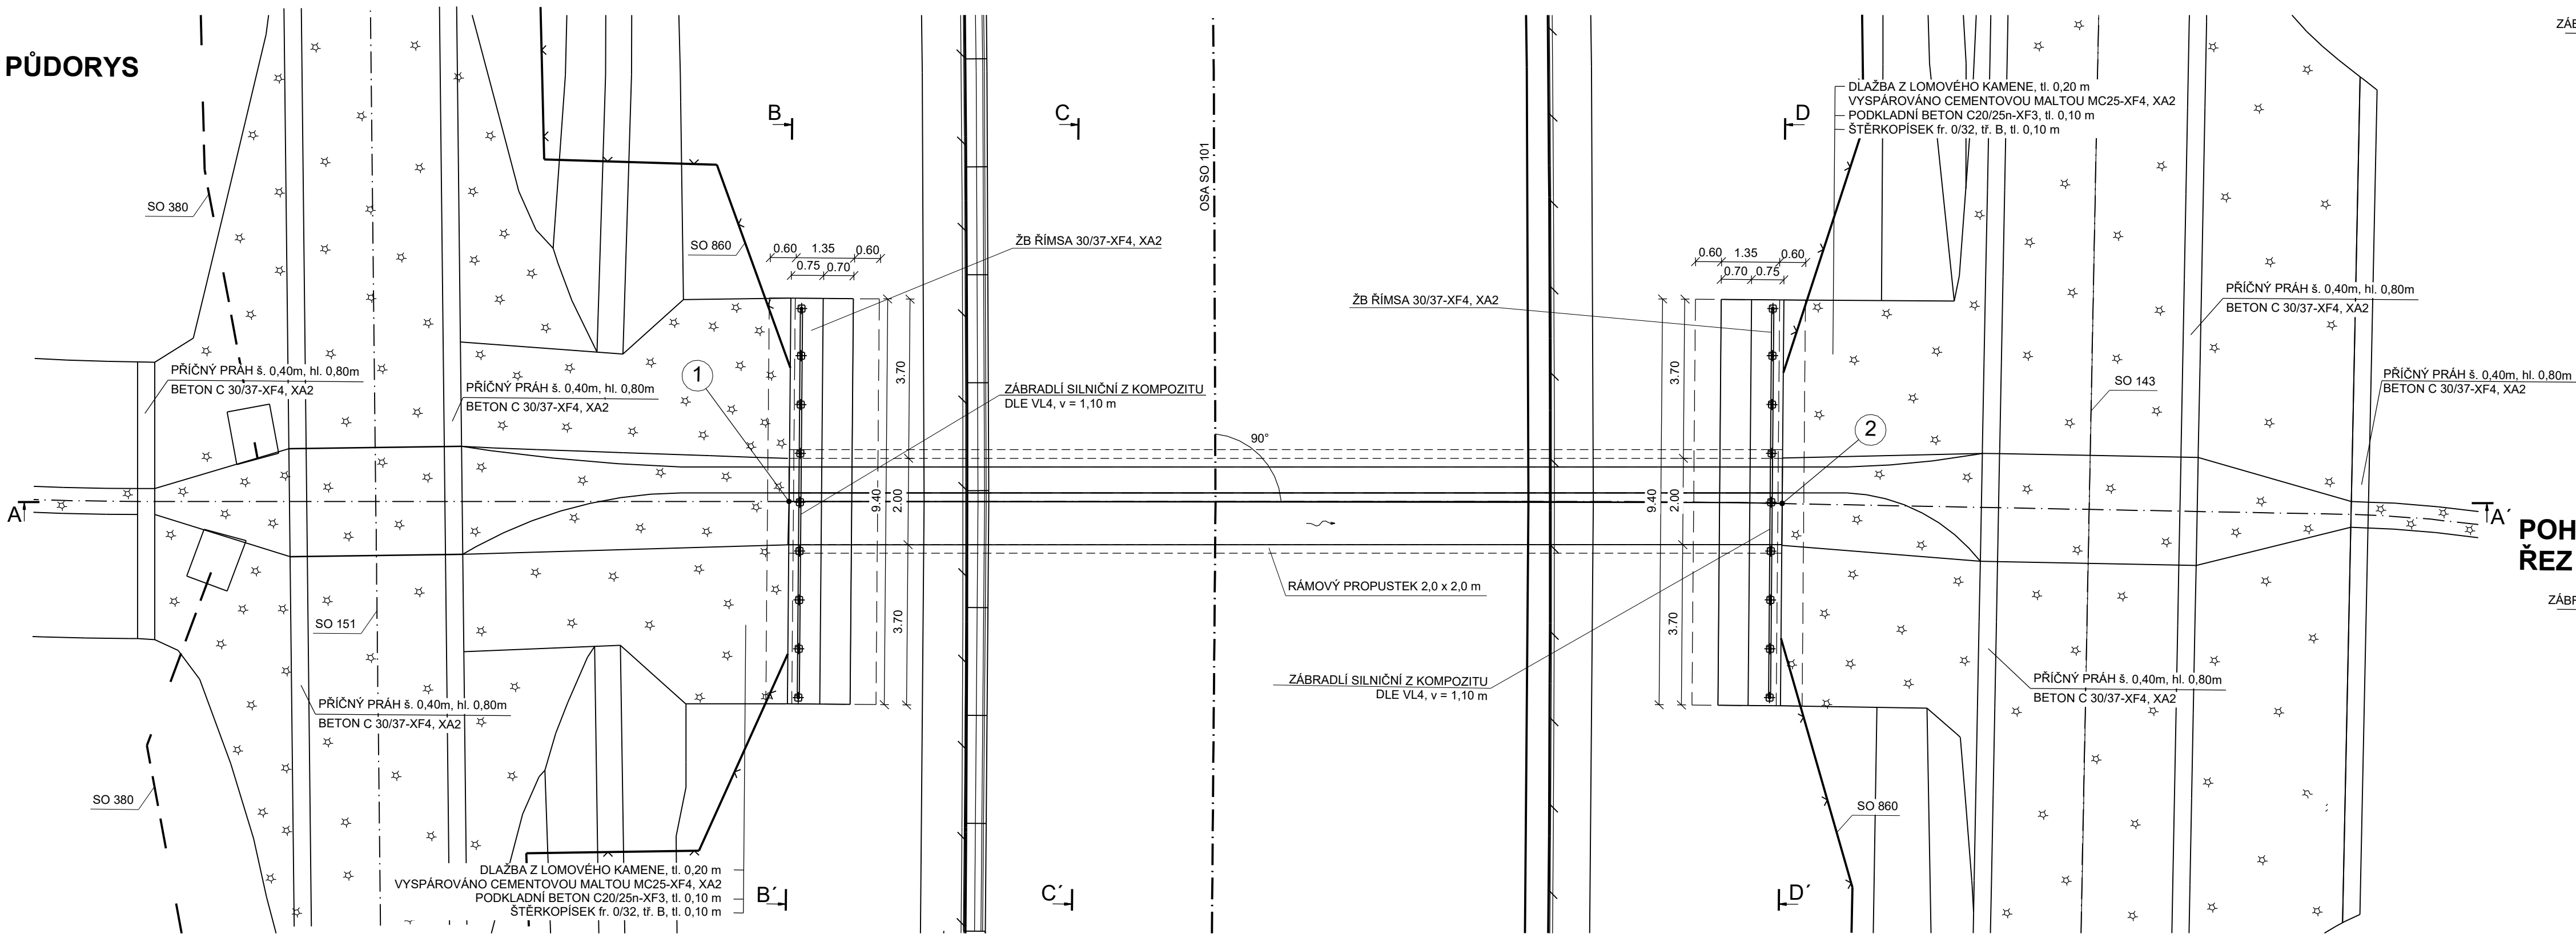

POHLED NA VÝTOK ŘEZ D-D'

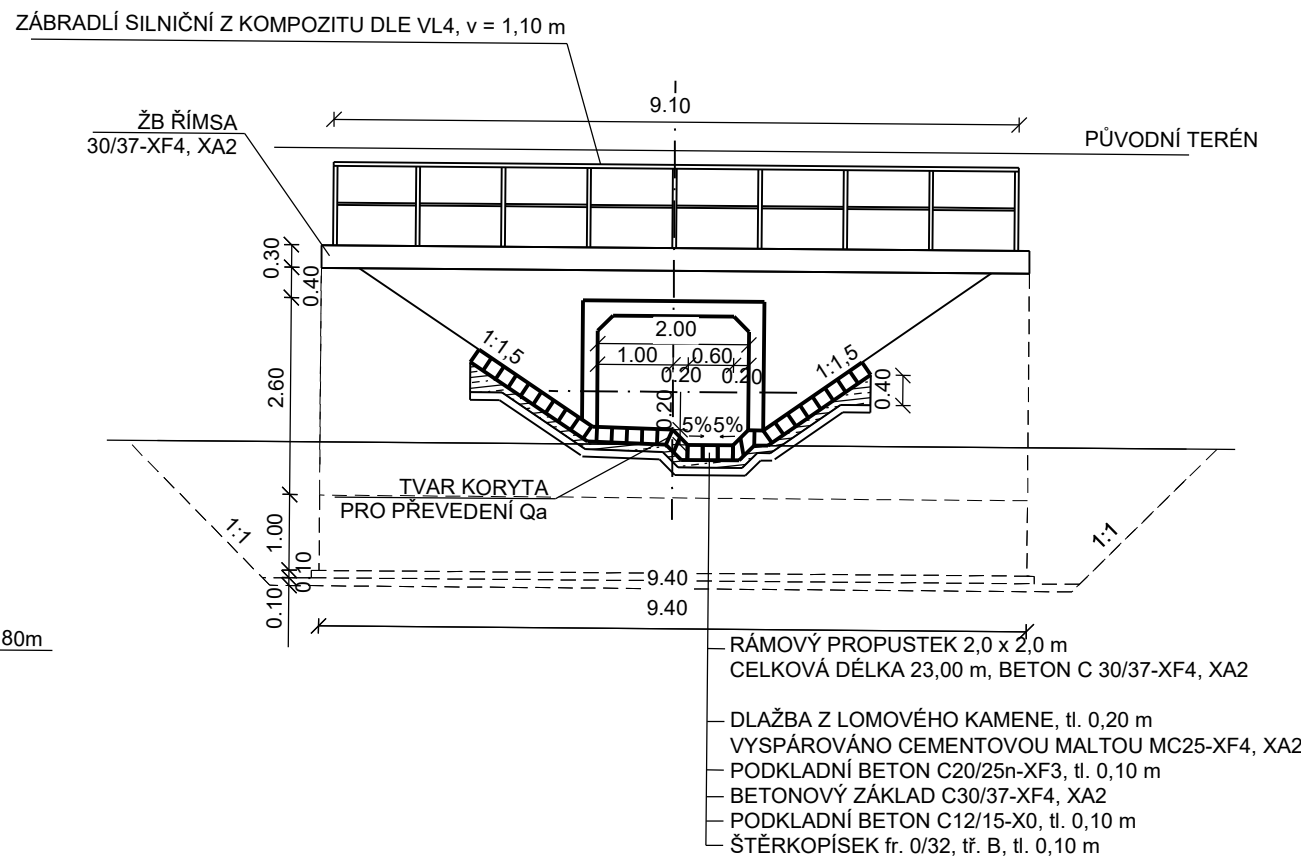


POHLED NA VTOK ŘEZ B-B'

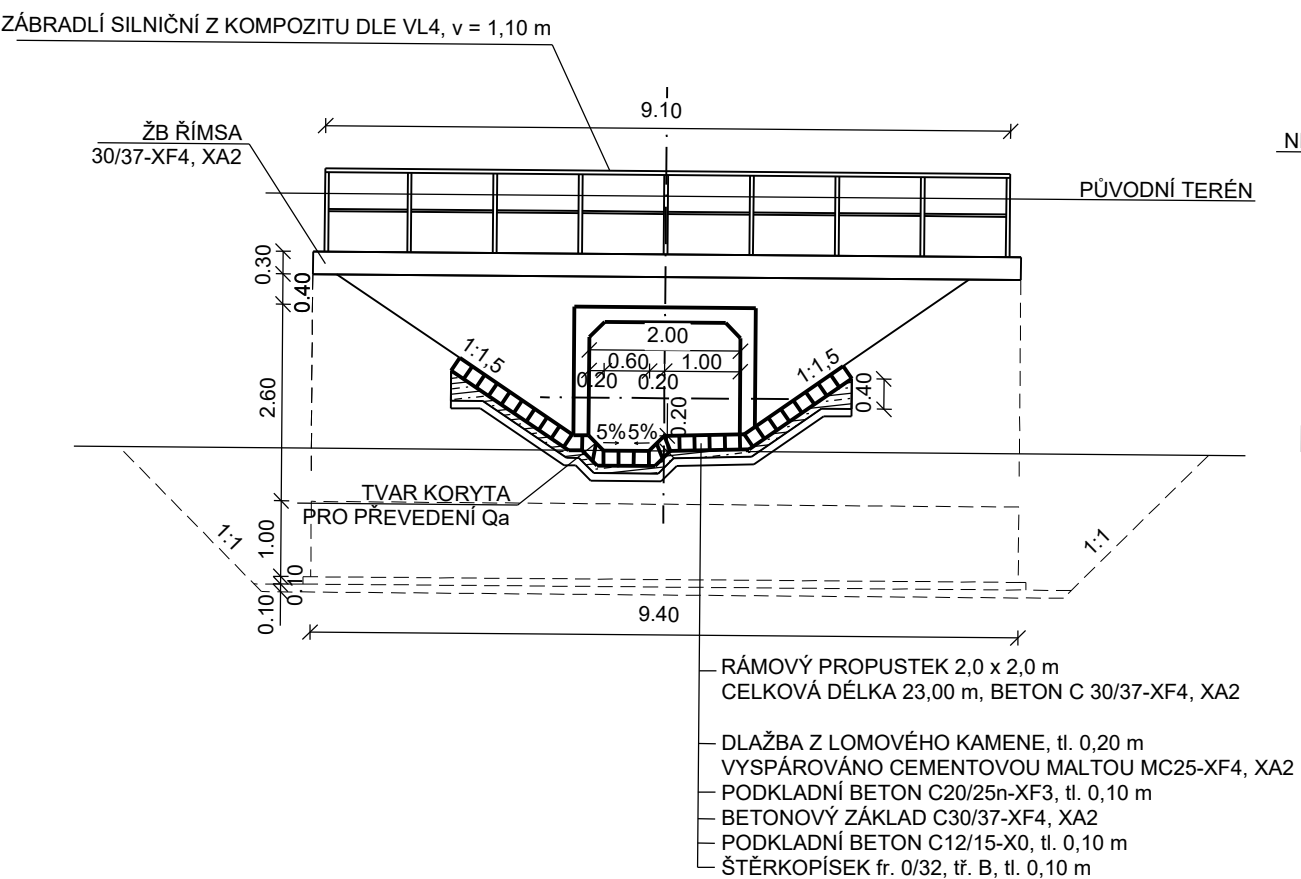


POZNÁMKA:

- SPÁROVÁNÍ DLAŽBY Z LOMOVÉHO KAMENE BUDE VYPĚNÉ CEMENTOVOU MALTOU M25 S ODOLNOSTÍ XF4, tl. min. 200 mm
- VŠECHNY BETONOVÉ PRVKY, KTERÉ PRŮJEDOU DO STŘEŠNÍ ZEMINY MUSÍ BYT OPATŘENY NATĚRY: 1x NpE A 2x NA
- VYTÝČENÍ BUDE PROVEDENO DLE TKP 1 A SOUVISEJÍCÍHO PŘEDPISU
- SKLONOV SVAHŮ JSOU URČENY SKLONEM SILNÍČNÍHO TĚLESA A PŘÍLEHLÝCH PŘÍKOPŮ
- DETAILY JSOU KOTOVÁNY V MILIMETRECH
- KORYTO BUDE VYTVAROVÁNO DO STŘEŠNÍ


DETAIL UKOTEVNÍ, M 1:10

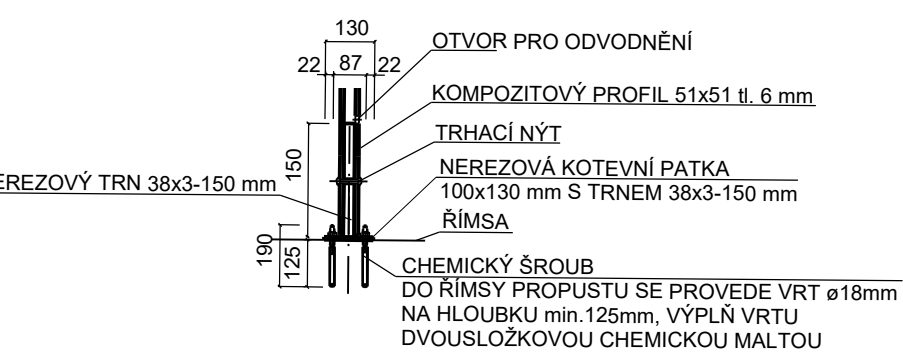


DETAIL KOTEVNÍ PATKY, M 1:10

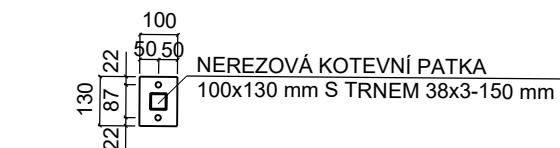

PODÉLNÝ ŘEZ A-A'

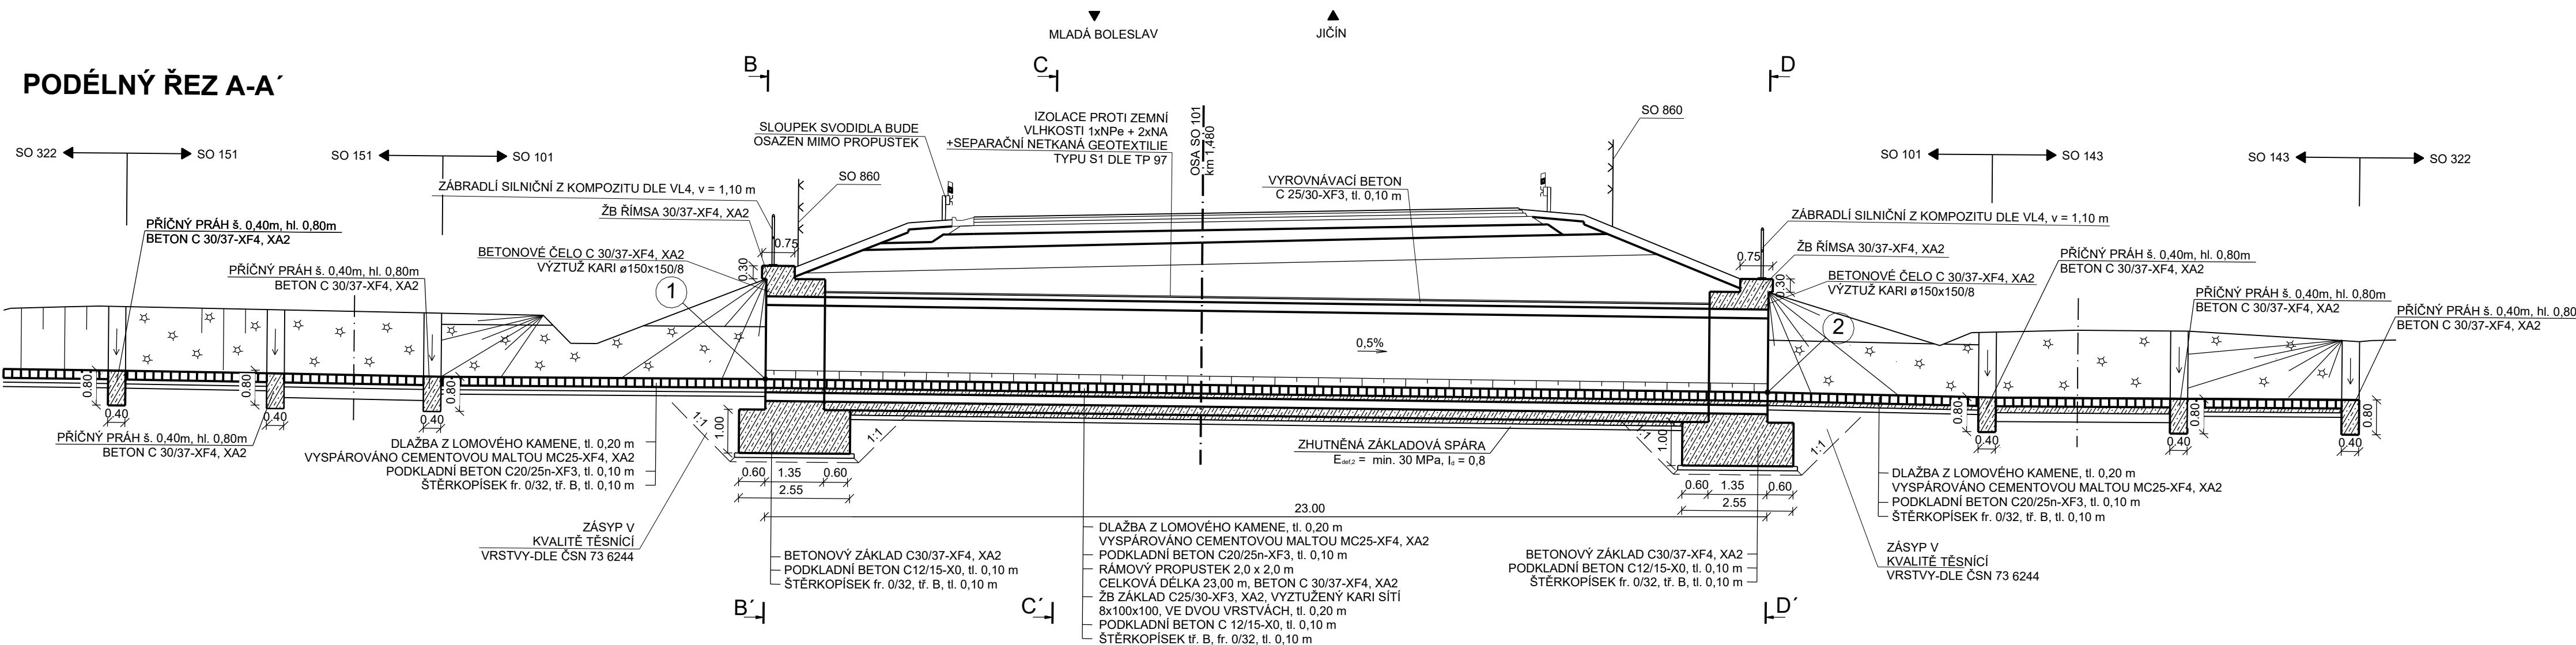

PŘÍČNÝ ŘEZ C-C'

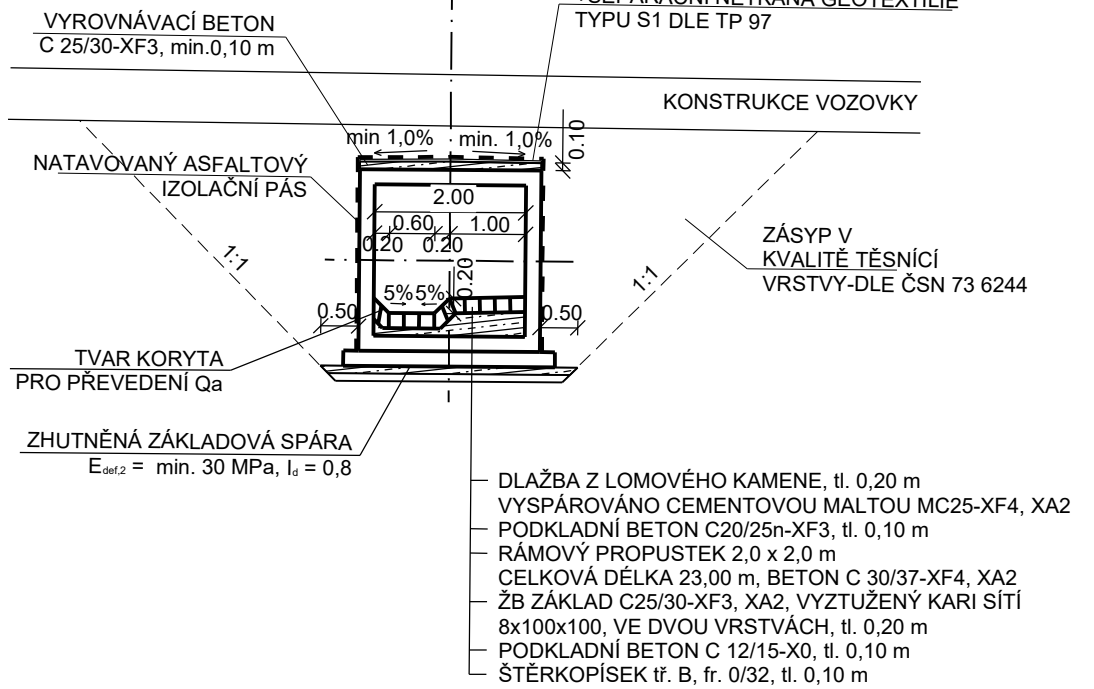

Souřadnicový systém: S-JTSK
Výškový systém: Bpv

SO 101 Silnice I/16 Mladá Boleslav - Martinovice**Objednatel:**

Ředitelství silnic a dálnic s. p.
Čerčanská 2023/12, Krč, 140 00 Praha 4

Zhotovitel:



Valbek, spol. s r.o.
Vaňurova 505/17
460 07 Liberec 3

	Vypracoval A. BARTONIČKOVÁ		Zak. číslo 21-I13-001
	Zodp. projektant ING. T. KLIMENT		Datum 02/2025
	Tech. kontrola ING. M. HANŽL		Stupeň PDPS
	Akce		Počet formátů 10 x A4
	I/16 MLADÁ BOLESLAV - MARTINOVICE		Měřítka 1 : 100
			Č. přílohy Paré
Zhotovitel: Valbek, s.r.o. s i.o. Vaňurova 505/17 460 07 Liberec 3	Příloha RÁMOVÝ PROPUSTEK 2,0 x 2,0 m V km 1,480		6.2