




SO 101 - SILNICE I/16 MLADÁ BOLESLAV - MARTINOVICE
PROPUSTEK DN 1200 V km 1,680, M 1 : 100

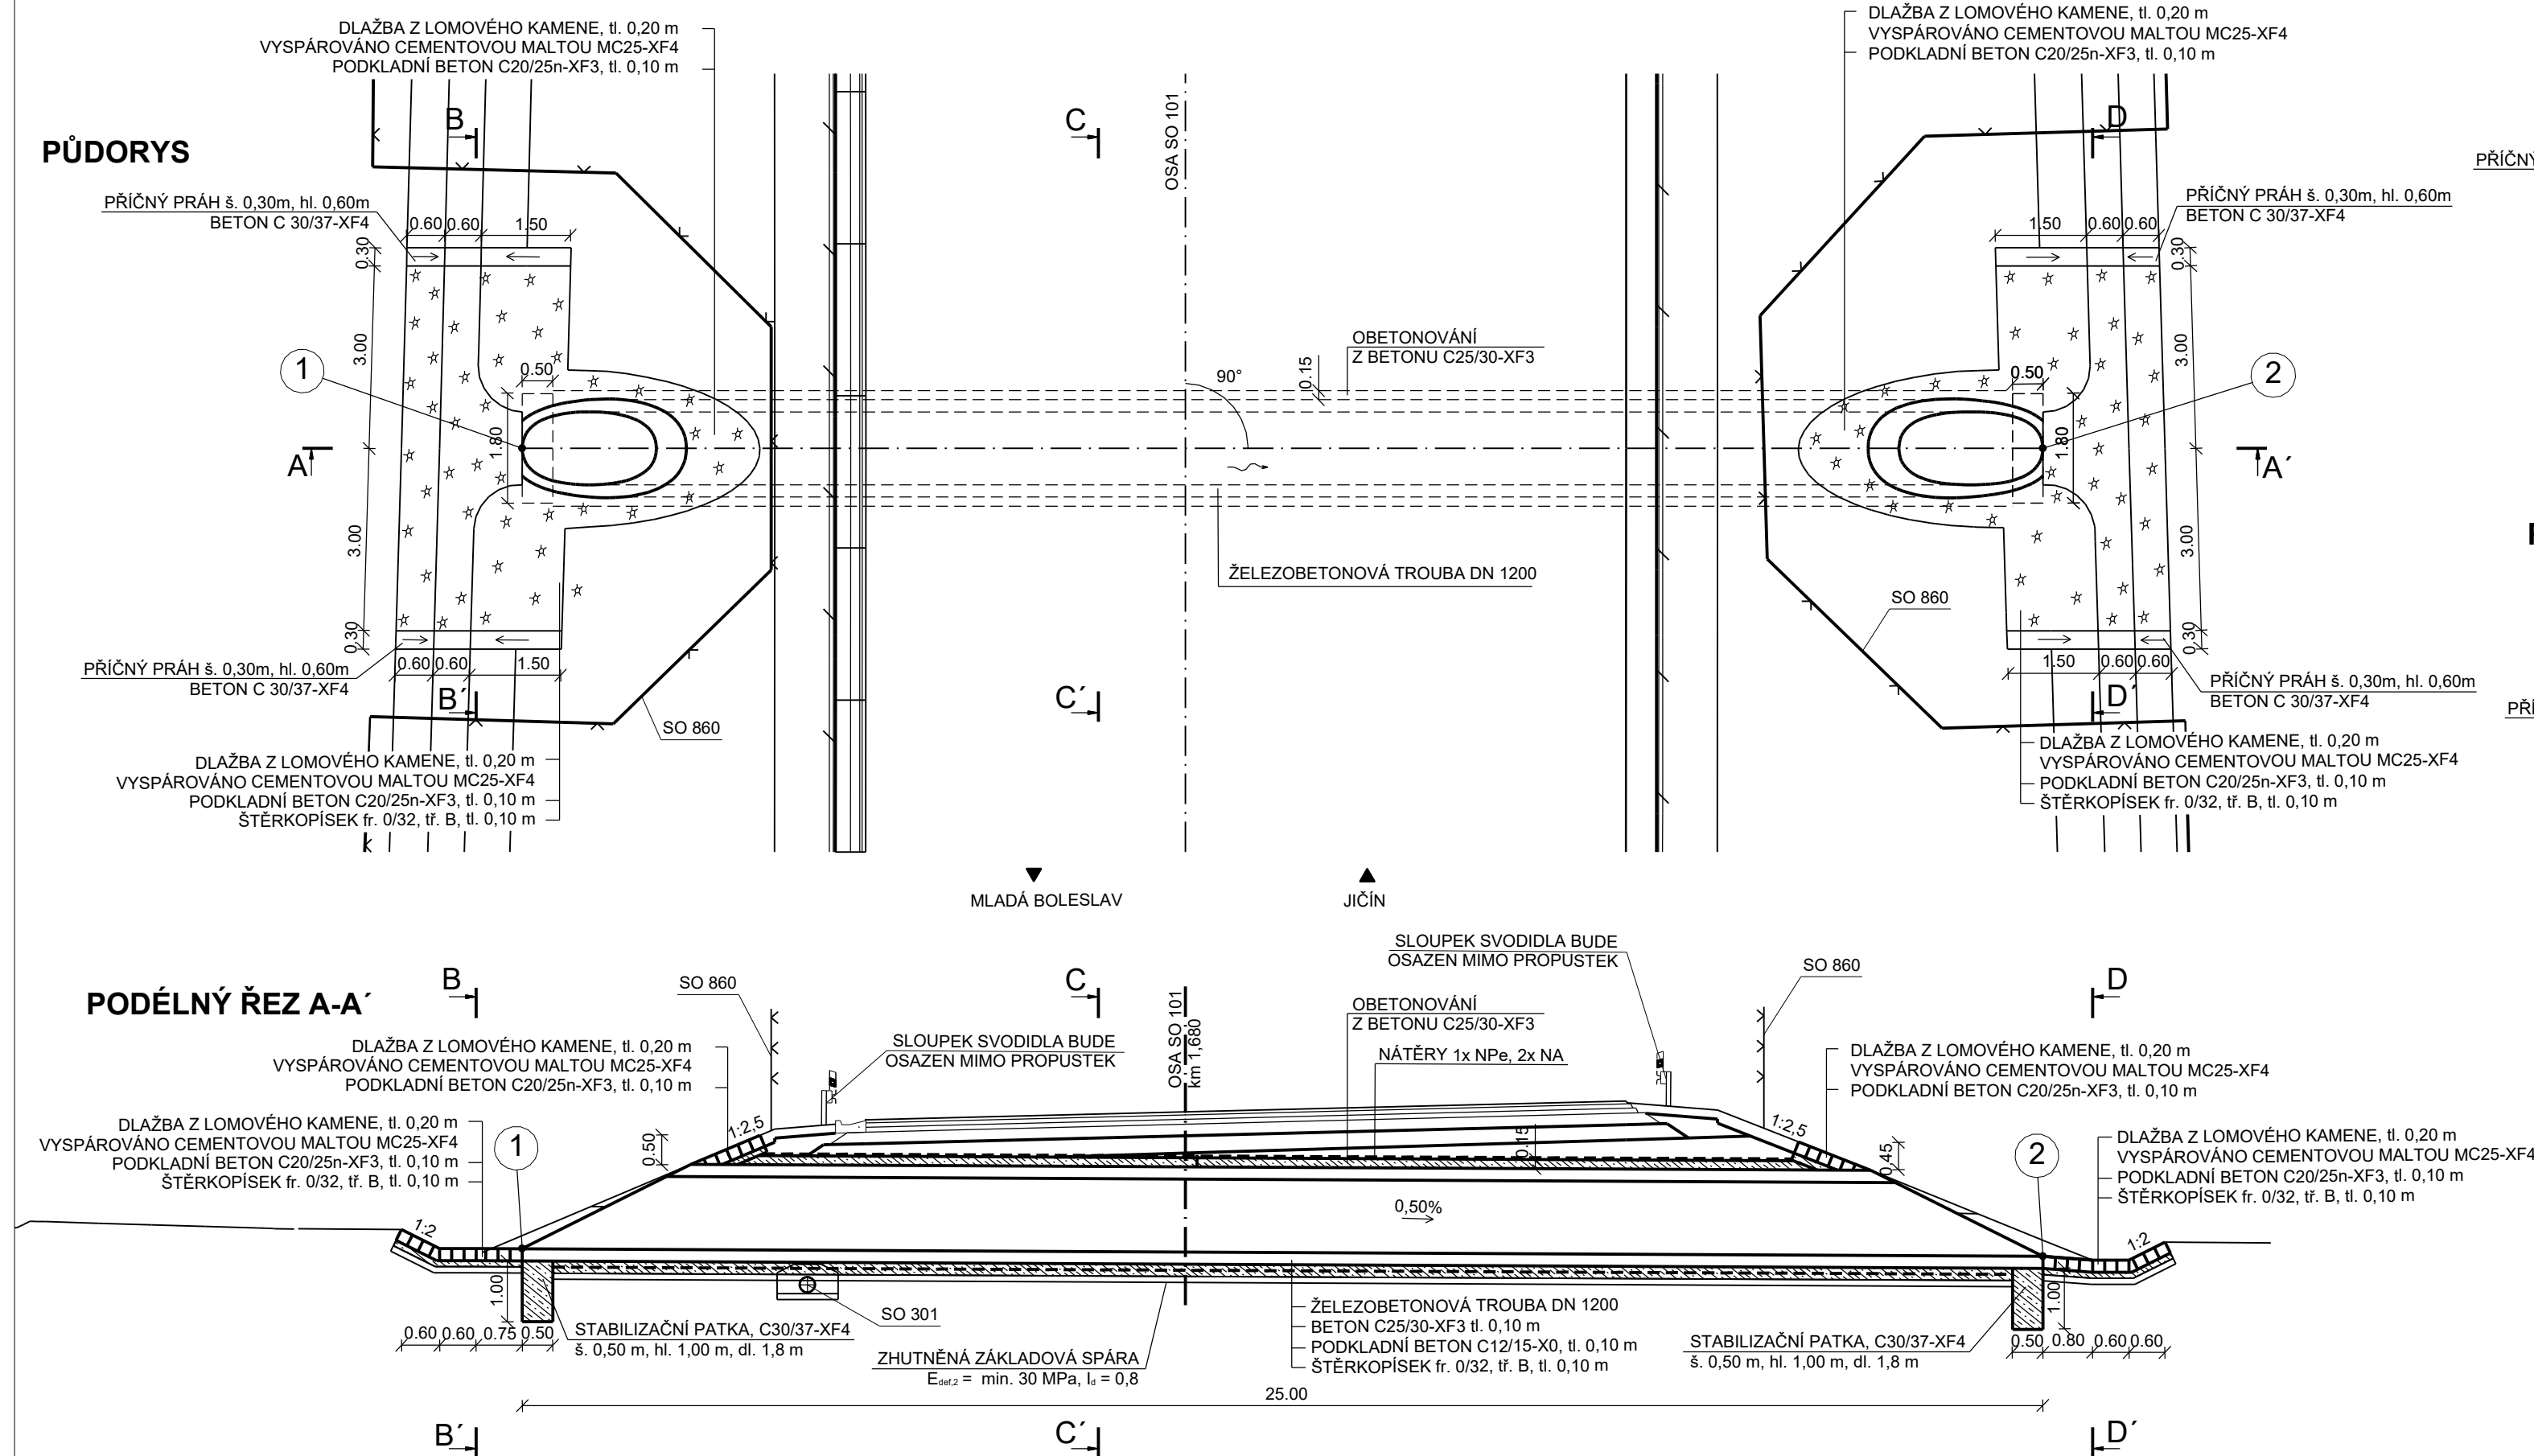


POHLED NA VТОK ŘEZ B-B

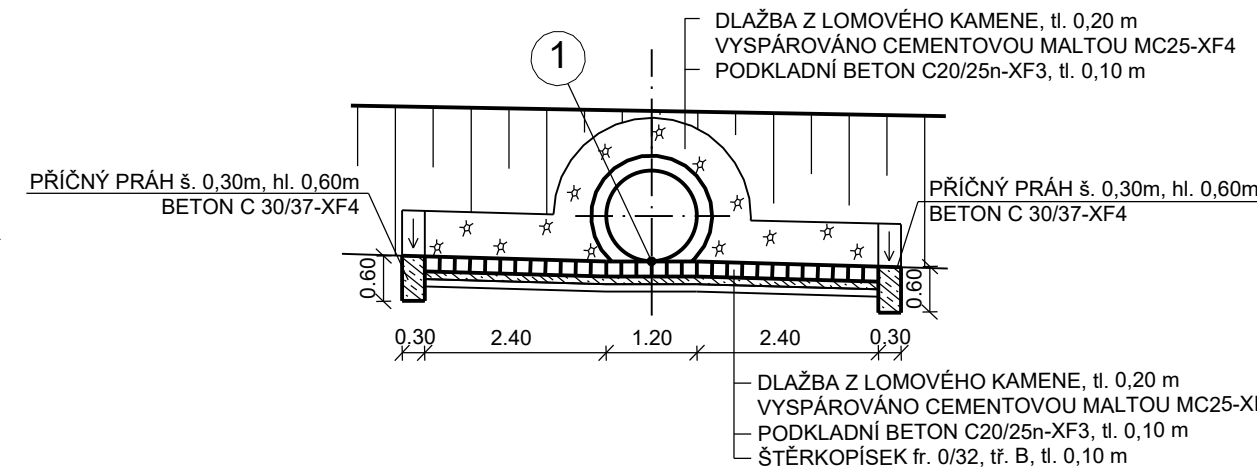

POHLED NA VÝTOK ŘEZ D-D

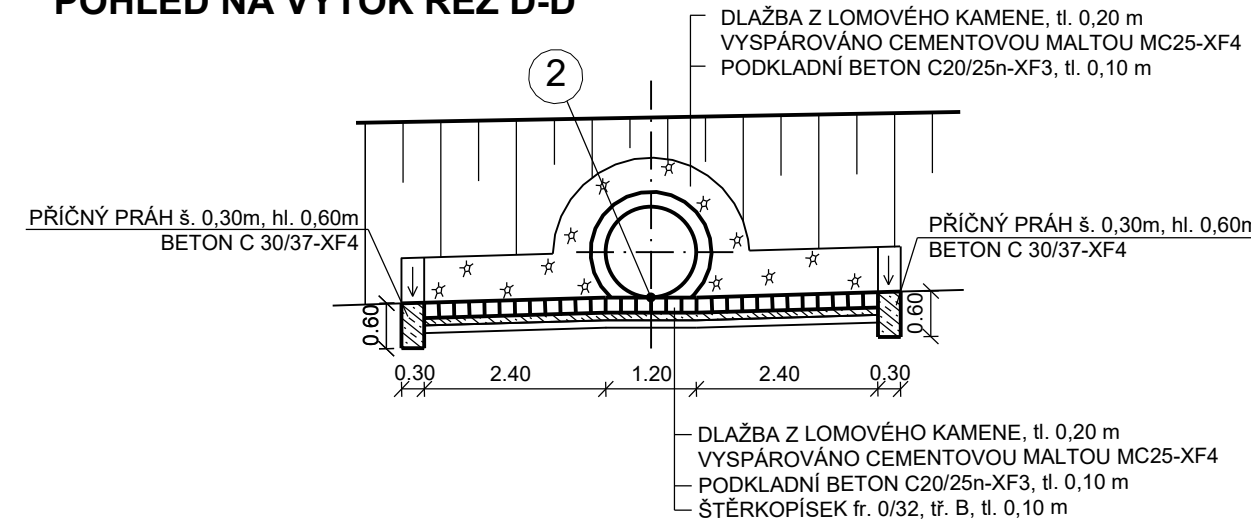

PŘÍČNÝ ŘEZ C-C

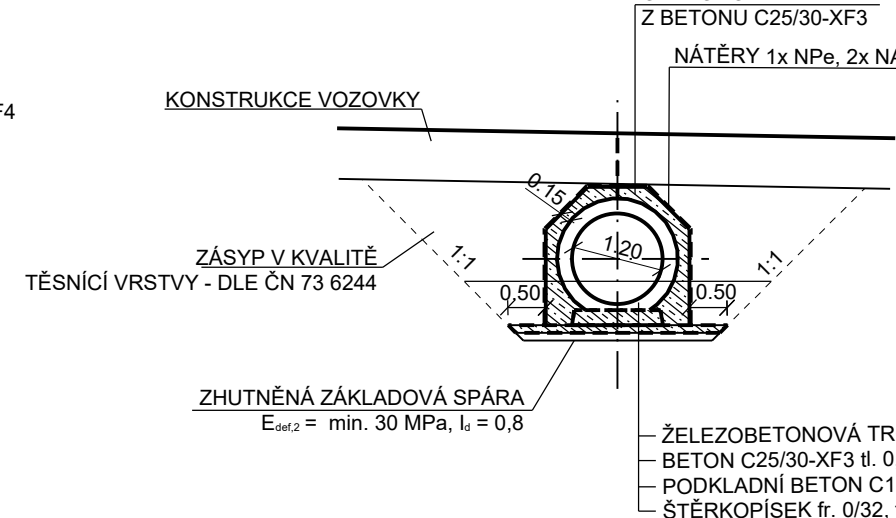

POZNÁMKY:

- SPÁROVÁNÍ DLAŽBY Z LOMOVÉHO KAMENE BUDE VYPLNĚNÉ CEMENTOVOU MALTOU MC25-XF4, tl. min. 0,20 m
- OBETNOVÁNÍ V MÍSTĚ HRDLA MINIMÁLNĚ 0,10 m
- VŠECHNY BETONOVÉ PRVKY, KTERÉ PŘÍJÍDOU DO STYKU SE ZEMINOU MUSÍ BÝT OPATŘENY NÁTĚRY: 1x NPe A 2x NA
- POČET PRAHŮ ZÁVISÍ NA TYPU ZVOLENÉ TROUBY A JEJÍHO ULOŽENÍ
- VYTÝČENÍ BUDE PROVEDENO DLE TKP 1 A SOUVISEJÍCÍCH PŘEDPISŮ
- SKLONY SVAHŮ JSOU URČENY SKLONEM SILNIČNÍHO TĚLESA A PŘÍLEHLÝCH PŘÍKOPŮ
- POKUD NEBUDOU NA KRAJÍCH OSAZENY ŠÍKMÉ PREFABRIKÁTY, BUDOU PRO SERIZNÍTOU POUŽITÝ BETONOVÉ TROUBY (Z DŮVODU KORODUJÍCÍ VÝŽUŽE)
- ŠÍŘE PODKLADNÍHO PRAHU JE 0,50 m NA KAŽDOU STRANU OD VNĚJŠÍHO OBRYSU TROUBY
- BETONOVÉ VÝROBKY VYSTAVĚNÉ PŘÍMĚMU OSTRÍKU ROZMRAZOVACÍCH PROSTŘEDKŮ A MRAZU A UMÍSTĚNÉ VE ZVÝDALENOSTI MOŽNÉHO OSTRÍKU (OD HRANY VOZOVKY 10 m VČETNĚ SOLNĚ MLHY) MUSÍ SPLŇOVAT POŽADAVKY NA STUPEŇ VLIVU PROSTŘEDÍ XF4.
- MUSÍ BÝT ZAJIŠTĚNA KOORDINACE STAVEBNÍCH PRACÍ VÝSTAVBY PROPUŠTKŮ A KANALIZACE V MÍSTĚ JEJICH KŘÍŽENÍ.

PARAMETRY PROPUSTKŮ					VÝTYČOVANÉ BODY	
STANIČENÍ [km]	TROUBA DN [mm]	DĚLKA DL [m]	SKLON S. [%]	ÚHEL α [°]	VŤOK - 01 Y / X [S-JTSK] / Z [Bpv]	VŤOK - 02 Y / X [S-JTSK] / Z [Bpv]
1,680	1200	25,00	0,50	90	699449,397/1011407,993/216,16	699452,093/1011432,847/215,98

Souřadnicový systém: S-JTSK
Výškový systém: Bpv

SO 101	Silnice I/16 Mladá Boleslav - Martinovice
Objednatel:	
	Ředitelství silnic a dálnic s. p. Čerčanská 2023/12, Krč, 140 00 Praha 4

Zhotovitel: 	Valbek, spol. s r.o. Vaňurova 505/17 460 07 Liberec 3
--	--

	Vypracoval	A. BARTONIČKOVÁ		Zak. číslo	21-L113-001
	Zodp. projektant	ING. T. KLIMENT		Datum	02/2025
	Tech. kontrola	ING. M. HANŽL		Stupeň	PDPS
	Akce I/16 MLADÁ BOLESLAV - MARTINOVCE			Počet formátů	5 x A4
Zhotovitel: Valbek, spol. s r.o. Vaňurova 505/17 460 07 Liberec 3	Příloha PROPUSTEK DN 1200 V km 1,680		Měřítko	1 : 100	Č. přílohy Paré
			6.3		