


SO 101 - SILNICE I/16 MLADÁ BOLESLAV - MARTINOVICE
PROPUSTEK DN 1200 V km 2,280, M 1 : 100

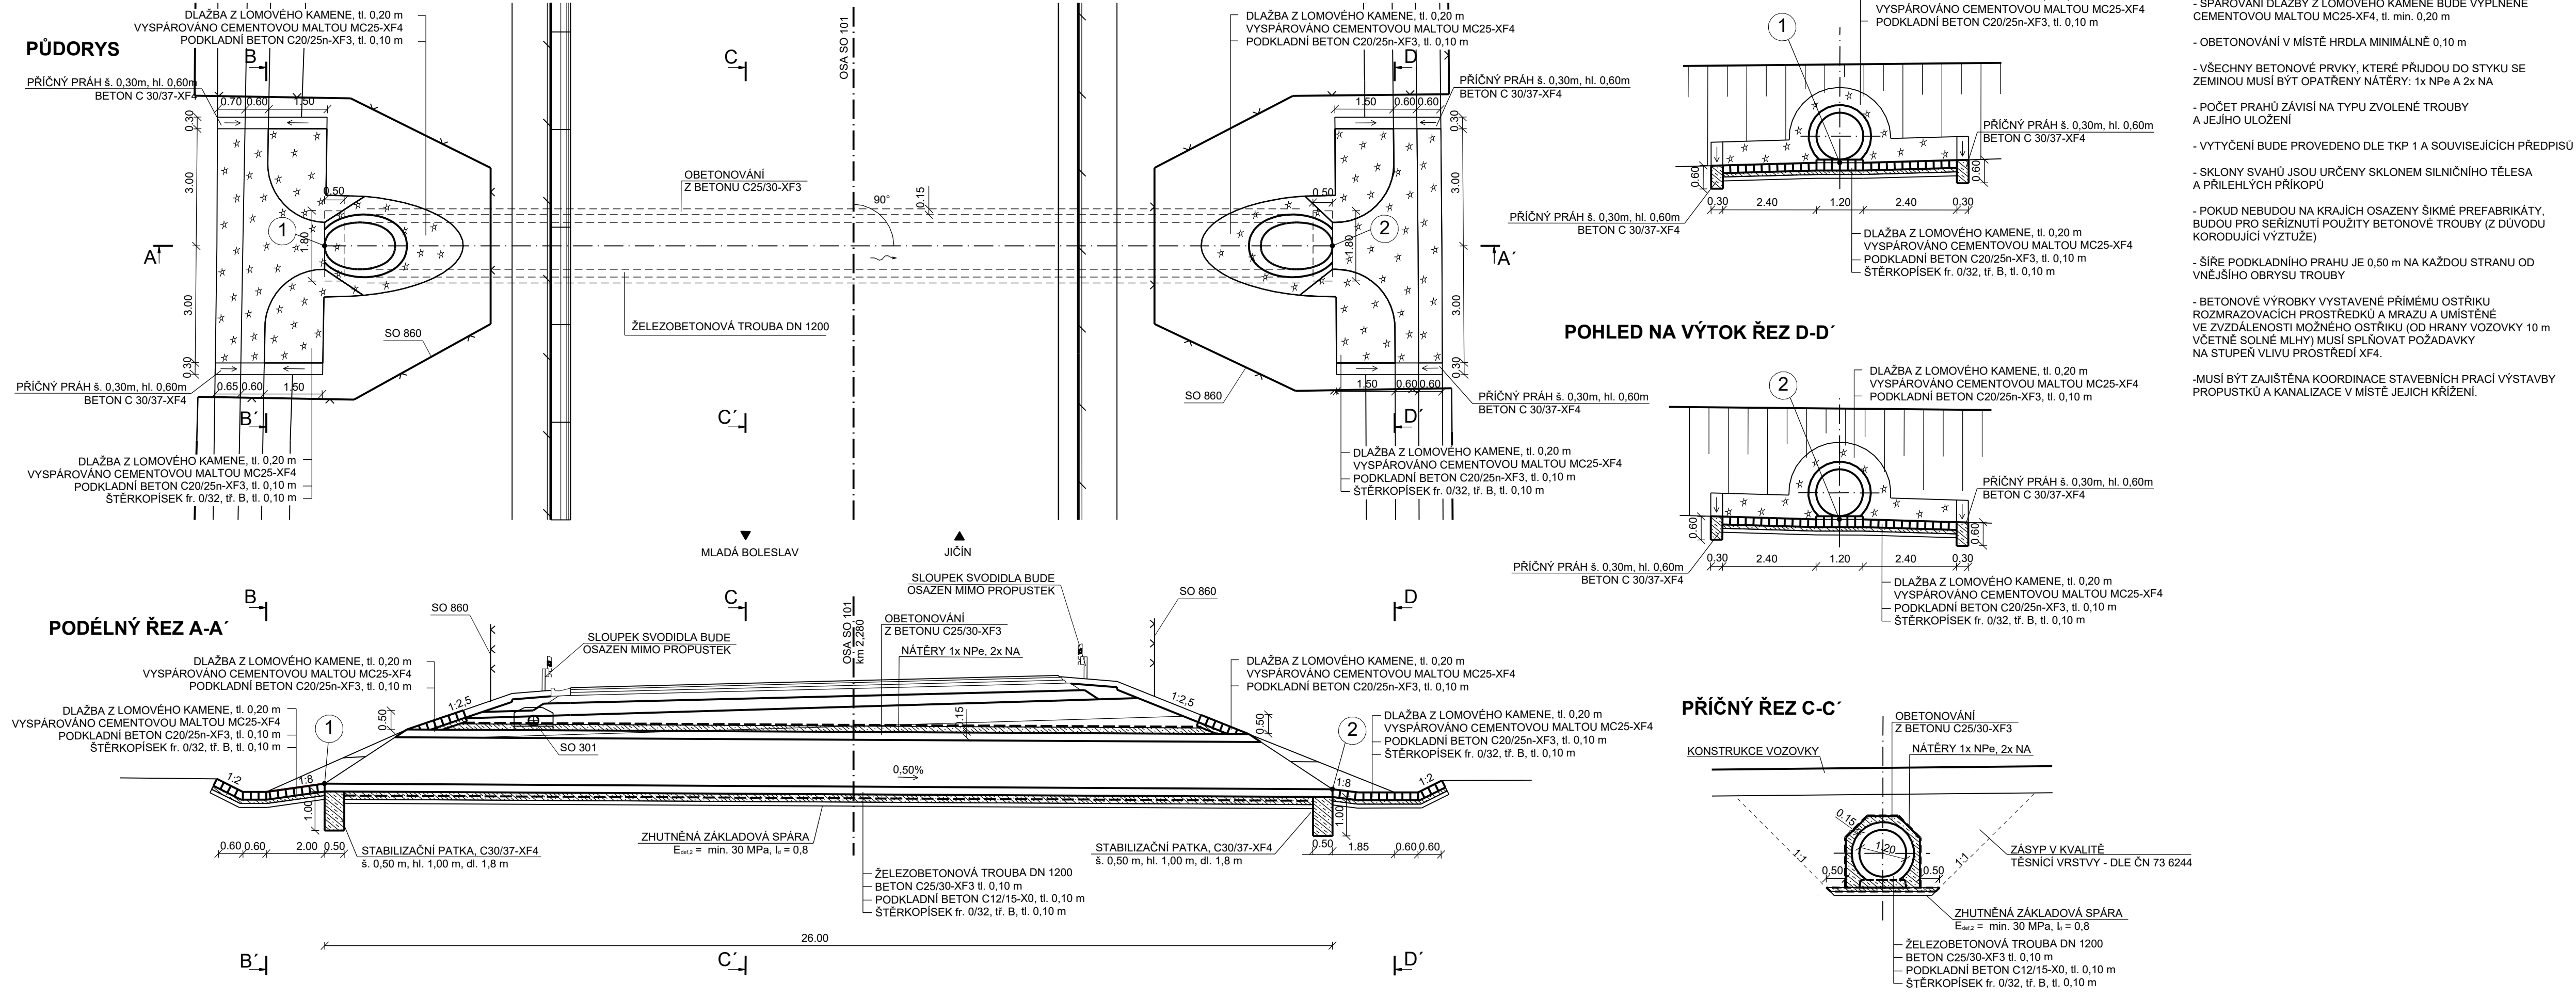

PARAMETRY PROPUSTKY					VÝTYČOVANÉ BODY	
STANIČENÍ [km]	TROUBA DN [mm]	DÉLKA DL [m]	SKLON S, [%]	ÚHEL α [°]	VTOK - 01 Y / X [S-JTSK] / Z [Bpv]	VÝTOK - 02 Y / X [S-JTSK] / Z [Bpv]
2,280	1200	26,00	0,50	90	698852,562/1011469,495/217,59	698855,322/1011495,172/217,45

Souřadnicový systém: S-JTSK
Výškový systém: Bpv

SO 101 Silnice I/16 Mladá Boleslav - Martinovice

Objednatel:

**ŘEDITELSTVÍ
SILNIC
A DÁLNIC**

Ředitelství silnic a dálnic s. p.
Čerčanská 2023/12, Krč, 140 00 Praha 4

Zhotovitel:

**Valbek**

Valbek, spol. s r.o.
Vaňurova 505/17
460 07 Liberec 3

	Vypracoval	A. BARTONIČKOVÁ		Zak. číslo	21-L113-001	
	Zodp. projektant	ING. T. KLIMENT		Datum	02/2025	
	Tech. kontrola	ING. M. HANŽL		Stupeň	PDPS	
	Akce	I/16 MLADÁ BOLESLAV - MARTINOVICE			Počet formátů	5 x A4
					Měřítko	1 : 100
Zhotovitel: Valbek, spol. s r. o. Vaňurova 505/17 460 07 Liberec 3	Příloha	PROPUSTEK DN 1200 V km 2,280			Č. přílohy	Paré
				6.4		