


SO 101 - SILNICE I/16 MLADÁ BOLESLAV - MARTINOVICE
PROPUSTEK DN 1200 V km 3,490, M 1 : 100

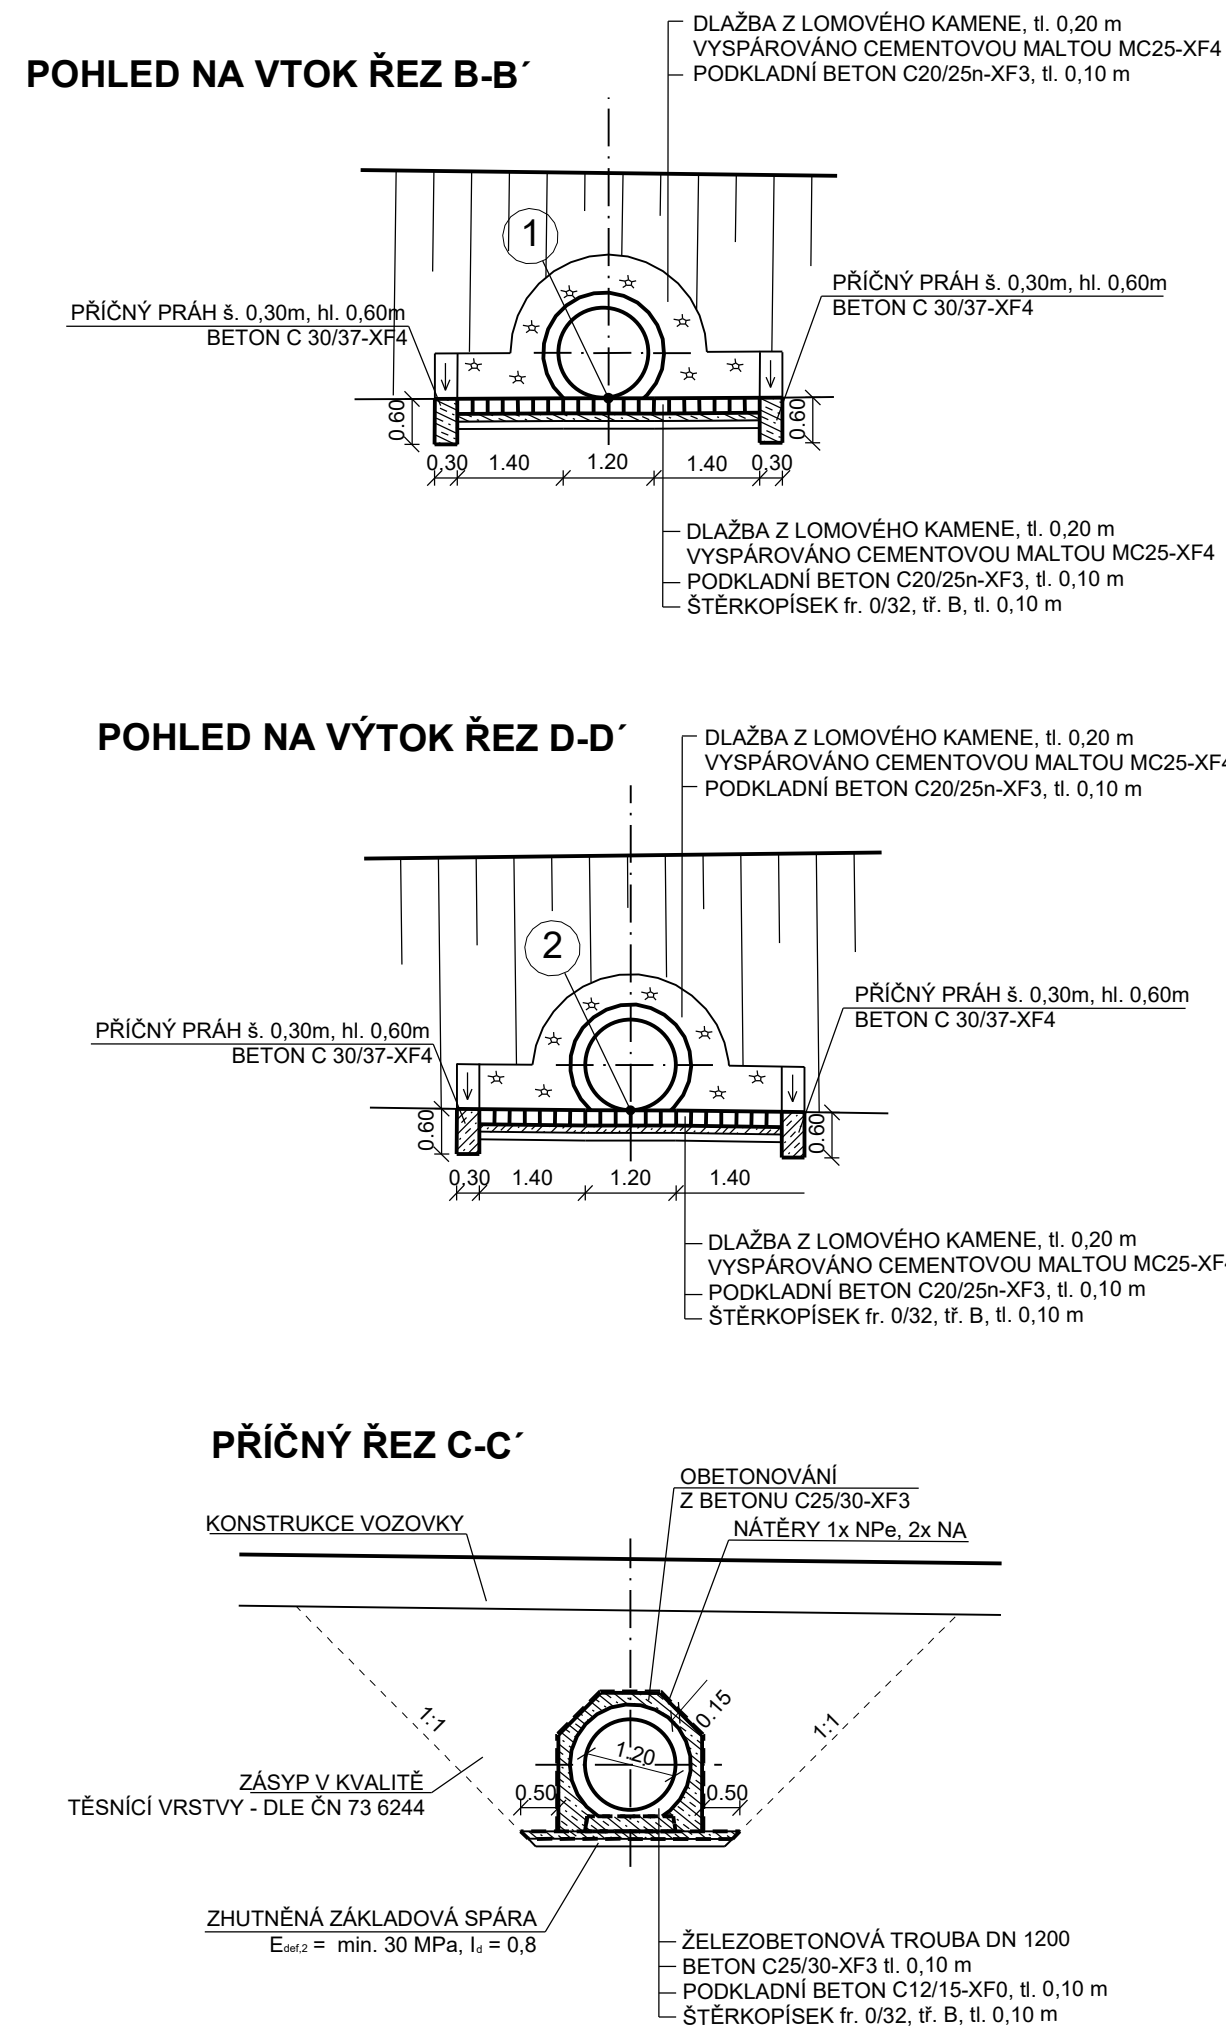

POZNÁMKY:

- SPÁROVÁNÍ DLAŽBY Z LOMOVÉHO KAMENE BUDE VYPLNĚNO CEMENTOVOU MALTOU MC25-XF4, tl. min. 0,20 m
- OBETNOVÁNÍ V MÍSTĚ HRDLA MINIMÁLNĚ 0,10 m
- VŠECHNY BETONOVÉ PRVKY, KTERÉ PŘIJDOU DO STYKU SE ZEMINOU MUSÍ BÝT OPATŘENY NÁTĚRY: 1x NpE a 2x NA
- POČET PRAHŮ ZÁVISÍ NA TYPU ZVOLENÉ TROUBY A JEJÍHO ULOŽENÍ
- VYTČENÍ BUDE PROVEDENO DLE TKP 1 A SOUVISEJÍCÍCH PŘEDPISŮ
- SKLONY SVAHŮ JSOU URČENY SKLONEM SILNIČNÍHO TĚLESA A PŘÍLEHLÝCH PŘÍKOPŮ
- POKUD NEBUDOU NA KRAJÍCH OSAZENY ŠIKMÉ PREFABRIKÁTY, BUDOU PRO SEŘÍZNUTÍ POUŽITY BETONOVÉ TROUBY (Z DŮVODU KORODUJÍCÍ VYTŽEŽE)
- ŠÍŘE PODKLADNÍHO PRAHU JE 0,50 m NA KAŽDOU STRANU OD VNĚJŠÍHO OBRYSU TROUBY
- BETONOVÉ VÝROBKY VYSTAVĚNÉ PŘÍMÉMU OŠTRÍKU, ROMRÁZOVACÍCH PROSTŘEDKŮ A MRAZU A UMÍSTĚNÉ VE ZVÝDALENOSTI MOŽNÉHO OŠTRÍKU (OD HRANY VOZOVKY 10 m VČETNĚ SOLNÉ MLHY) MUSÍ SPLŇOVAT POŽADAVKY NA STUPEŇ VLIVU PROSTŘEDÍ XF4.
- MUSÍ BÝT ZAJIŠTĚNA KOORDINACE STAVEBNÍCH PRACÍ VÝSTAVBY PROPUŠTKŮ A KANALIZACE V MÍSTĚ JEJICH KŘÍŽENÍ.

PARAMETRY PROPUSTKŮ					VYTÝČOVANÉ BODY	
STANICENÍ [km]	TROUBA DN [mm]	DĚLKA DL [m]	SKLON S. [%]	ÚHEL α [°]	VTKO - 01 Y / X [S-JTSK] / Z [Bpv]	VYTOK - 02 Y / X [S-JTSK] / Z [Bpv]
3,490	1200	28,50	0,50	90	697719,848/1011857,092/221,30	697729,513/1011884,313/221,15

Souřadnicový systém: S-JTSK
Výškový systém: Bpv

SO 101 Silnice I/16 Mladá Boleslav - Martinovice	
Objednatel:	 ŘEDITELSTVÍ SILNIC A DÁLNIC Ředitelství silnic a dálnic s. p. Čerčanská 2023/12, Krč, 140 00 Praha 4

Zhotovitel: 	Valbek, spol. s r.o. Vaňurova 505/17 460 07 Liberec 3
--	---

	Vypracoval	A. BARTONÍČKOVÁ	Zak. číslo	21-L113-001
	Zodp. projektant	ING. T. KLIMENT	Datum	02/2025
	Tech. kontrola	ING. M. HANŽL	Stupeň	PDPS
	Akce	Počet formátů		5 x A4
I/16 MLADÁ BOLESLAV - MARTINOVICE	PROPUSTEK DN 1200 V km 3,490		Měřítko	1 : 100
			Č. přílohy	Paré
Zhotovitel: Valbek, spol. s r.o. Vaňurova 505/17 460 07 Liberec 3	Příloha		6.7	