
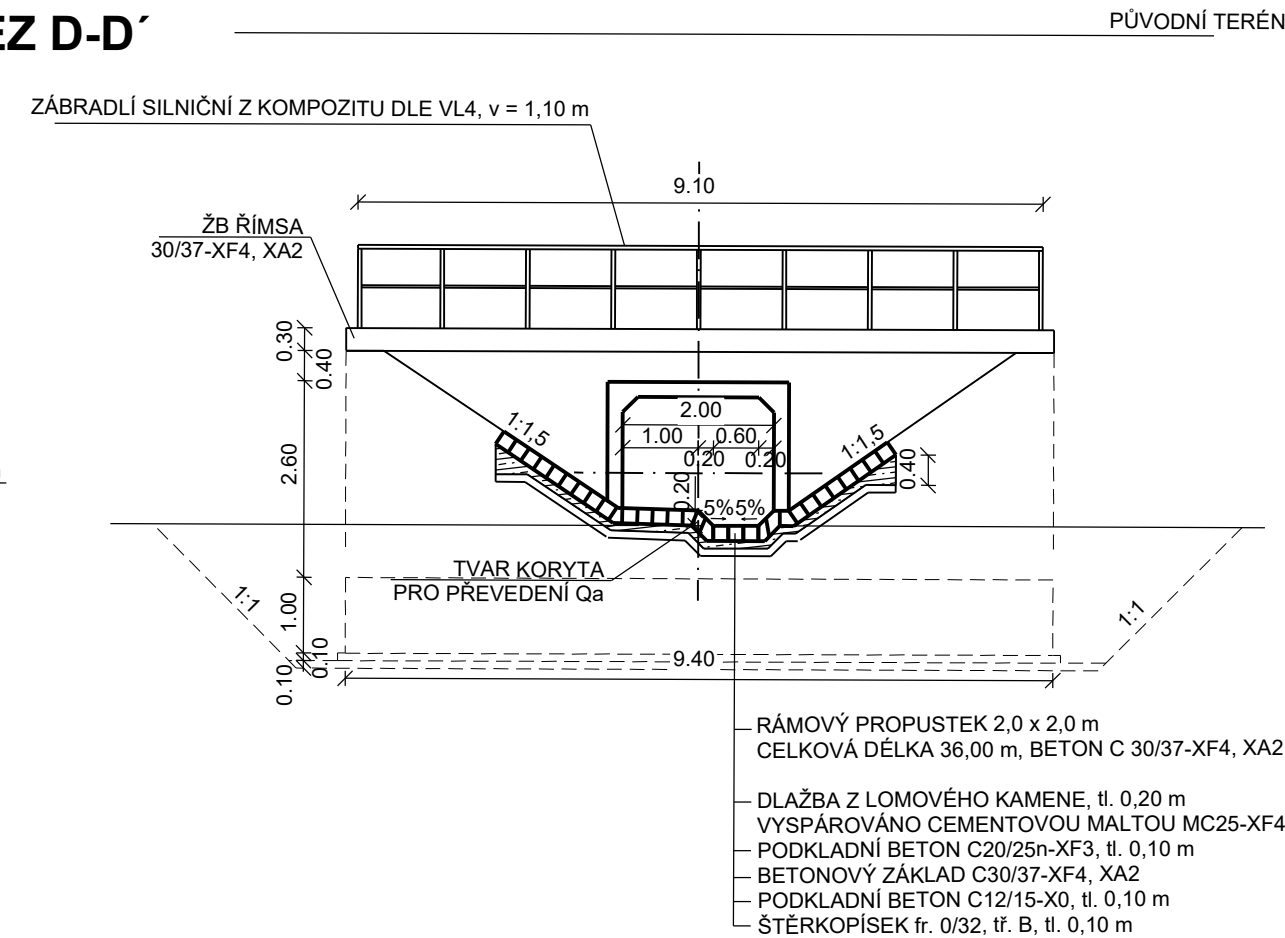


SO 101 - SILNICE I/16 MLADÁ BOLESLAV - MARTINOVICE
RÁMOVÝ PROPUSTEK 2,0 x 2,0 m V km 3,910, M 1 : 100

PARAMETRY PROPUSTKŮ					VYTÝČOVANÉ BODY	
STANČENÍ [km]	DN [m]	DĚLKA DL [m]	SKLON S _i [%]	ÚHEL α [°]	VTOK - 01 Y / X [S-JTSK] / Z [Bpv]	VTÓK - 02 Y / X [S-JTSK] / Z [Bpv]
3,910	2 x 2	36,00	0,75	90	697312,874/1011919,347/218,21	697312,622/1011955,347/217,194

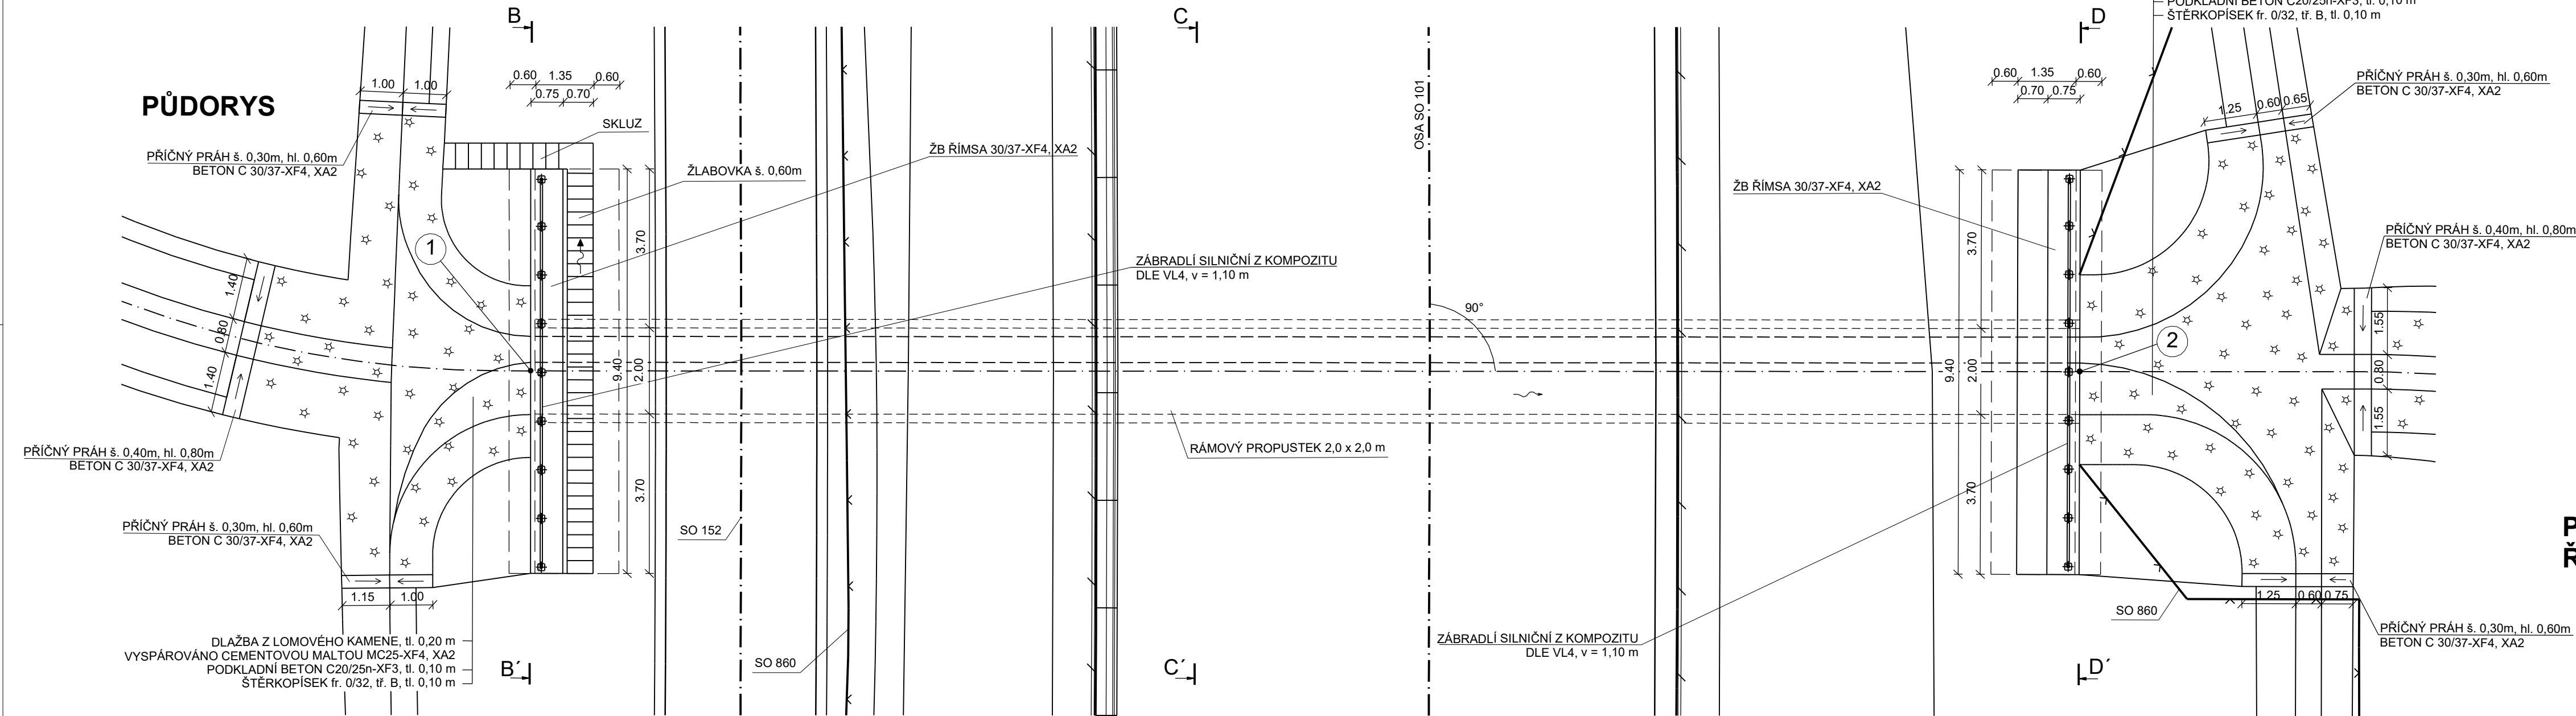

POZNÁMKA:

- SPÁROVÁNÍ DLAŽBY Z LOMOVÉHO KAMENE BUDE VYPLNĚNÉ CEMENTOVOU MALTOU M25 S ODOLNOSTÍ XF4, tl. min. 200 mm

- VŠECHNY BETONOVÉ PRVKY, KTERÉ PŘIJDOU DO STYKU SE ZEMINOU MUSÍ BÝT OPATŘENY NÁTĚRY: 1x NPe A 2x NA


- VYTYČENÍ BUDE PROVEDENO
1 A SOUVISEJÍCÍCH PŘEDPISŮ

-SKLONY SVAHŮ JSOU URČENY SKLONEM
SILNIČNÍHO TĚLESA A PŘILEHLÝCH PŘÍKOPŮ


-DETAILY JSOU KÓTOVÁNY V MILIMETRECH

-KORYTO BUDE VYTVAROVÁNO DO STŘELKY




-MUSÍ BÝT ZAJIŠTĚNA KOORDINACE STAVEBNÍCH PRACÍ VÝSTAVBY
PROPUSTKŮ A KANALIZACE V MÍSTĚ JEJICH KŘÍŽENÍ.

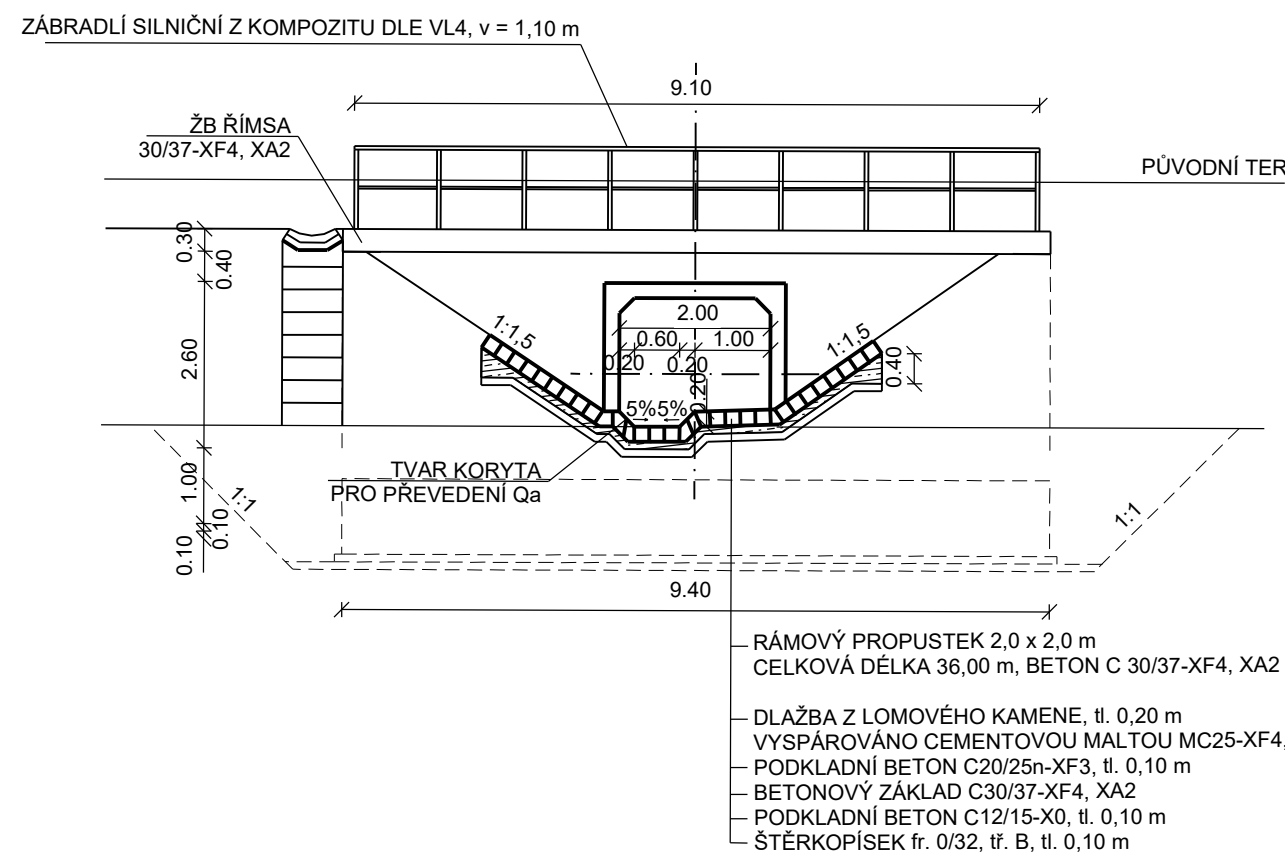

DETAIL UKOTEVNÍ, M 1:10

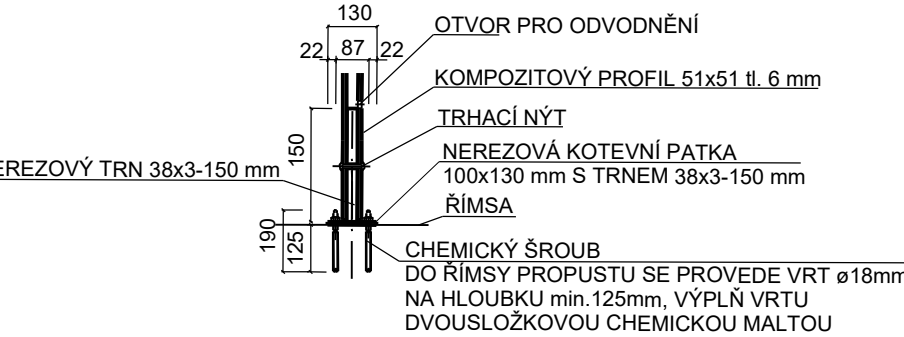

DETAIL KOTEVNÍ PATKY, M 1:10

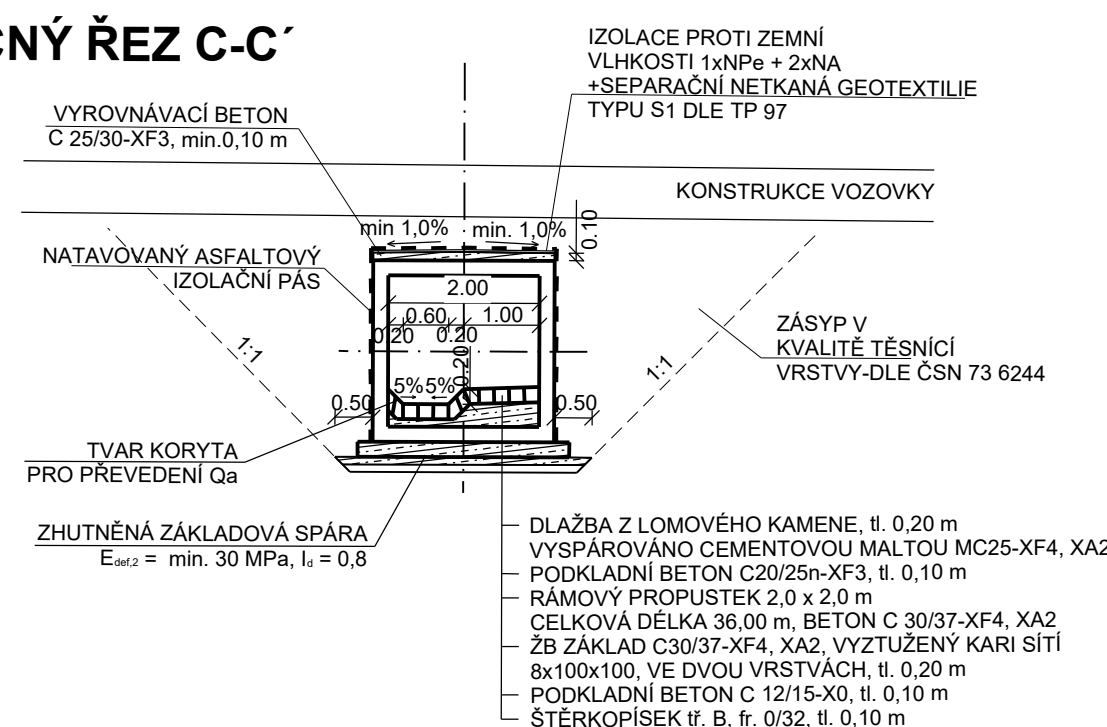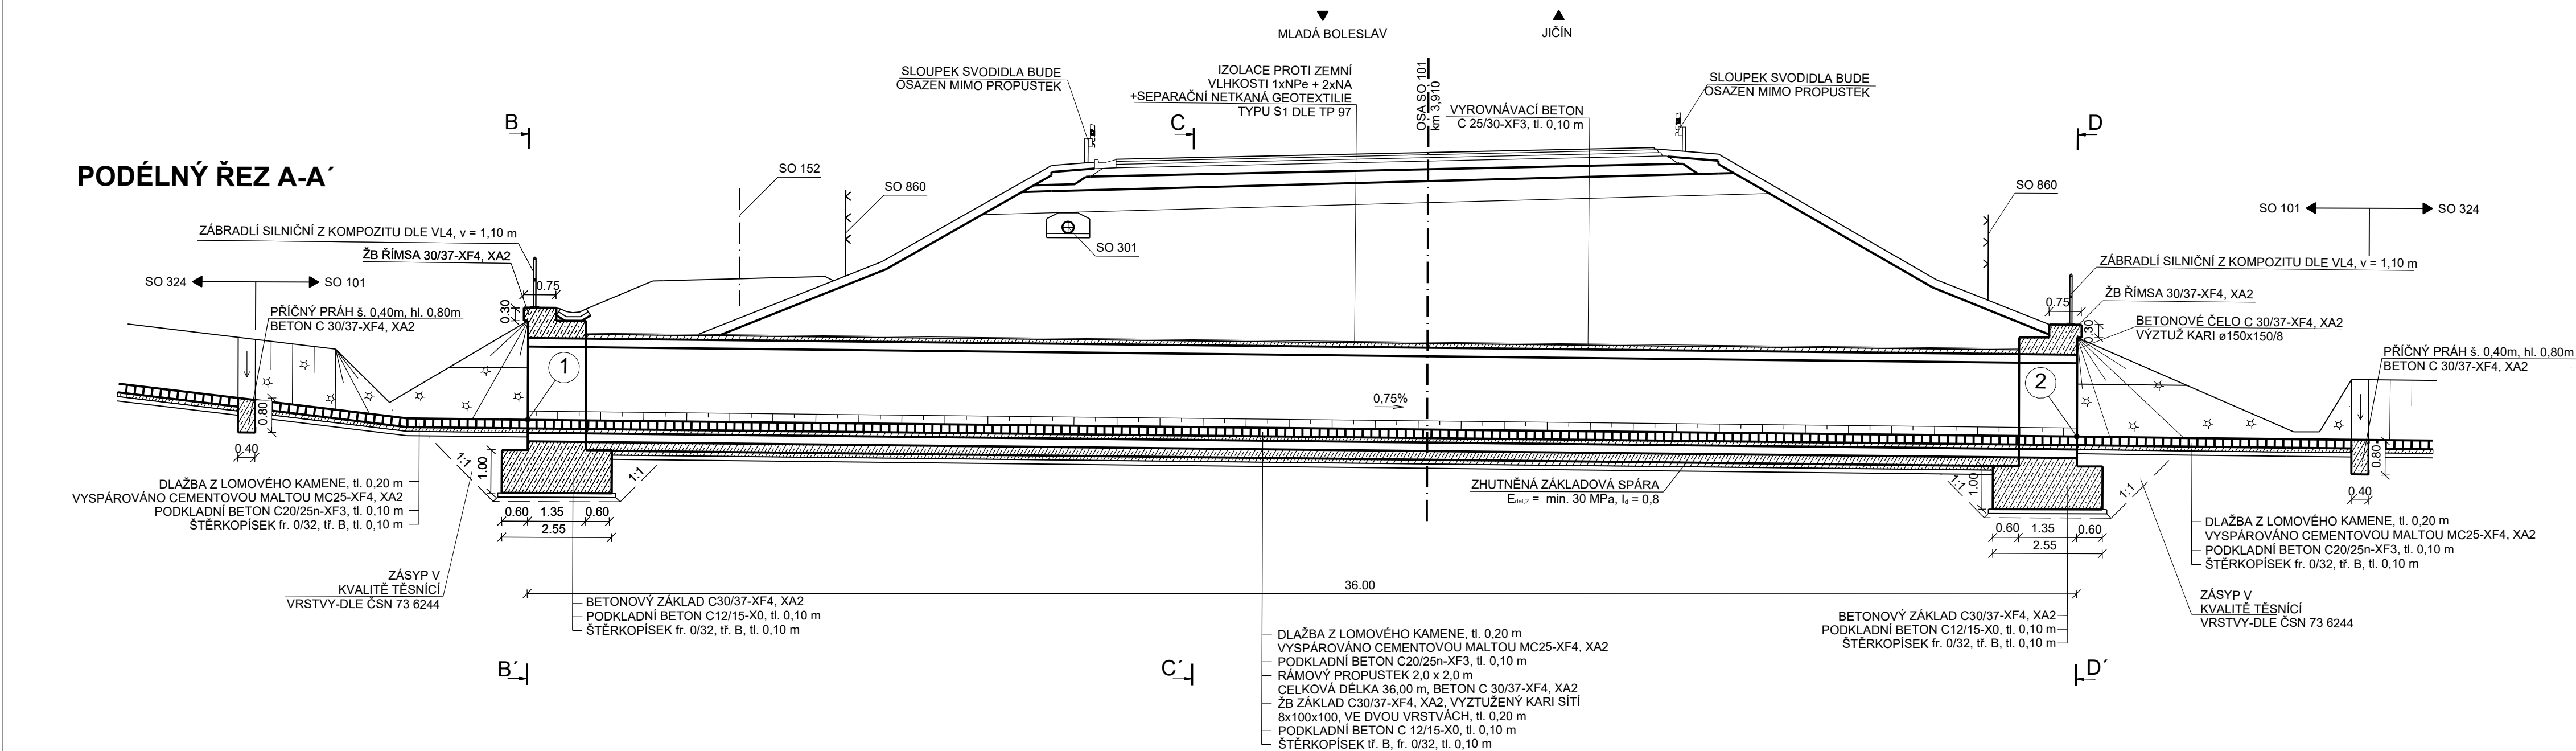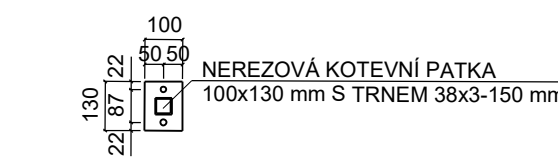

Souřadnicový systém: S-JTSK
Výškový systém: Bpv

SO 101 Silnice I/16 Mladá Boleslav - Martinovice

Objednatel: **ŘEDITELSTVÍ
SILNIC
A DÁLNIC**

Ředitelství silnic a dálnic s. p.
Čerčanská 2023/12, Krč, 140 00 Praha 4

Zhotovitel: 	Valbek, spol. s r.o. Vaňurova 505/17 460 07 Liberec 3
--	--

	Vypracoval	A. BARTONIČKOVÁ	Zak. číslo	21-LH3-001
	Zodp. projektant	ING. T. KLIMENT	Datum	02/2025
	Tech. kontrola	ING. M. HANŽL	Stupeň	PDPDS
	Akte	I/16 MLADÁ BOLESLAV - MARTINOVICE		Počet formátů
	Měřítko			1 : 100
	Č. přílohy			Paré
Zhotovitel: Valbek, spol. s r.o. Valbersko 550/17 460 07 Liberec 3	Příloha RÁMOVÝ PROUSTEK 2,0 x 2,0 m V km 3,910	6.8		