



SO 101 SILNICE I/16 MLADÁ BOLESLAV - MARTINOVICE
PROPUSTEK DN 1200 V km 4,410, M 1 : 100


PŮDORYS

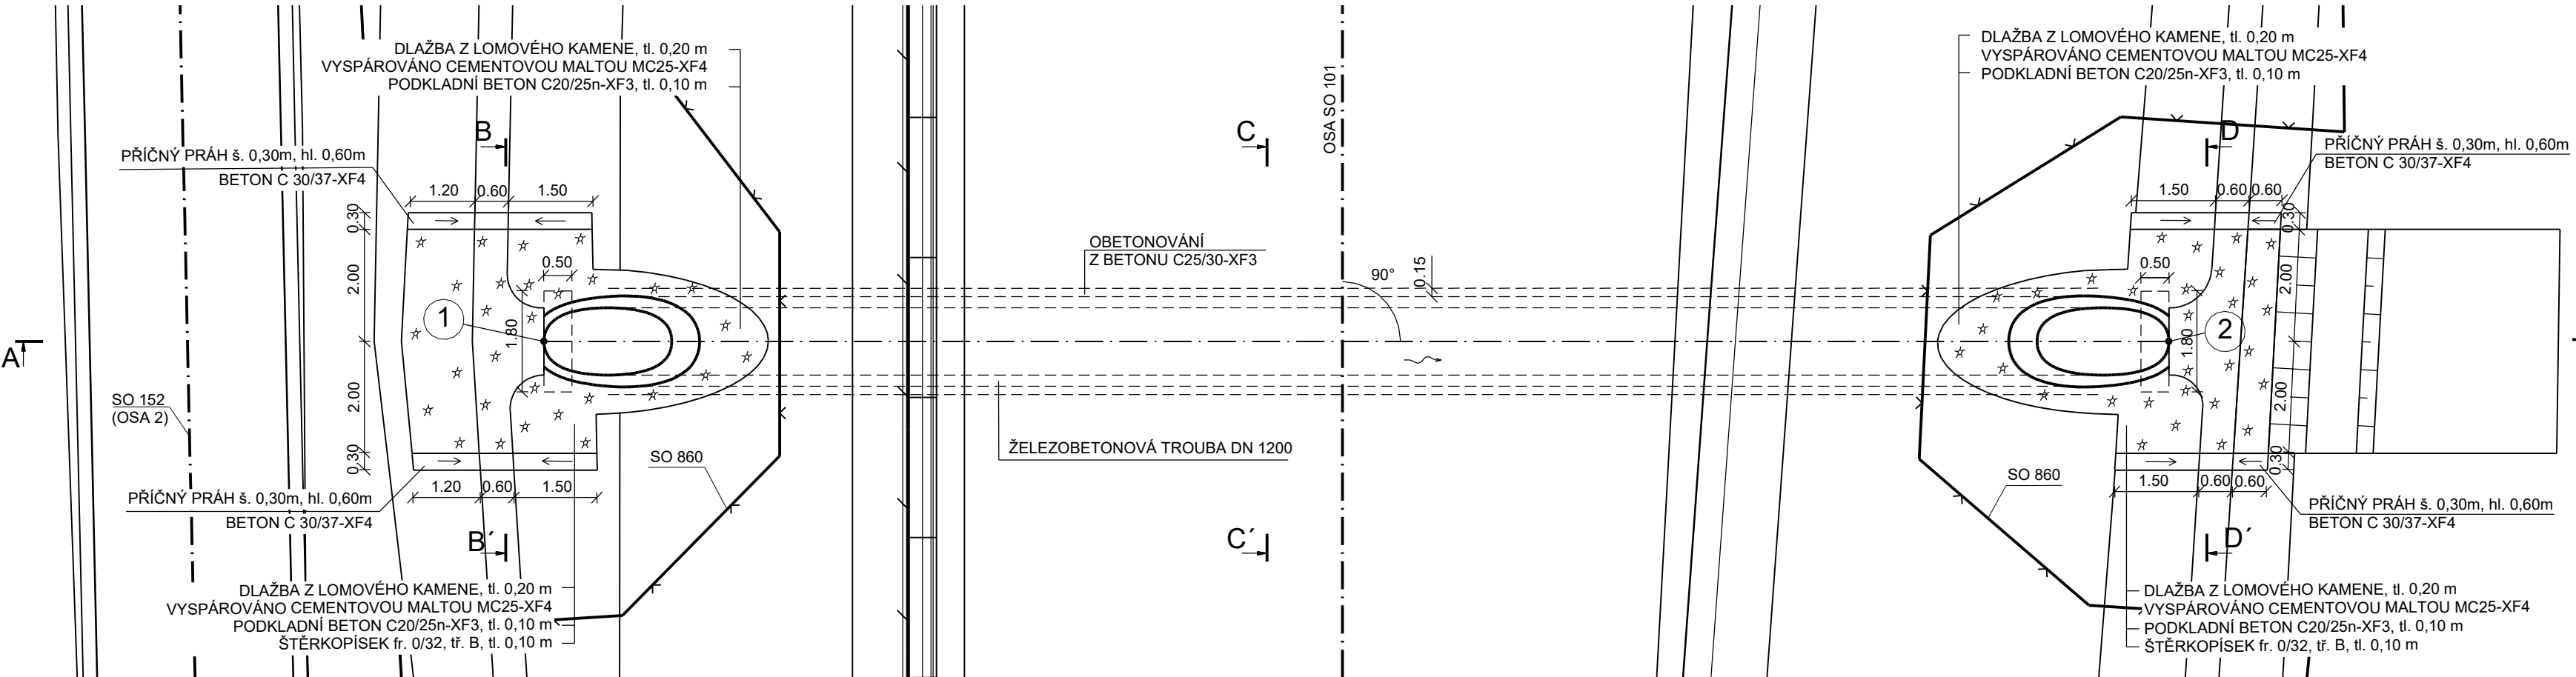


PODÉLNÝ ŘEZ A-A'

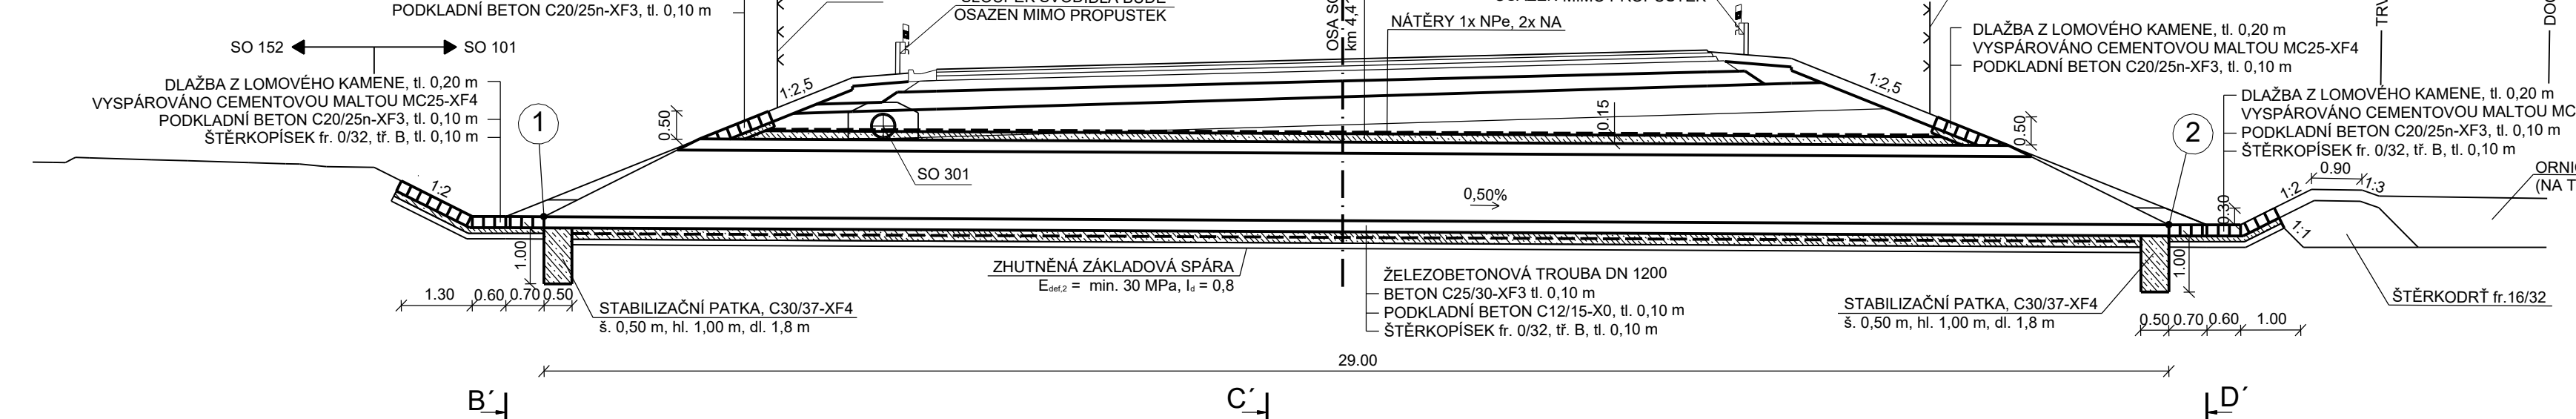


POHLED NA VTOK ŘEZ B-B'

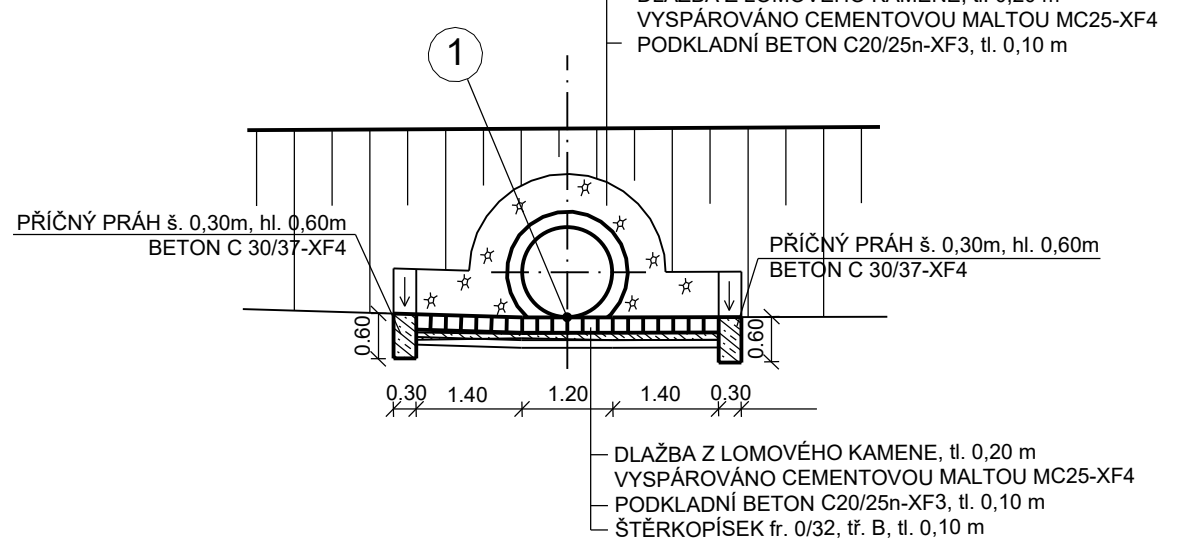

POHLED NA VÝTOK ŘEZ D-D'

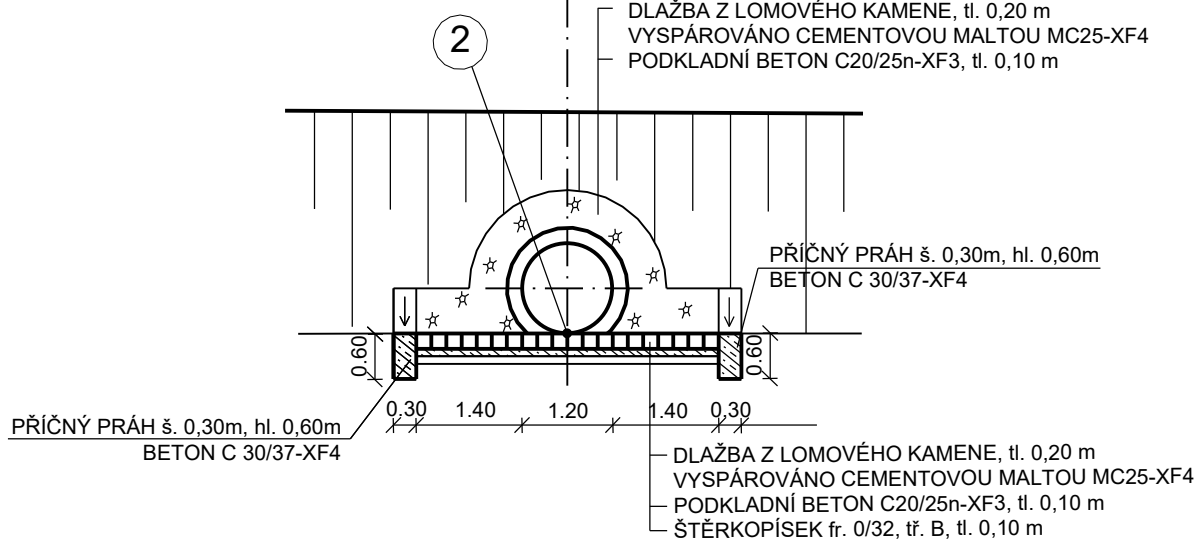

PŘÍČNÝ ŘEZ C-C'

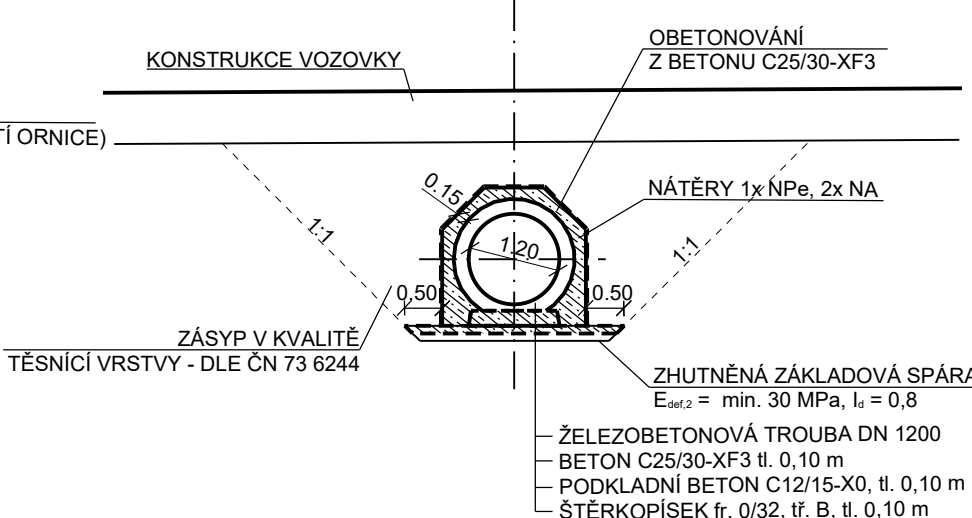

POZNÁMKY:

- SPÁROVÁNÍ DLAŽBY Z LOMOVÉHO KAMENE BUDE VYPLNĚNÉ CEMENTOVOU MALTOU MC25-XF4, tl. min. 0,20 m
- OBETONOVÁNÍ V MÍSTĚ HRDLA MINIMÁLNĚ 0,10 m
- VŠECHNY BETONOVÉ PRVKY, KTERÉ PŘÍJDOU DO STYKU SE ZEMINOU MUSÍ BÝT OPATŘENY NÁTĚRY: 1x NPe A 2x NA
- POČET PRAHŮ ZÁVISÍ NA TYPU ZVOLENÉ TROUBY A JEJÍHO ULOŽENÍ
- VYTÝČENÍ BUDE PROVEDENO DLE TKP 1 A SOUVISEJÍCÍCH PŘEDPISŮ
- SKLONY SVAHŮ JSOU URČENY SKLONEM SILNIČNÍHO TĚLESA A PŘÍLEHLÝCH PŘÍKOPŮ
- POKUD NEBUDOU NA KRAJÍCH OSAZENY ŠIKMÉ PREFABRIKÁTY, BUDOU PRO SEŘÍZNUTÍ POUŽITY BETONOVÉ TROUBY (Z DŮVODU KORODUJÍCÍ VÝZTUŽE)
- ŠÍŘE PODKLADNÍHO PRAHU JE 0,50 m NA KAŽDOU STRANU OD VNĚJŠÍHO OBRYSU TROUBY
- BETONOVÉ VÝROBKY VYSTAVENÉ PŘÍMĚMU OSTRÍKU ROZMRAZOVACÍCH PROSTŘEDKŮ A MRAZU A UMÍSTĚNÉ VE VZDÁLENOSTI MOŽNÉHO OSTRÍKU (OD HRANY VOZOVKY 10 m VČETNĚ SOLNĚ MLHY) MUSÍ SPLŇOVAT POŽADAVKY NA STUPEŇ VLIVU PROSTŘEDÍ XF4.
- MUSÍ BÝT ZAJIŠTĚNA KOORDINACE STAVEBNÍCH PRACÍ VÝSTAVBY PROPUSTKŮ A KANALIZACE V MÍSTĚ JEJICH KŘÍŽENÍ.

PARAMETRY PROPUSTKŮ					VYTYČOVANÉ BODY	
STANIČENÍ [km]	TROUBA DN [mm]	DĚLKA DL [m]	SKLON S _i [%]	ÚHEL α [°]	VTOK - 01 Y / X [S-JTSK] / Z [Bpv]	VÝTOK - 02 Y / X [S-JTSK] / Z [Bpv]
4,410	1200	29,00	0,50	90	696814,646/1011895,703/219,18	696812,705/1011924,638/219,03

SO 101Silnice I/16 Mladá Boleslav - Martinovice

Objednatel:

ŘEDITELSTVÍ
SILNIC
A DÁLNIC

Ředitelství silnic a dálnic s. p.
Čerčanská 2023/12, Krč, 140 00 Praha 4

Zhotovitel:

Valbek

Valbek, spol. s r.o.

Vaňurova 505/17
460 07 Liberec 3

	Vypracoval	A. BARTONIČKOVÁ	Zak. číslo	21-LI13-001
	Zodp. projektant	ING. T. KLIMENT	Datum	02/2025
	Tech. kontrola	ING. M. HANŽL	Stupeň	PDPS
	Akce	I/16 MLADÁ BOLESLAV - MARTINOVICE		Počet formátů
Zhotovitel: Valbek, spol. s r.o. Vaňurova 505/17 460 07 Liberec 3	Příloha PROPUSTEK DN 1200 V km 4,410		Měřítko	1 : 100
			Č. přílohy	Paré

6.10