

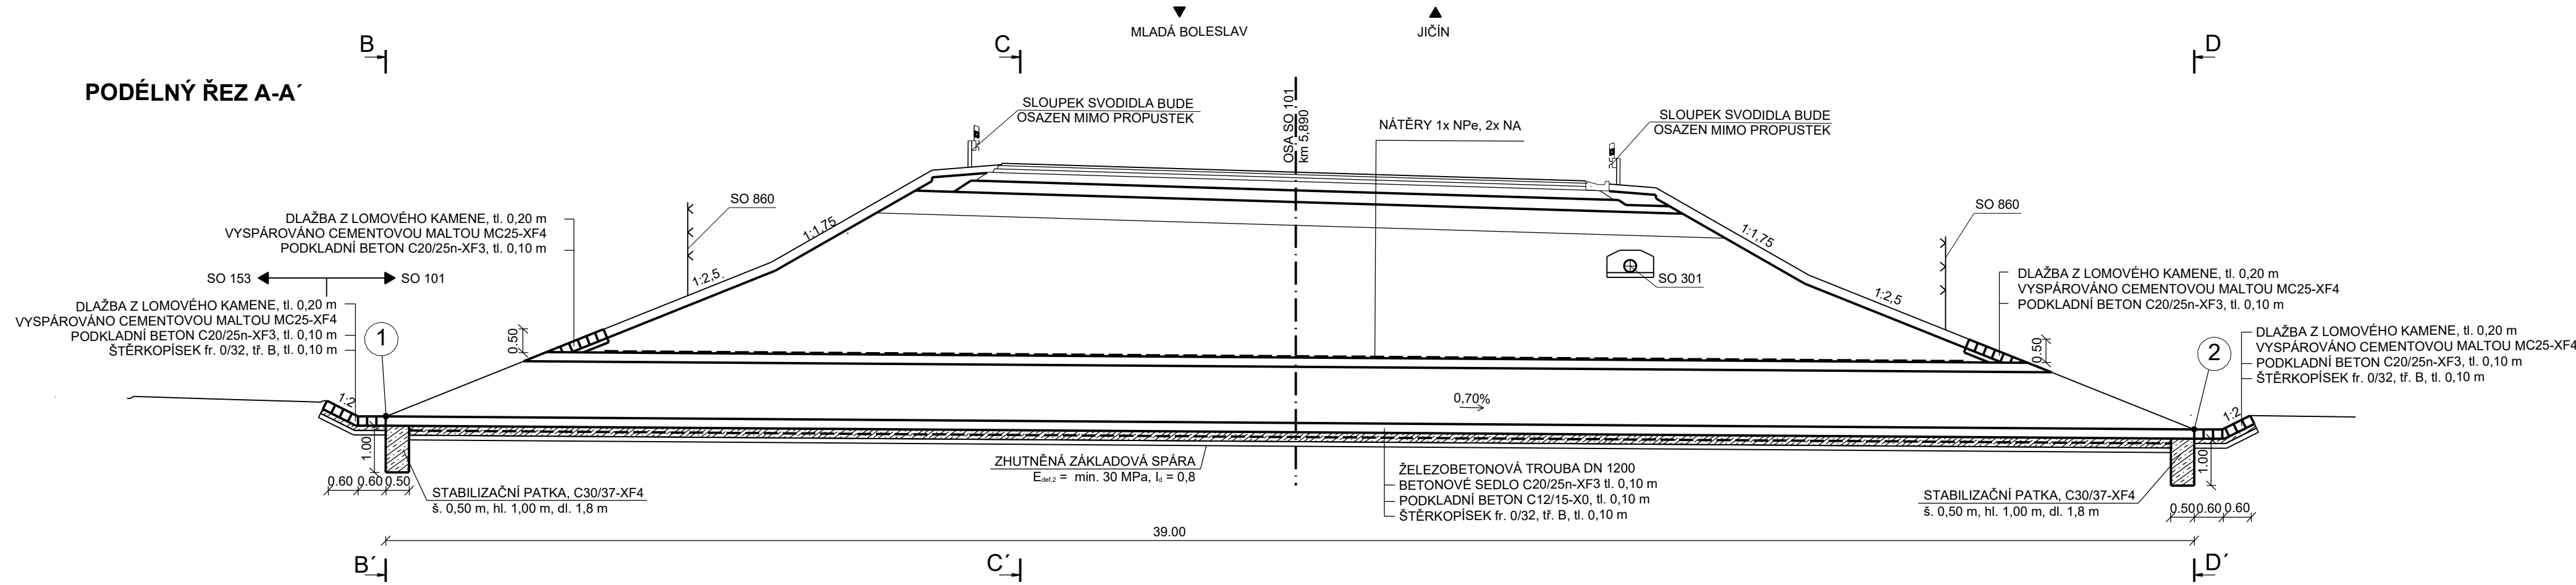



SO 101 - SILNICE I/16 MLADÁ BOLESLAV - MARTINOVICE
PROPUSTEK DN 1200 V km 5,890, M 1 : 100

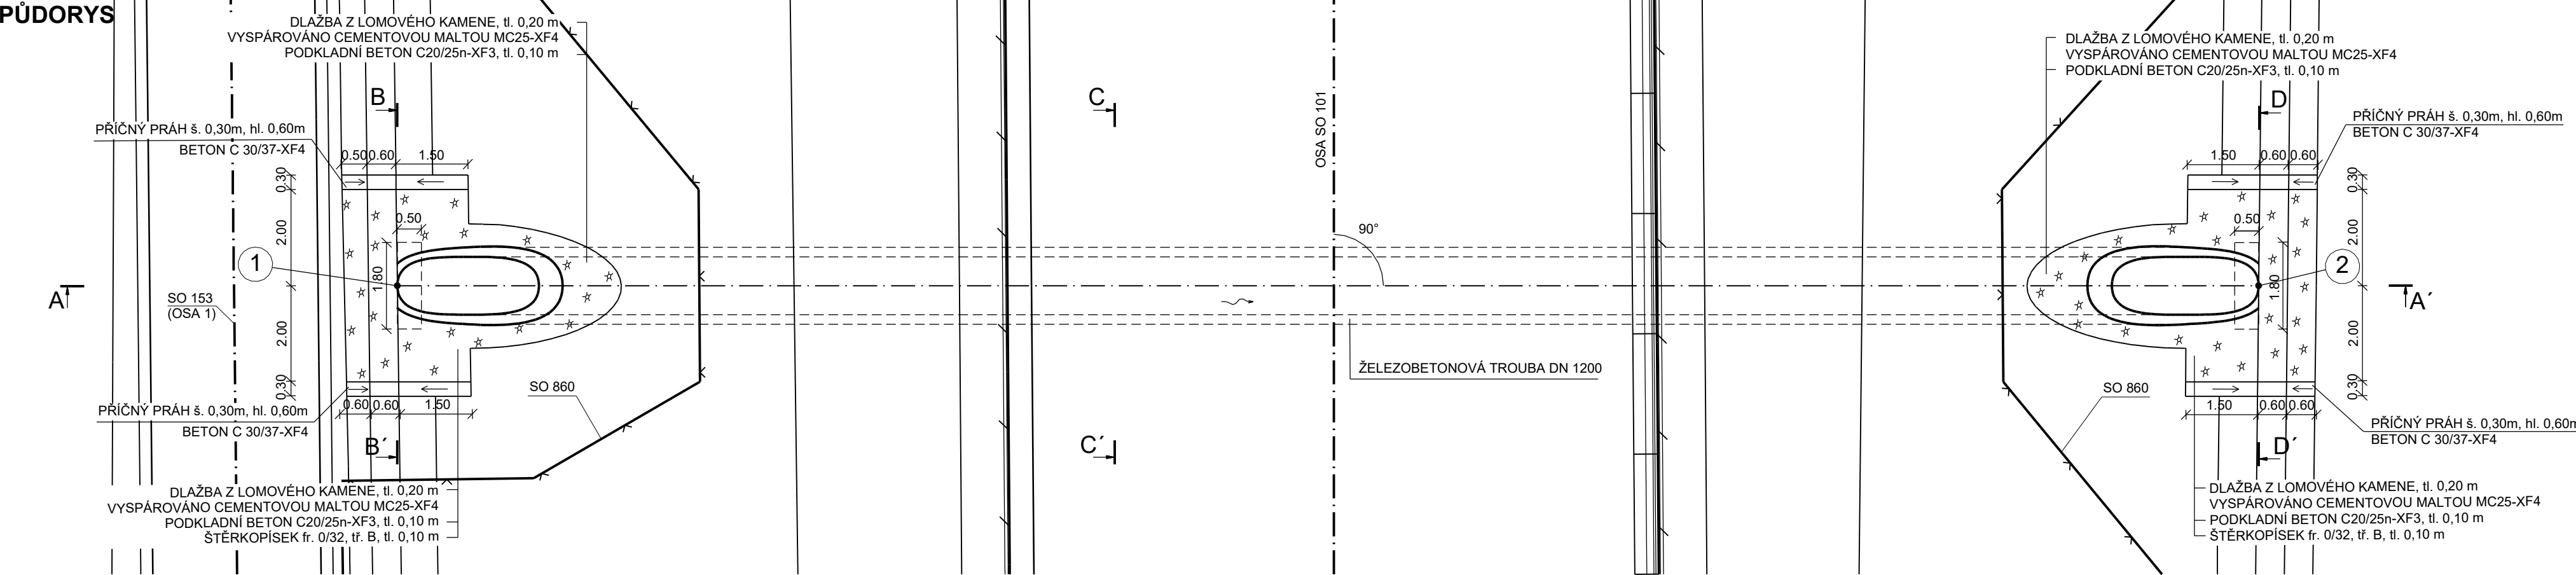


POHLED NA VTOK ŘEZ B-B'

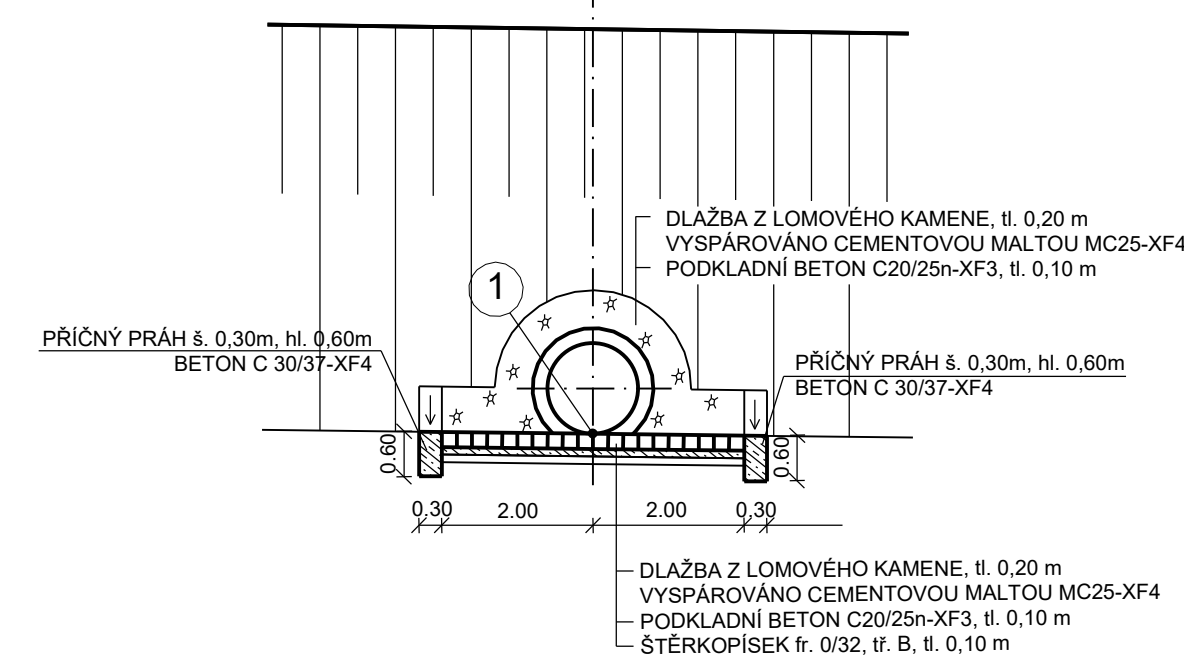

POHLED NA VÝTOK ŘEZ D-D'

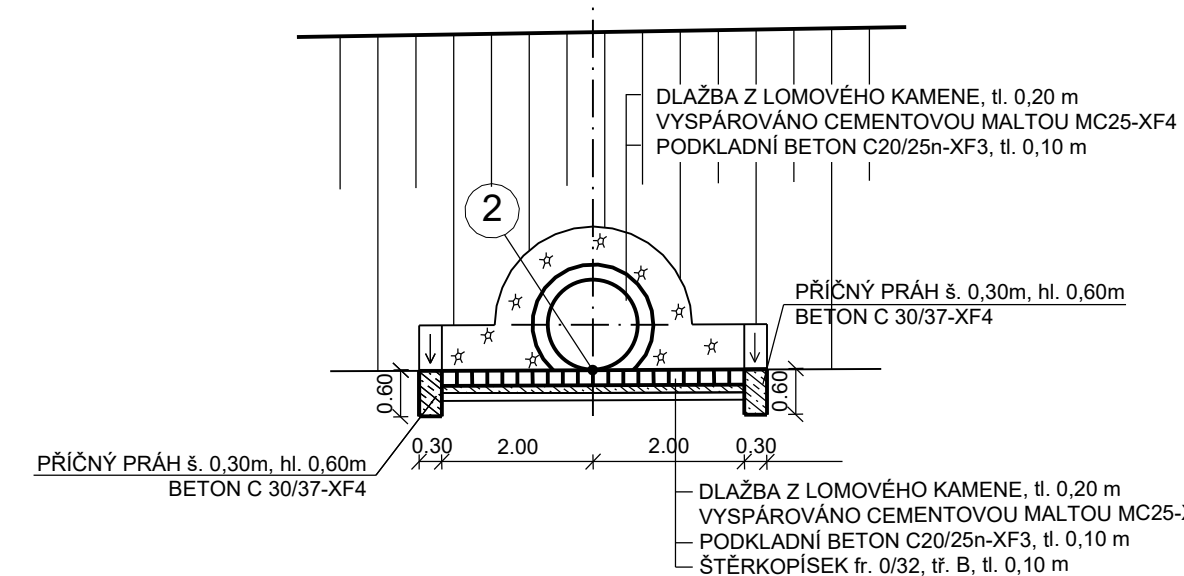

PRÍČNÝ ŘEZ C-C'

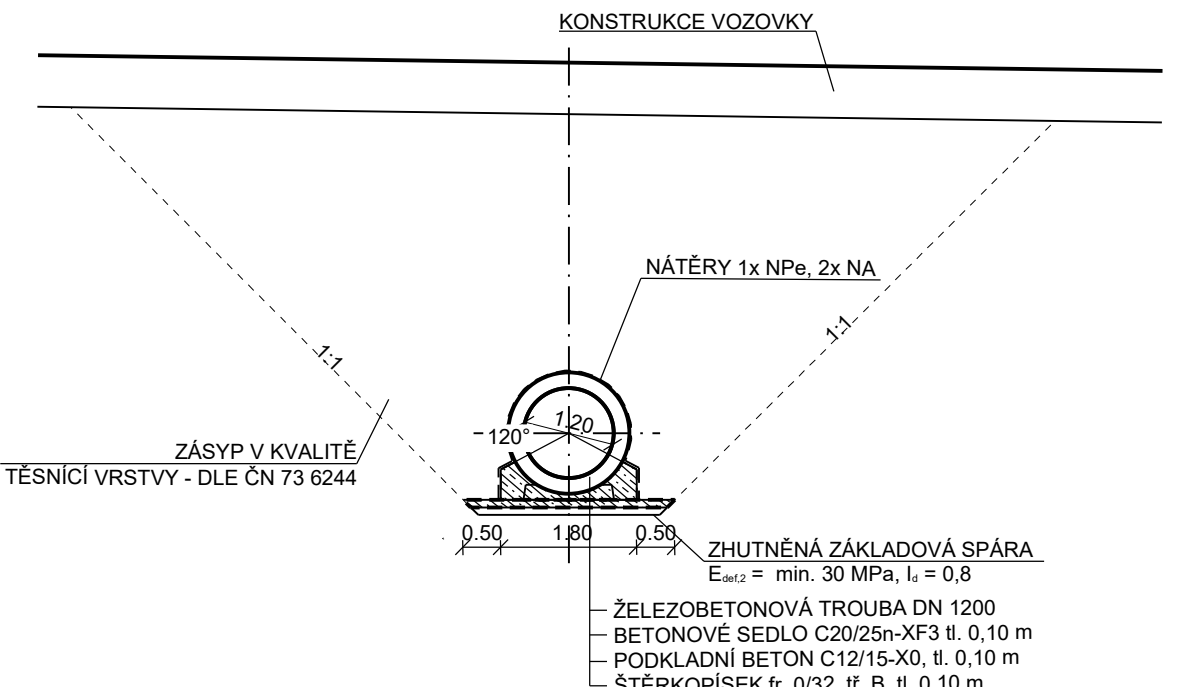

POZNÁMKY:

- SPÁROVÁNÍ DLAŽBY Z LOMOVÉHO KAMENE BUDE VYPLNĚNÉ CEMENTOVOU MALTOU MC25-XF4, tl. min. 0,20 m
- VŠECHNY BETONOVÉ PRVKY, KTERÉ PŘIJÍDOU DO STYKU SE ZEMINOU MUSÍ BÝT OPATŘENY NÁTĚRY: 1x NPe A 2x NA
- POČET PRAHŮ ZÁVISÍ NA TYPU ZVOLENÉ TROUBY A JEJÍHO ULOŽENÍ
- VYTÝČENÍ BUDE PROVEDENO DLE TKP 1 A SOUVISEJÍCÍCH PŘEDPISŮ
- SKLONY SVAHŮ JSOU URČENY SKLONEM SILNIČNÍHO TĚLESA A PŘÍLEHLÝCH PŘÍKOPŮ
- POKUD NEBUDOU NA KRAJÍCH OSAZENY ŠIKMÉ PREFABRIKÁTY, BUDOU PRO SEŘÍZNUTÍ POUŽITY BETONOVÉ TROUBY (Z DŮVODU KORODUJÍCÍ VÝZTUŽE)
- ŠÍŘE PODKLADNÍHO PRAHU JE 0,50 m NA KAŽDOU STRANU OD VNĚJŠÍHO OBRYSU TROUBY
- BETONOVÉ VÝROBKY VYSTAVENÉ PŘÍMĚMU OSTRÍKU ROZMRAZOVACÍCH PROSTŘEDKŮ A MRAZU A UMÍSTĚNÉ VE VZDÁLENOSTI MOŽNÉHO OSTRÍKU (OD HRANY VOZOVKY 10 m VČETNĚ SOLNĚ MLHY) MUSÍ SPLŇOVAT POŽADAVKY NA STUPEŇ VLIVU PROSTŘEDÍ XF4.
- MUSÍ BÝT ZAJIŠTĚNA KOORDINACE STAVEBNÍCH PRACÍ VÝSTAVBY PROPUSTKŮ A KANALIZACE V MÍSTĚ JEJICH KŘÍŽENÍ.

PARAMETRY PROPUSTKŮ					VYTYČOVANÉ BODY	
STANIČENÍ [km]	TROUBA DN [mm]	DĚLKA DL [m]	SKLON S. [%]	ÚHEL α [°]	VTOK - 01 Y / X [S-JTSK] / Z [Bpv]	VÝTOK - 02 Y / X [S-JTSK] / Z [Bpv]
5,890	1200	39,00	0,70	90	695519,439/1011317,085/224,08	695491,443/1011343,832/223,80

Souřadnicový systém: S-JTSK
Výškový systém: Bpv

SO 101

Silnice I/16 Mladá Boleslav - Martinovice

Objednatel:

ŘEDITELSTVÍ SILNIC A DÁLNIC

Ředitelství silnic a dálnic s. p.
Čerčanská 2023/12, Krč, 140 00 Praha 4

Zhotovitel:

Valbek

Valbek, spol. s r.o.
Vaňurova 505/17
460 07 Liberec 3

	Vypracoval	A. BARTONIČKOVÁ		Zak. číslo	21-L113-001
	Zodp. projektant	ING. T. KLIMENT		Datum	02/2025
	Tech. kontrola	ING. M. HANŽL		Stupeň	PDPS
	Akce			Počet formátů	5 x A4
Zhotovitel: Valbek, spol. s r.o. Vaňurova 505/17 460 07 Liberec 3	I/16 MLADÁ BOLESLAV - MARTINOVICE			Měřítko	1 : 100
				Č. přílohy	Paré
	Příloha			6.12	
	PROPUSTEK DN 1200 V km 5,890				