




SO 101 - SILNICE I/16 MLADÁ BOLESLAV - MARTINOVICE
PROPUSTEK DN 1200 V km 5,970, M 1 : 100

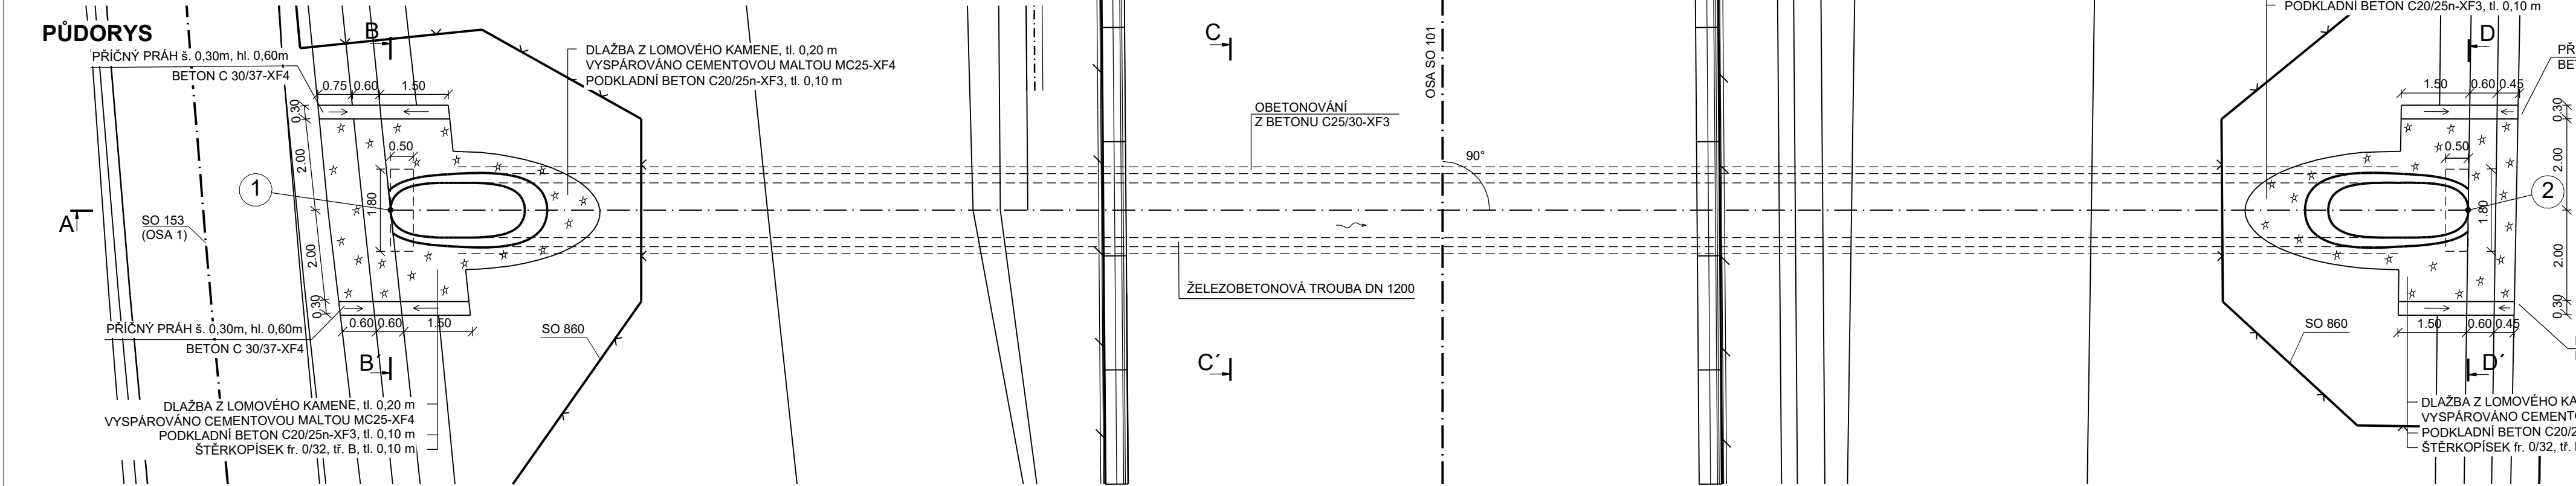


PODÉLNÝ ŘEZ A-A'

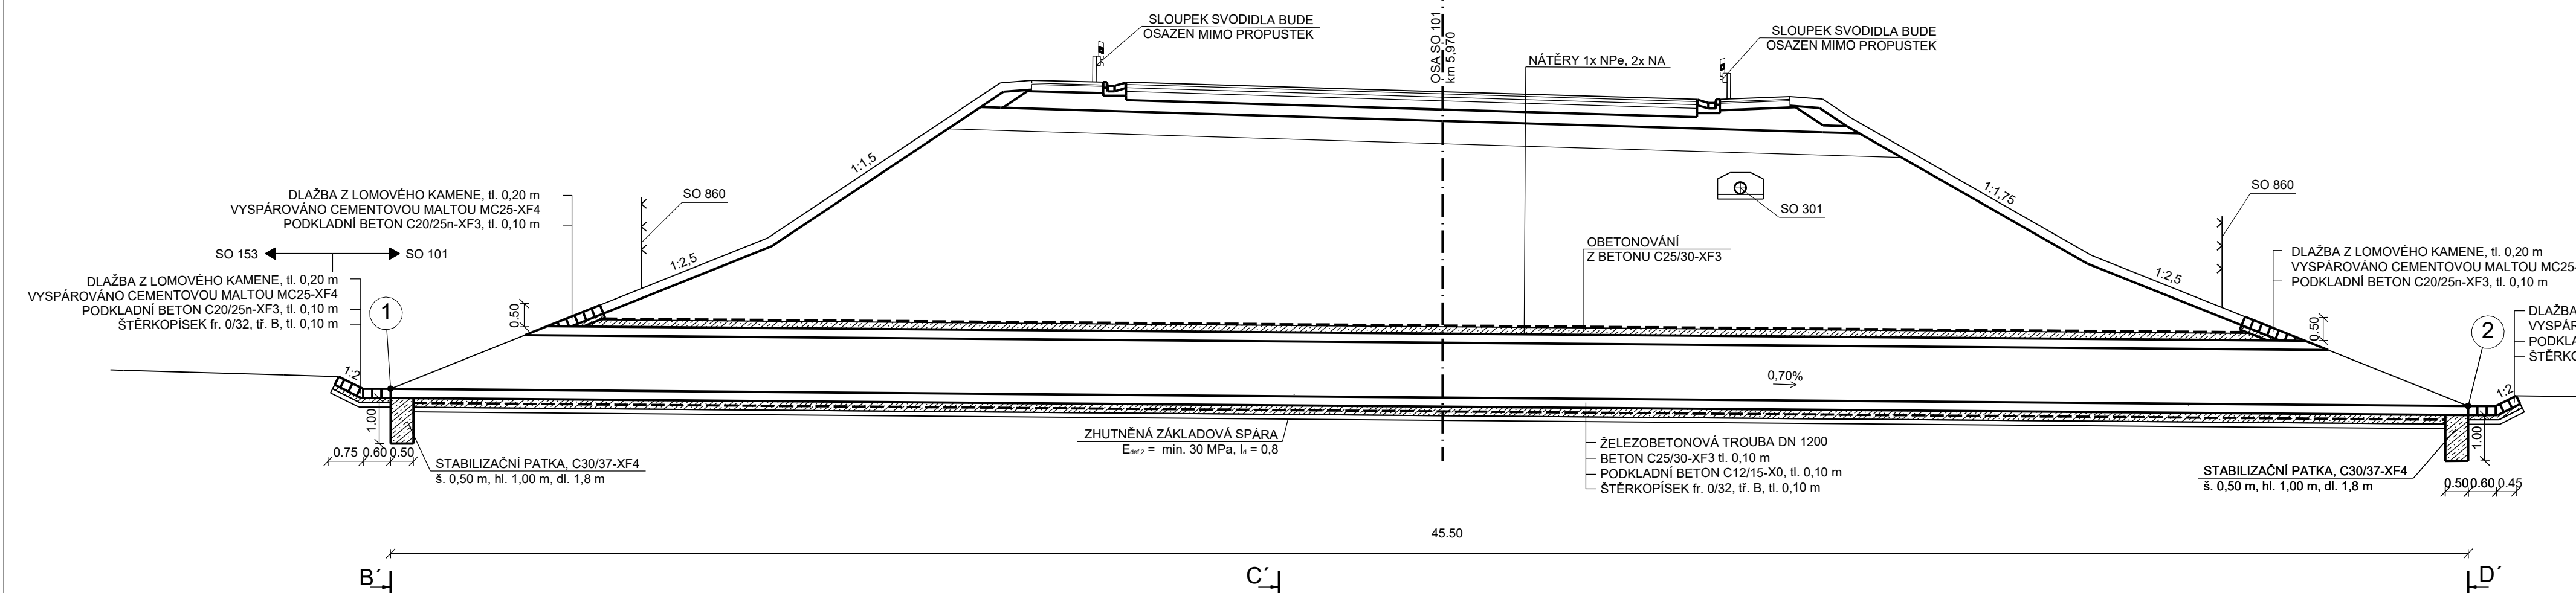

POHLED NA VTOK ŘEZ B-B'

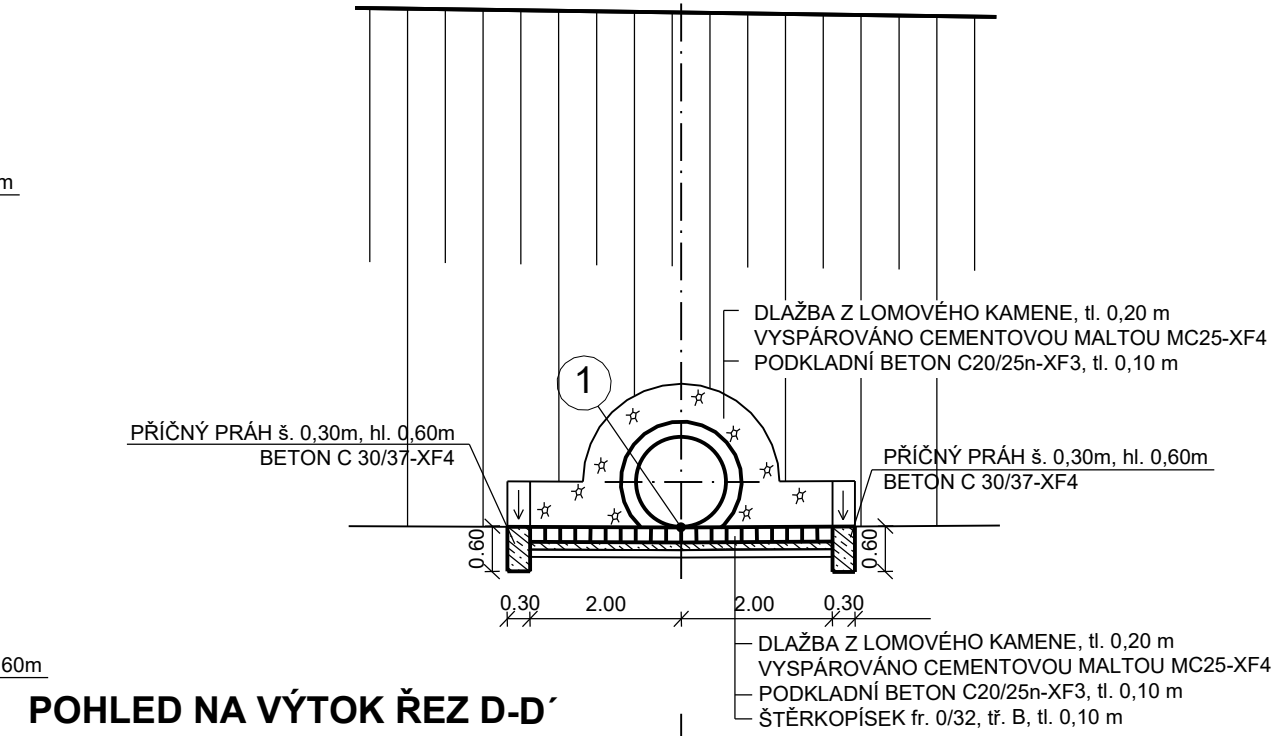

POHLED NA VÝTOK ŘEZ D-D'

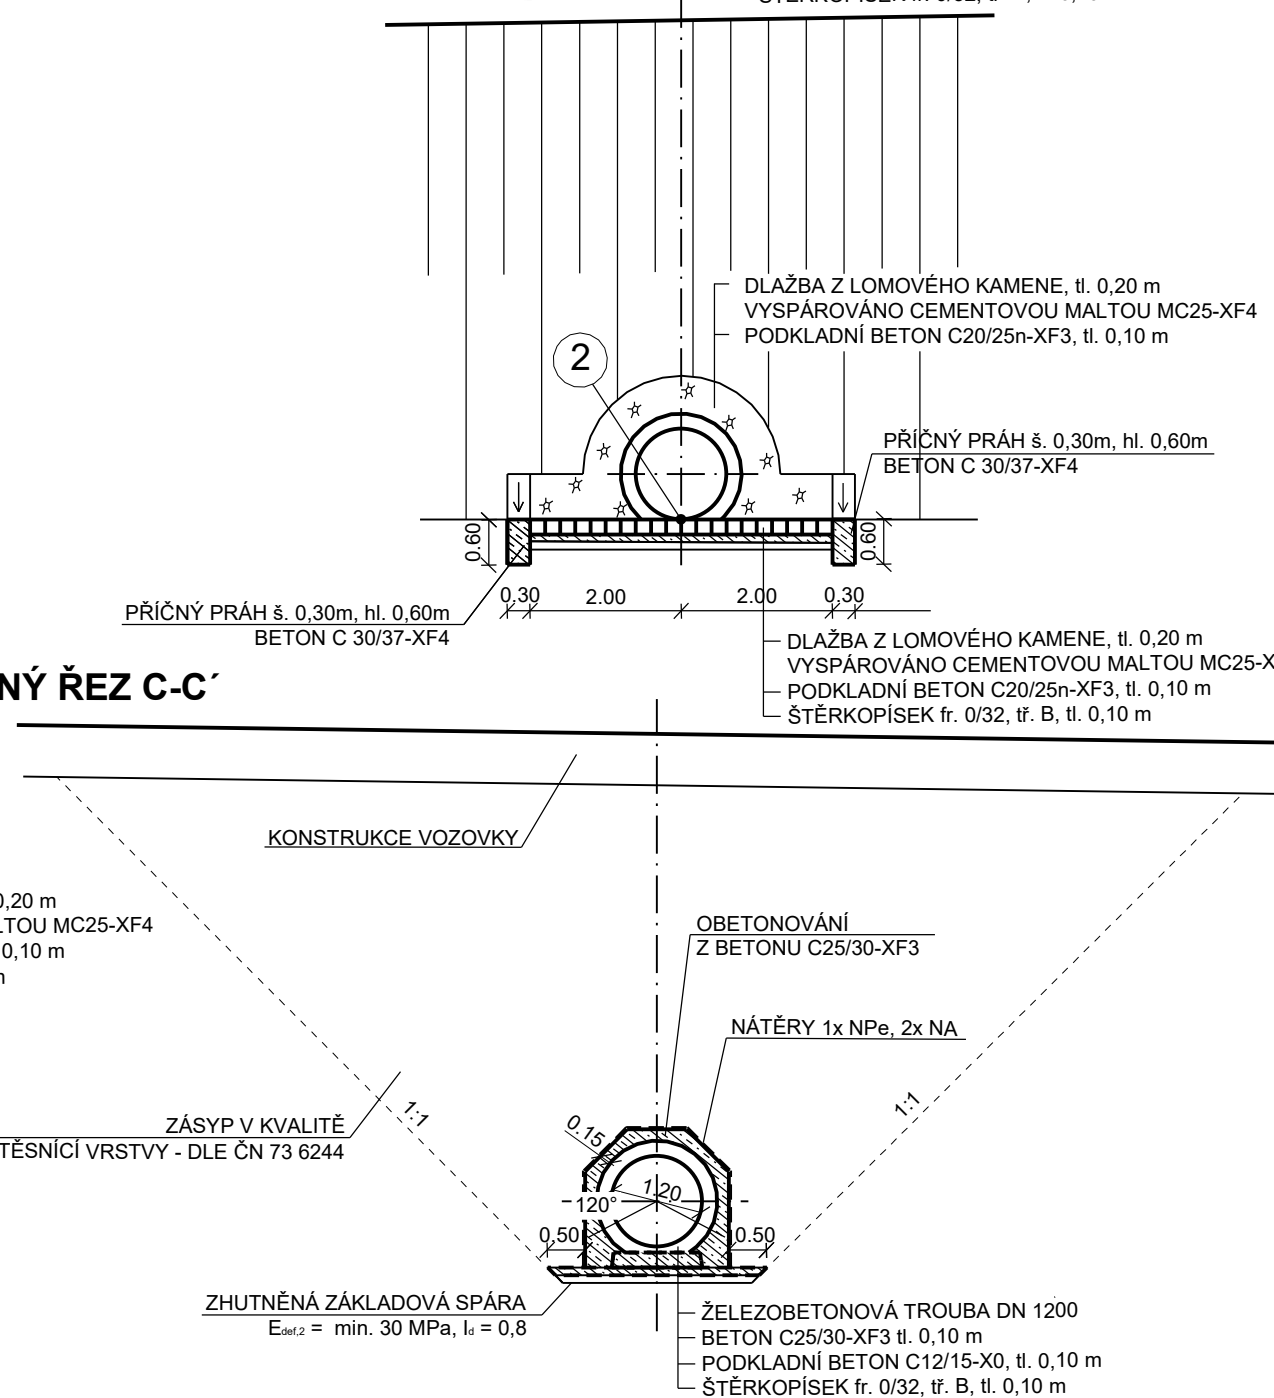

POZNÁMKY:

- SPÁROVÁNÍ DLAŽBY Z LOMOVÉHO KAMENE BUDE VYPLNĚNÉ CEMENTOVOU MALTOU MC25-XF4, tl. min. 0,20 m
- VŠECHNY BETONOVÉ PRVKY, KTERÉ PŘIJÍDOU DO STYKU SE ZEMINOU MUSÍ BÝT OPATŘENY NÁTĚRY: 1x NPc A 2x NA
- POČET PRÁHŮ ZÁVISÍ NA TYPU ZVOLENÉ TROUBY A JEJÍHO ULOŽENÍ
- VYTÝČENÍ BUDE PROVEDENO DLE TKP 1 A SOUVISEJÍCÍCH PŘEDPISŮ
- SKLONY SVAHŮ JSOU URČENY SKLOMEM SILNIČNÍHO TĚLESA A PŘÍLEHLÝCH PŘÍKOPŮ
- POKUD NEBUDOU NA KRAJÍCH OSAZENY ŠÍKME PREFABRIKÁTY, BUDOU PRO SEŘÍZNUTÍ POUŽITY BETONOVÉ TROUBY (Z DŮVODU KORODOUJÍCÍ VÝZTUŽE)
- ŠÍŘE PODKLADNÍHO PRAHU JE 0,50 m NA KAŽDOU STRANU OD VNĚJŠÍHO OBRYSU TROUBY
- BETONOVÉ VÝROBKY VYSTAVENÉ PŘÍMÉMU OSTRÍKU ROZMRAZOVACÍCH PROSTŘEDKŮ A MRAZU A UMÍSTĚNÉ VE VZDÁLENOSTI MOŽNÉHO OSTRÍKU (OD HRANY VOZOVKY 10 m VČETNĚ SOLNÉ MLHY) MUSÍ SPLŇOVAT POŽADAVKY NA STUPEŇ VLIVU PROSTŘEDÍ XF4.
- MUSÍ BÝT ZAJIŠTĚNA KOORDINACE STAVEBNÍCH PRACÍ VÝSTAVBY PROPUSTKŮ A KANALIZACE V MÍSTĚ JEJICH KŘÍŽENÍ.

PARAMETRY PROPUSTKŮ					VYTÝČOVANÉ BODY	
STANIČNÍ [km]	TROUBA DN [mm]	DĚLKA DL [m]	SKLON S _i [‰]	ÚHEL α [°]	VTOK - 01 Y / X [S-JTSK] / Z [Bpv]	VÝTOK - 02 Y / X [S-JTSK] / Z [Bpv]
5,970	1200	45,50	0,70	90	695466,740/1011256,790/224,00	695433,856/1011288,207/223,62

Souřadnicový systém: S-JTSK
Výškový systém: Bpv

SO 101 Silnice I/16 Mladá Boleslav - Martinovice

Objednatel:

 **ŘEDITELSTVÍ SILNIC A DÁLNIC**

Ředitelství silnic a dálnic s. p.
Čerčanská 2023/12, Krč, 140 00 Praha 4

Zhotovitel:

 **Valbek**

Valbek, spol. s r.o.
Vaňurova 505/17
460 07 Liberec 3

	Vypracoval	A. BARTONIČKOVÁ		Zak. číslo	21-LH3-001
	Zodp. projektant	ING. T. KLIMENT		Datum	02/2025
	Tech. kontrola	ING. M. HANŽL		Stupeň	PDPS
	Akce I/16 MLADÁ BOLESLAV - MARTINOVICE			Počet formátů	5 x A4
				Měřítka	1 : 100
Zhotovitel: Valbek, spol. s r.o. Vaňurova 505/17 460 07 Liberec 3	Příloha PROPUSTEK DN 1200 V km 5,970			Č. přílohy	Paré
					6.13