



SO 101 - SILNICE I/16 MLADÁ BOLESLAV - MARTINOVICE
RÁMOVÝ PROPUSTEK 2,0 x 2,0 m V km 6,500, M 1: 100


PŪDORYS

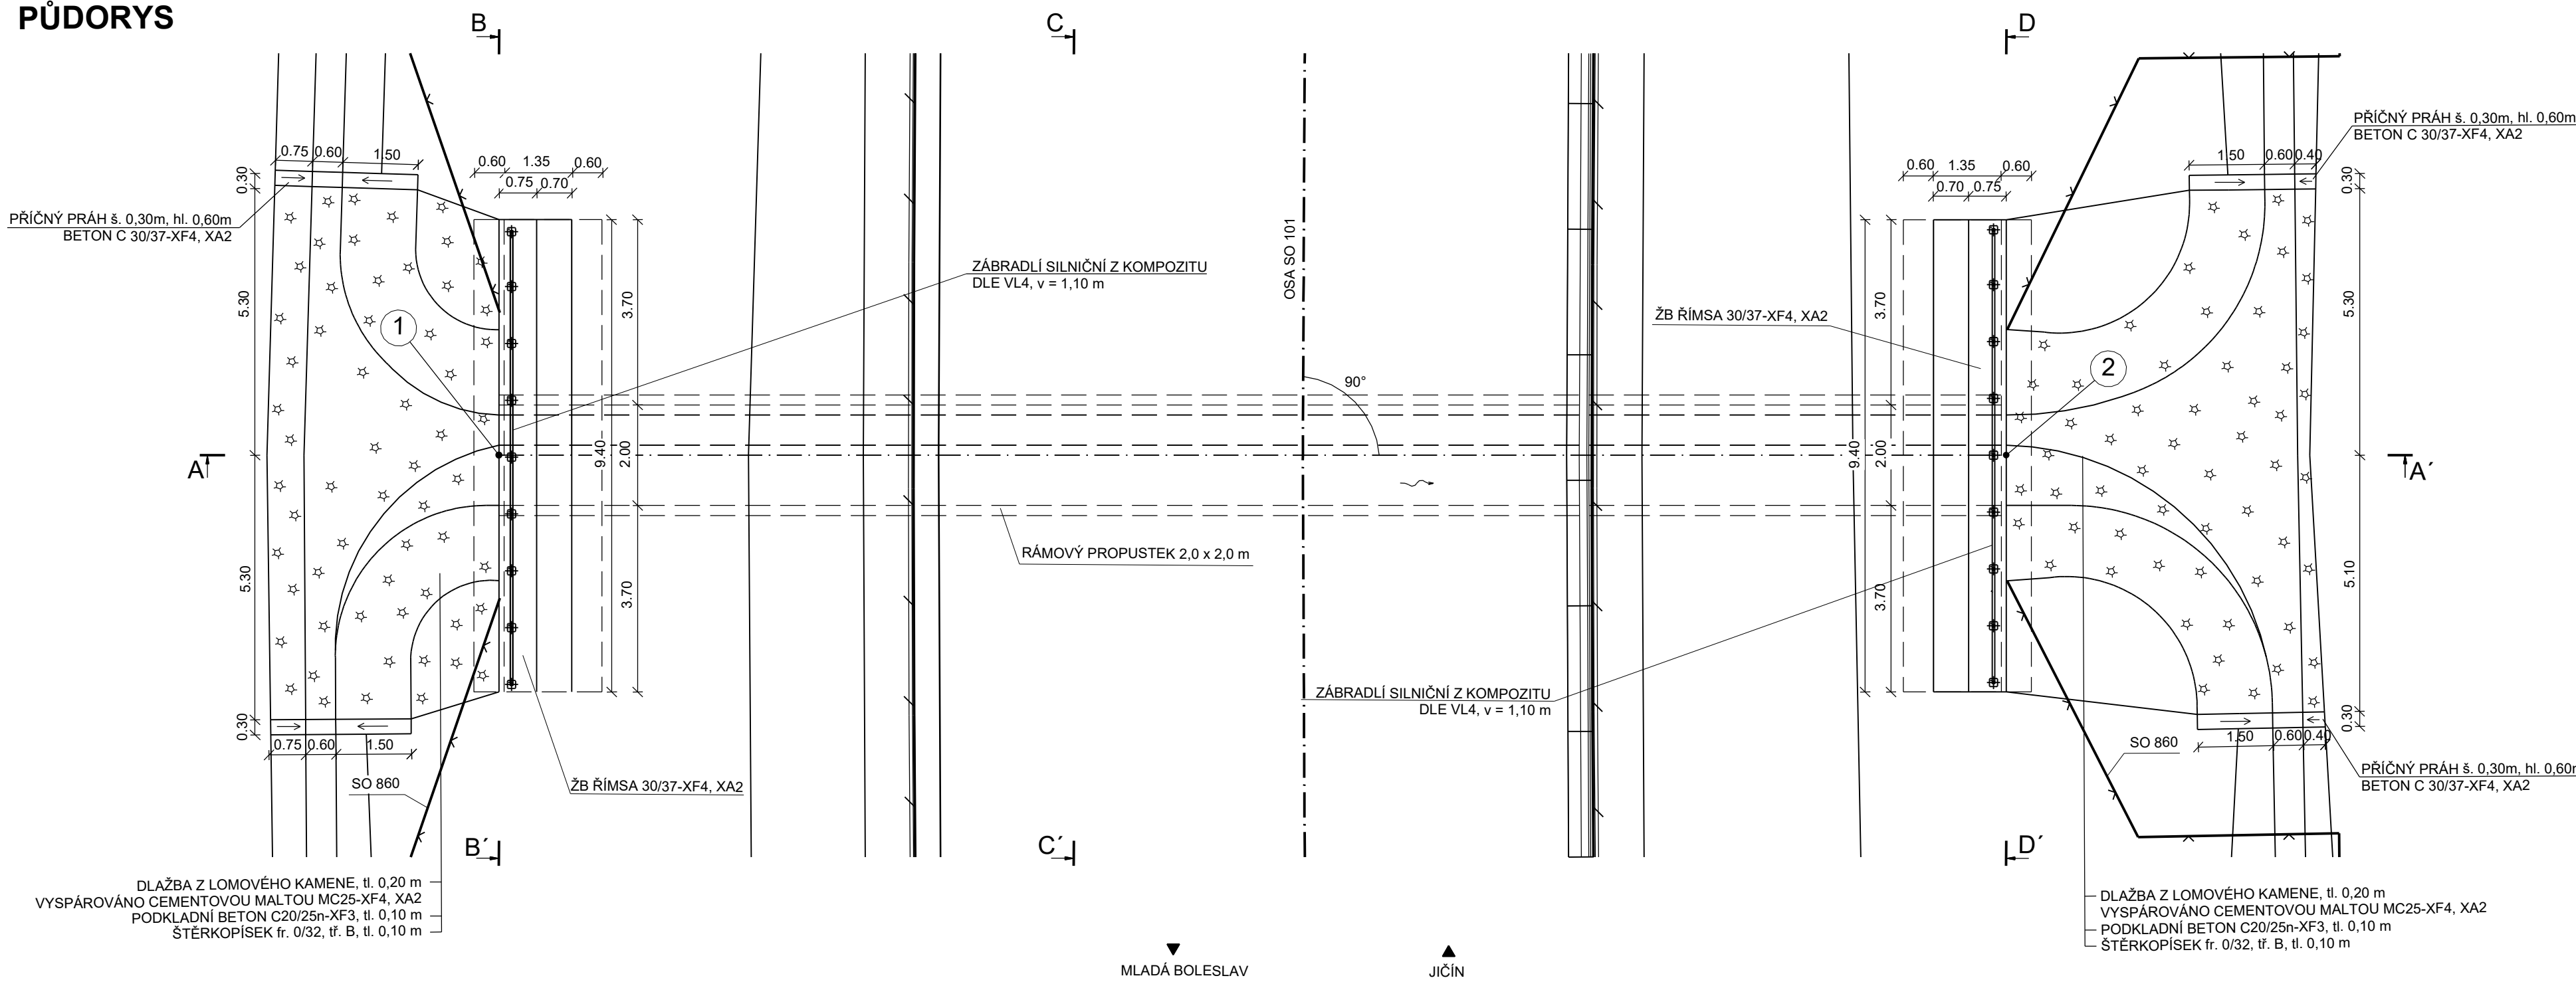


PODÉLNÝ ŘEZ A-A

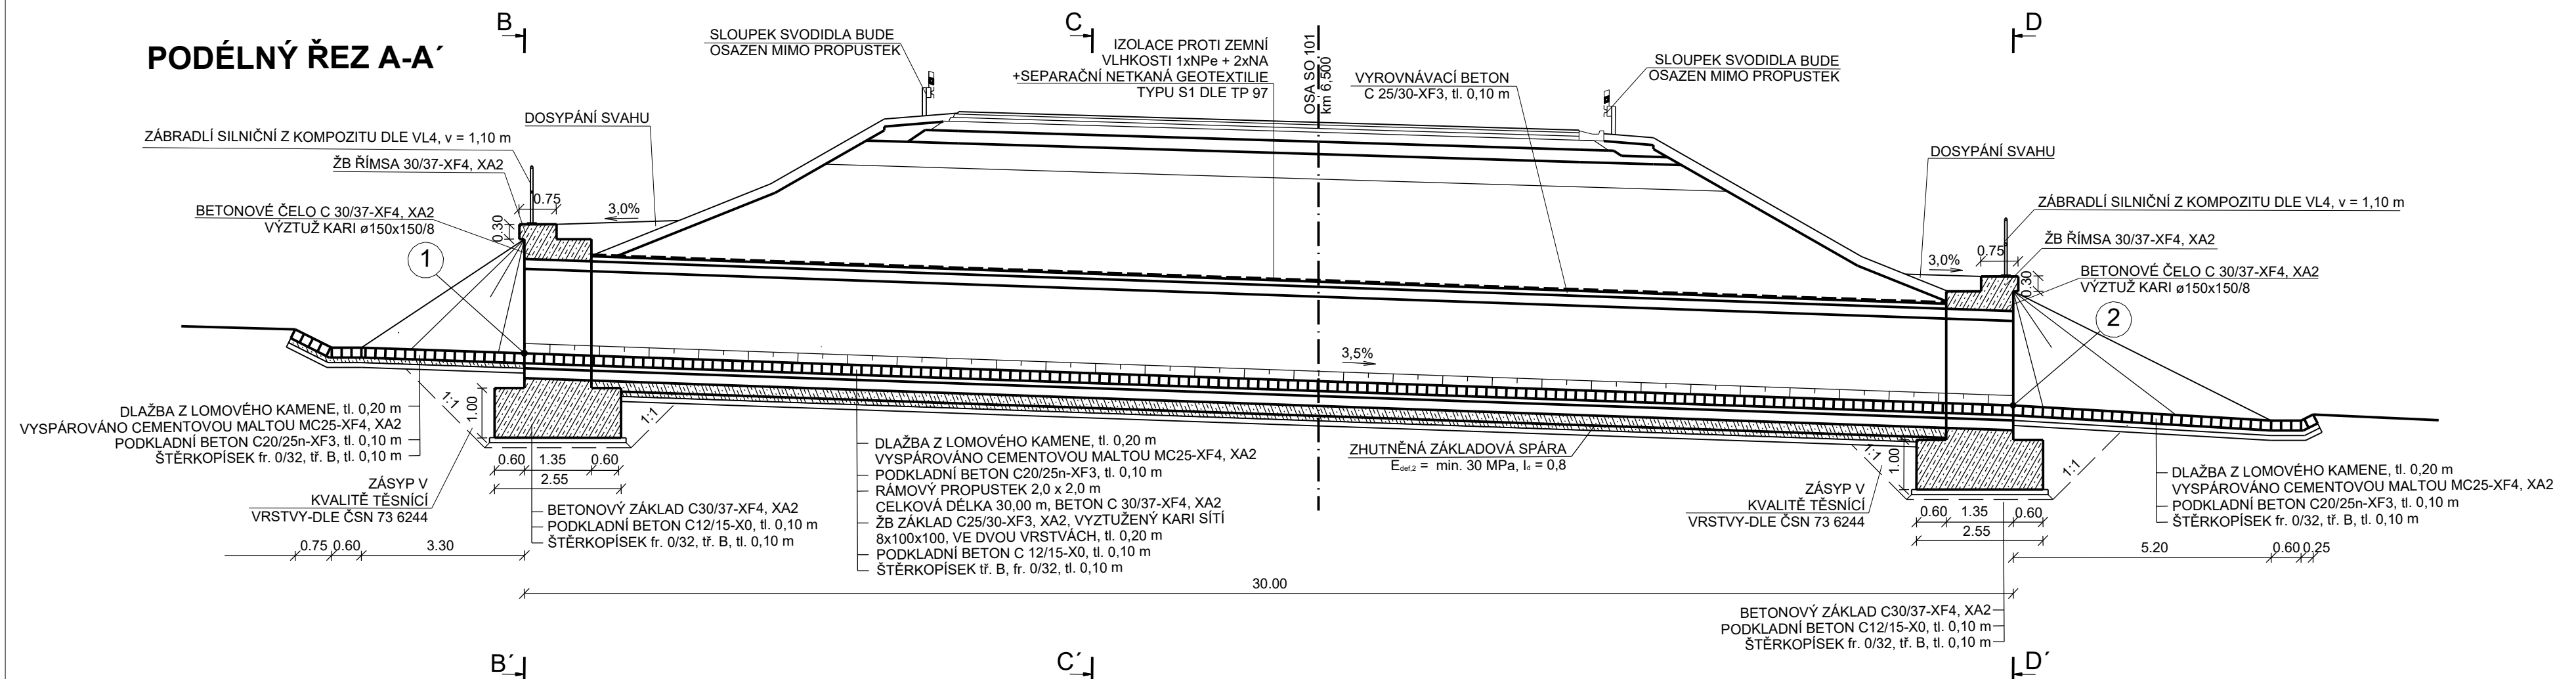


POHLED NA VÝTOK ŘEZ D-D'

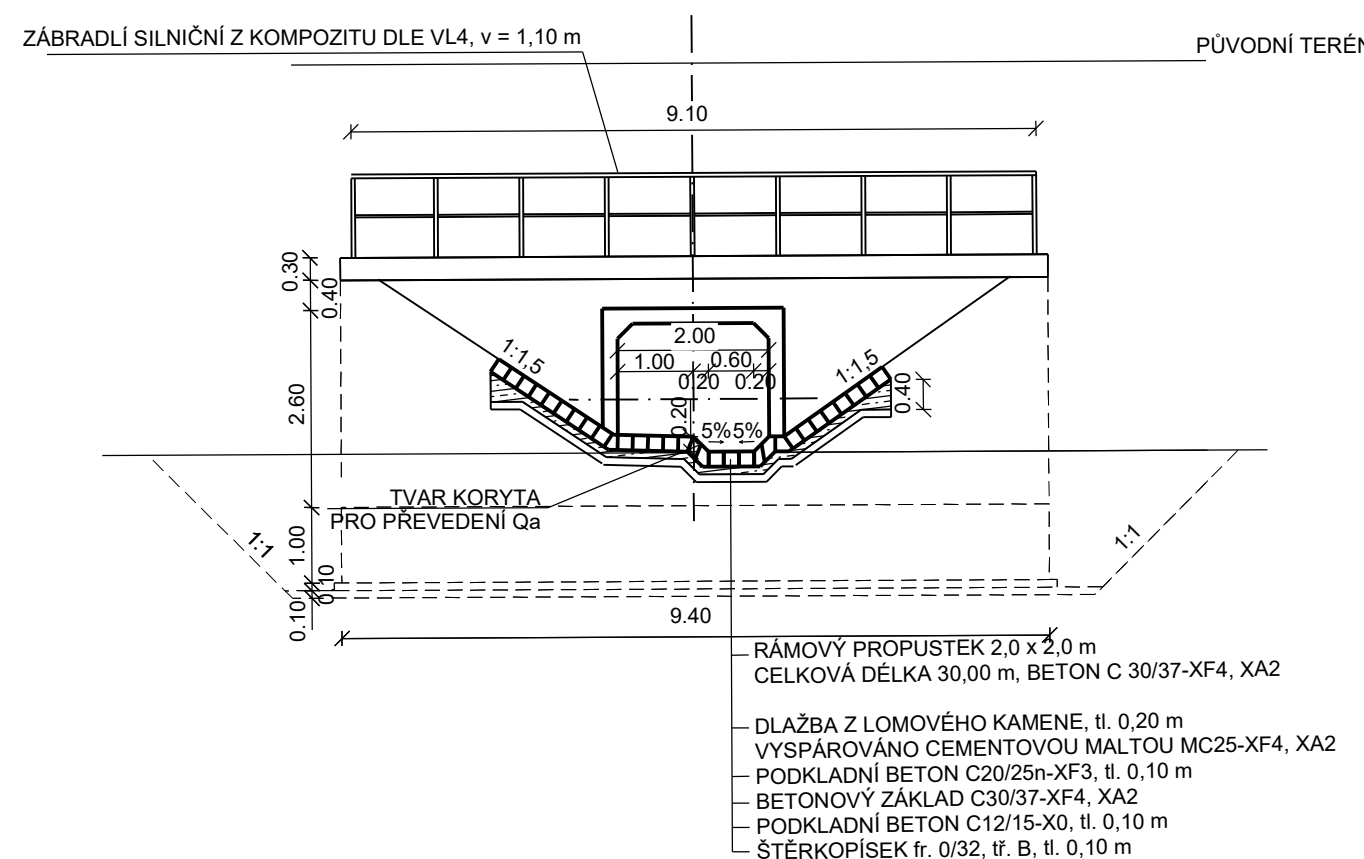

POHLED NA VTOK ŘEZ B-B'

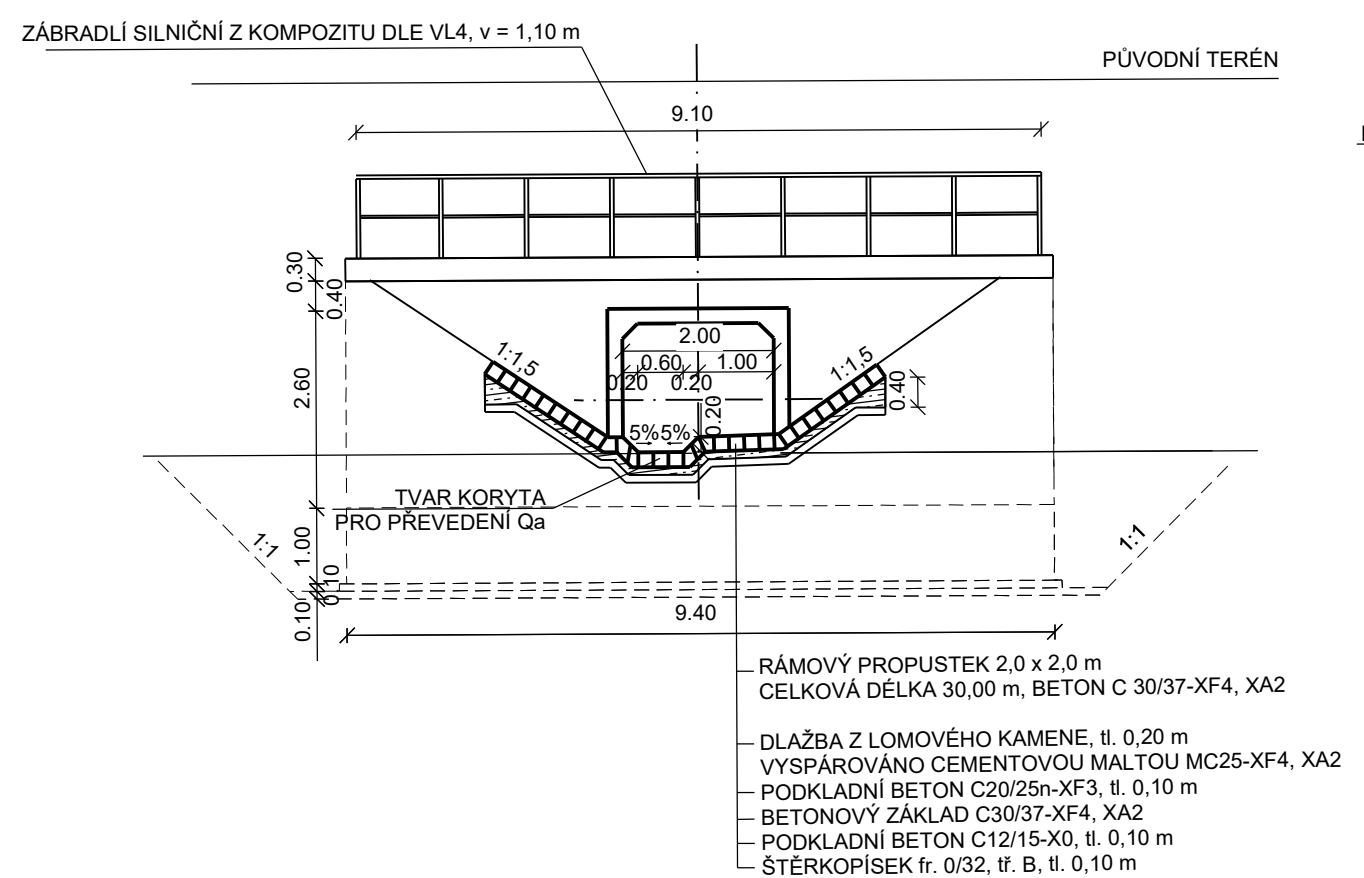


PŘÍČNÝ ŘEZ C-C

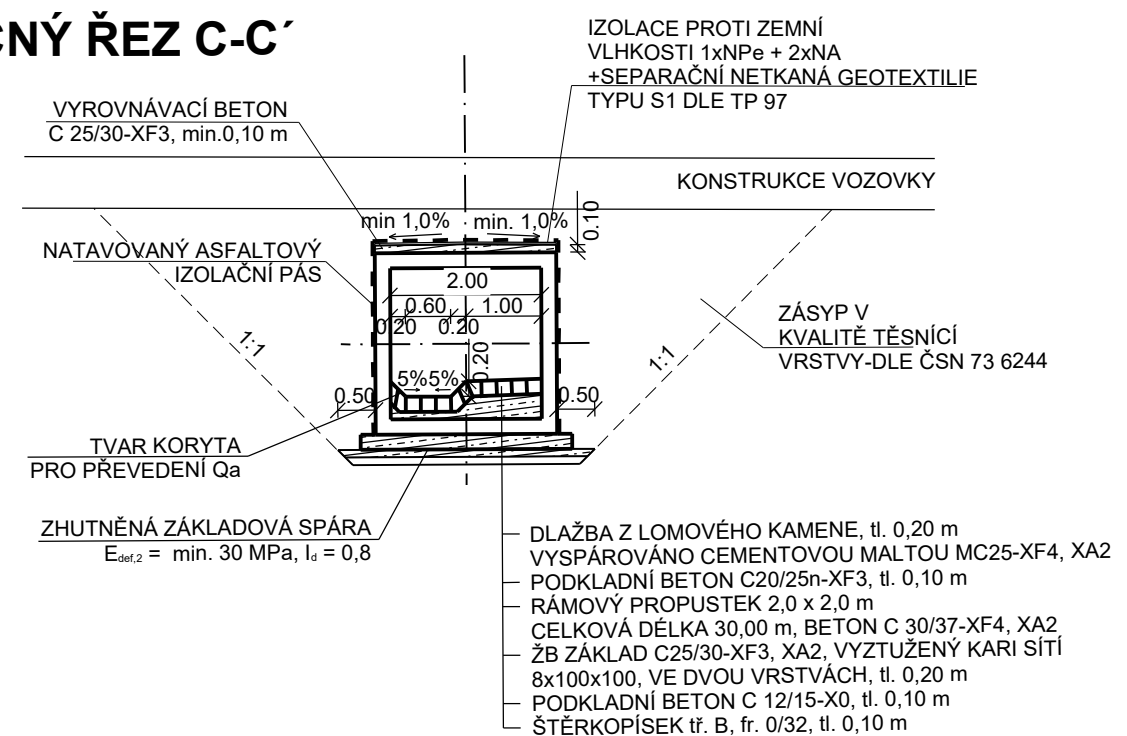


POZNÁMKA:

- SPÁROVÁNÍ DLAŽBY Z LOMOVÉHO KAMENE BUDE VYPLNĚNO CEMENTOVOU MALTOU M25 S ODOLNOSTÍ XF4, tl. min. 200 mm
- VŠECHNY BETONOVÉ PRVKY, KTERÉ PŘIJOU DÍL STYKU SE ZEMÍ, MUSÍ BÝT OPATŘENY NÁTĚRY: 1x NP a 2x ZA
- VYTÝČENÍ BUDE PROVEDENO DLE TKP 1 A SOUVISEJÍCÍ PŘEDPISU
- SKLONY SVAHŮ JSOU URČENY SKLONEM I SILNICNÍHO TĚLESA A PŘÍLEHLÝCH PŘÍKOPŮ
- DETAILY JSOU KÓTOVÁNY V MILIMETRECH
- KORYTO BUDE VYTVAROVÁNO DO STŘELKY

DETAIL UKOTEVNÍ, M 1:10

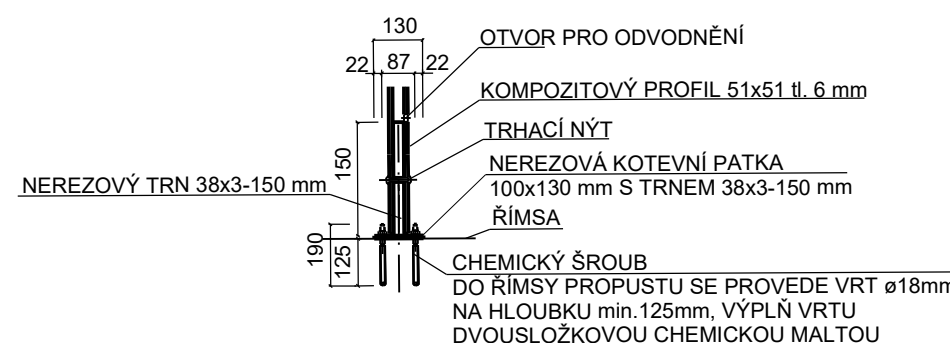

DETAIL KOTEVNÍ PATKY, M 1:10

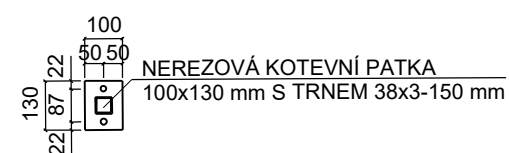

PARAMETRY PROPUSTKŮ					VYTÝČOVANÉ BODY	
STANIČNÍ [km]	DN [m]	DĚLKA DL [m]	SKLON S. [%]	ÚHEL α [°]	VTOK - 01 Y / X [S-JTSK] / Z [Bpv]	VÝTOK - 02 Y / X [S-JTSK] / Z [Bpv]
6,500	2 x 2	30,00	3,50	90	695039,152/1010938,577/228,58	695027,315/1010966,144/227,53

Souřadnicový systém: S-JTSK
Výškový systém: Bpv

SO 101 Silnice I/16 Mladá Boleslav - Martinovice

Objednatel:



Ředitelství silnic a dálnic s. p.
Čerčanská 2023/12, Krč, 140 00 Praha 4

Zhotovitel:



Valbek, spol. s r.o.
Vaňurova 505/17
460 07 Liberec 3

	Vypracoval A. BARTONIČKOVÁ		Zak. číslo 21-L113-001
	Zodp. projektant ING. T. KLIMENT		Datum 02/2025
	Tech. kontrola ING. M. HANŽL		Stupeň PDPs
	Akce I/16 MLADÁ BOLESLAV - MARTINOVICE		Počet formátů 10 x A4
Zhotovitel: Valbek, spol. s r.o. Vaňurova 505/17 460 07 Liberec 3	Příloha ŘÁMOVÝ PROPUSTEK 2,0 x 2,0 m V km 6,500		Měřitko 1 : 100
			Č. přílohy Paré
			6.14