



SO 101 - SILNICE I/16 MLADÁ BOLESLAV - MARTINOVICE
PROPUSTEK DN 1200 V km 7,090, M 1 : 100


PŮDORYS

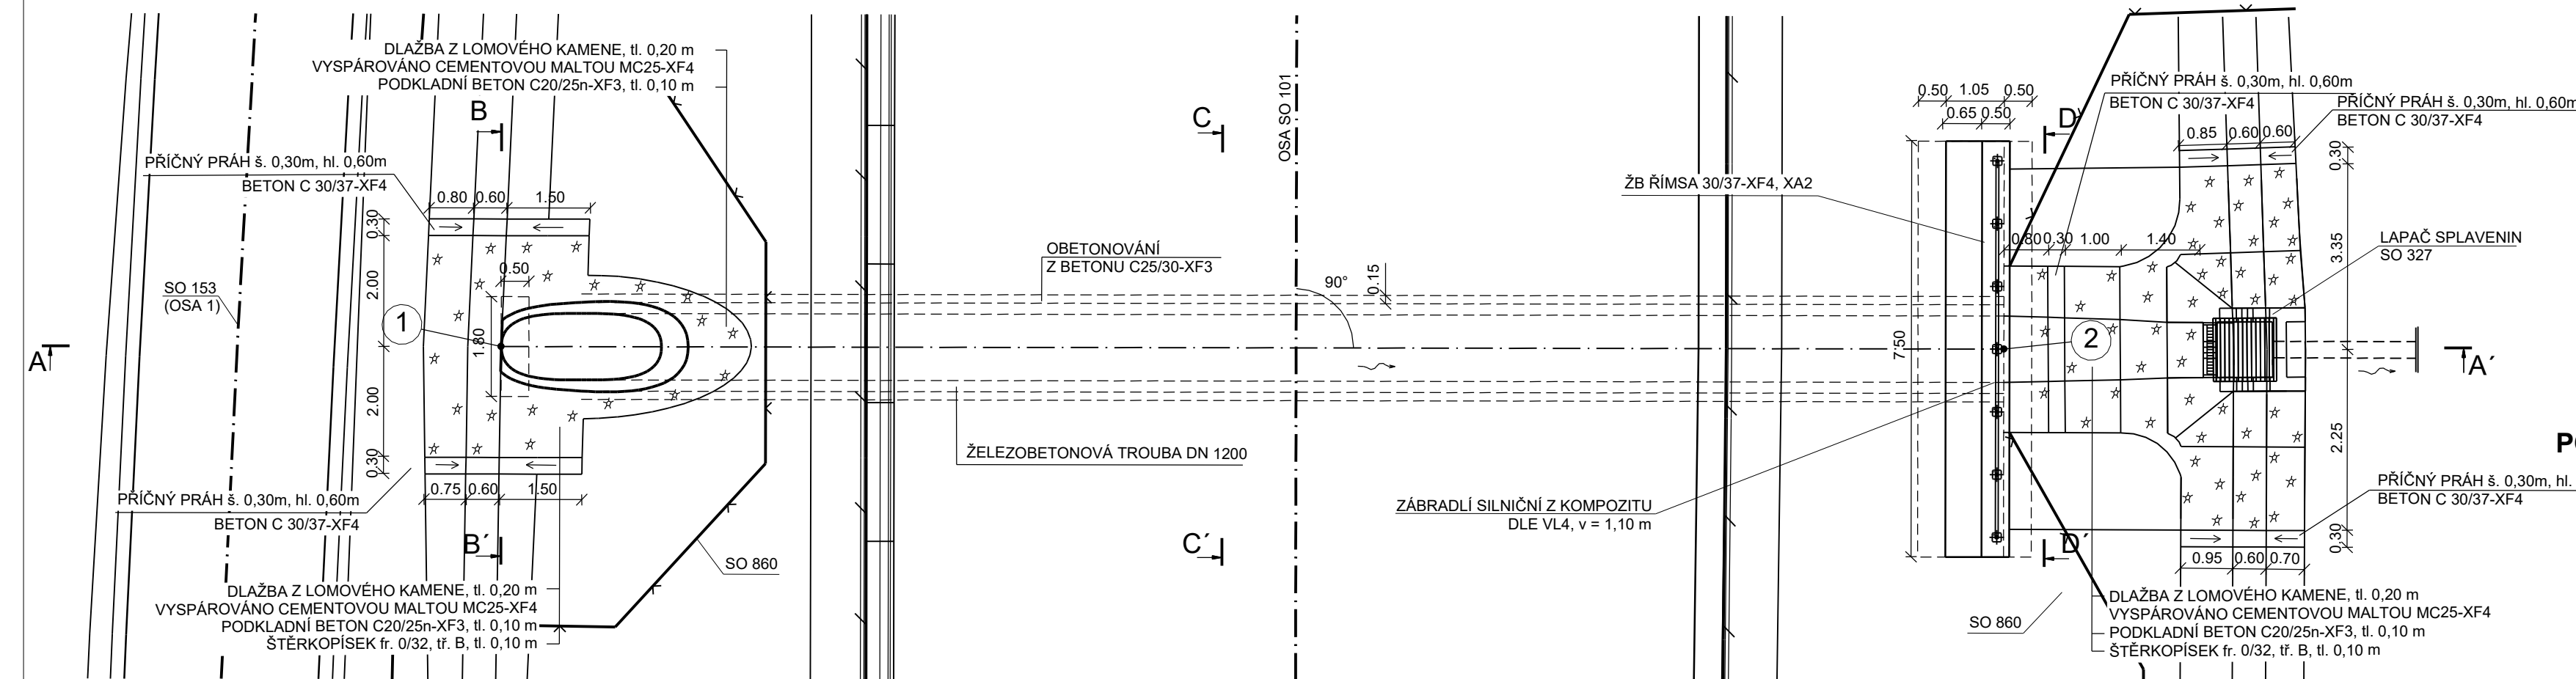


PODÉLNÝ ŘEZ A-A

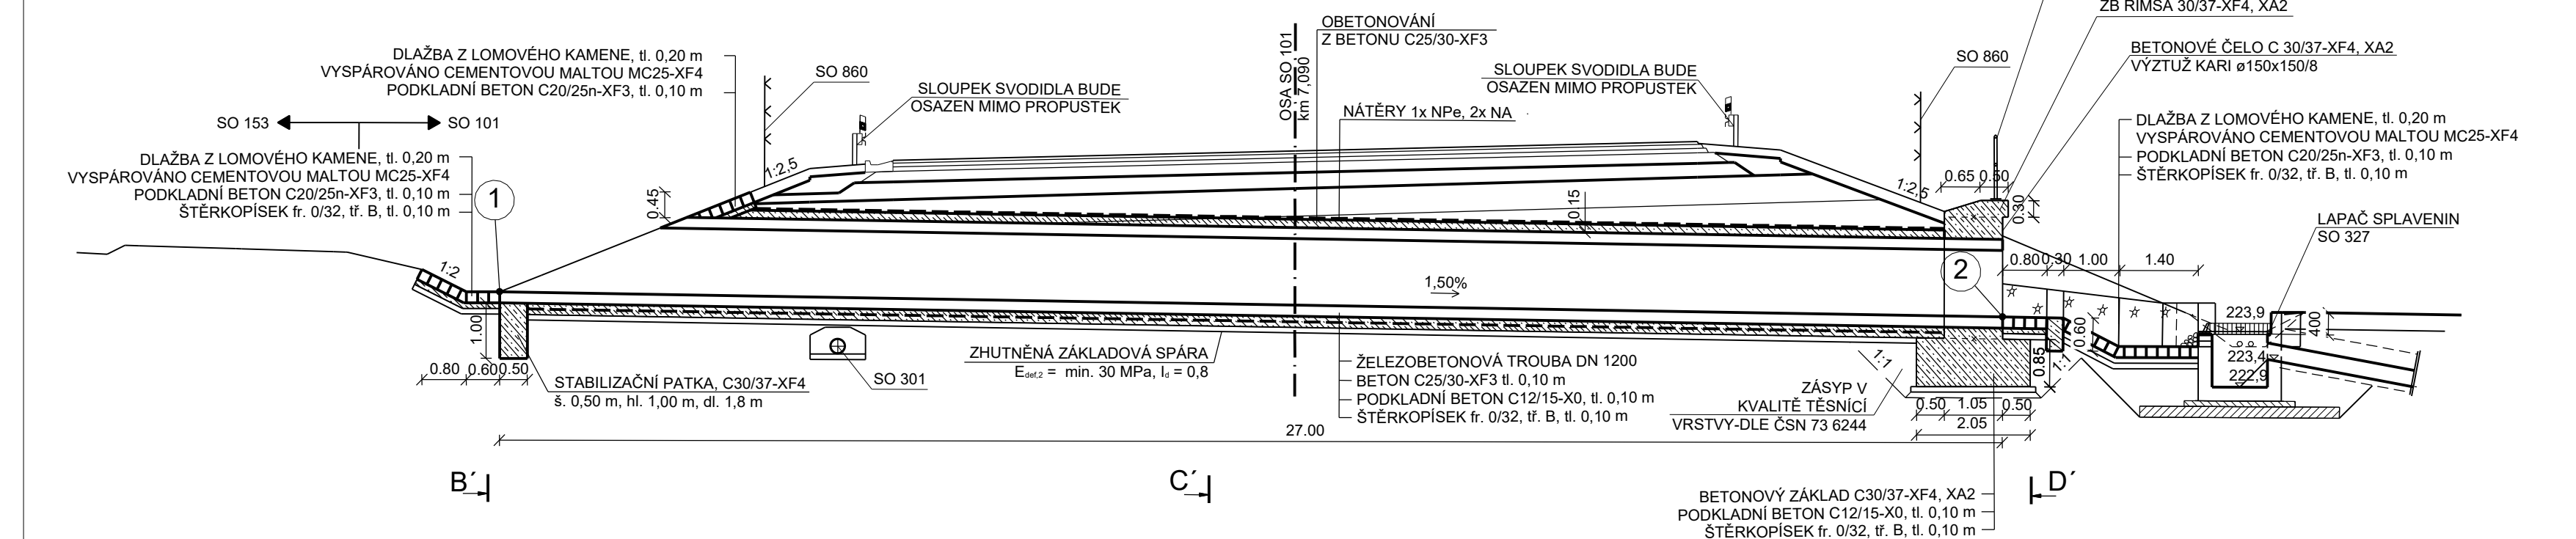


POHLED NA VTOK ŘEZ B-B

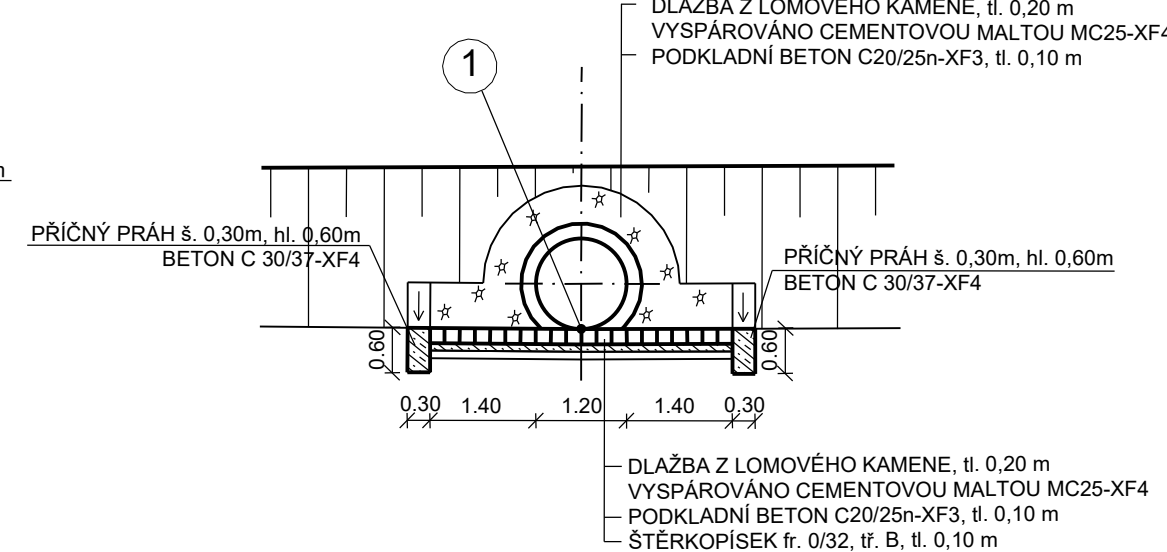

POHLED NA VÝTOK ŘEZ D-D'

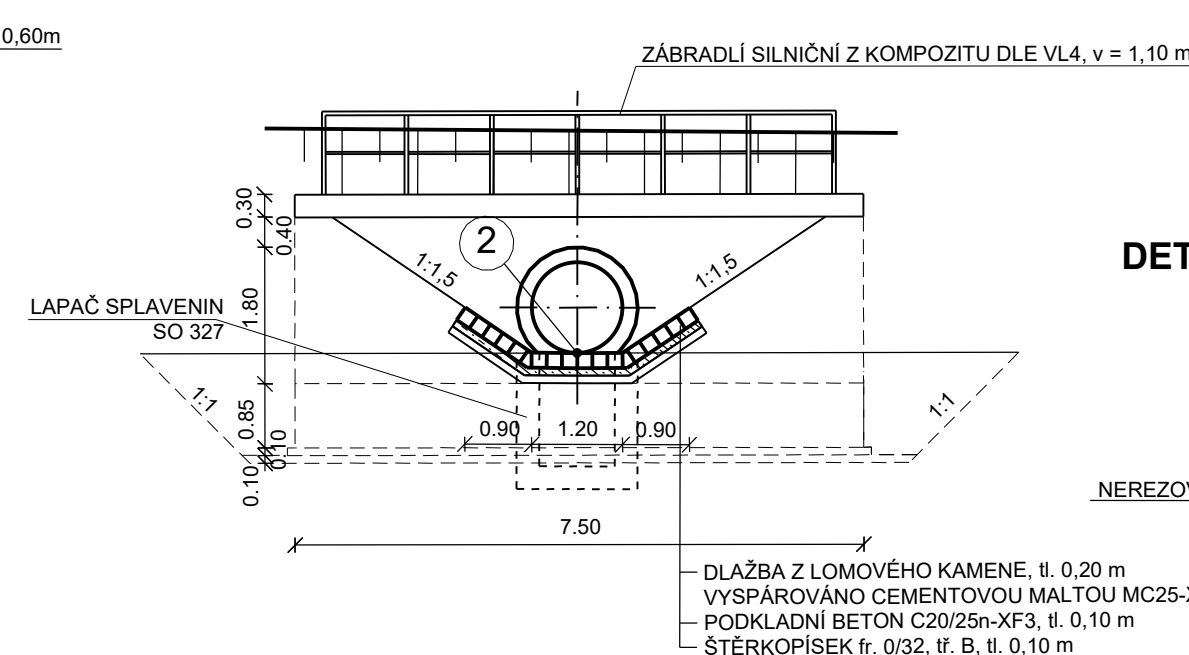


PŘÍČNÝ ŘEZ C-C'

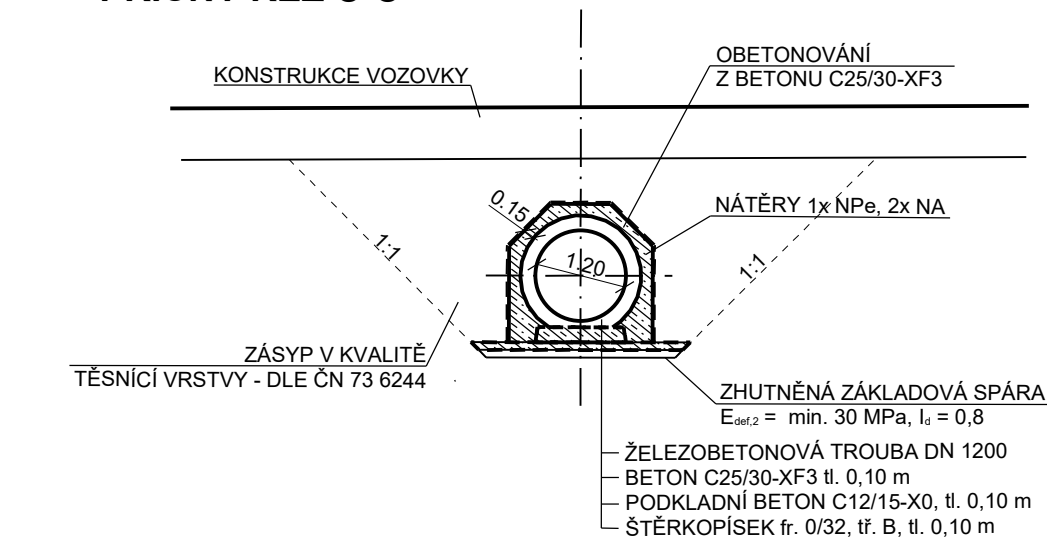


POZNÁMKY:

- SPÁROVÁNÍ DLAŽBY Z LOMOVÉHO KAMENE BUDE VYPLNĚNÉ CEMENTOVOU MALTOU MC25-XF4, tl. min. 0,20 m
- OBETONOVÁNÍ V MÍSTĚ HRDLA MINIMÁLNĚ 0,10 m
- VŠECHNY BETONOVÉ PRVKY, KTERÉ PŘÍJDOU DO STYKU SE ZEMINOU MUSÍ BÝT OPATŘENY NATĚRY: 1x NpE a 2x NA
- POČET PRAHŮ ZÁVISÍ NA TYPU ZVOLENÉ TROUBY A JEJÍHO ULOŽENÍ
- VYTÝČENÍ BUDE PROVEDENO DLE TKP 1 A SOUVISEJÍCÍCH PŘEDPISŮ
- POKUD SVAHŮ JSOU URČENY SKLONEM SILNIČNÍHO TĚLESA A PŘÍLEHLÝCH PŘÍKOPŮ
- POKUD NEBUDOU NA KRAJÍCH OSAZENY ŠIKMÉ PREFABRIKÁTY, BUDOU PRO SĚRŽITNUTÍ POUŽITY BETONOVÉ TROUBY (Z DŮVODU KORODUJÍCÍ VÝTŽUŽE)
- ŠÍŘE PODKLADNÍHO PRAHU JE 0,50 m NA KAŽDOU STRANU OD VNĚJŠÍHO OBRYSU TROUBY
- BETONOVÉ VÝROBKY VYSTAVĚNÉ PŘÍMÉMU OSTRŮKU ROZMARZOVACÍCH PROSTŘEDKŮ A MRAZU A UMÍSTĚNÉ VE VZDÁLENOSTI MOŽNÉHO OSTRŮKU (OD HRANY VOZOVKY 10 m VČETNĚ SOLNÉ MLHY) MUSÍ SPLŇOVAT POŽADAVKY NA STUPĚN VLIVU PROSTŘEDÍ XF4.
- MUSÍ BÝT ZAJIŠTĚNA KOORDINACE STAVEBNÍCH PRACÍ VÝSTAVBY PROPUSTKŮ A KANALIZACE V MÍSTĚ JEJICH KŘÍŽENÍ.

DETAIL UKOTEVNÍ, M 1:10

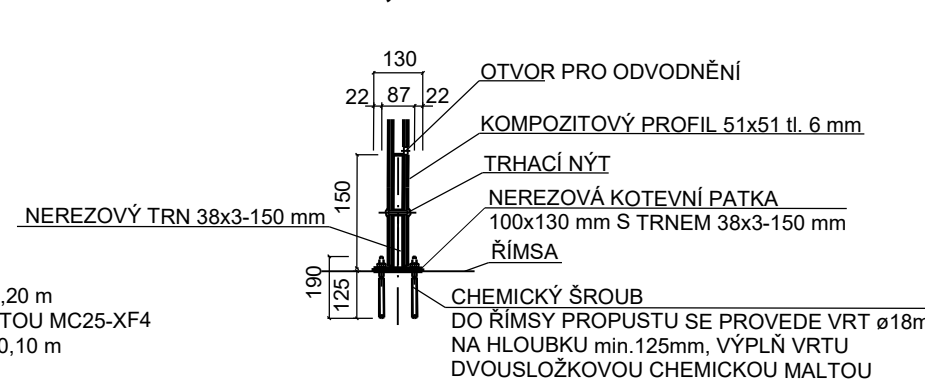

DETAIL KOTEVNÍ PATKY, M 1:10

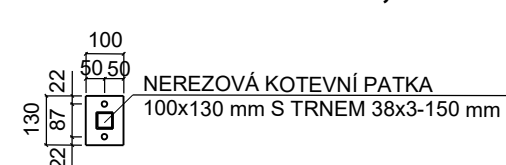

PARAMETRY PROPUSTKŮ					VYTÝČOVANÉ BODY	
STANIČENÍ [km]	TROUBA DN [mm]	DÉLKA DL [m]	SKLON S: [%]	ÚHEL α [°]	VÝTOK - 01 Y / X [S-JTSJK] / Z [BpV]	VÝTOK - 02 Y / X [S-JTSJK] / Z [BpV]
7,090	1200	27.00	1.50	90	694453,947/1010855,993/224,57	694453,836/1010883,086/224,16

Souřadnicový systém: S-JTSK
Výškový systém: Bpv

SO 101	Silnice I/16 Mladá Boleslav - Martinovice
---------------	---

Objednatel: ŘEDITELSTVÍ SILNIC A DÁLNIC	Ředitelství silnic a dálnic s. p. Čerčanská 2023/12, Krč, 140 00 Praha 4
--	--

Zhotovitel: 	Valbek, spol. s r.o. Vaňurova 505/17 460 07 Liberec 3
--	---

	Vypracoval	A. BARTONIČKOVÁ		Zak. číslo	21-LI13-001
	Zodp. projektant	ING. T. KLIMENT		Datum	02/2025
	Tech. kontrola	ING. M. HANŽL		Stupeň	PDPS
	Akce			Počet formátů	5 x A4
	I/16 MLADÁ BOLESLAV - MARTINOVICE			Měřítko	1 : 100
Č. přílohy				Paré	
6.15					
		Zhotovitel: Valbek, spol. s r.o. Vařutova 505/17 460 07 Liberec 3	Příloha PROPUSTEK DN 1200 V km 7,090		