


SO 101 - SILNICE I/16 MLADÁ BOLESLAV - MARTINOVICE


SANAČNÍ OPATŘENÍ, M 1 : 100

SANACE PODLOŽÍ NÁSYPU - TYP I

SANACE N.1	PLATÍ V km 0,000 - 0,220 (km 0,000 - 0,218 úsek N1 DLE GTP)	SANACE N.12	PLATÍ V km 3,800 - 4,460 (km 3,820 - km 3,798 - 4,480 ÚSEK N12 DLE GTP)
SANACE N.2	PLATÍ V km 0,250 - 0,840 (km 0,252 - 0,865 úsek N2 DLE GTP)	SANACE N.14	PLATÍ V km 4,940 - 5,040 (km 4,920 - 5,041 úsek N14 DLE GTP) *
SANACE N.4	PLATÍ V km 1,340 - 1,780 (km 1,270 - 1,795 úsek N4 DLE GTP)	SANACE N.15	PLATÍ V km 5,060 - 5,140 (km 5,055 - 5,150 úsek N15 DLE GTP) *
SANACE N.6	PLATÍ V km 2,120 - 2,680 (km 2,105 - 2,685 úsek N6 DLE GTP)	SANACE N.18	PLATÍ V km 6,040 - 6,060, km 6,100 - 6,690 (km 6,077 - 6,680 úsek N18 DLE GTP)
SANACE N.7	PLATÍ V km 2,680 - 2,760 (km 2,703 - 2,745 úsek N7 DLE GTP)	SANACE N.19	PLATÍ V km 6,715 - 6,760 (km 6,716 - 6,780 úsek N19 DLE GTP)
SANACE N.9	PLATÍ V km 3,040 - 3,220 (km 3,035 - 3,235 úsek N9 DLE GTP)	SANACE N.21	PLATÍ V km 6,980 - 7,140 (km 6,960 - 7,150 úsek N21 DLE GTP)
SANACE N.11	PLATÍ V km 3,420 - 3,780 (km 3,415 - 3,784 úsek N11 DLE GTP)		

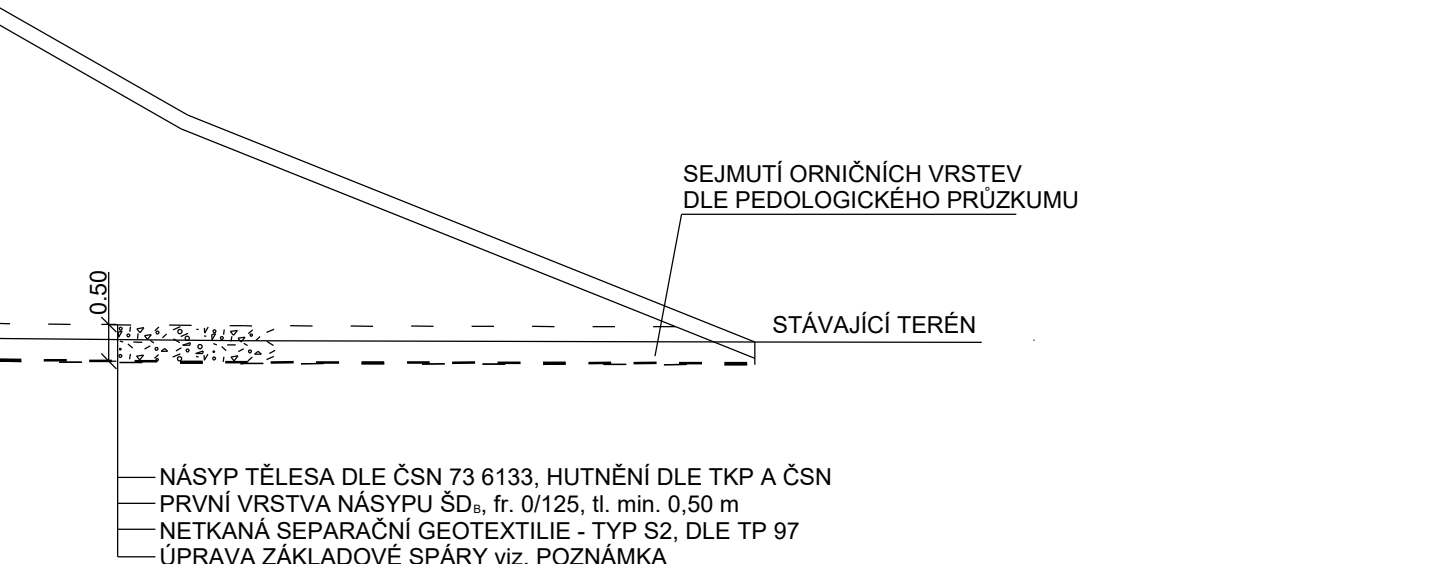


SANACE PODLOŽÍ NÁSYPU - TYP II

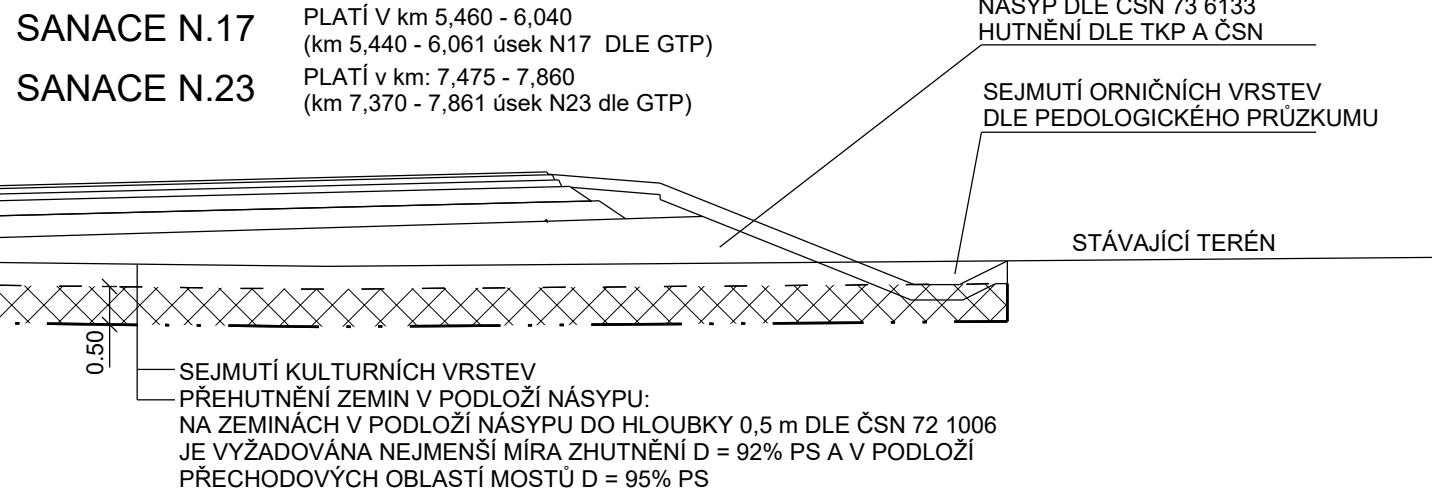


SANACE ZÁŘEZU - TYP III

SANACE Z.3	PLATÍ v km 0,860 - 1,340 (km 0,865 - 1,270 úsek Z3 dle GTP)	SANACE Z.13	PLATÍ v km: 4,480 - 4,920 (km 4,480 - 4,920 úsek Z13 dle GTP)
SANACE Z.5	PLATÍ v km: 1,780 - 2,120 (km 1,795 - 2,105 úsek Z5 dle GTP)	SANACE Z.20	PLATÍ v km: 6,780 - 6,960 (km 6,780 - 6,960 úsek Z20 dle GTP)
SANACE Z.8	PLATÍ v km: 2,760 - 3,020 (km 2,745 - 3,035 úsek Z8 dle GTP)	SANACE Z.22	PLATÍ v km: 7,160 - 7,360 (km 7,150 - 7,370 (úsek Z22 dle GTP)
SANACE UT.10	PLATÍ v km: 3,240 - 3,400 (km 3,235 - 3,415 úsek ÚT10 dle GTP)	SANACE N.23	PLATÍ v km: 7,380 - 7,475 (km 7,370 - 7,861 úsek N23 dle GTP)

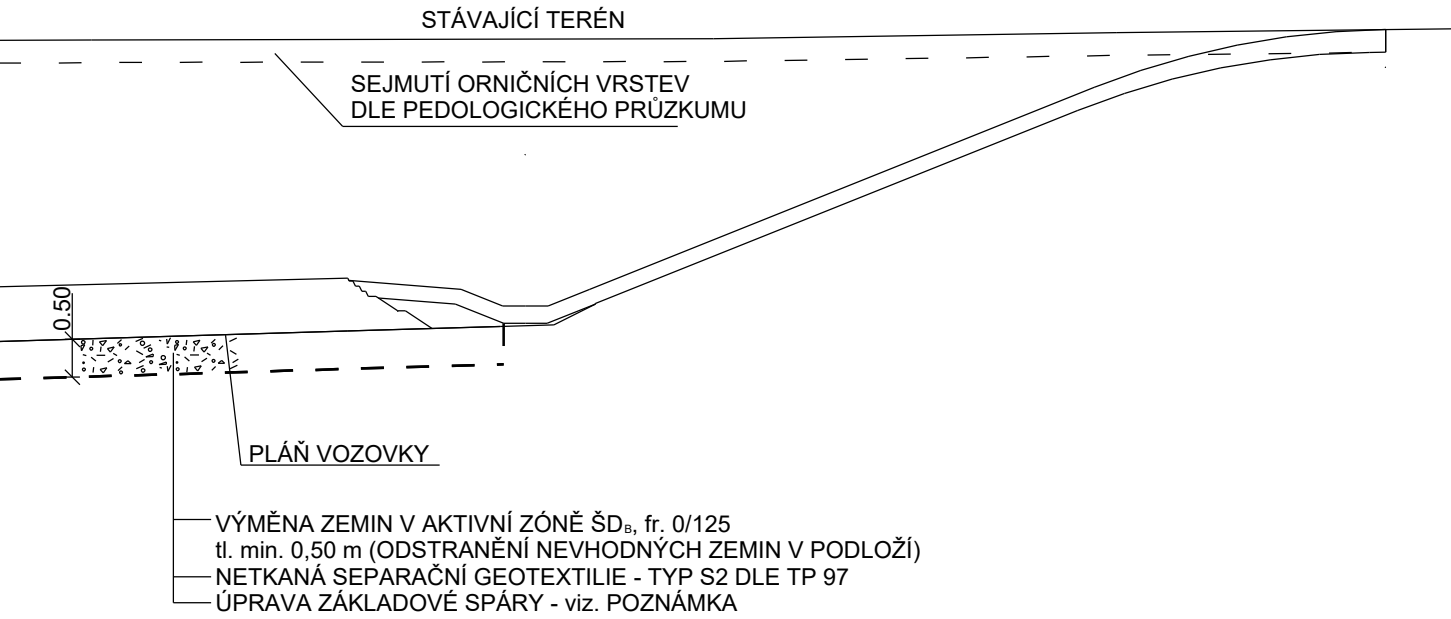

SANACE PODLOŽÍ V ÚROVNI TERÉNU - TYP IV

SANACE UT.16	PLATÍ v km: 5,160 - 5,440 (km 5,150 - 5,440 úsek ÚT16 dle GTP)
SANACE UT.24	PLATÍ v km: 7,877 - 8,200 (km 7,877 - 8,200 úsek ÚT24 dle GTP) *

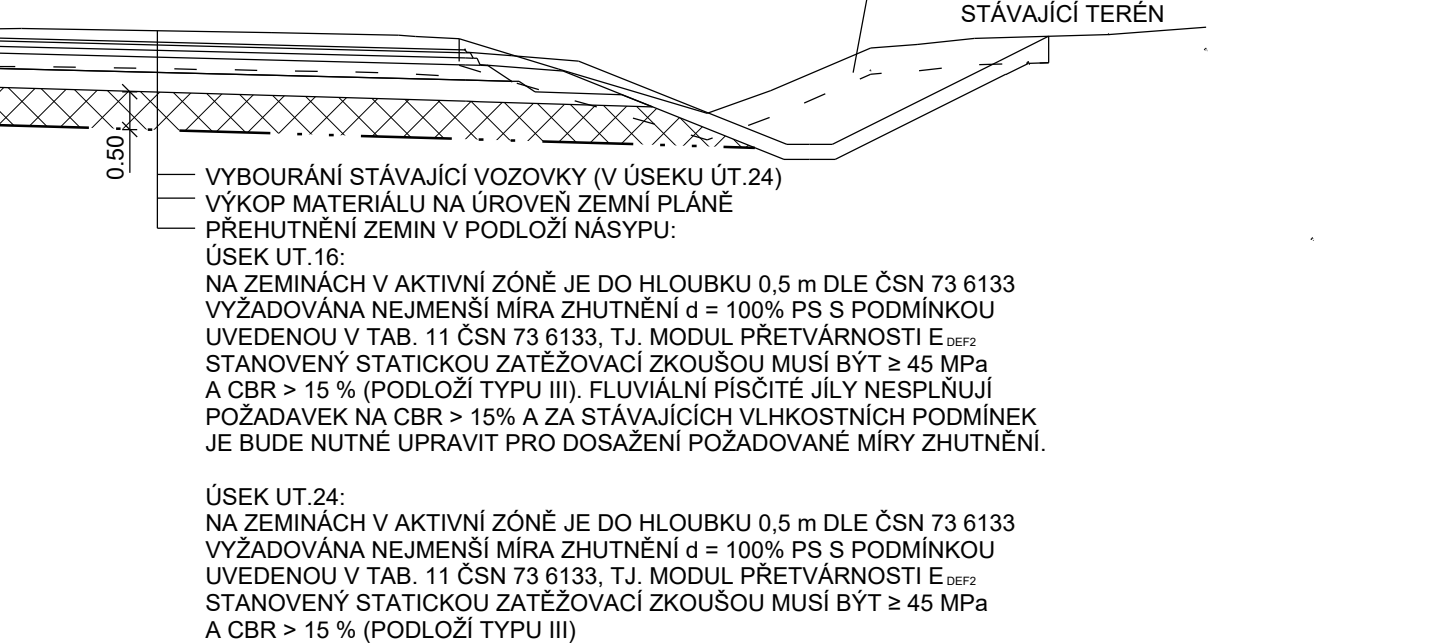

* V ÚSEKU UT.24 v km 7,877 - 8,060 BUDE PROVEDENO DOPLNĚNÍ AKTIVNÍ ZÓNY MIMO STÁVAJÍCÍ SILNIČNÍ TĚLESO,

POZNÁMKA:

POŽADOVANÁ MÍRA ZHUTNĚNÍ NA PRVNÍ SANAČNÍ VRSTVĚ NÁSYPU: HUTNĚNÍ DLE ČSN 73 6133 A TKP, I_o = 0,75, E_{def12} = min 30 MPa, E_{def12} ≤ 3,0 ZKOUŠENÍ A ČETNOST DLE ČSN 73 6133 TABULKA 10a, DOPORUČUJE SE OVĚRIT ZHUŤNOVACÍ ZKOUŠKOU

POŽADOVANÁ MÍRA ZHUTNĚNÍ NA ZÁKLADOVÉ SPÁŘE NÁSYPU: HUTNĚNÍ DLE ČSN 73 6133 A TKP, D=92 % PS (95% PS V PŘECHODOVÝCH OBLASTECH MOSTŮ), IBI min 5% ZKOUŠENÍ A ČETNOST DLE ČSN 73 6133 TABULKA 10a, DOPORUČUJE SE OVĚRIT ZHUŤNOVACÍ ZKOUŠKOU

POŽADOVANÁ MÍRA ZHUTNĚNÍ NÁSYPOVÉHO TĚLESA: HUTNĚNÍ DLE ČSN 73 6133 A TKP, PŘI POUŽITÍ JEMNOZRNÝCH NEBO PÍŠČITÝCH ZEMIN D ≥ 95% PS, NEBO I_o ≥ 0,80, PŘI POUŽITÍ ŠTĚRKOVITÝCH ZEMIN D ≥ 97% PS, NEBO I_o ≥ 0,75 ZKOUŠENÍ A ČETNOST DLE ČSN 73 6133 TABULKA 10a, DOPORUČUJE SE OVĚRIT ZHUŤNOVACÍ ZKOUŠKOU


POŽADOVANÁ MÍRA ZHUTNĚNÍ AKTIVNÍ ZÓNY/ZEMNÍ PLÁNĚ: HUTNĚNÍ DLE ČSN 73 6133 A TKP, MINIMÁLNÍ POŽADAVEK D ≥ 100% PS, NEBO PŘI POUŽITÍ PÍŠČITÝCH ZEMIN I_o ≥ 0,90, PŘI POUŽITÍ ŠTĚRKOVITÝCH ZEMIN I_o ≥ 0,85 ZKOUŠENÍ A ČETNOST DLE ČSN 73 6133 TABULKA 10a, DOPORUČUJE SE OVĚRIT ZHUŤNOVACÍ ZKOUŠKOU

PŘI SKLONU STÁVAJÍCÍHO TERÉNU, KOLMÉHO NA OSU NÁSYPU, VĚTŠÍHO NEŽ 10 %, MUSÍ BÝT ZŘÍZENY V PODLOŽÍ NÁSYPU STUPNĚ V SOULADU S VL 1 32-02

SKUTEČNÝ ROZSAH JEDNOTLIVÝCH SANAČNÍCH ÚSEKŮ MŮŽE BÝT UPŘESNĚN GEOTECHNIKEM ZHOTOVITELE NA ZÁKLADĚ SKUTEČNOSTI NA STAVBĚ A NA ZÁKLADĚ VLASTNOSTÍ SKUTEČNĚ SE VYSKYTUJÍCÍCH ZEMIN, KONEČNÁ ÚPRAVA SANAČÍ BUDE PROVEDENA PO DOHODĚ INVESTORA, ZHOTOVITELE A GEOTECHNIKA

SANAČNÍ OPATŘENÍ JSOU PODROBNĚ POPSÁNA - viz. TECHNICKÁ ZPRÁVA, kap. POPIS SANAČNÍCH OPATŘENÍ

SANACE V MÍSTĚ KORYT STÁVAJÍCÍCH VODOTEČÍ POD TĚLESEM NÁSYPU

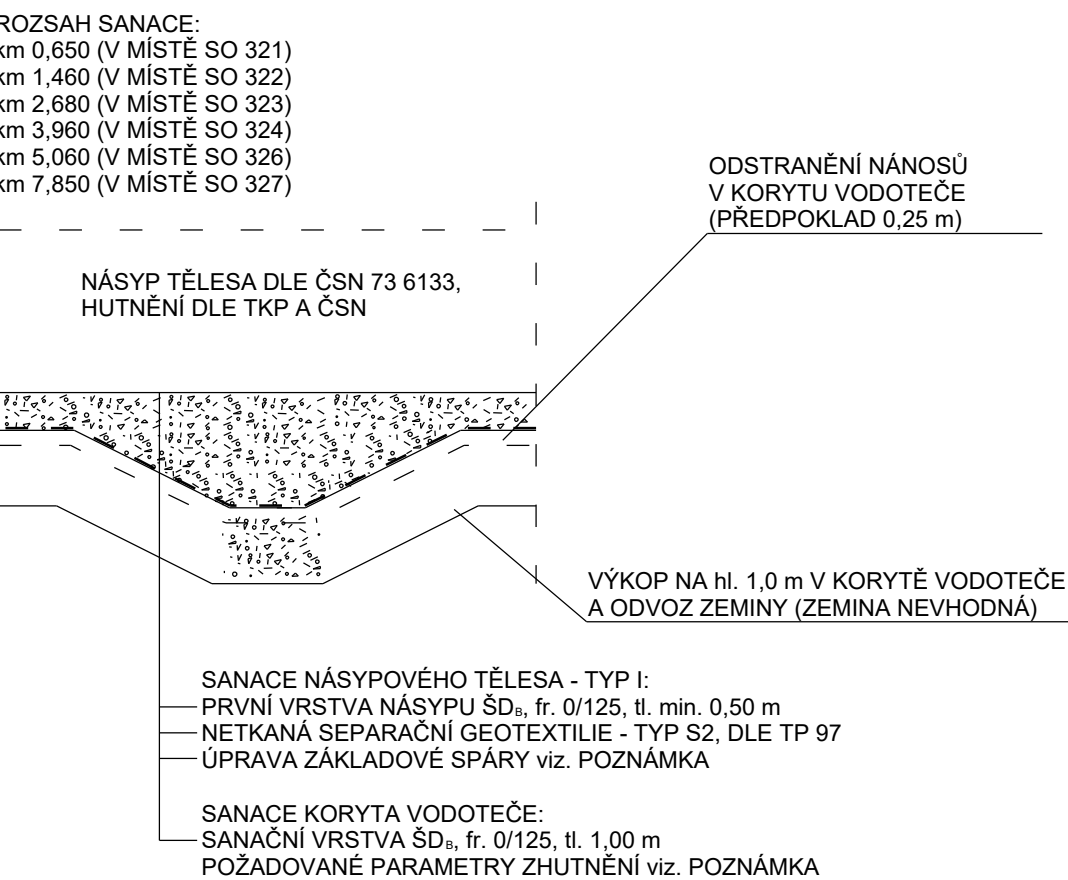

SO 101 Silnice I/16 Mladá Boleslav - Martinovice

Objednatel:	 ŘEDITELSTVÍ SILNIC A DÁLNIC	Ředitelství silnic a dálnic s. p. Čerčanská 2023/12, Krč, 140 00 Praha 4
-------------	--	--

Zhotovitel:	 Valbek	Valbek, spol. s r.o. Vaňurova 505/17 460 07 Liberec 3
-------------	---	--

	Vypracoval	ING. M. HRUBOŇ		Zak. číslo	21-L113-001
	Zodp. projektant	ING. T. KLIMENT		Datum	02/2025
	Tech. kontrola	ING. M. HANŽL		Stupeň	PDPS
	Akce I/16 MLADÁ BOLESLAV - MARTINOVICE			Počet formátů	3 x A4
				Měřitko	1 : 100
Zhotovitel: Valbek, spol. s r.o. Vaňurova 505/17 60 07 Liberec 3	Příloha SANAČNÍ OPATŘENÍ			Č. přílohy	Paré
				7	