
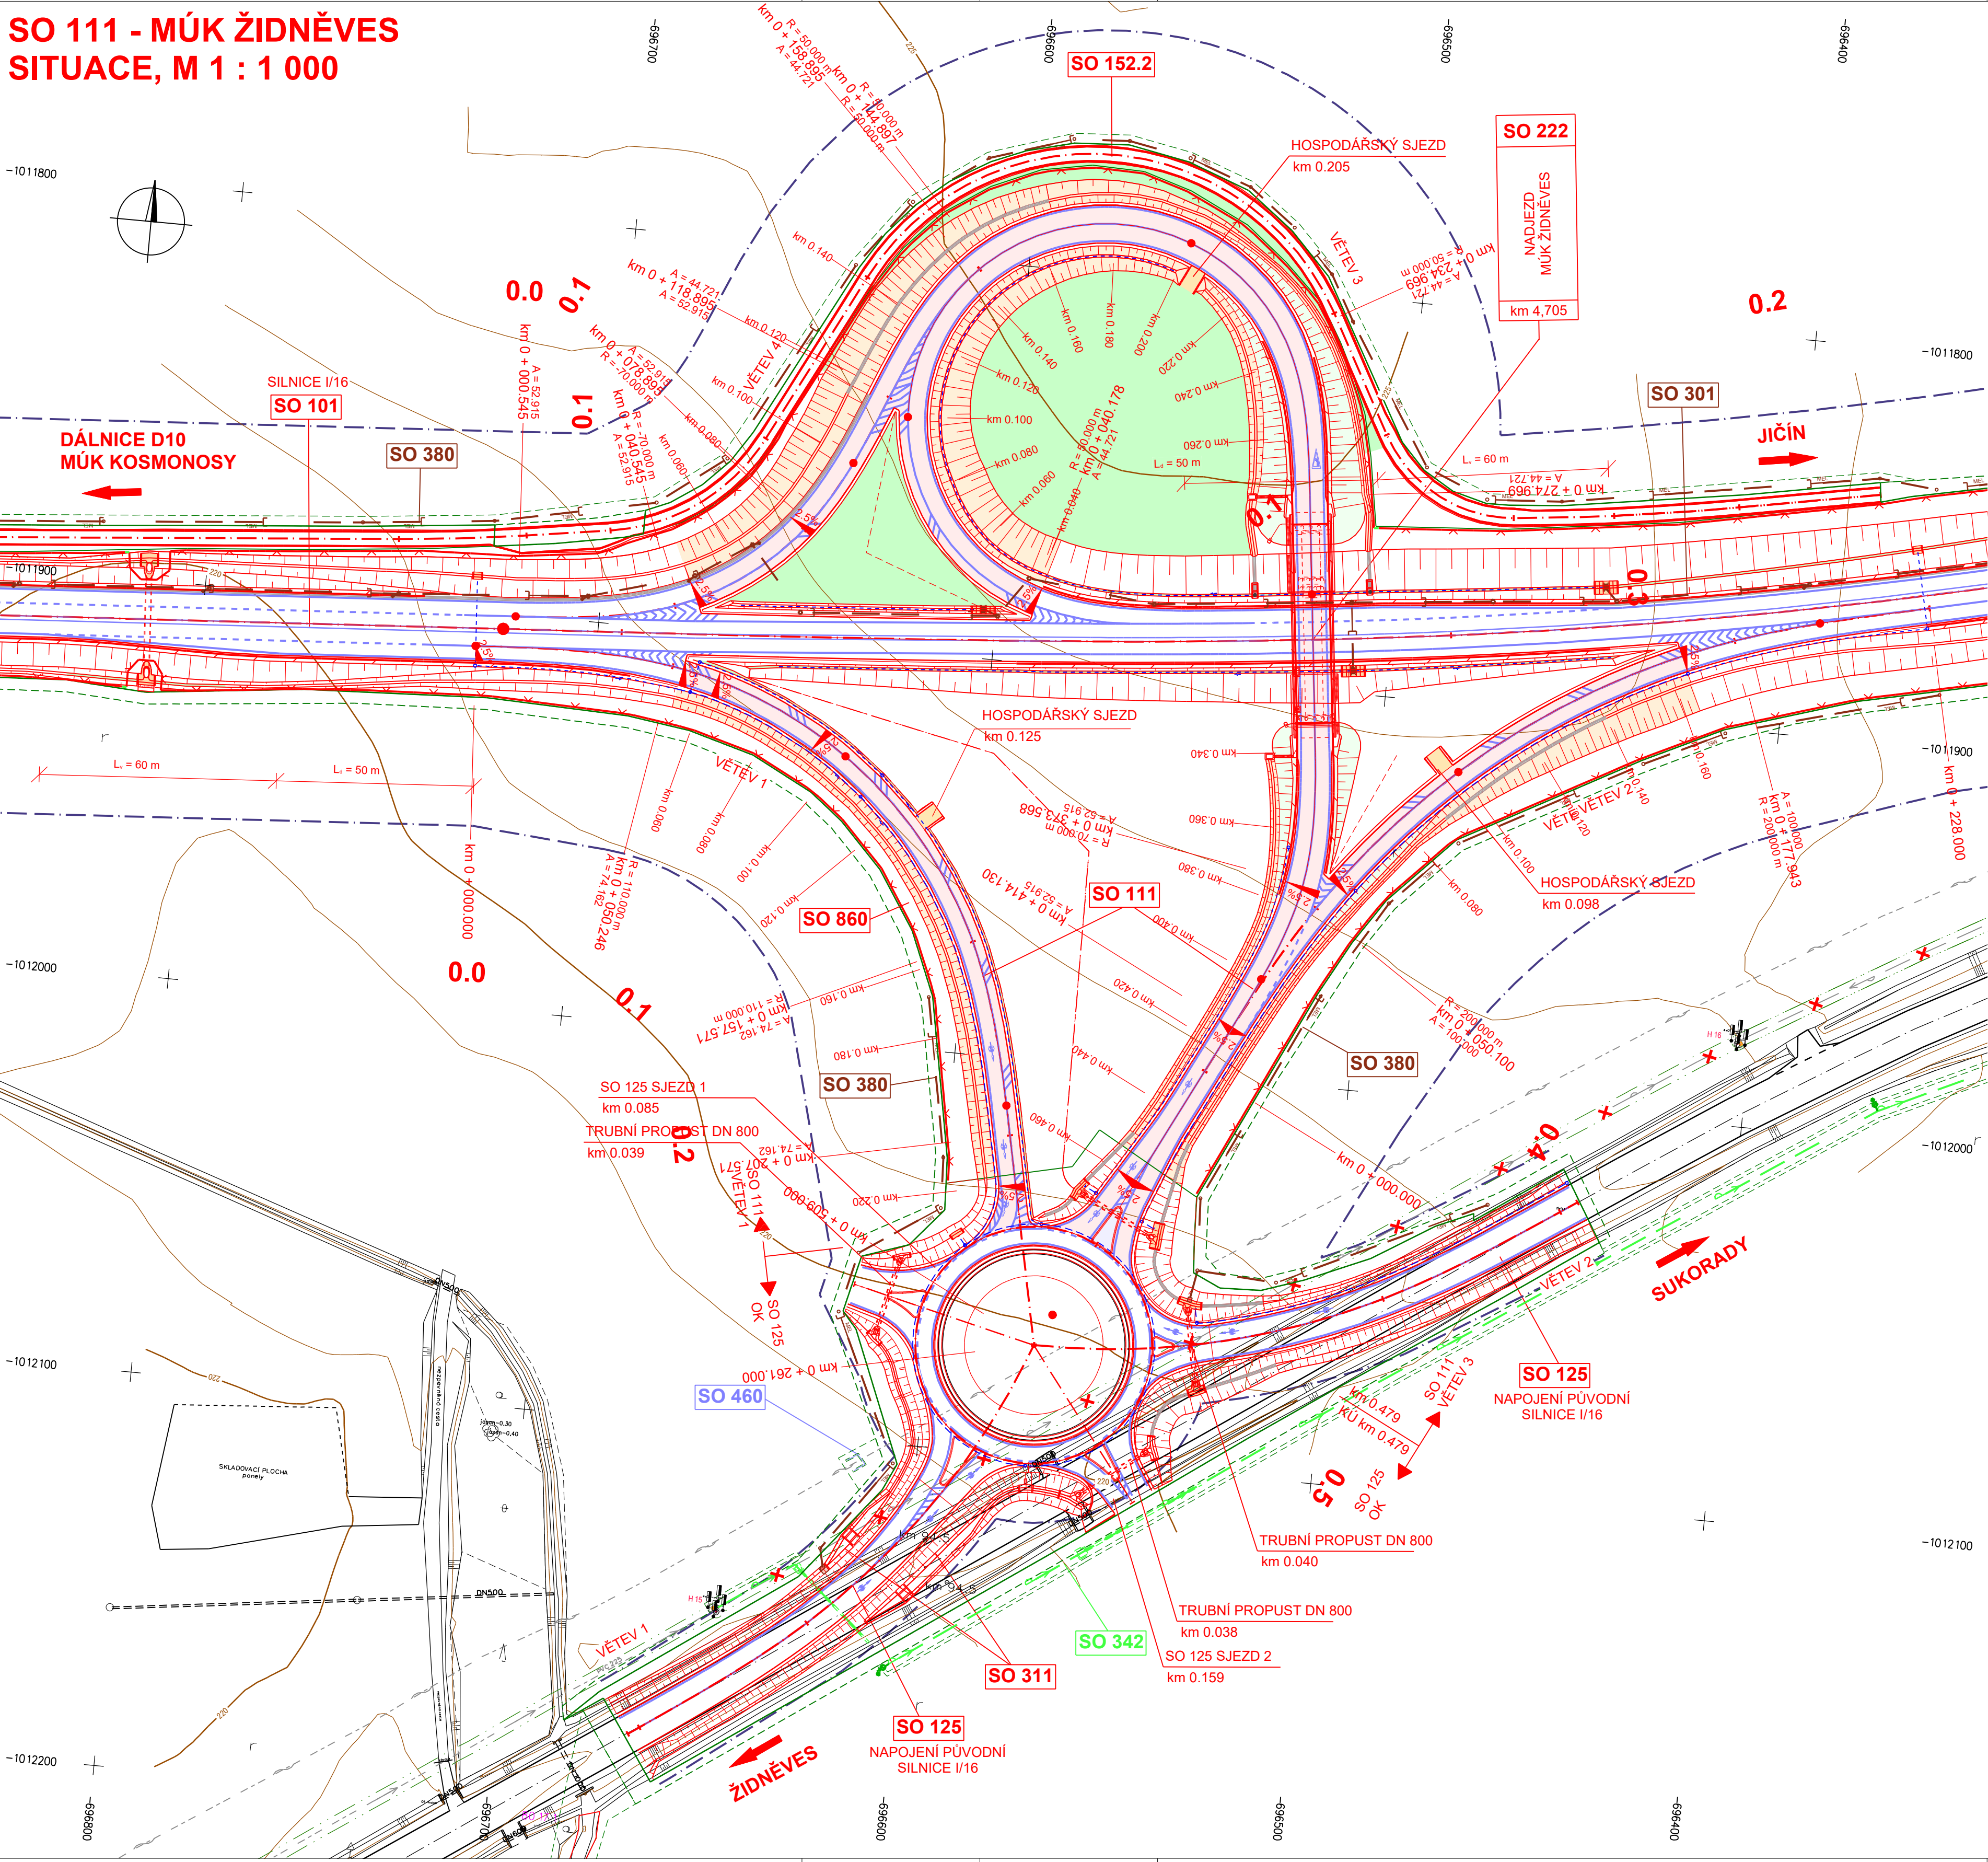
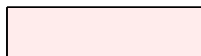
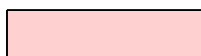
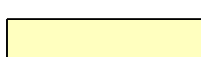
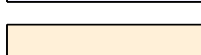
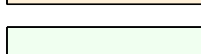


SO 111 - MÚK ŽIDNĚVES
SITUACE, M 1 : 1 000

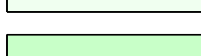

LEGENDA:			
PLOCHY		NOVÉ IS	
	VOZOVKA - ASFALTOVÝ KRYT		DEŠŤOVÁ KANALIZACE
	VOZOVKA - FRÉZOVANÁ		MELIORACE
	VOZOVKA - POLNÍ CESTY		VÝTLAK
	CHODNÍK		VODOVOD
	DLAŽBA VOZOVKY		NADZEMNÍ VEDENÍ NN
	SVAHY VÝKOPU		NADZEMNÍ VEDENÍ VN
	SVAHY NÁSYPU		PODZEMNÍ VEDENÍ NN
	VEGETAČNÍ ÚPRAVY		PODZEMNÍ SDĚLOVACÍ VEDENÍ
OBVOD STAVBY			PLYNOVOD - STL
	TRVALÝ ZÁBOR	STÁVAJÍCÍ IS - INFORMATIVNÍ ZÁKRES	
	DOČASNÝ ZÁBOR		PODZEMNÍ VEDENÍ NN
			PODZEMNÍ VEDENÍ VN
			NADZEMNÍ VEDENÍ NN
			NADZEMNÍ VEDENÍ VN
			NADZEMNÍ VEDENÍ VVN
			DEŠŤOVÁ KANALIZACE
			PLYNOVOD - STL
			PODZEMNÍ SDĚLOVACÍ VEDENÍ
			VODOVOD

Souřadnicový systém: S-JTSK

SO 111 MÚK Židněves



**ŘEDITELSTVÍ
SILNIC
A DÁLNIC**

Ředitelství silnic a dálnic s. p.
Čerčanská 2023/12, Krč, 140 00 Praha 4



Valbek

Valbek, spol. s r.o.
Vaňurova 505/17
460 07 Liberec 3

HIP:
ING. T. KLIMENT

	Vypracoval	ING. A. DUMANSKA	Zak. číslo	21-LI13-001
	Zodp. projektant	ING. T. KLIMENT	Datum	02/2025
	Tech. kontrola	ING. M. HANŽL	Stupeň	PDPS
	Akce	I/16 MLADÁ BOLESLAV - MARTINOVICE		Počet formátů
Zhotovitel: Valbek, spol. s r.o. Vaňurova 505/17 460 07 Liberec 3	Měřítko			1 : 1 000
	Příloha	SITUACE	Č. přílohy	Paré
			2	