
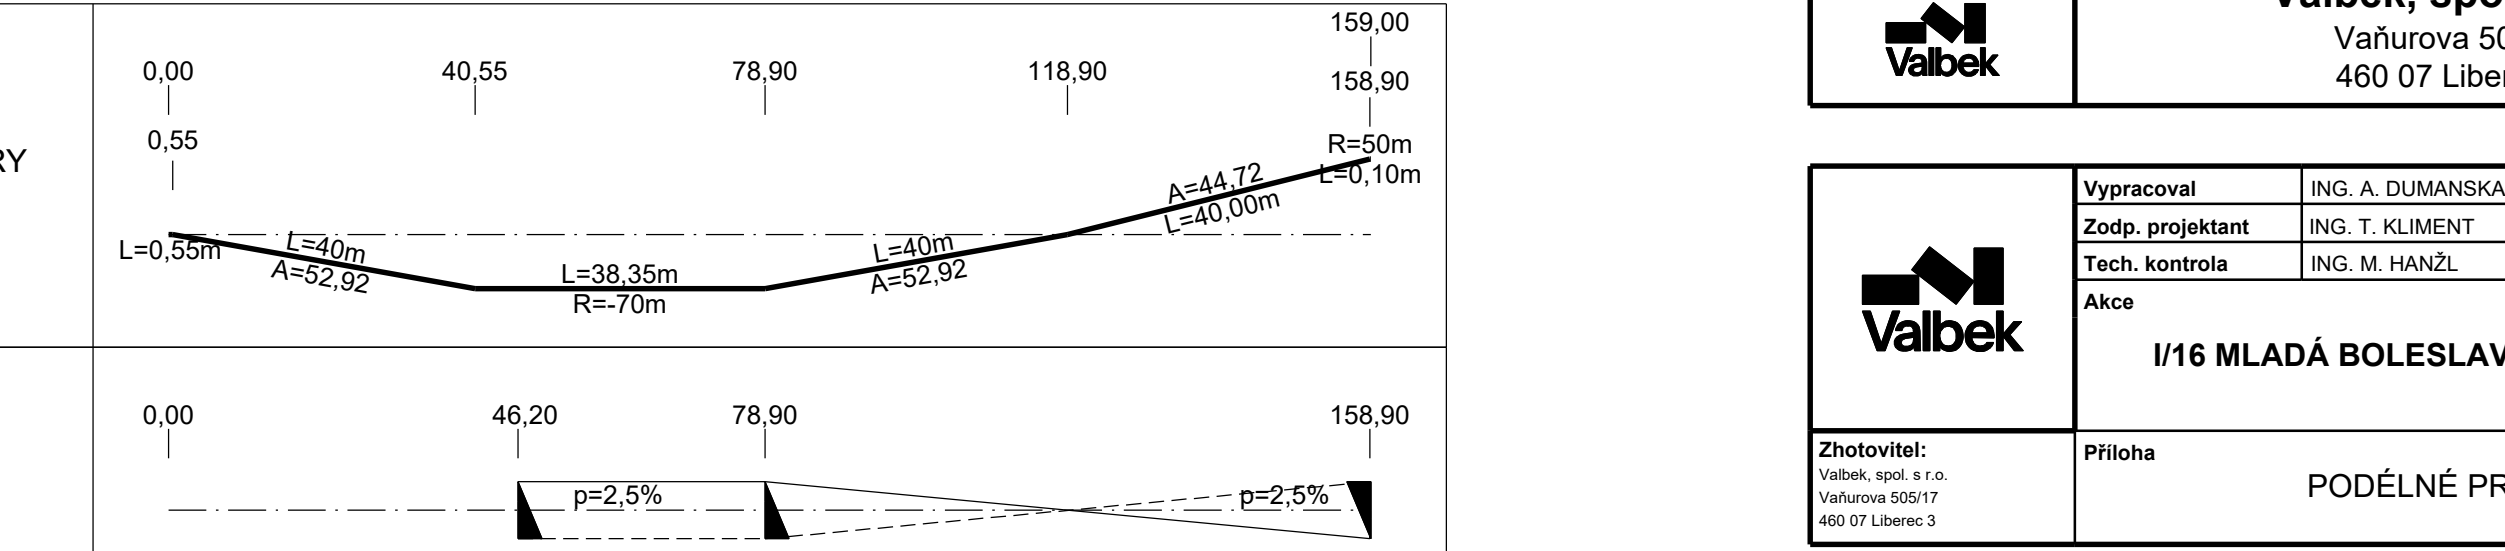
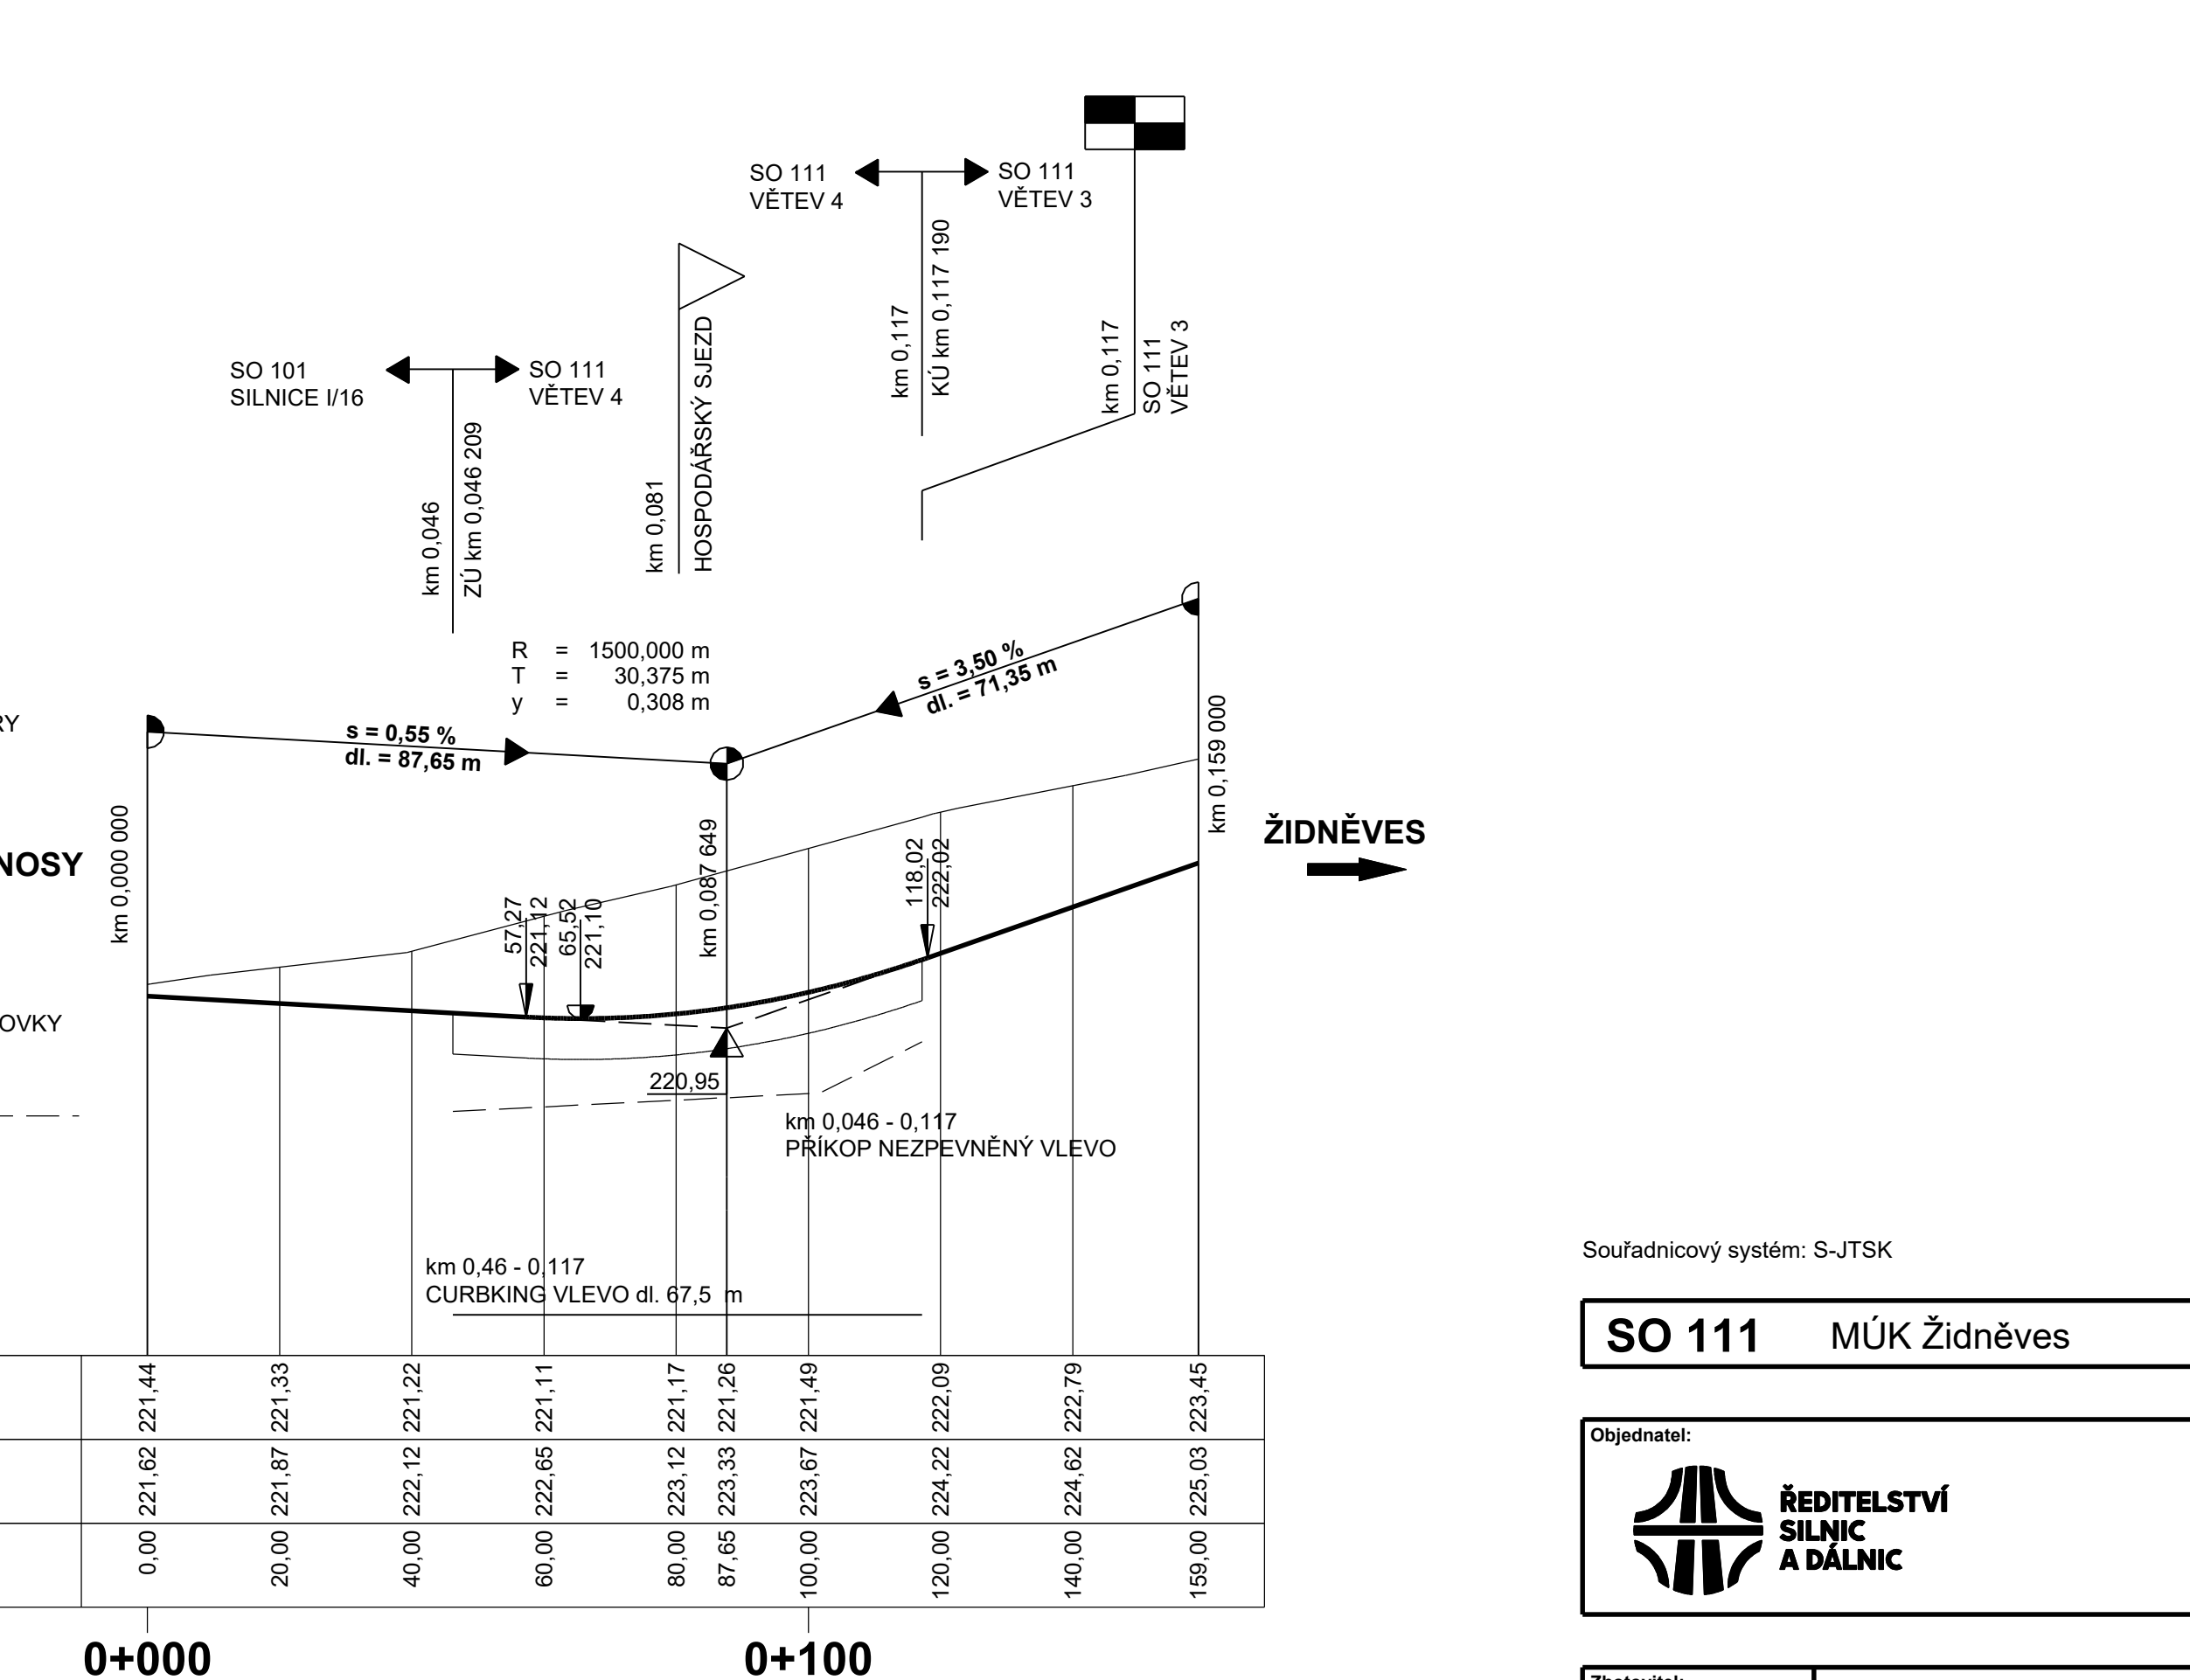
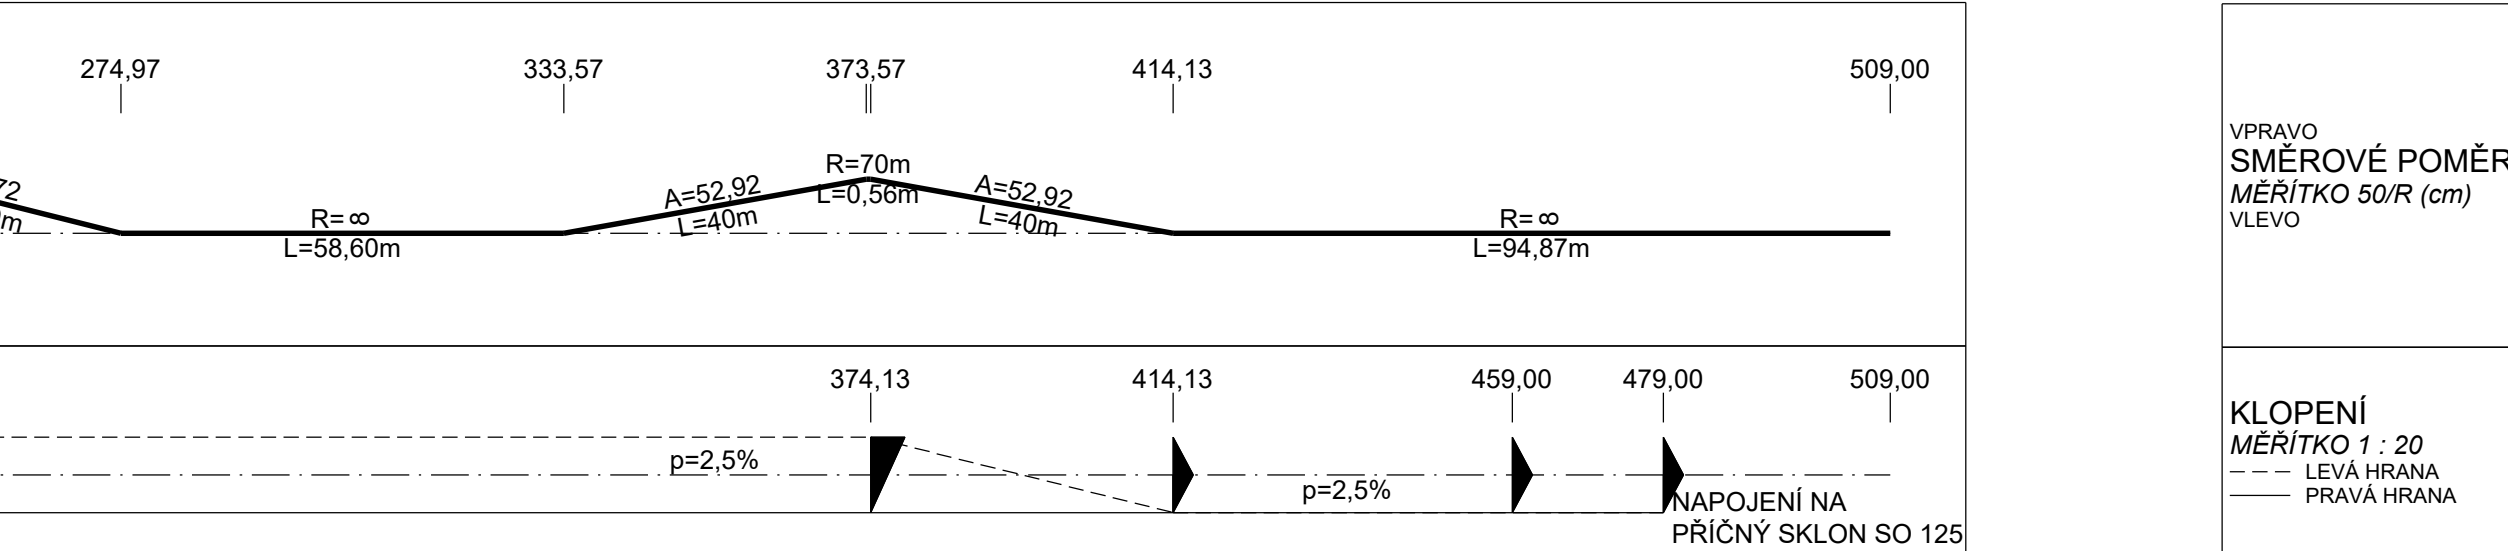
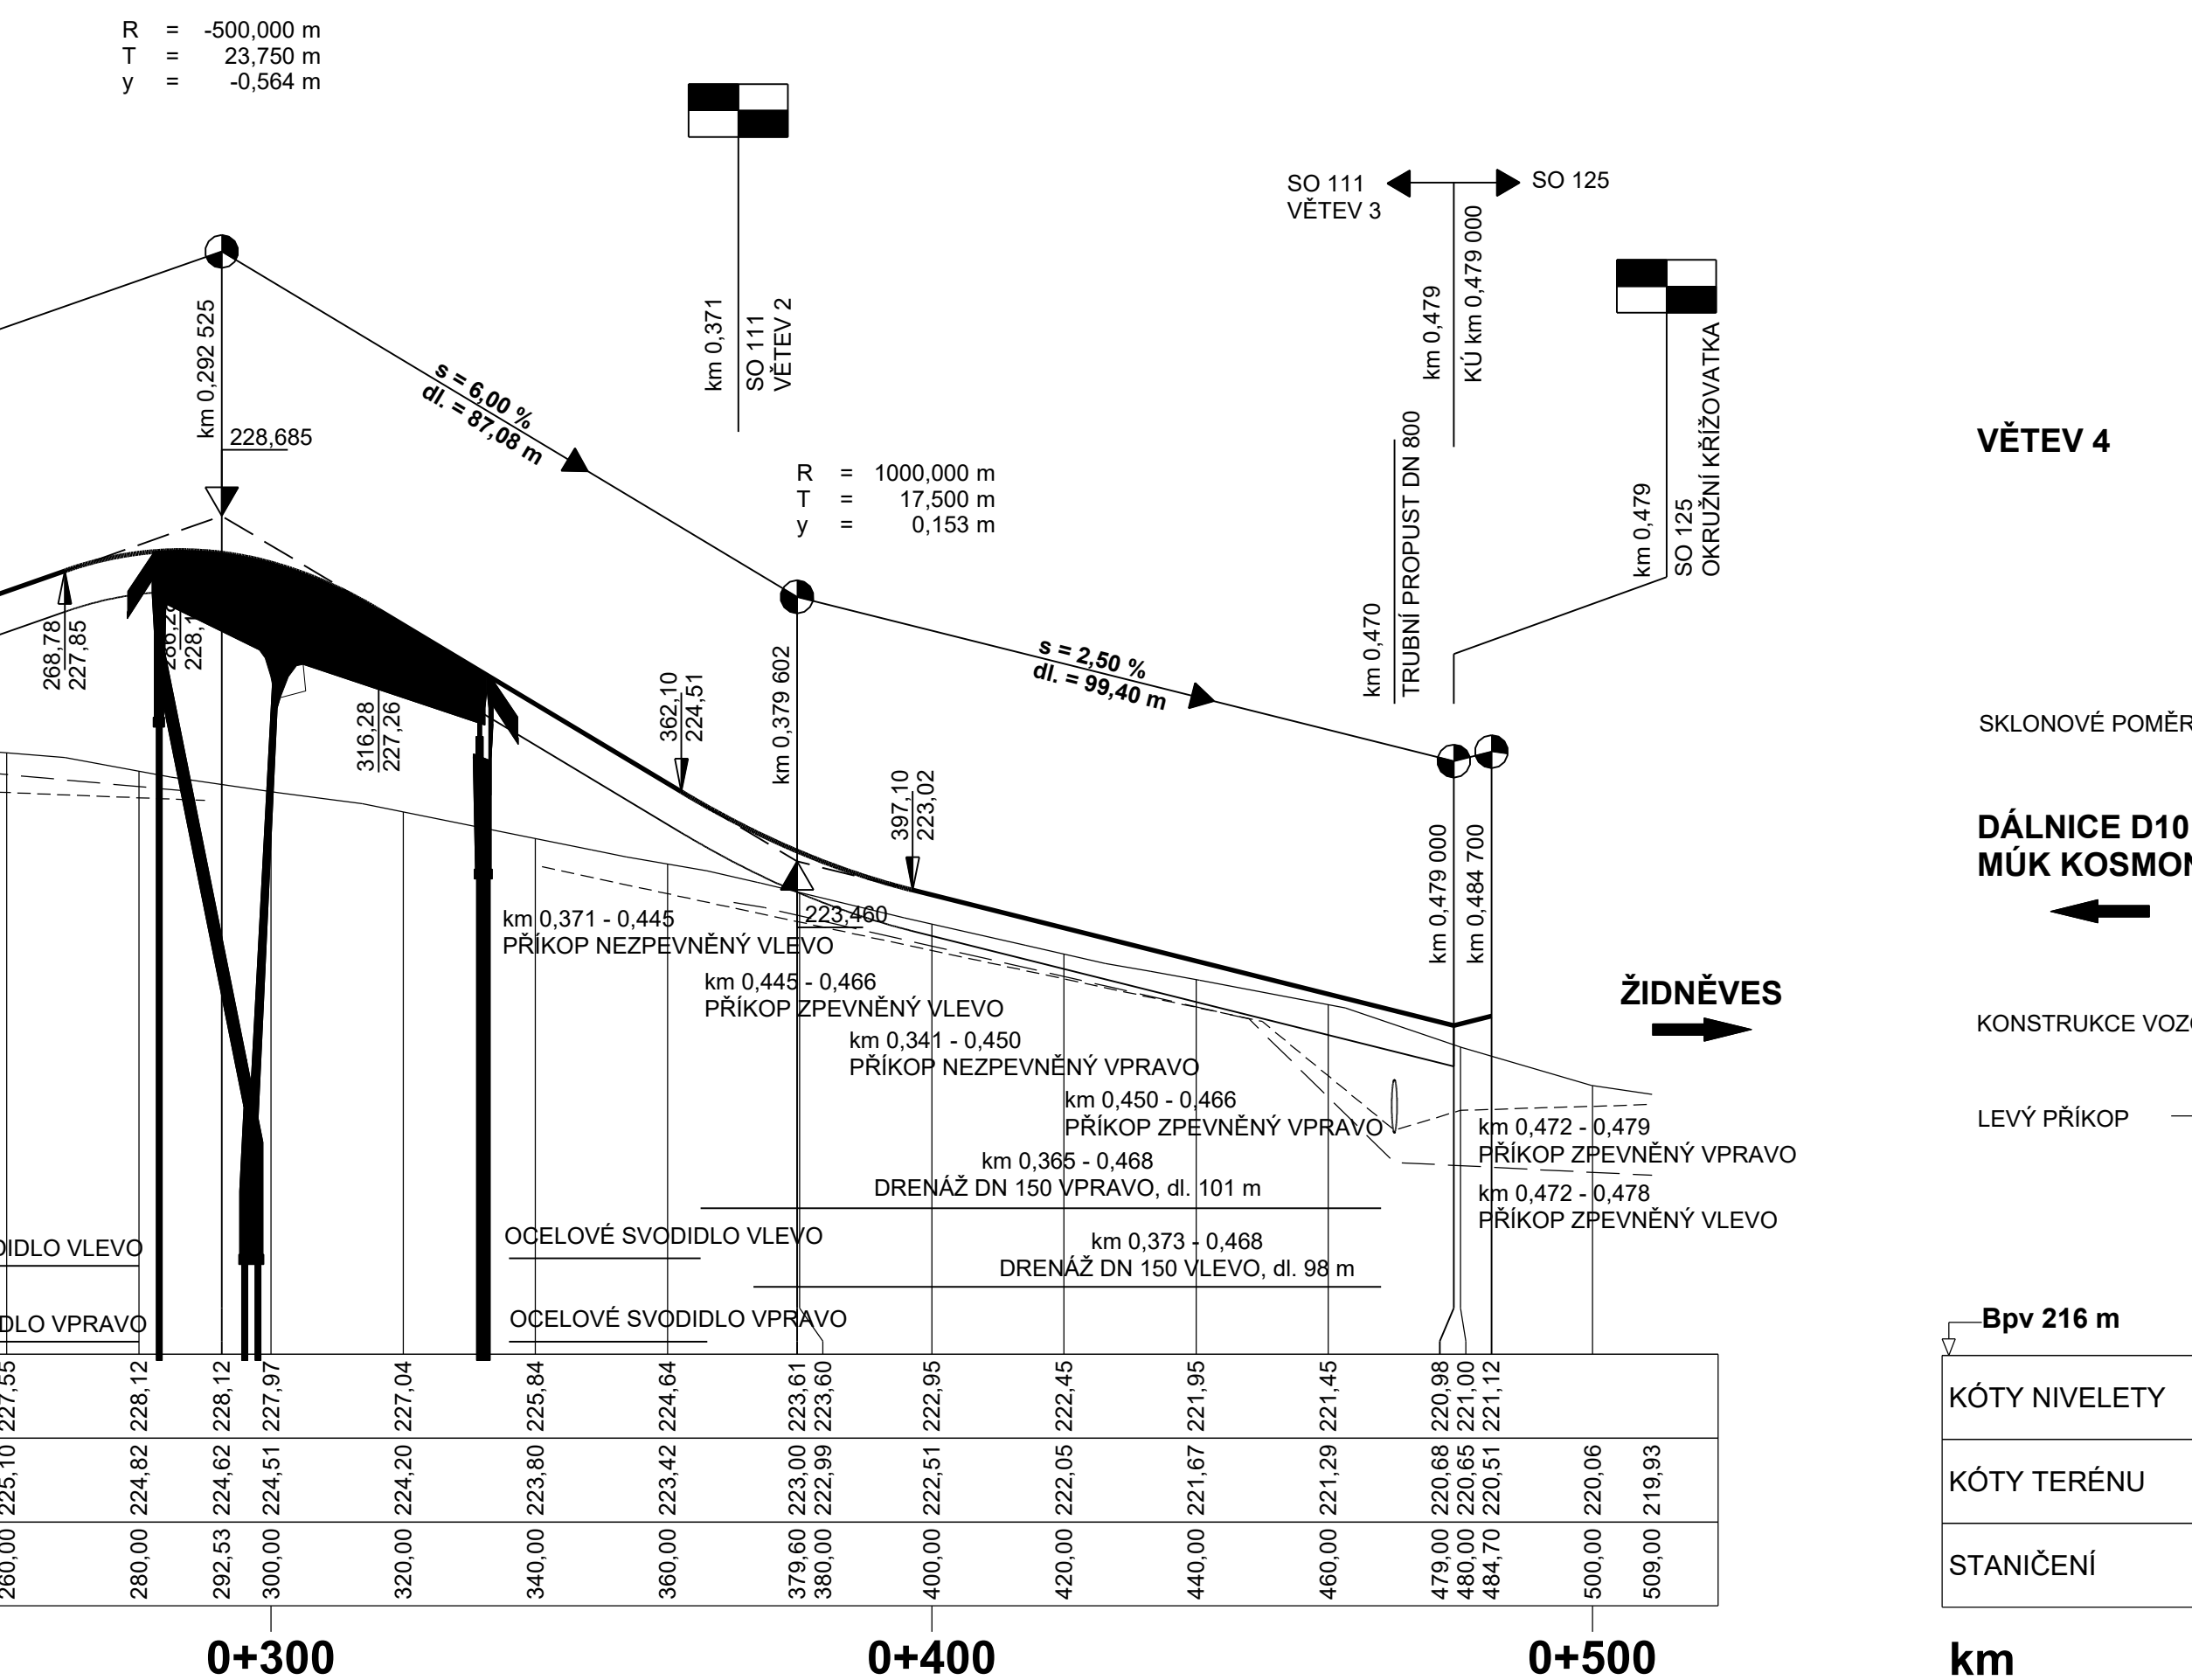
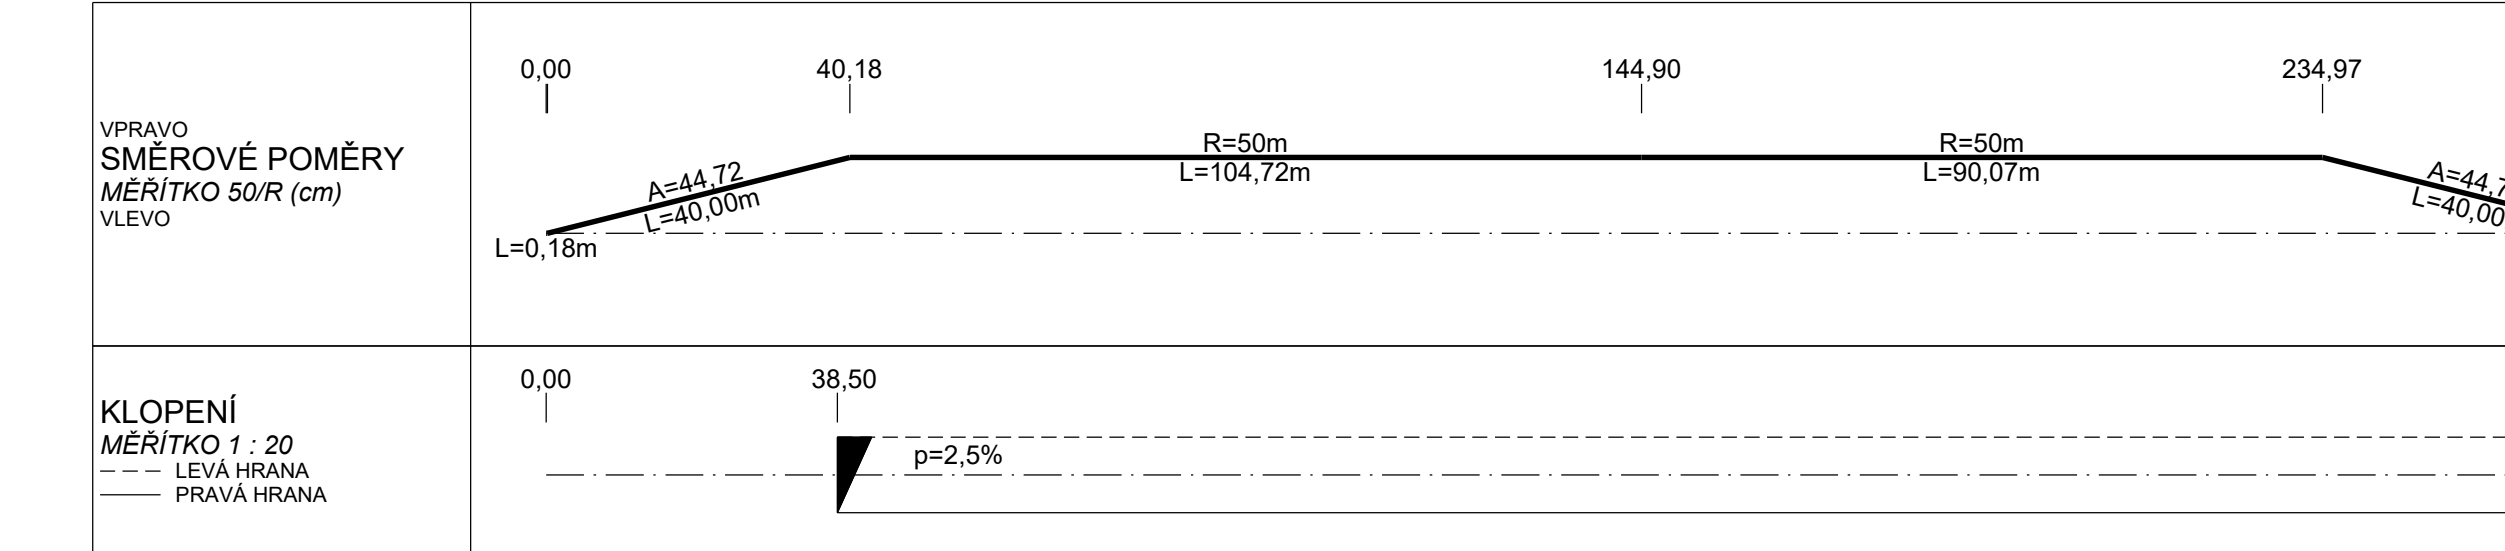
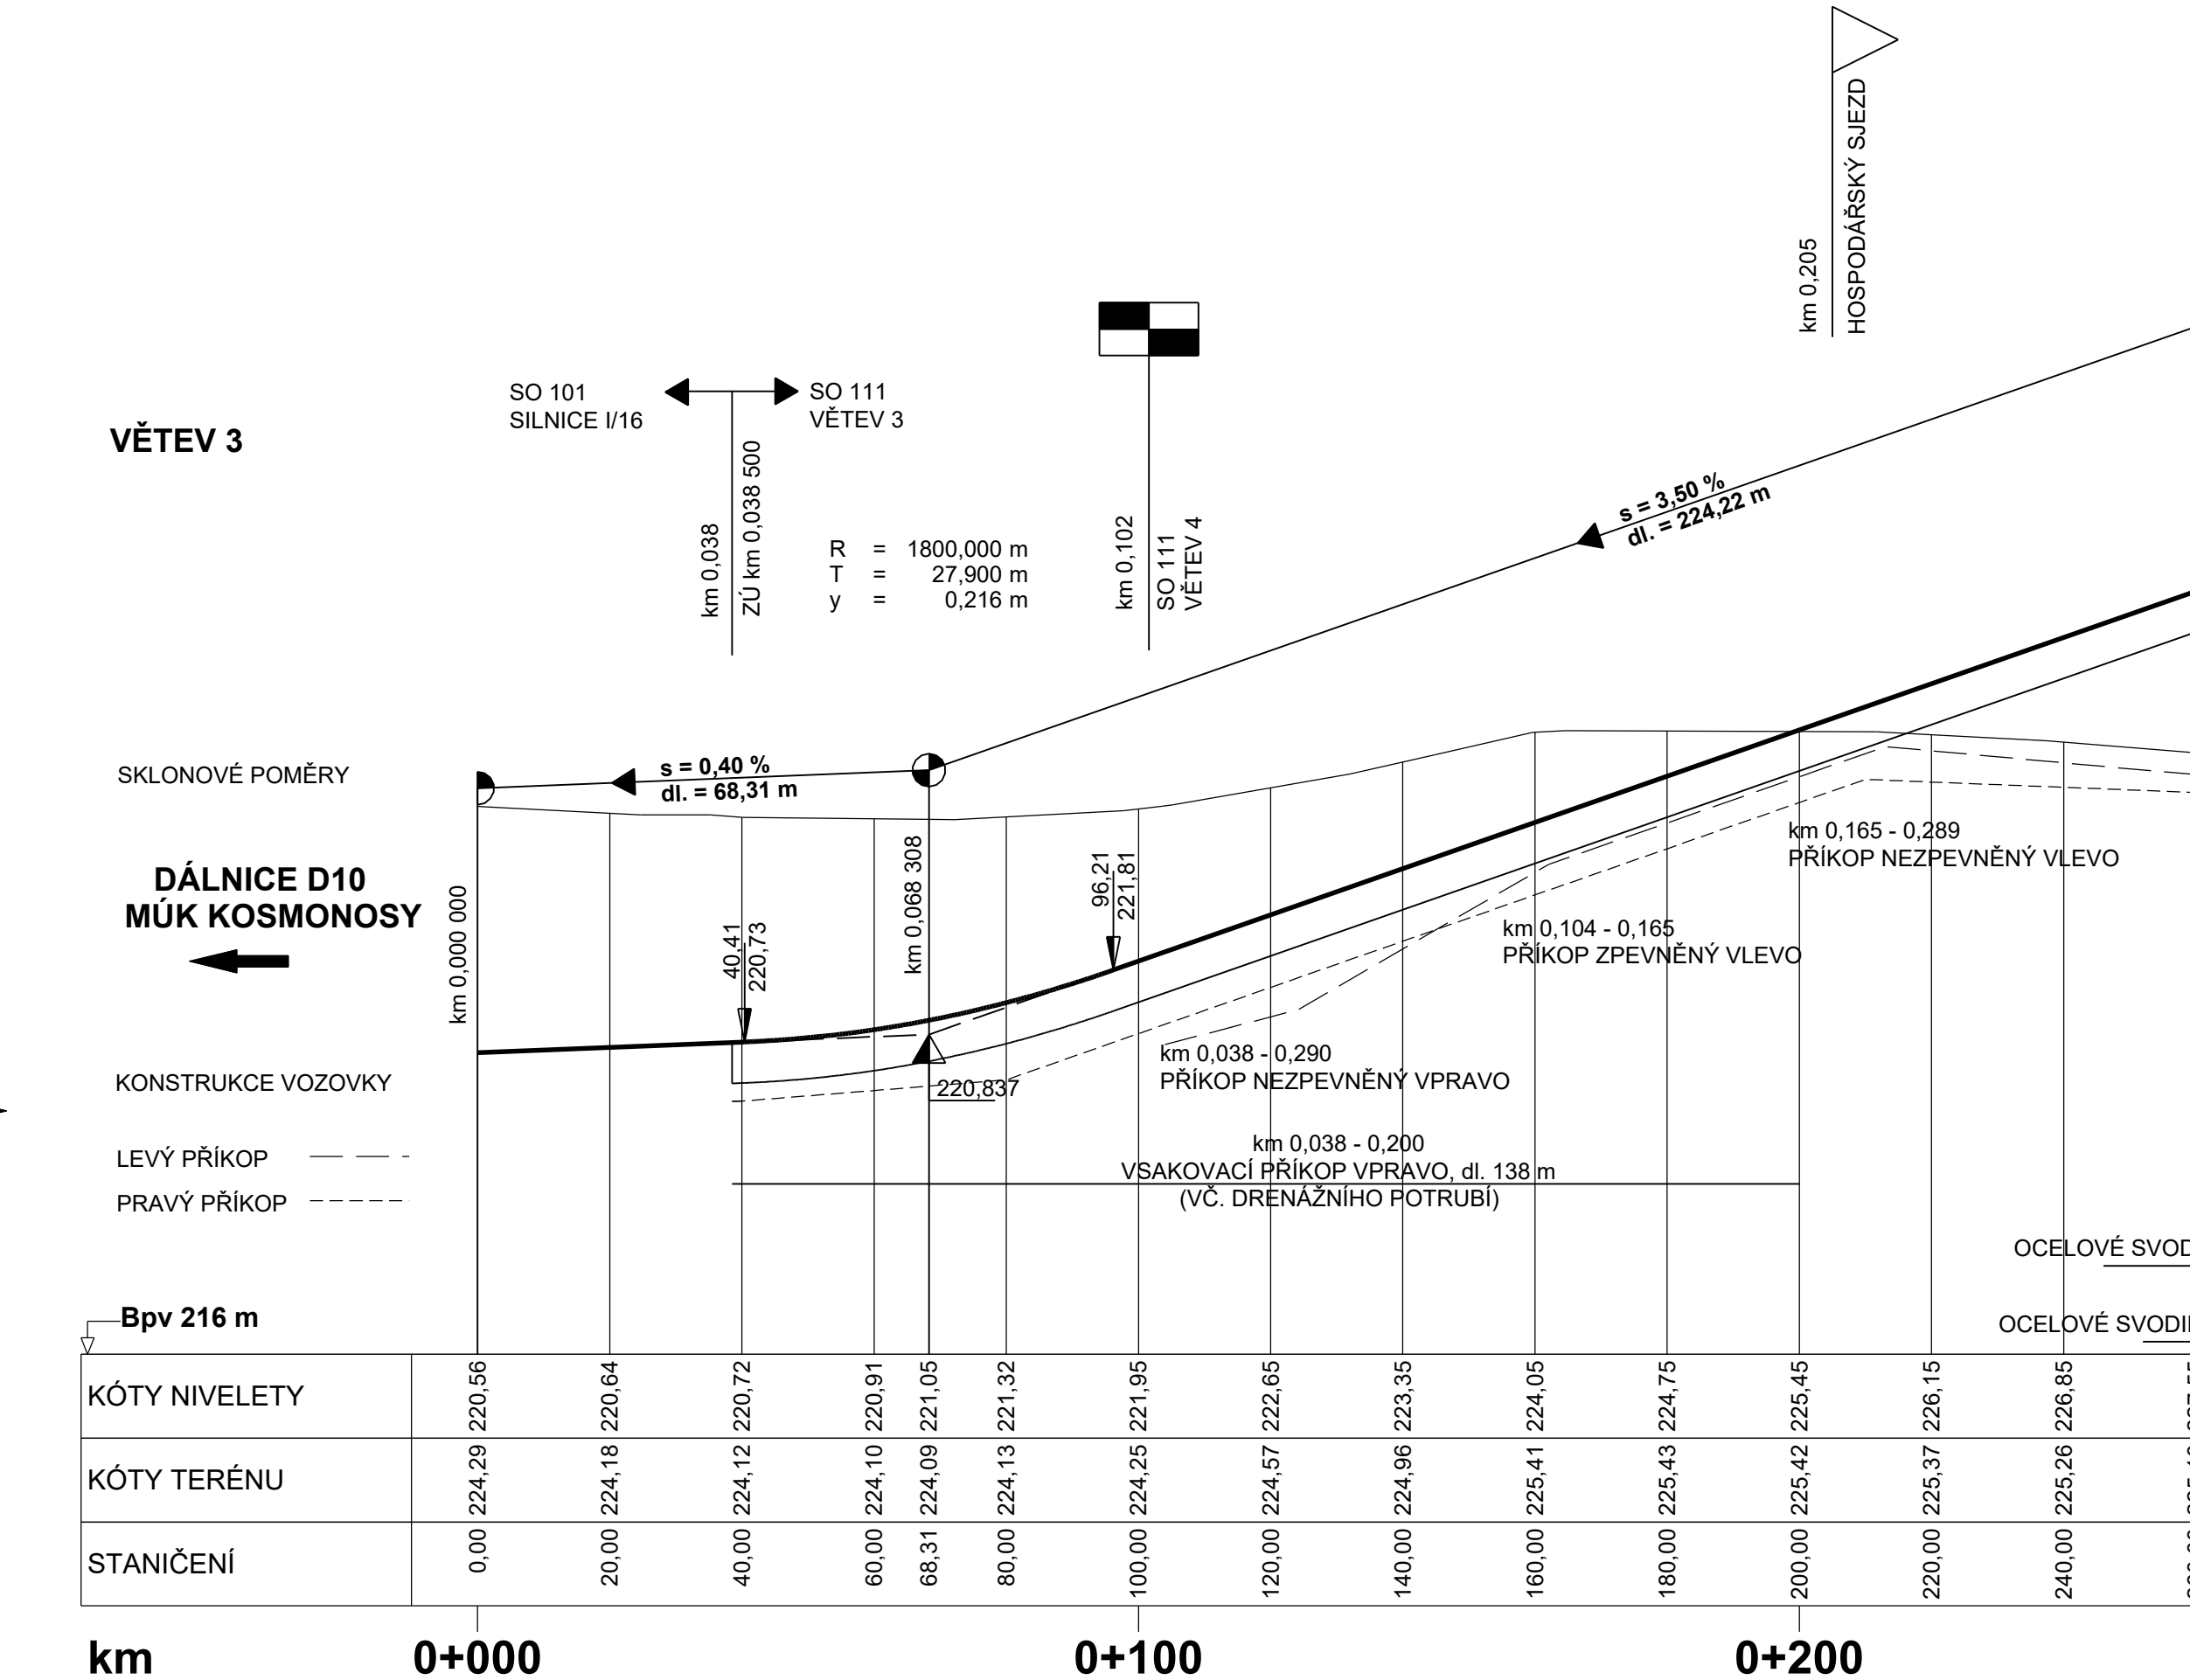
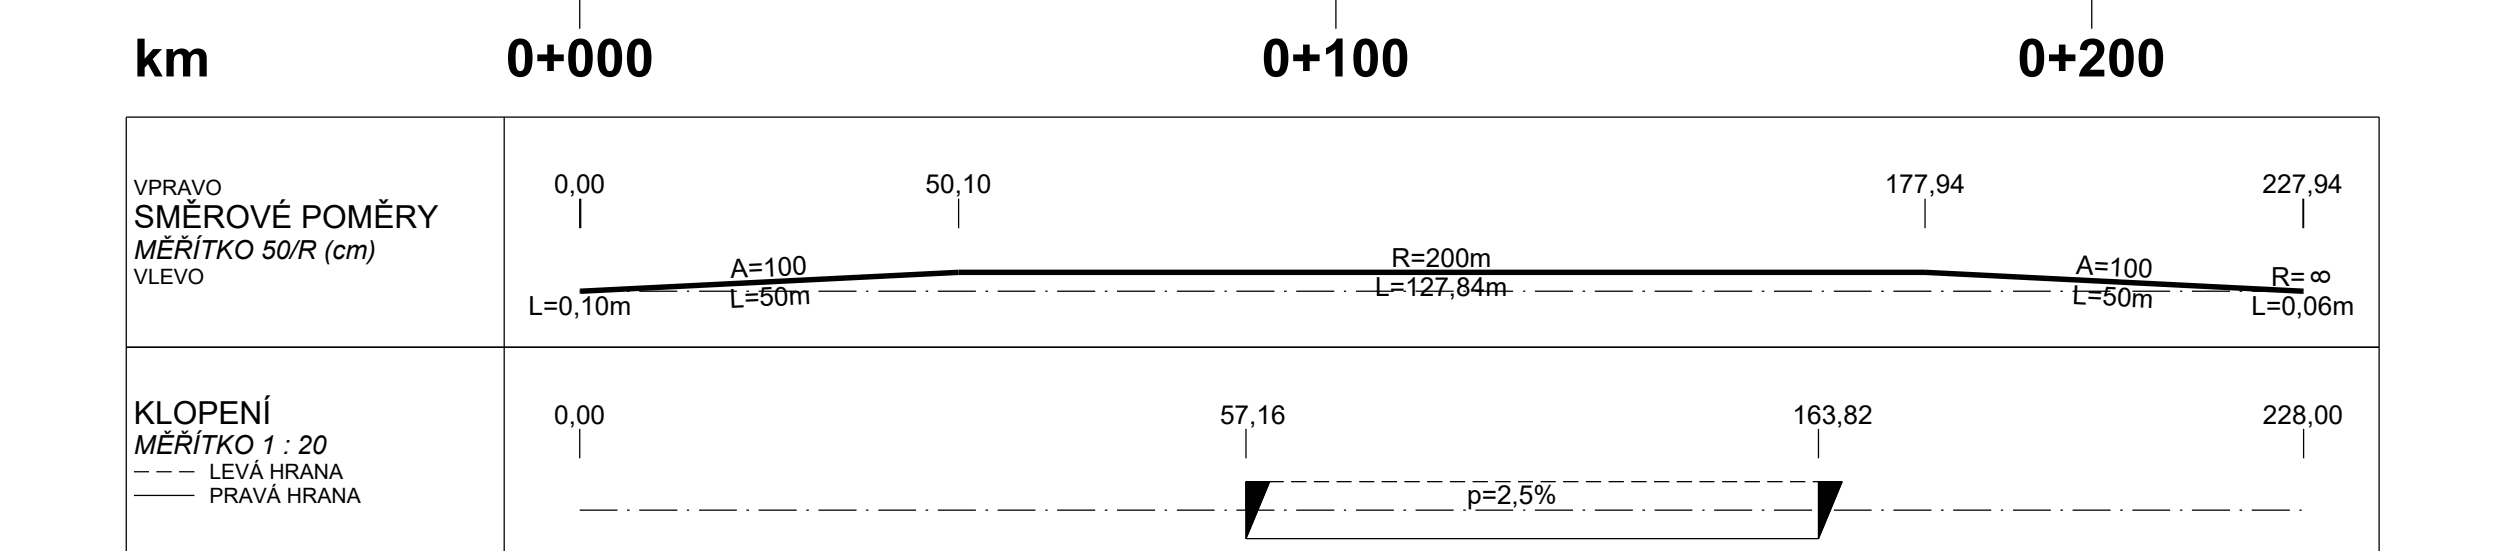
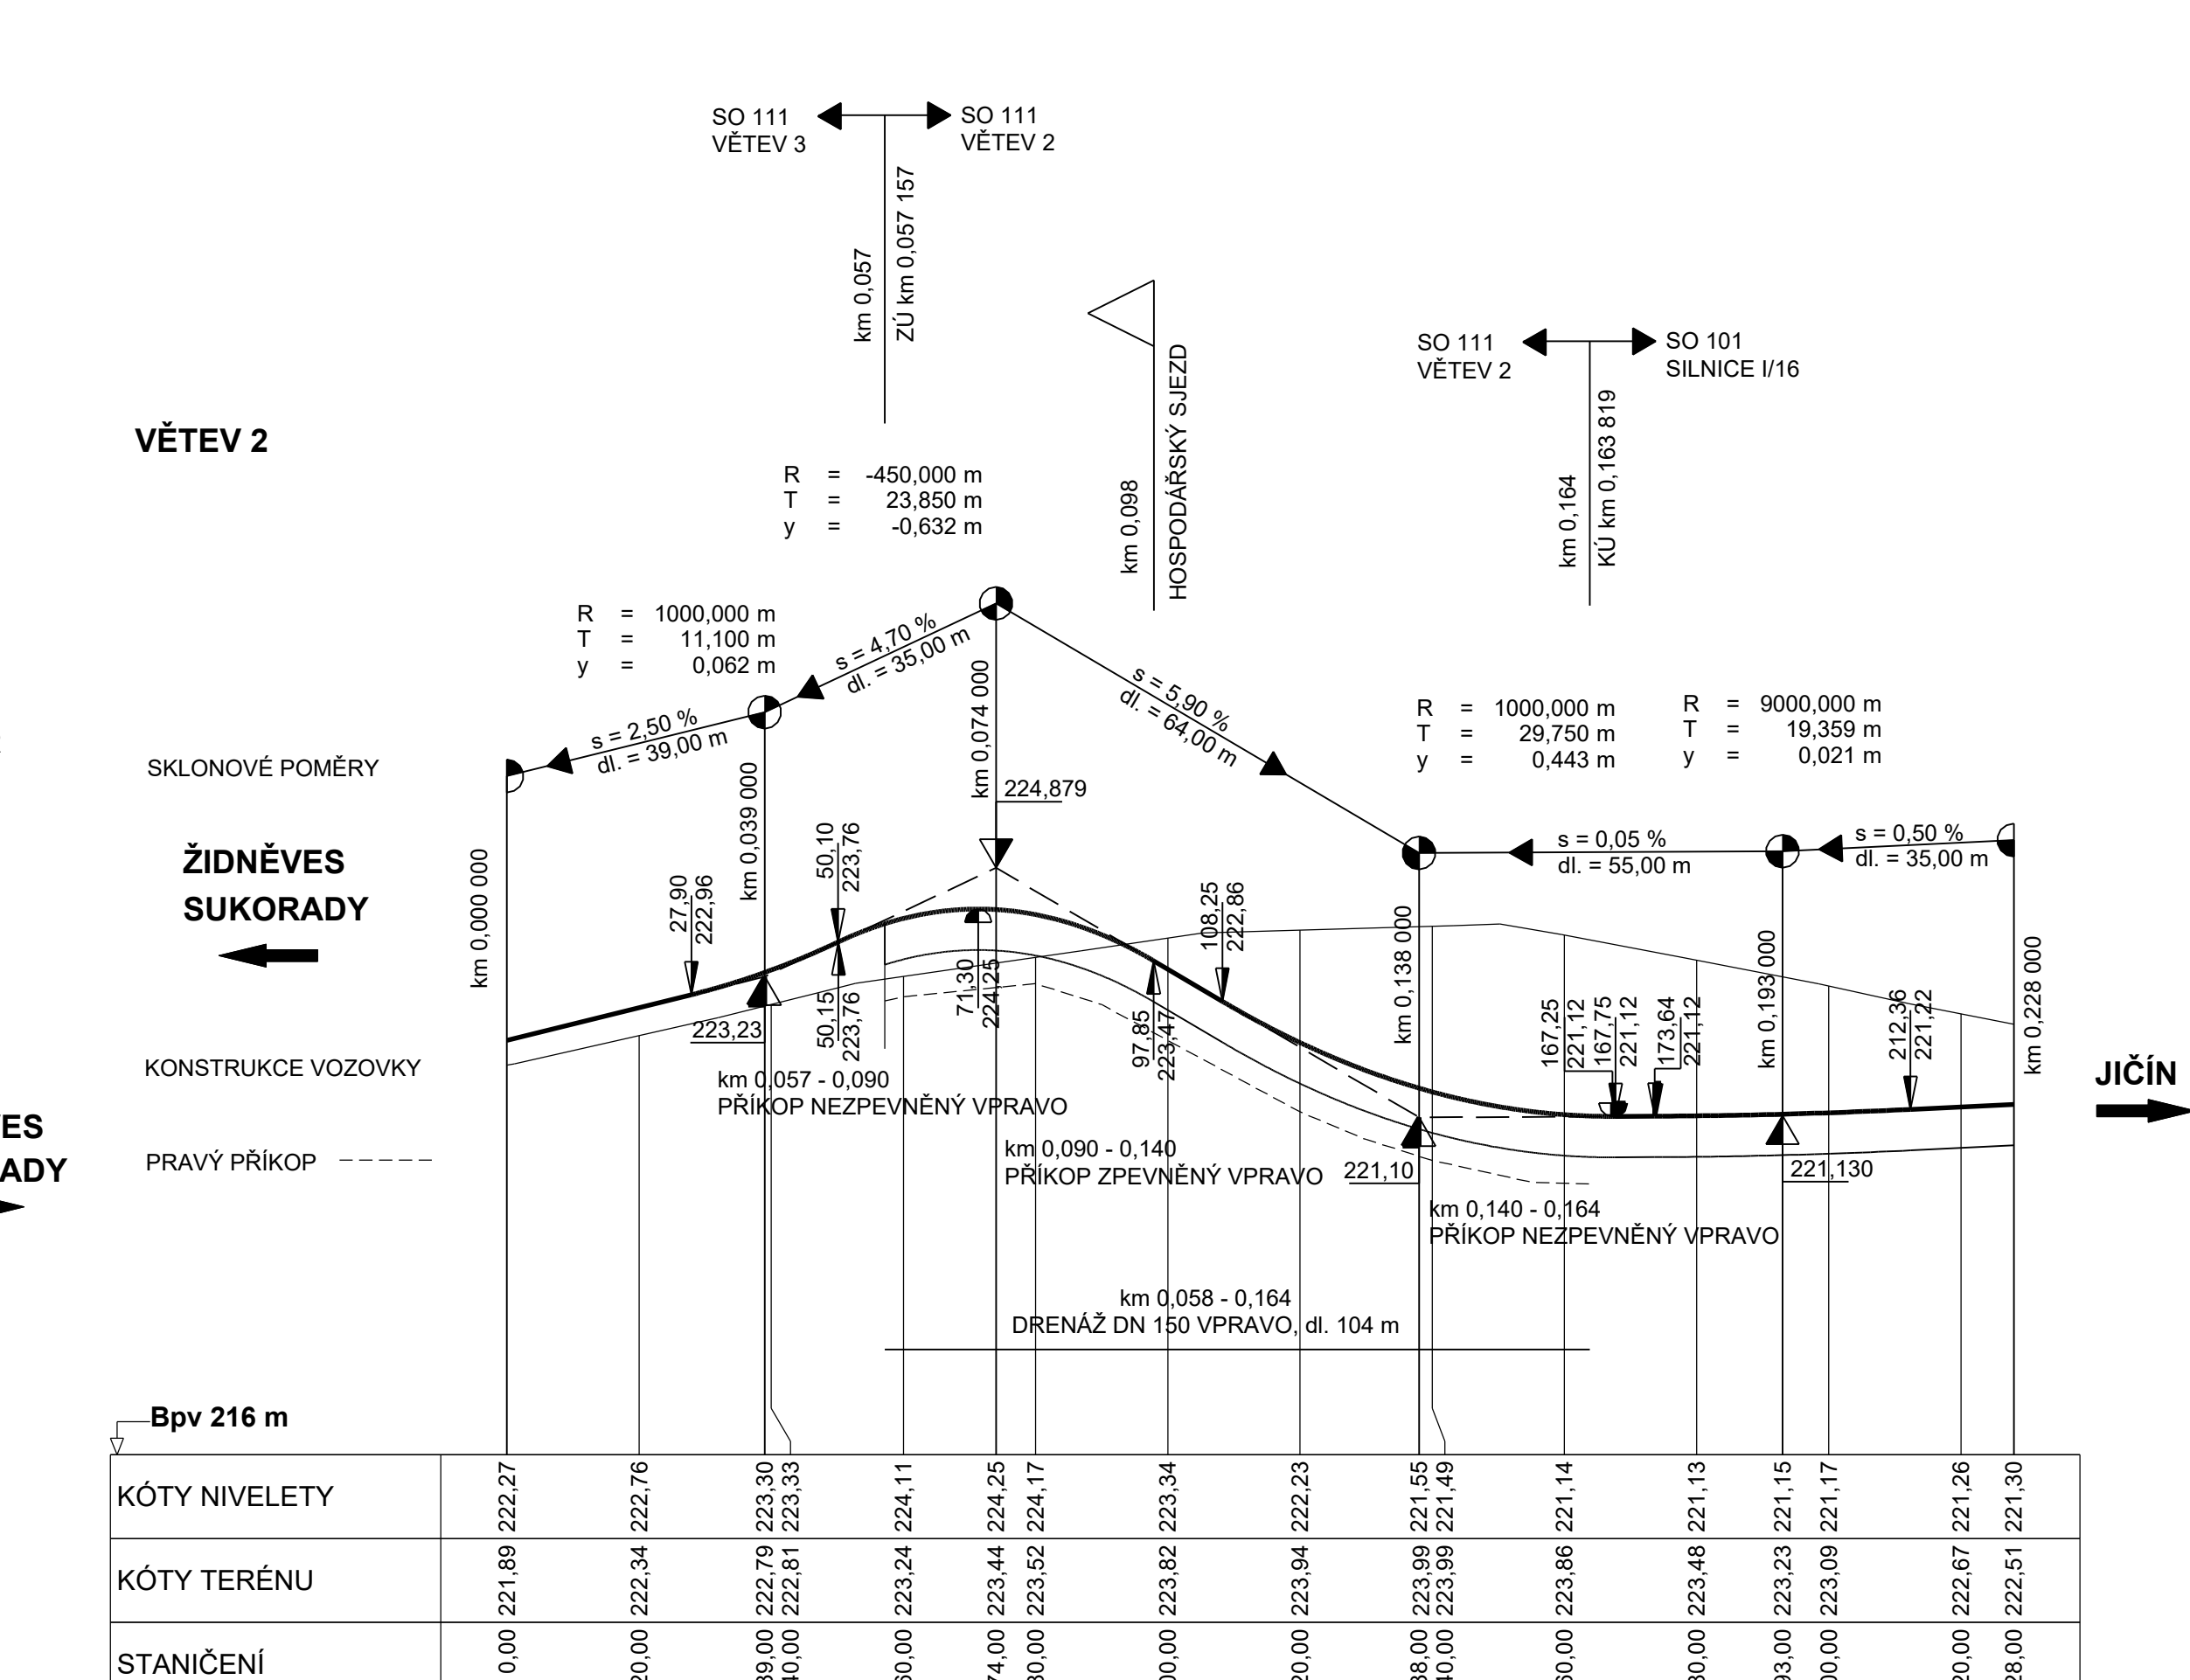
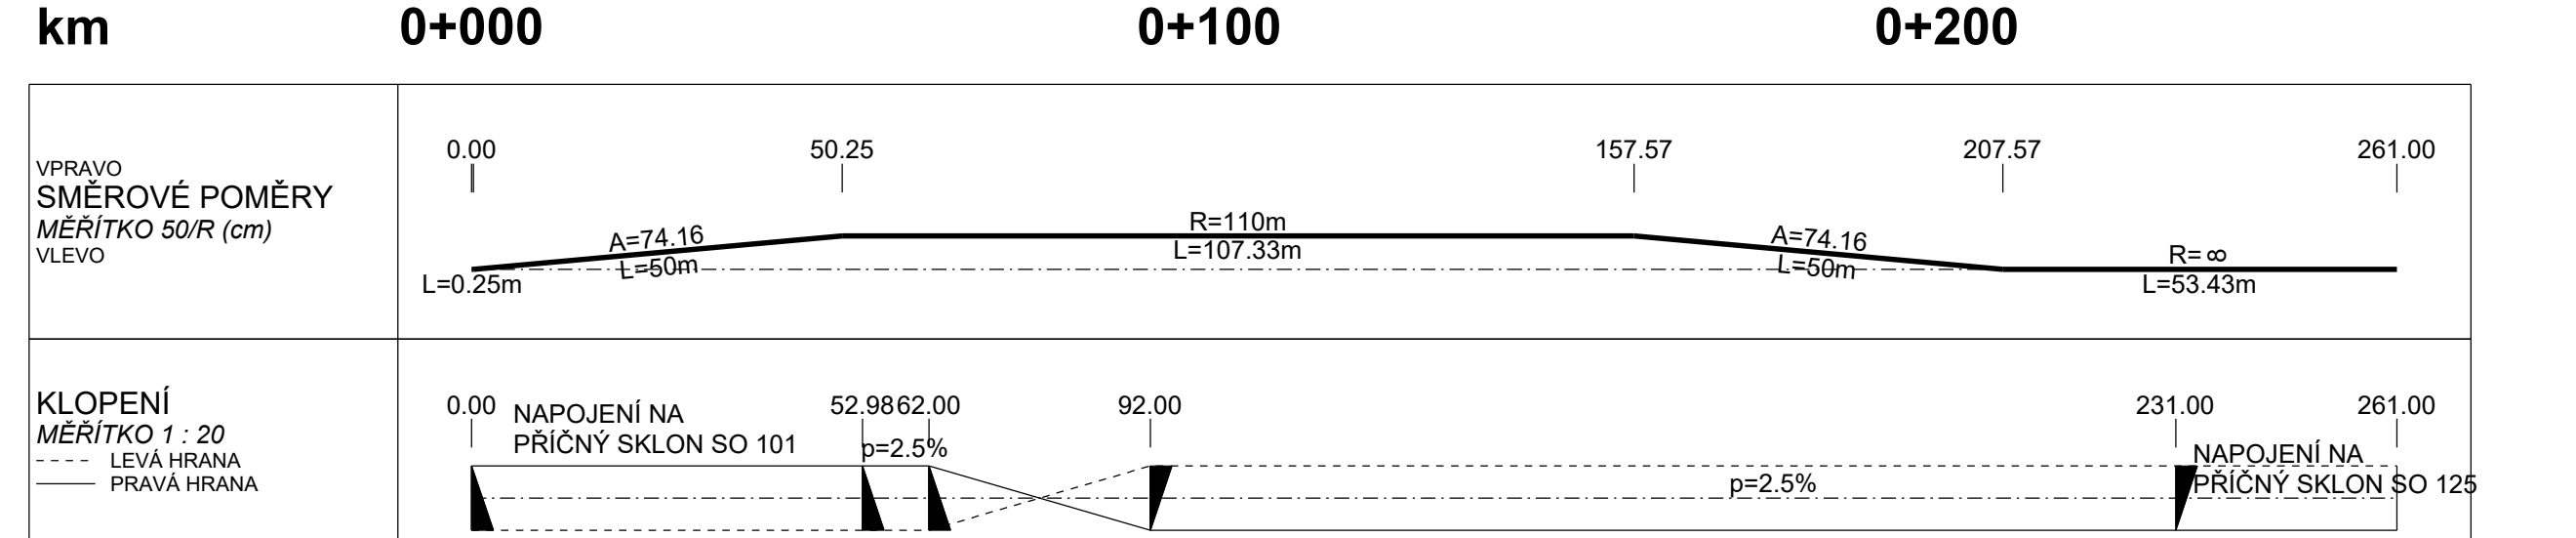


SO 111 - MŮK ŽIDNĚVES
PODÉLNÉ PROFILY, M 1 : 1 000 / 100

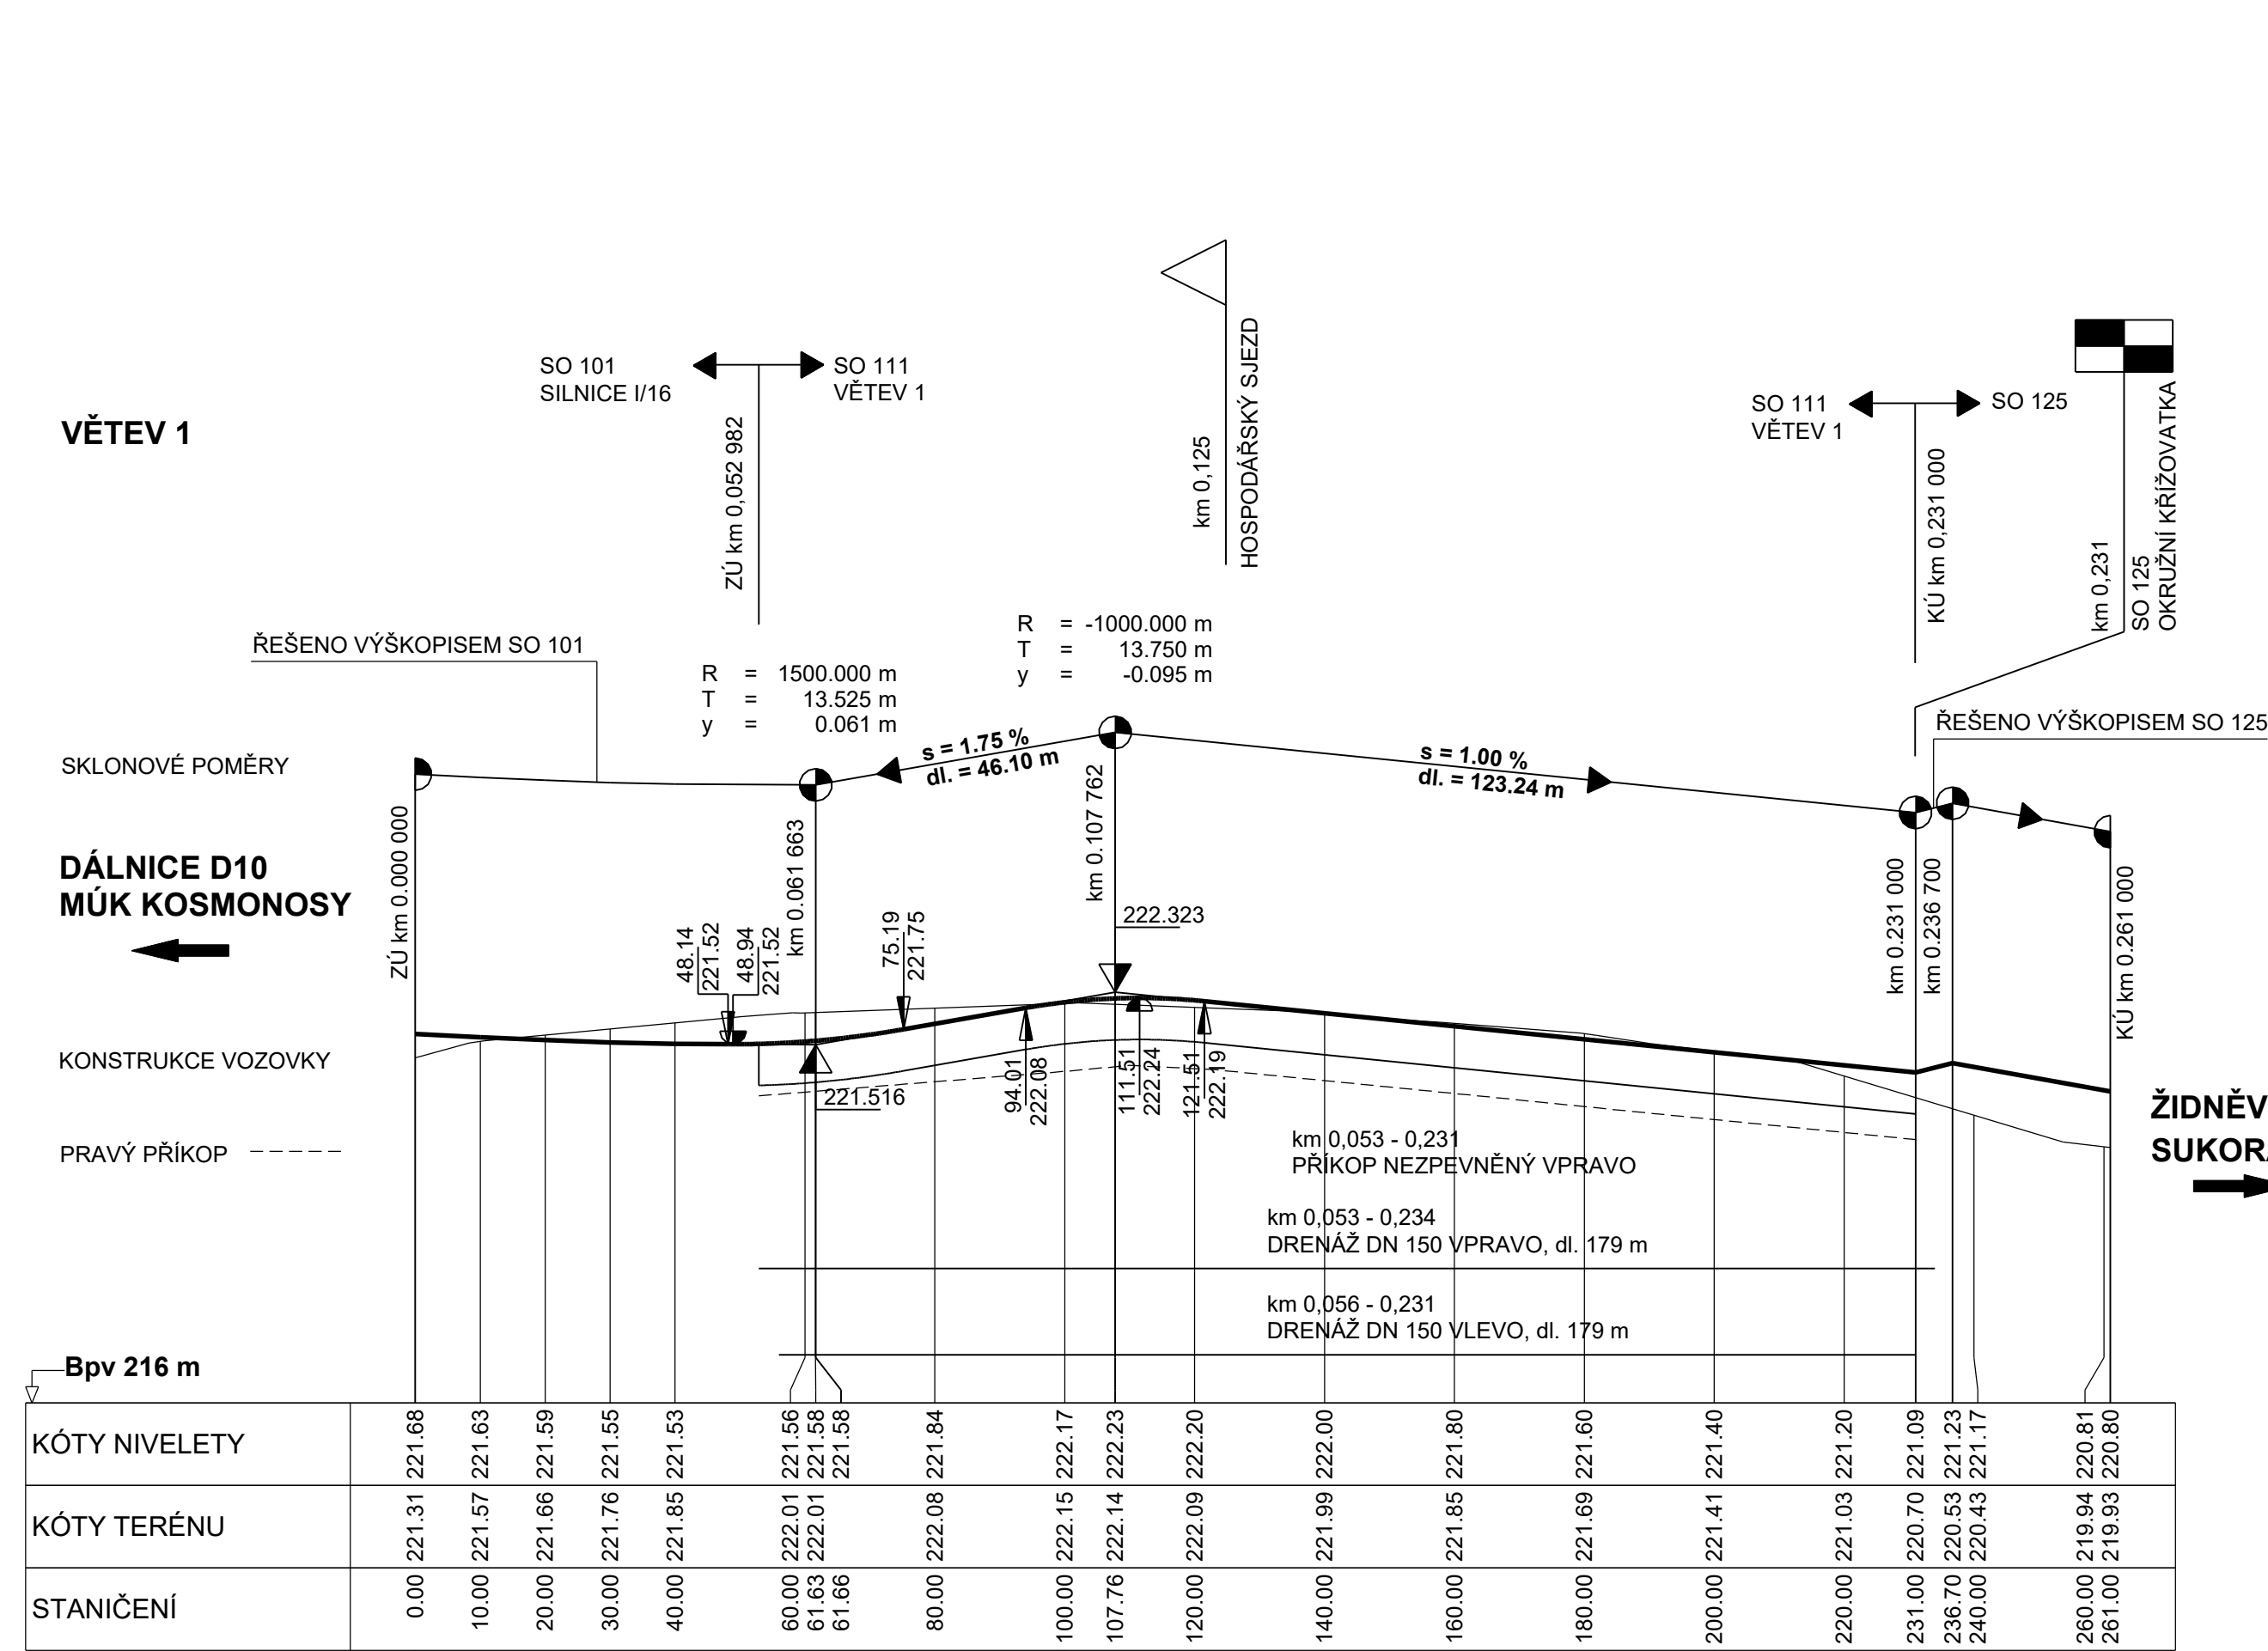

Souřadnicový systém: S-JTSK

SO 111 MŮK Židněves

Objednatel: Ředitelství silnic a dálnic

Ředitelství silnic a dálnic s. p.
Čerňanská 2023/12, Křt, 140 00 Praha 4

Zhotovitel: Valbek spol. s r.o.
Valbeka 505/17
460 07 Liberec 3

HIP: ING. T. KLIMENT

Vypracoval: ING. A. DUMANSKA
Zodp. projektant: ING. T. KLIMENT
Tech. kontrola: ING. M. HANŽL
Akce: I/16 MLADÁ BOLESLAV - MARTINOVICE

Zak. číslo: 21-L13-001
Datum: 02/2025
Stupeň: PDPS
Počet formátů: 18 x A4
Měřítko: 1 : 1 000
C. přílohy: Pare

3