


SO 111 - MÚK ŽIDNĚVES
VZOROVÉ PŘÍČNÉ ŘEZY
M 1 : 100


OBOUSMĚRNÁ VĚTEV

TRÍDA DOPRAVNÍHO ZATÍŽENÍ I
NÁVRHOVÁ ÚROVEŇ PORUŠENÍ D0
TYP PODLOŽÍ PIII (D0-A-3)

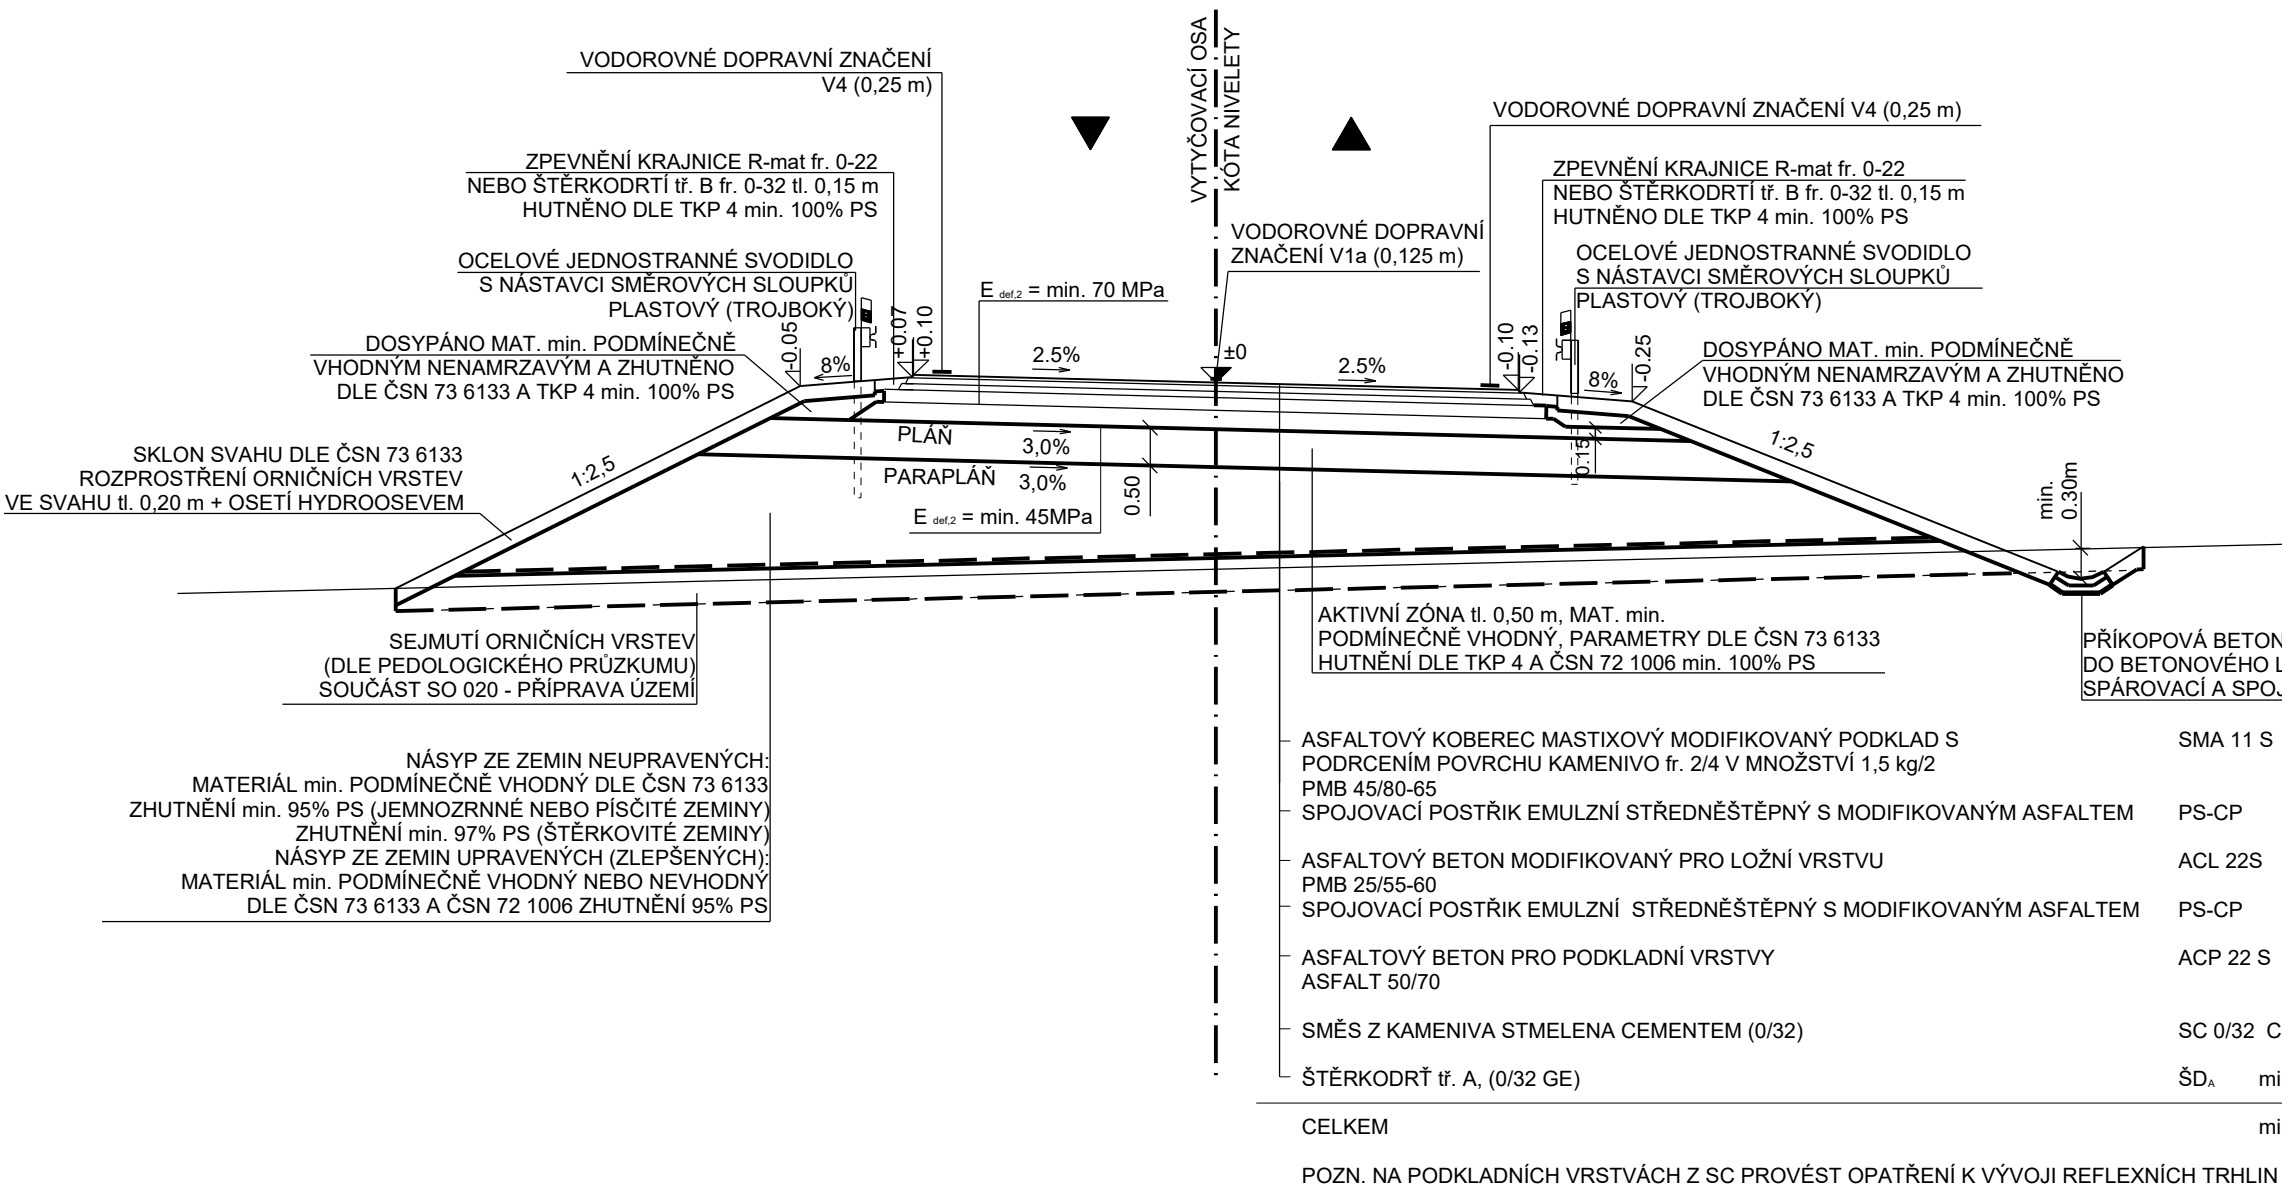


JEDNOSMĚRNÁ VĚTEV

TRÍDA DOPRAVNÍHO ZATÍŽENÍ I
NÁVRHOVÁ ÚROVEŇ PORUŠENÍ D0
TYP PODLOŽÍ PIII (D0-A-3)

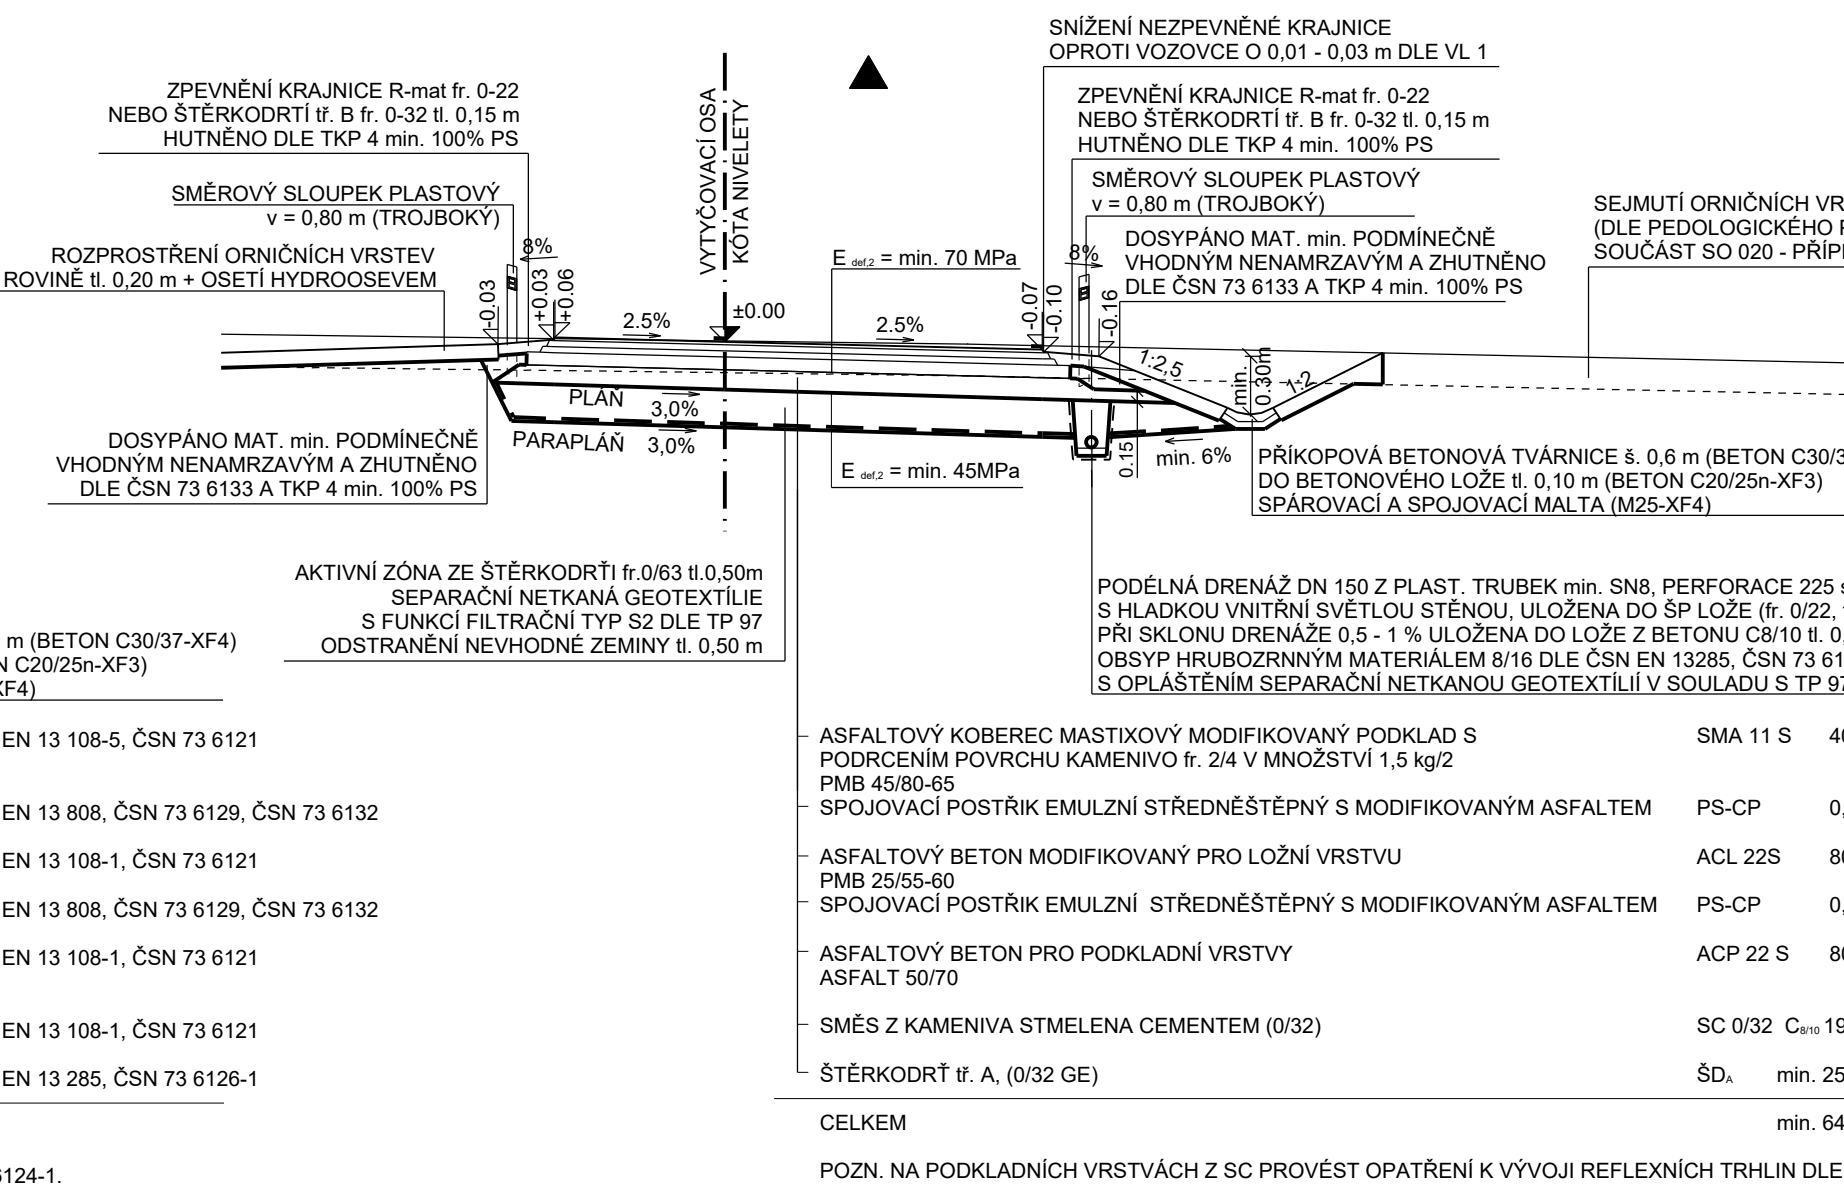


OBOUSMĚRNÁ VĚTEV
DĚLÍCI OSTRŮVEK

TRÍDA DOPRAVNÍHO ZATÍŽENÍ I
NÁVRHOVÁ ÚROVEŇ PORUŠENÍ D0
TYP PODLOŽÍ PIII (D0-A-3)

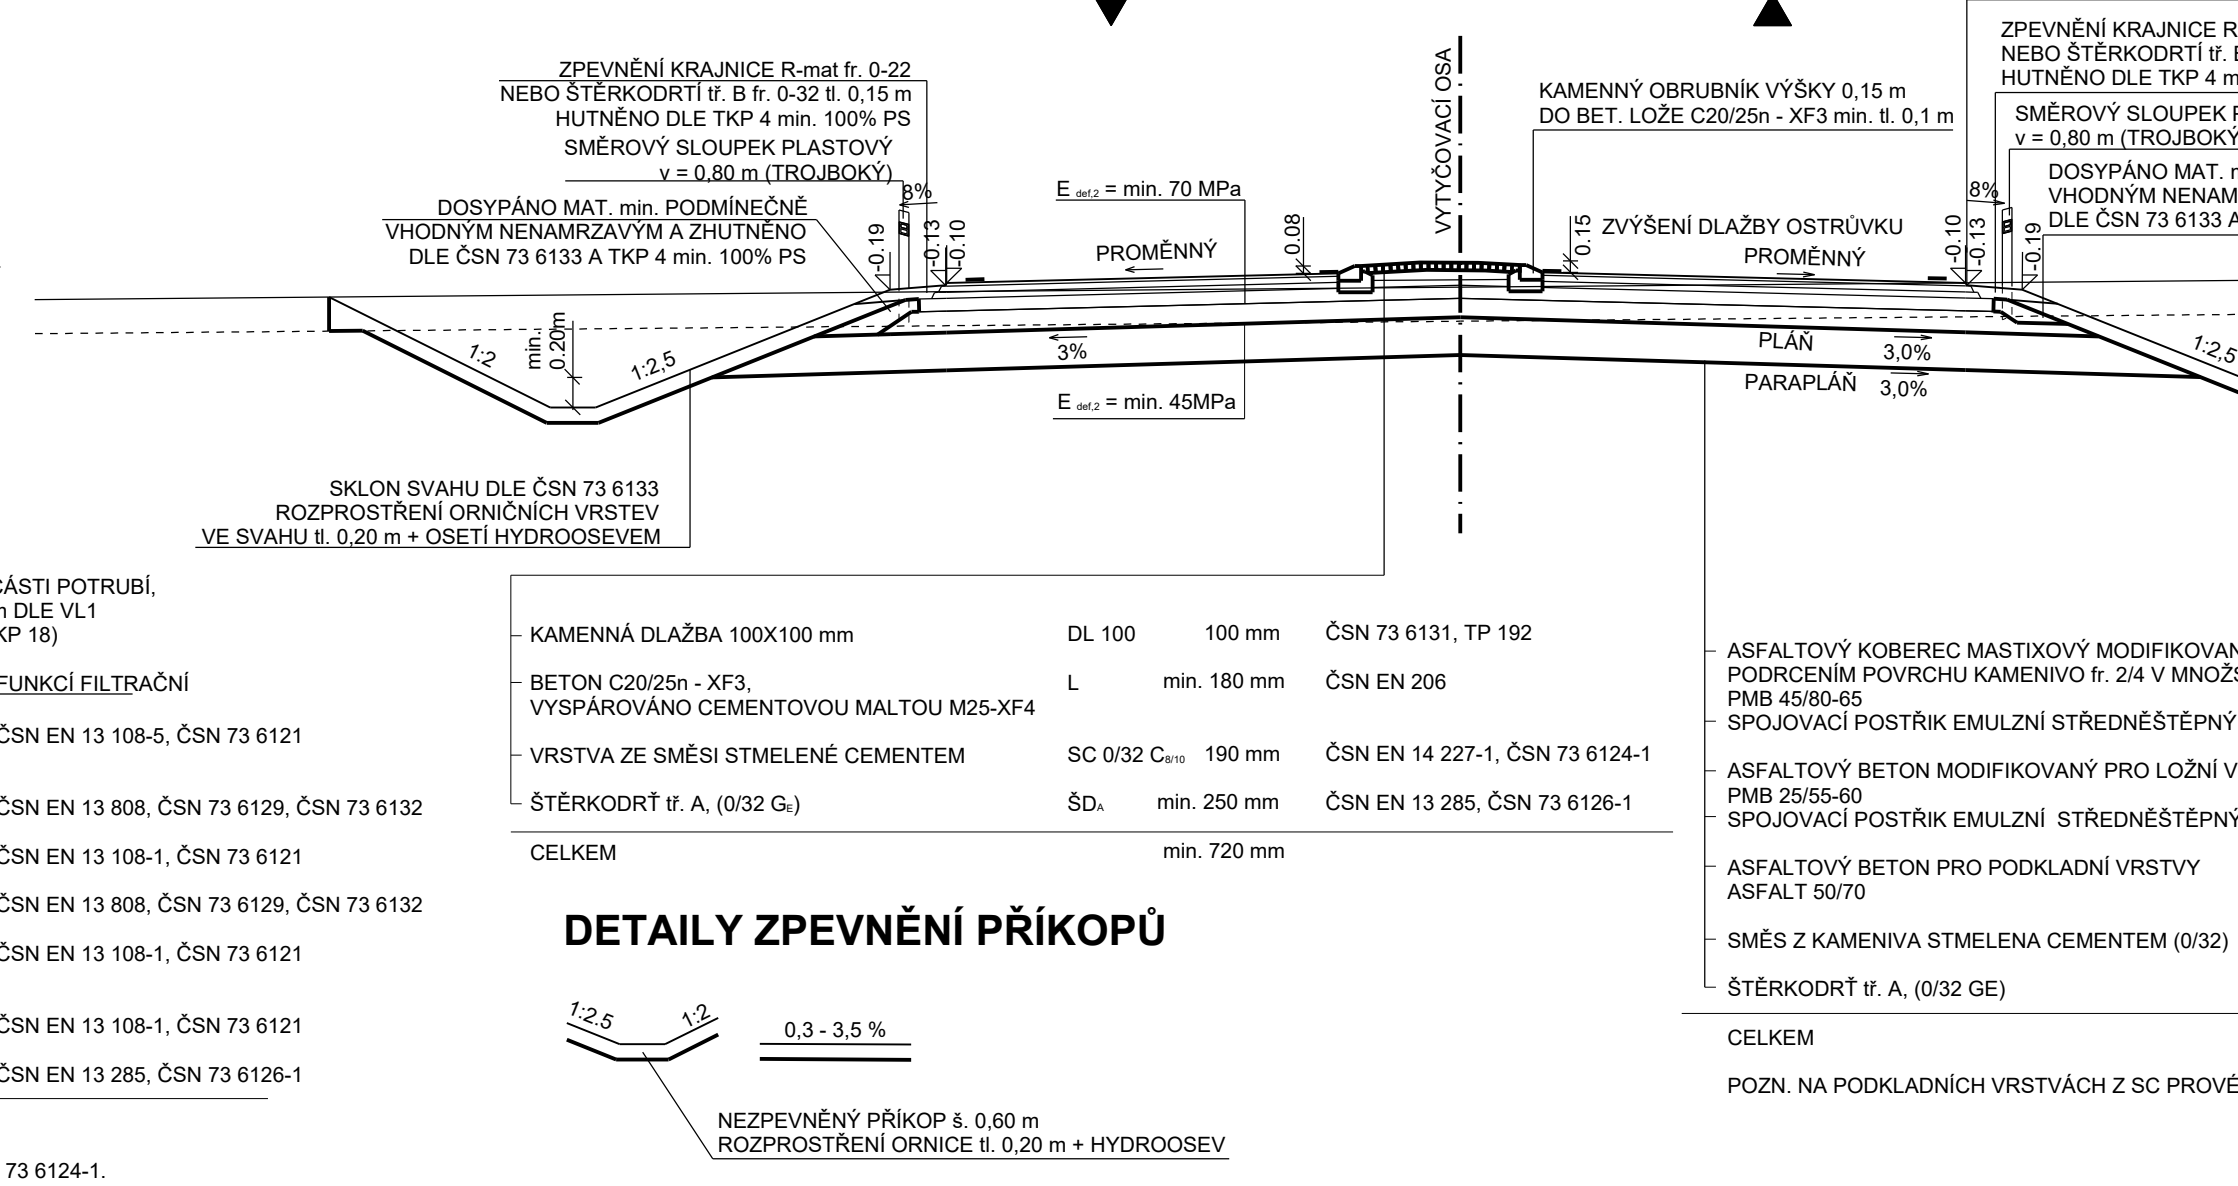


HOSPODÁŘSKÝ SJEZD


TRÍDA DOPRAVNÍHO ZATÍŽENÍ VI
NÁVRHOVÁ ÚROVEŇ PORUŠENÍ D2
TYP PODLOŽÍ PIII (D2-N-1)

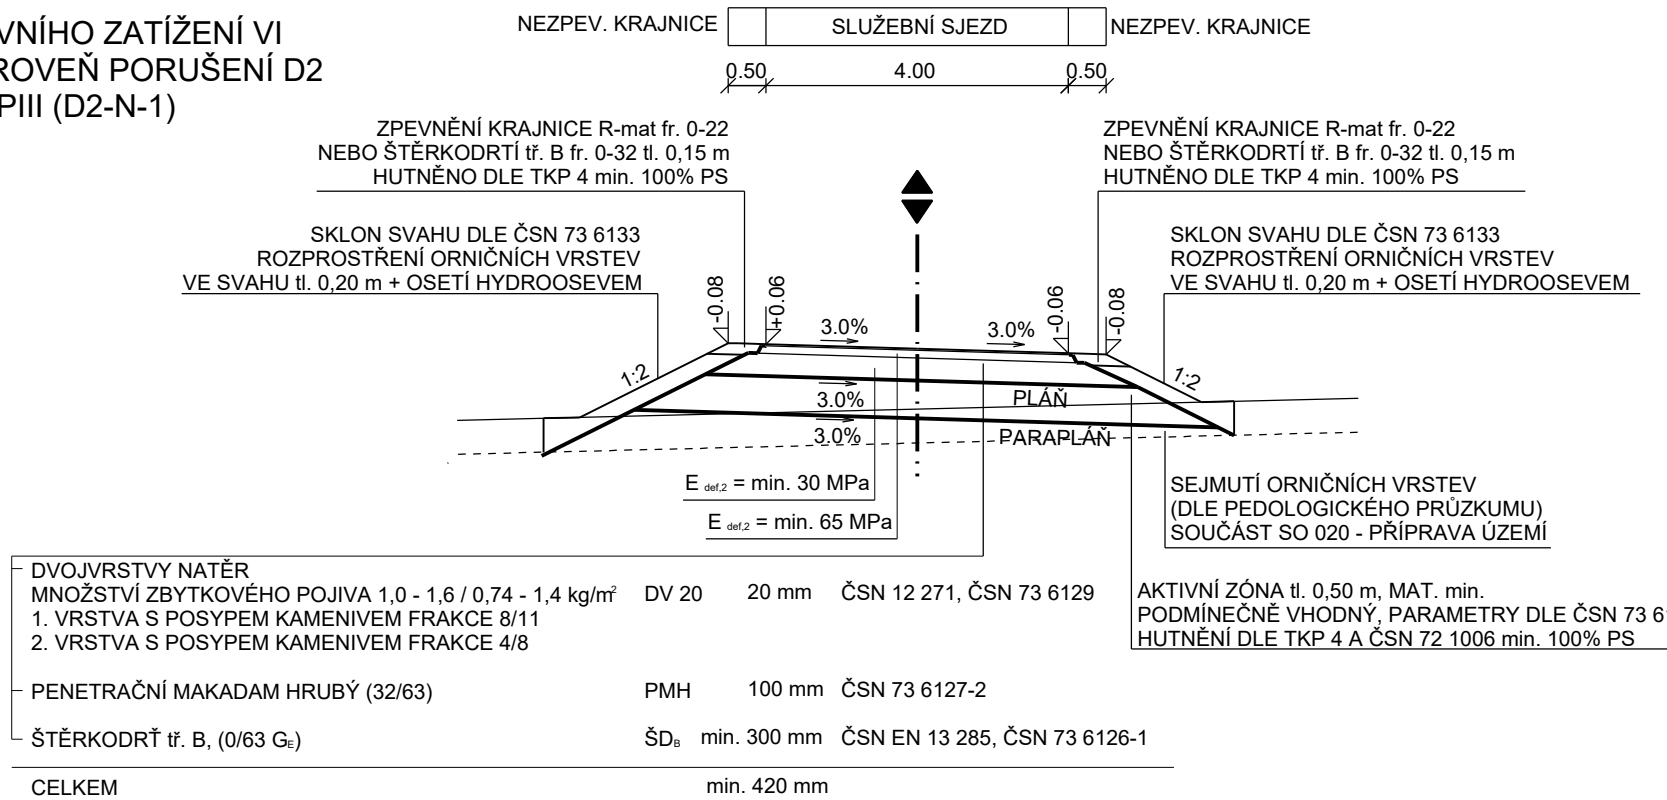


DETAILY ZPEVNĚNÍ PŘÍKOPŮ

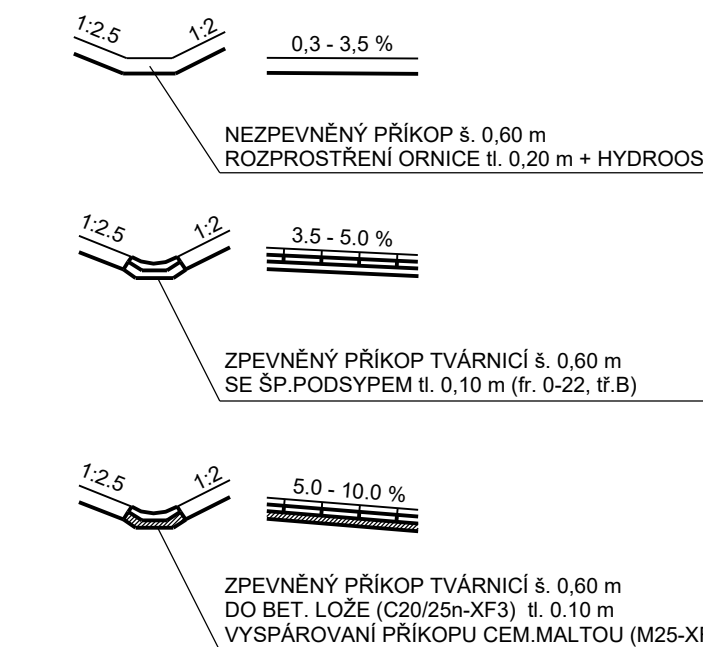


SANACE TYP I

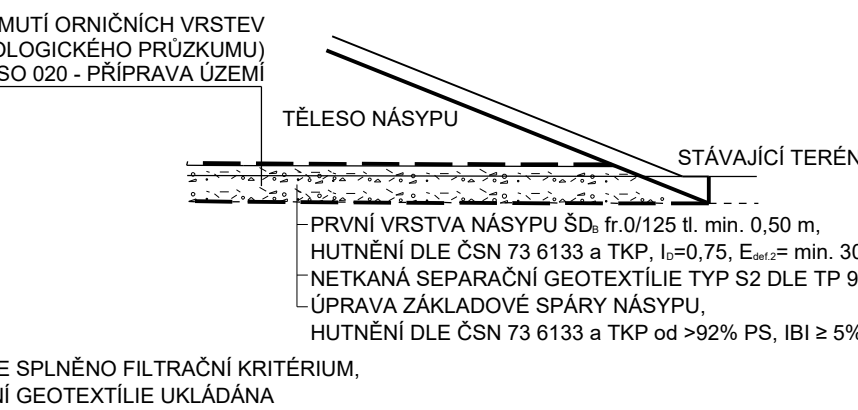


SANACE TYP III

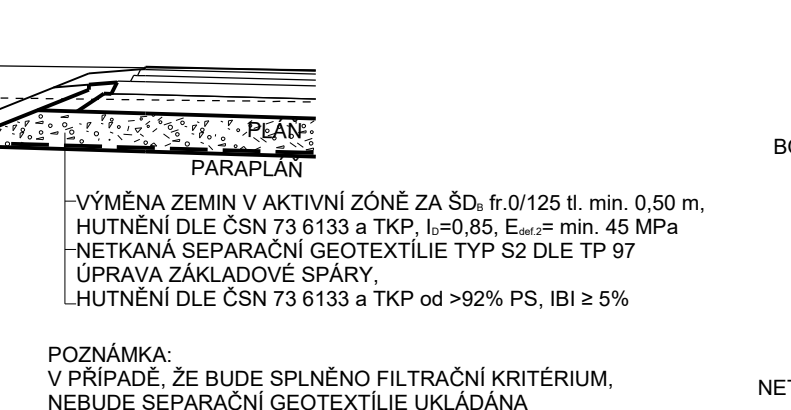

DETAIL STYKU VOZOVKY S RIGOLEM M 1 : 50

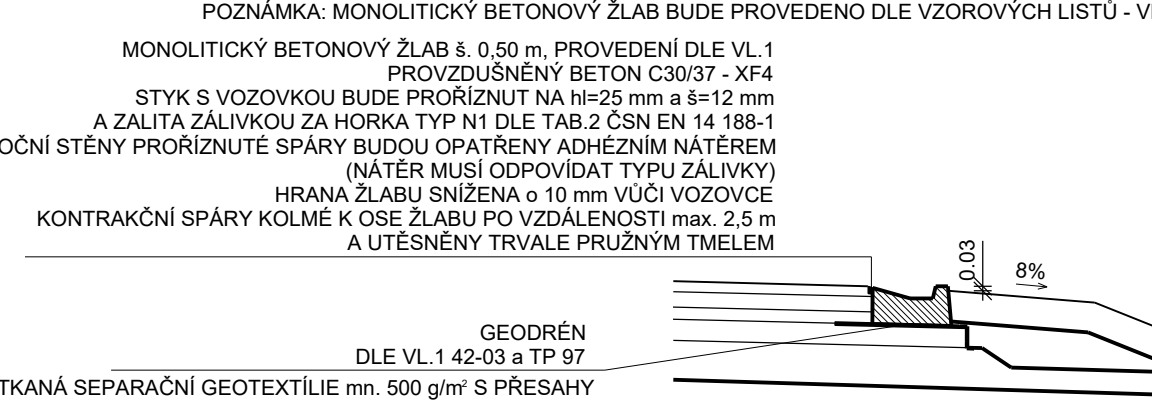

DETAIL PŘÍKOPU V MÍSTĚ VSAKOVÁNÍ

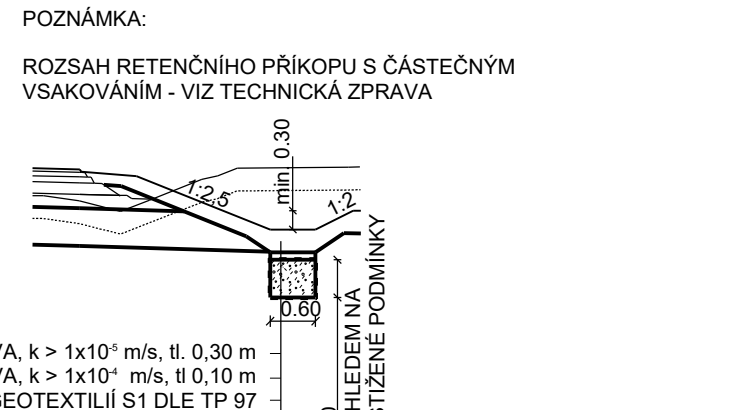

DOD.24

SO 111 MÚK ŽIDNĚVES

Objednatel: Ředitelství silnic a dálnic
Ředitelství silnic a dálnic s. p.
Čerčanská 2032/12, Krč, 140 00 Praha 4

Zhotovitel: Valbek
Valbek, spol. s r.o.
Vaňurova 505/17
460 07 Liberec 3
HIP: ING. T. KLIMENT

Valbek	Vypracoval	ING. A. DUMANSKA	Zak. číslo	21-LH3-001
	Zodp. projektant	ING. T. KLIMENT	Datum	02/2025
	Tech. kontrola	ING. M. HANŽL	Stupeň	PDPS
	Akce	I/16 MLADÁ BOLESLAV - MARTINOVICE	Počet formátů	6 x A4
Zhotovitel: Valbek, spol. s r.o. Vaňurova 505/17 460 07 Liberec 3	Příloha	VZOROVÉ PŘÍČNÉ ŘEZY	Č. přílohy	Paré
			4	