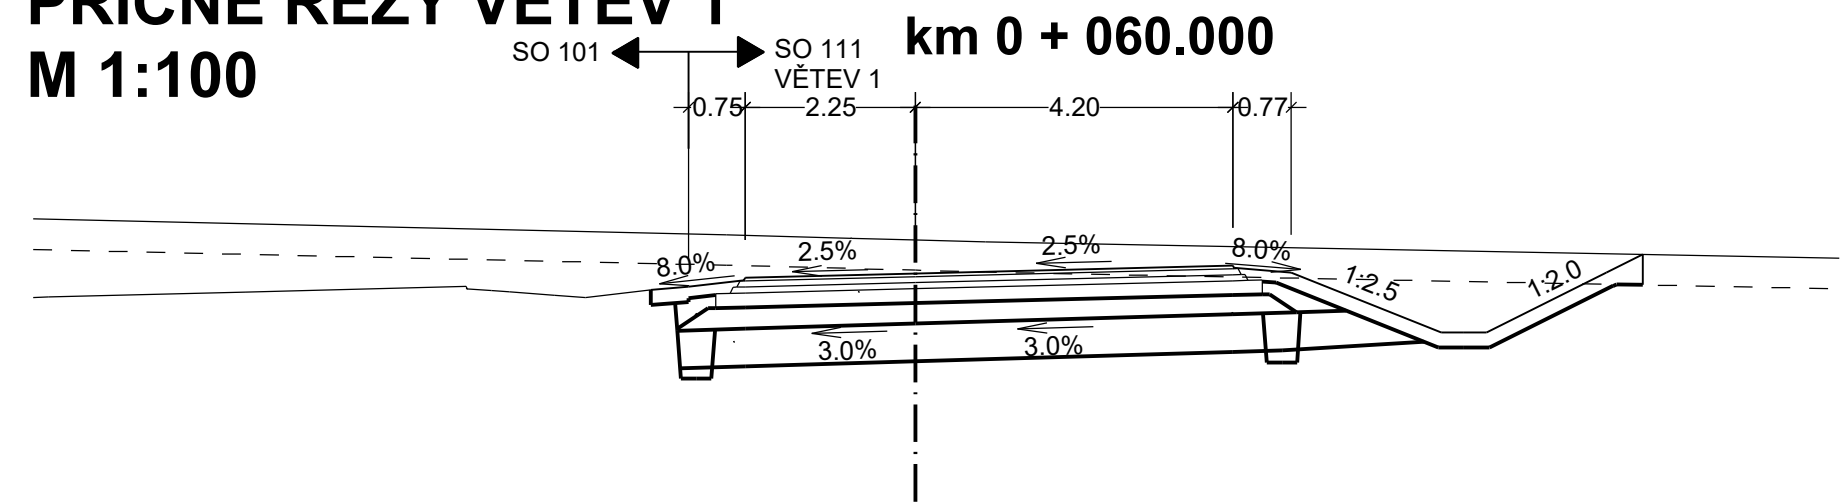
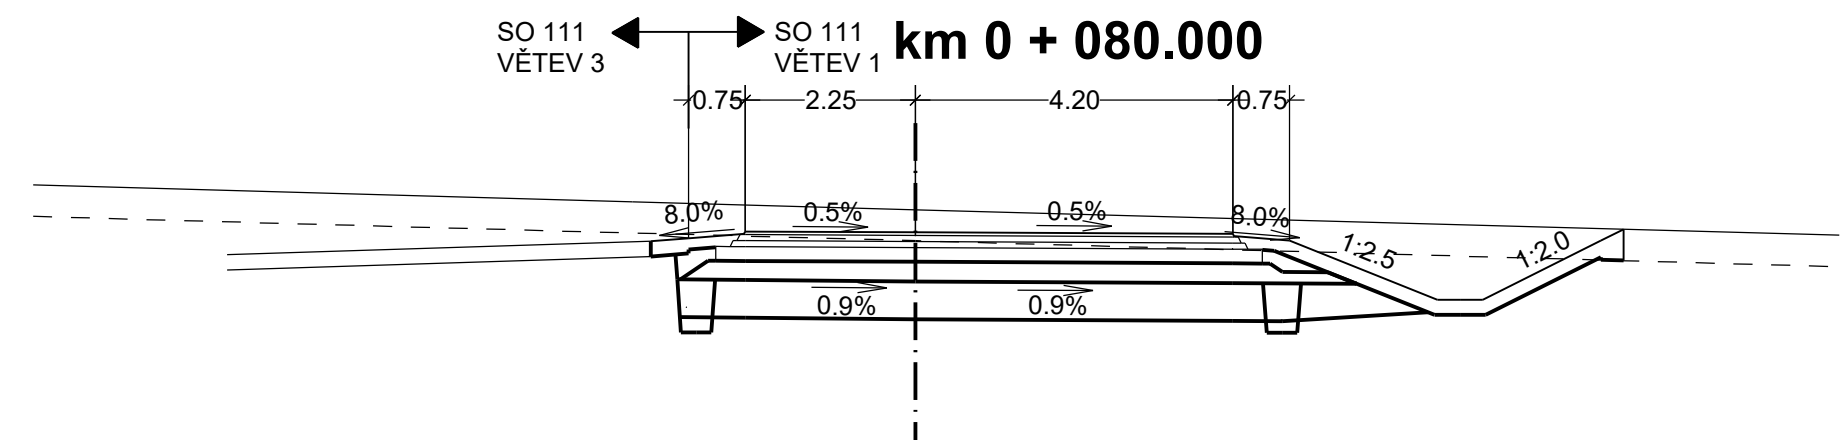
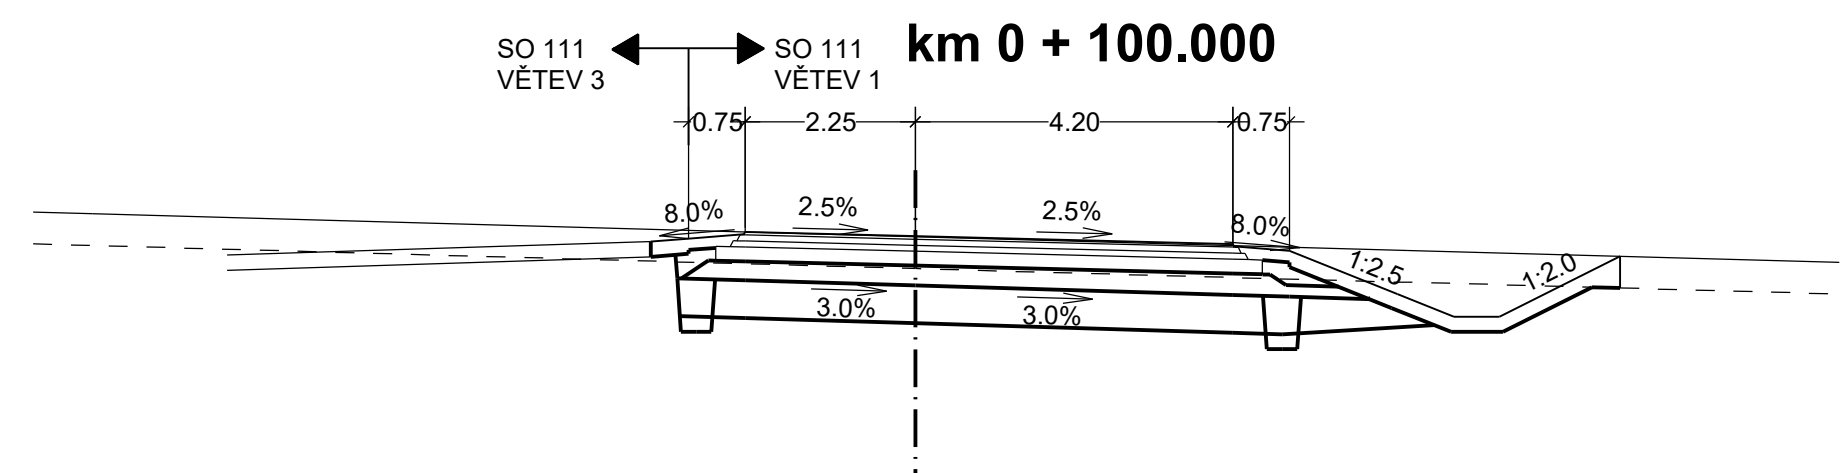


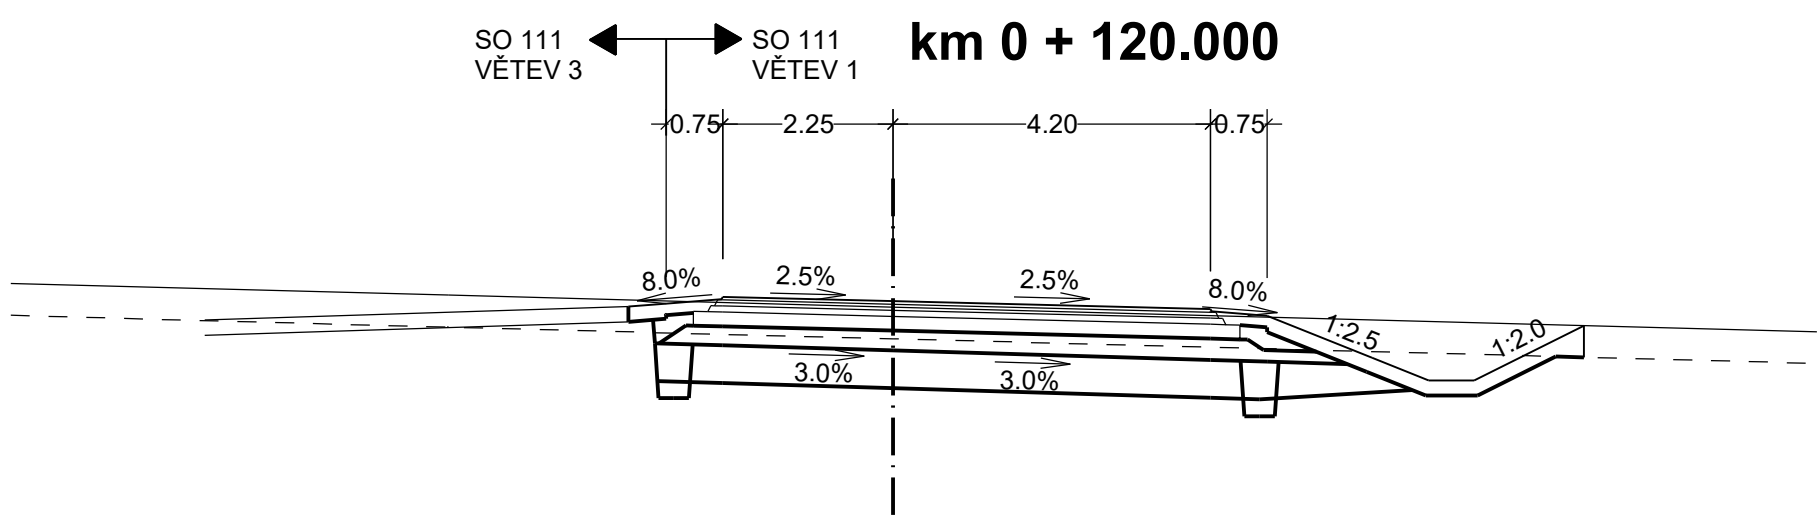
SO 111 - MÚK ŽIDNĚVES
PŘÍČNÉ ŘEZY VĚTVÍ 1
M 1:100

[illegible]

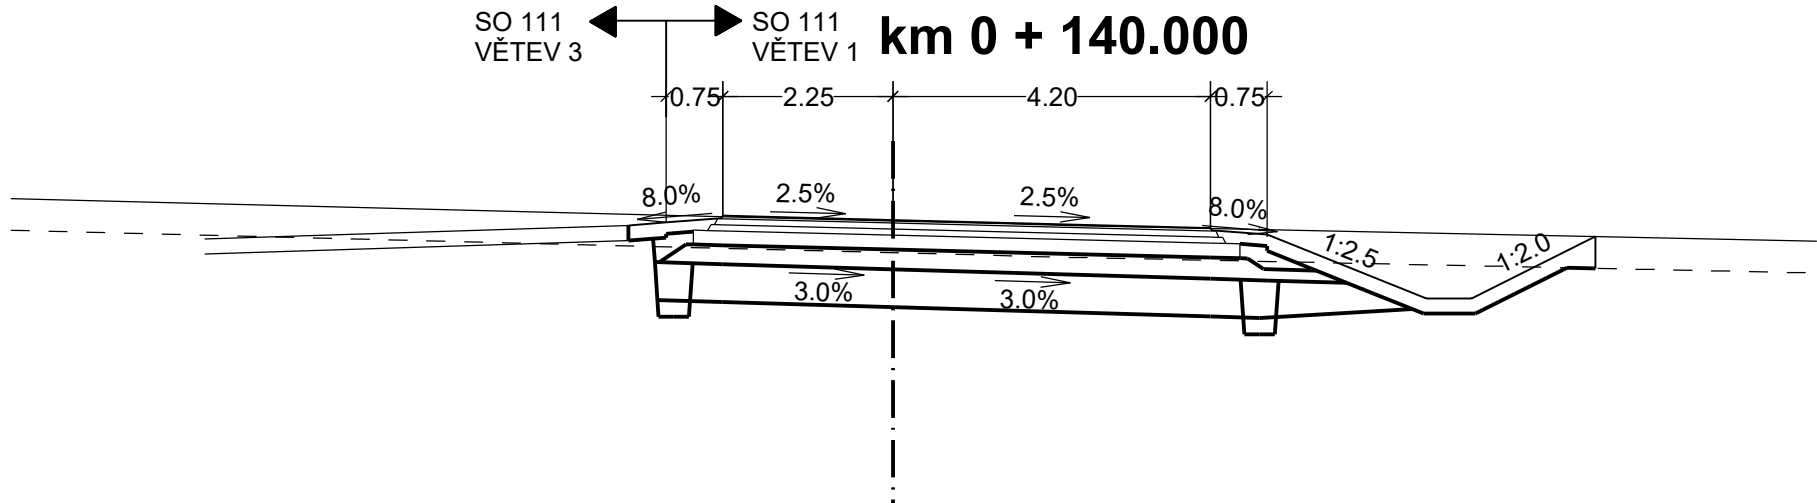
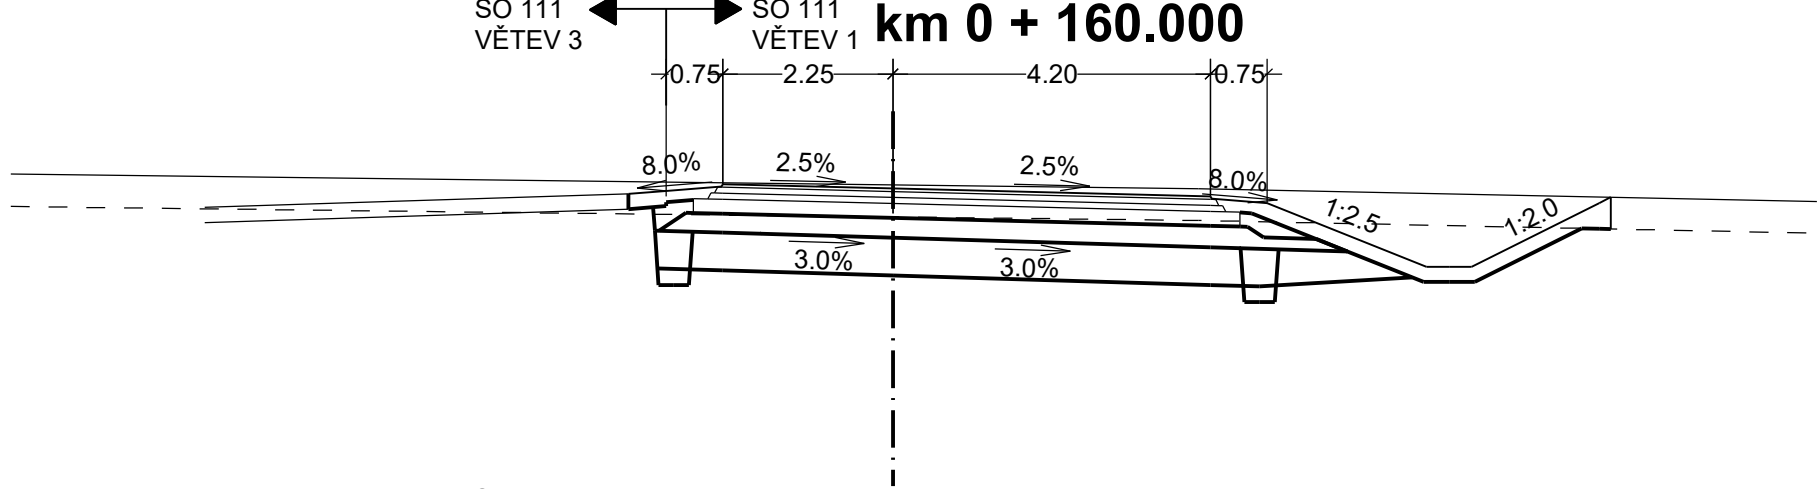
		S. R. 217 m	
PROJEKTOVANÝ STAV			
ODSAZENÍ OD OSY		-3,50 221,72 -3,00 221,76 -2,27 221,82 -2,27 221,81 -2,25 221,85	0,00 221,84
			4,20 221,82 4,22 221,78 4,22 221,79 4,95 221,73
			6,90 220,95 7,20 220,95 7,50 220,95
STÁVAJÍCÍ TERÉN		-3,74 222,24	
ODSAZENÍ OD OSY		0,00 222,14	
			9,07 221,73 9,37 221,88 9,37 221,47



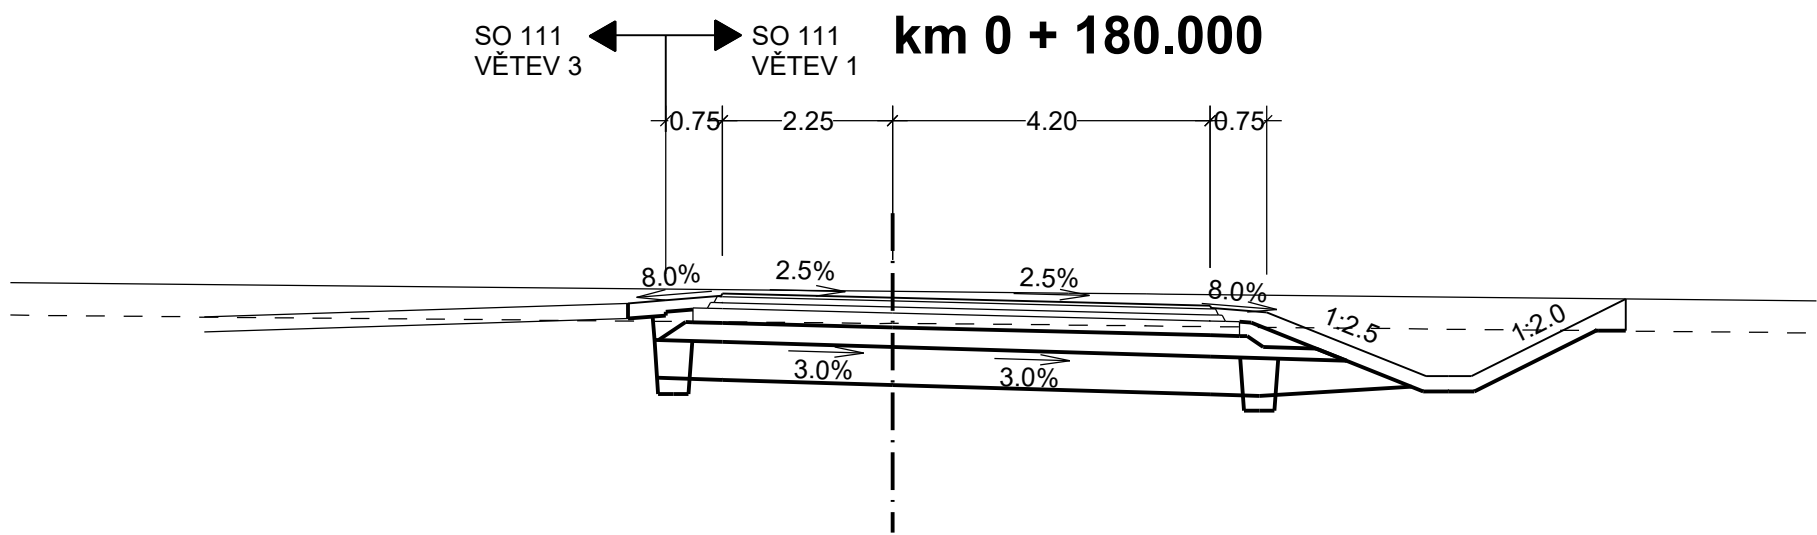
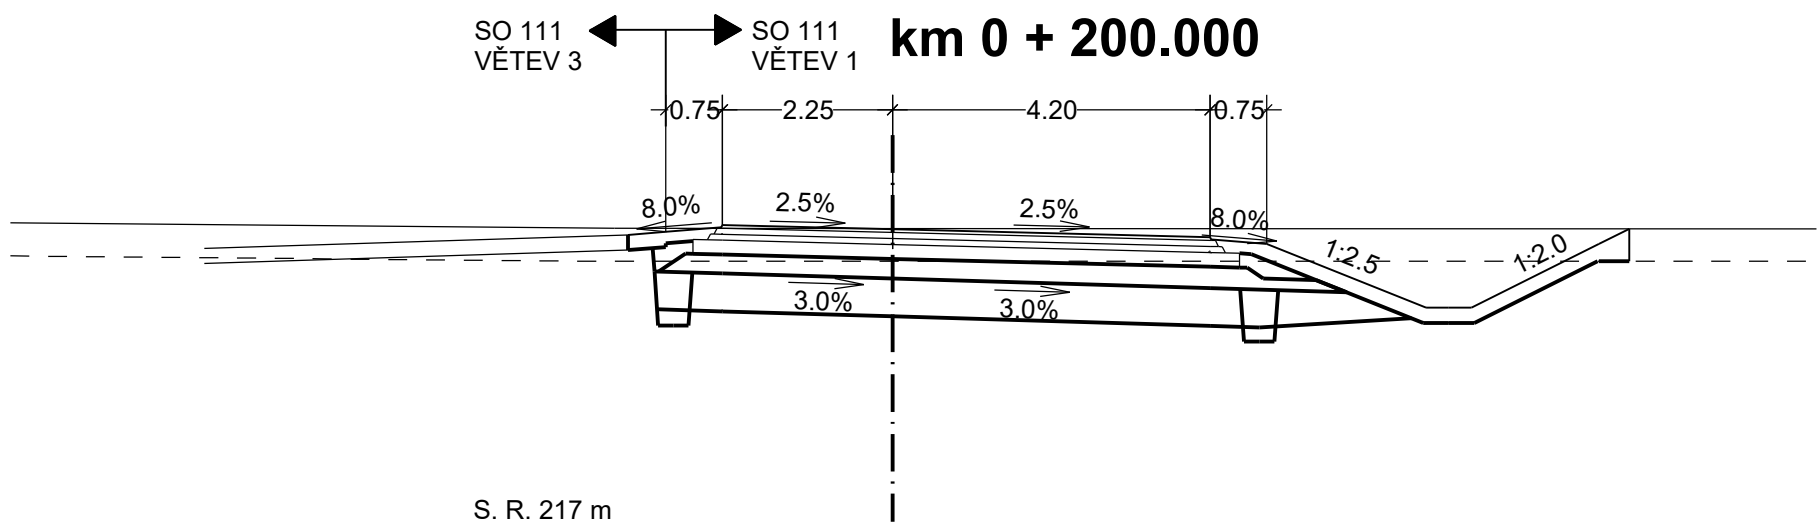
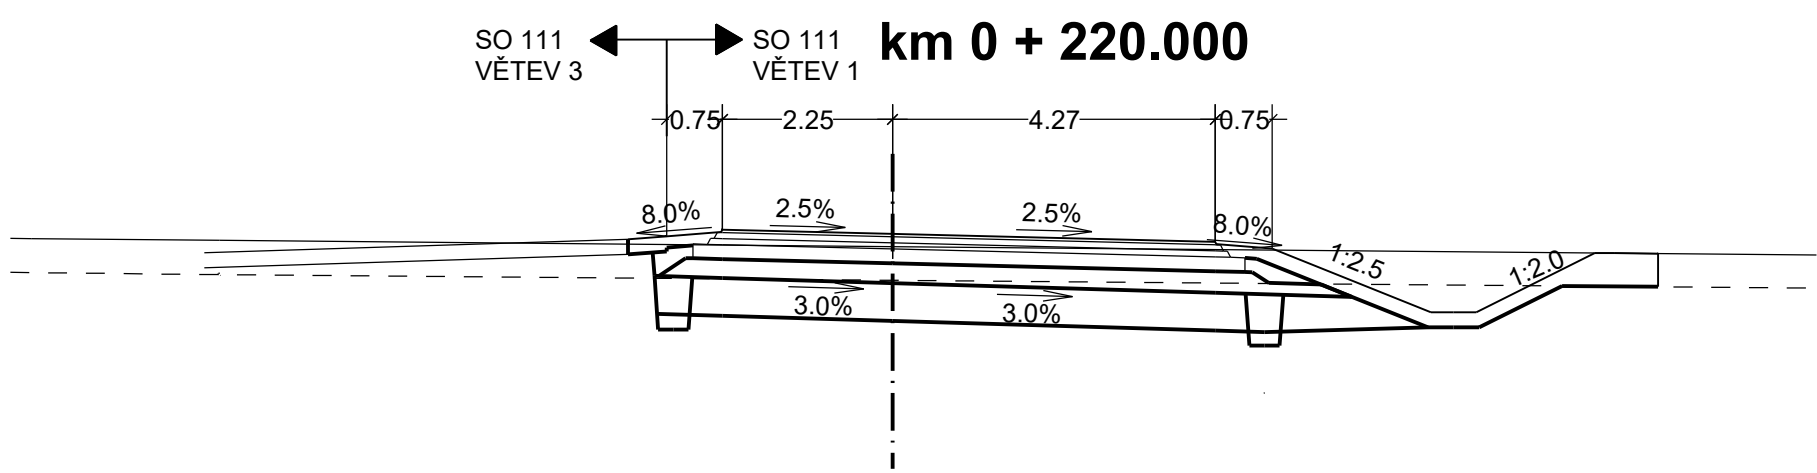
PROJEKTOVANÝ STAV	-3.50	222.10
ODSAZENÍ OD OSY	-3.00	222.14
	-2.27	222.20
	-2.27	222.19
	-2.25	222.23
	0.00	222.17
	4.20	222.06
	4.22	222.02
	4.22	222.03
	4.95	221.98
	6.38	221.41
	7.13	221.11
	7.73	221.11
	9.32	221.90
	9.32	221.48
STÁVAJÍCÍ TERÉN	0.00	222.16
ODSAZENÍ OD OSY	6.52	221.98



PROJEKTOVANÝ STAV ODSAZENÍ OD OSY	-3,50 -222,13 -3,00 -225,17 -2,27 -229,23 -2,27 -229,22 -2,25 -222,26	0,00 -222,20	4,20 -229,09 4,22 -229,05 4,22 -229,08 4,95 -222,01	6,34 -221,45 7,09 -221,15 7,69 -221,15	9,14 -221,88 9,14 -221,46
STÁVAJÍCÍ TERÉN ODSAZENÍ OD OSY	-5,88 -222,28	0,00 -222,12			

[illegible]

PROJEKTOVANÝ STAV		-3,50 221,73 -3,00 221,77 -2,97 221,83 -2,27 221,82 -2,25 221,86	0,00 221,80	4,20 221,70 4,22 221,65 4,22 221,67 4,95 221,61	7,06 220,76 7,36 220,76 7,66 220,76	9,34 221,61 9,50 221,68 9,50 221,26
ODSAZENÍ OD OSY						
STÁVAJÍCÍ TERÉN			0,00 221,85	4,04 221,80		
ODSAZENÍ OD OSY						

[illegible][illegible][illegible]

Výškový systém Bpv

SO 111	MÚK Židněves
---------------	--------------

Objednatel:



Ředitelství silnic a dálnic s. p.
Čerčanská 2023/12, Krč, 140 00 Praha 4

Zhotovitel:



Valbek, spol. s r.o.
Vaňurova 505/17
460 07 Liberec 3

HIP:

ING. T. KLIMENT



Zhotovitel:
Valbek, spol. s r.o.
Vaňurova 505/17
460 07 Liberec 3

Vypracoval	ING. A. DUMANSKA	
Zodp. projektant	ING. T. KLIMENT	
Tech. kontrola	ING. M. HANŽL	
Akce		
I/16 MLADÁ BOLESLAV - MARTINOVICE		

Příloha	PŘÍČNÉ ŘEZY VĚTEV 1
---------	---------------------

k. číslo	21-LI13-001
----------	-------------

Superň	PDPS
--------	------

Formát	10 x 17
Číslo	1:100
Prílohy	Paré

5.1