




SO 111 - MÚK ŽIDNĚVES
PŘÍČNÉ ŘEZY VĚTEV 2
M 1:100

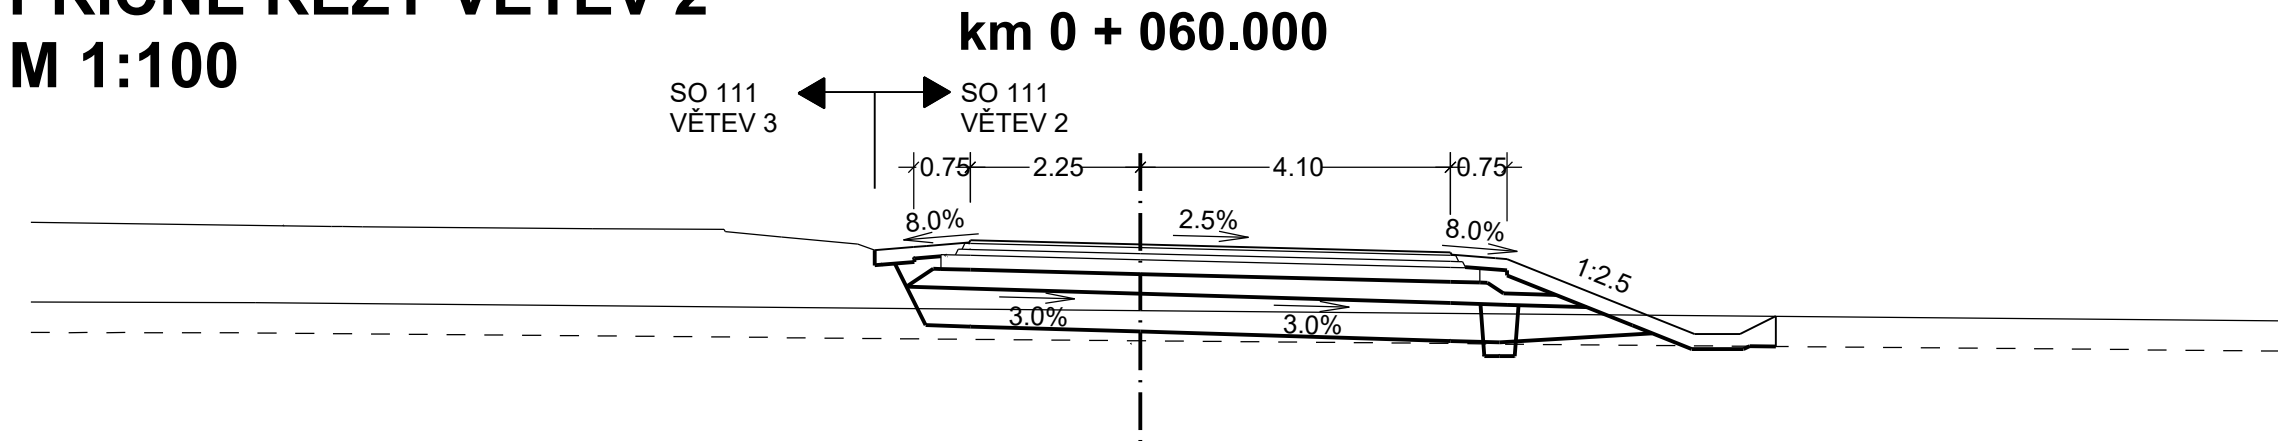


KÓTY NOVÉHO STAVU	S. R. 220 m
VZDÁLENOST OD OSY	-3.50 224.04 -3.00 224.08 -2.64 224.11 -2.27 224.14 -2.27 224.13 -2.25 224.17
KÓTY TERÉNU	0.00 224.11
VZDÁLENOST OD OSY	4.10 224.01 4.12 223.97 4.12 223.98 4.49 223.95 4.85 223.92 6.70 223.18 7.33 222.93 7.93 222.93 8.40 222.76

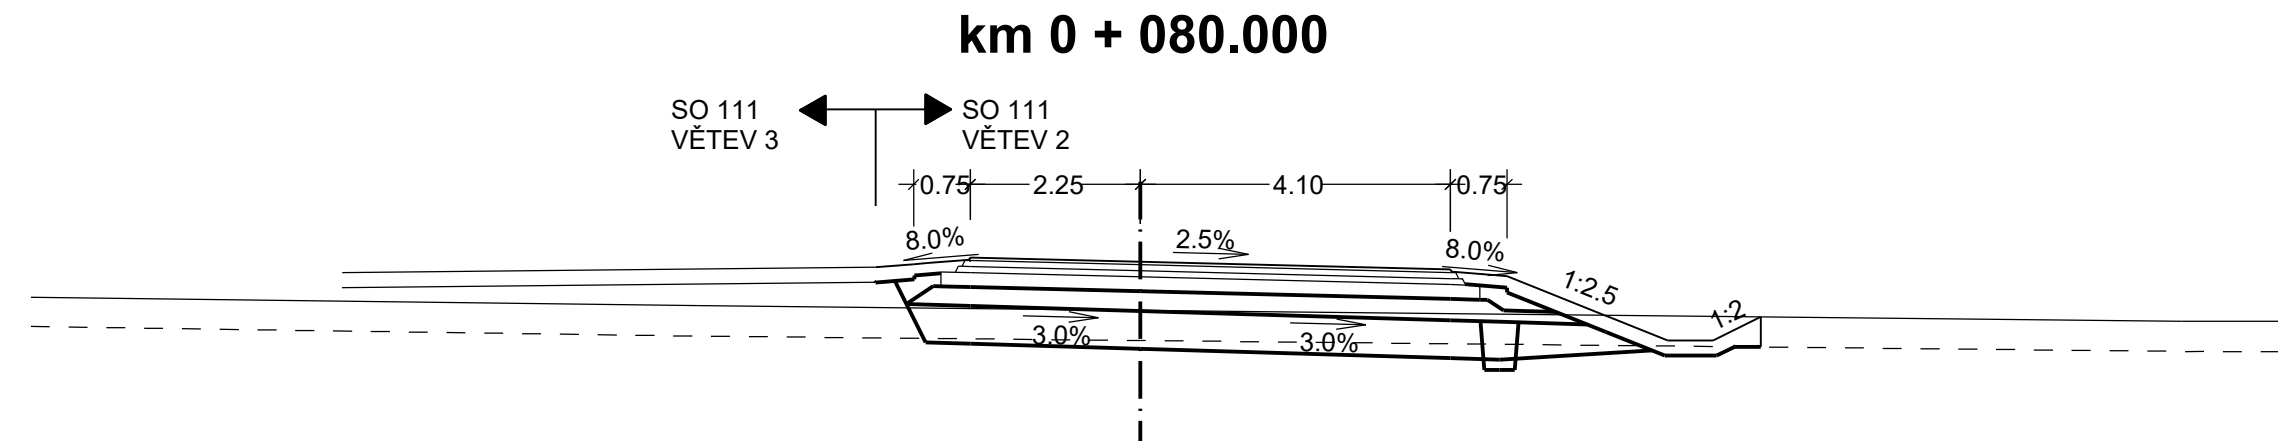


KÓTY NOVÉHO STAVU	S. R. 220 m
VZDÁLENOST OD OSY	-3.50 224.10 -3.00 224.14 -2.64 224.17 -2.27 224.20 -2.27 224.19 -2.25 224.23
KÓTY TERÉNU	0.00 223.53
VZDÁLENOST OD OSY	4.10 224.07 4.12 224.03 4.12 224.04 4.49 224.01 4.85 223.98 6.14 223.46 6.23 223.43 6.98 223.13 7.58 223.13 8.20 223.44 8.20 223.04

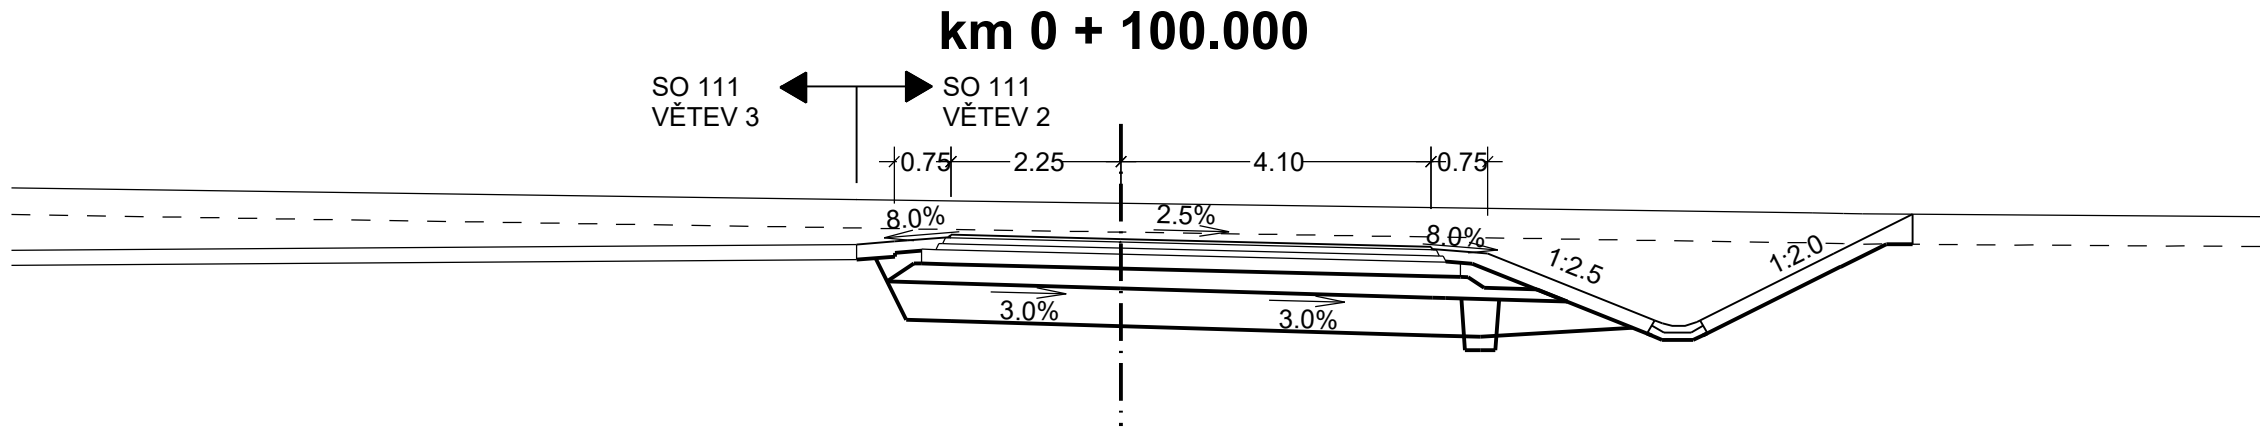


KÓTY NOVÉHO STAVU	S. R. 219 m
VZDÁLENOST OD OSY	-3.50 223.27 -3.00 223.31 -2.64 223.34 -2.27 223.37 -2.27 223.36 -2.25 223.40
KÓTY TERÉNU	0.00 223.82
VZDÁLENOST OD OSY	4.10 223.24 4.12 223.20 4.12 223.21 4.49 223.18 4.85 223.15 7.06 222.27 7.36 222.27 7.96 222.27 10.47 223.67 10.47 223.28

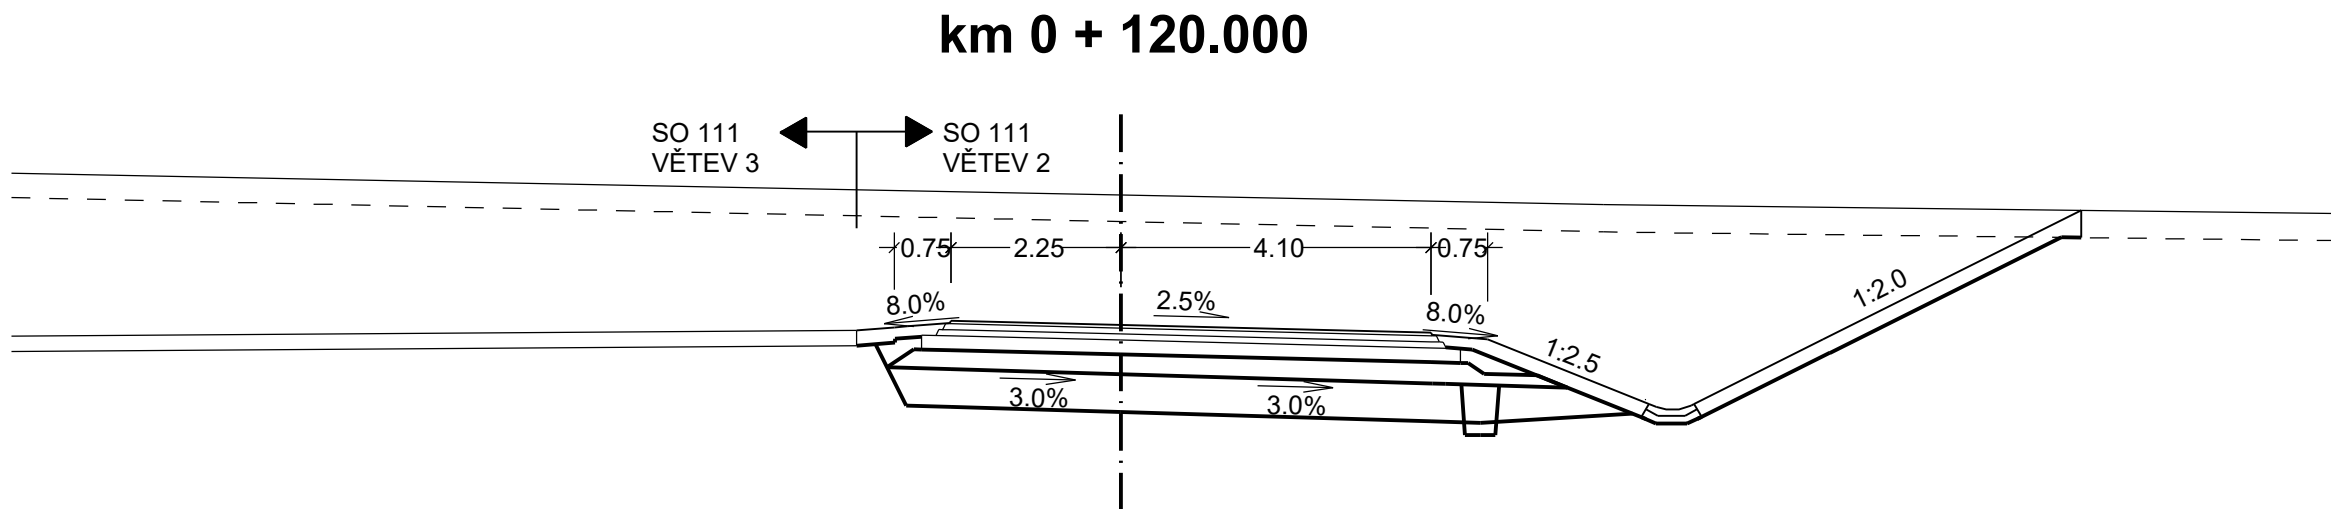

KÓTY NOVÉHO STAVU	S. R. 218 m
VZDÁLENOST OD OSY	-3.50 222.16 -3.00 222.20 -2.64 222.23 -2.27 222.26 -2.27 222.25 -2.25 222.29
KÓTY TERÉNU	0.00 223.95
VZDÁLENOST OD OSY	4.10 222.13 4.12 222.09 4.12 222.10 4.49 222.07 4.85 222.04 6.38 223.83 6.98 221.19 7.28 221.19 7.58 221.19 9.29 222.04 12.70 223.75 12.70 223.39

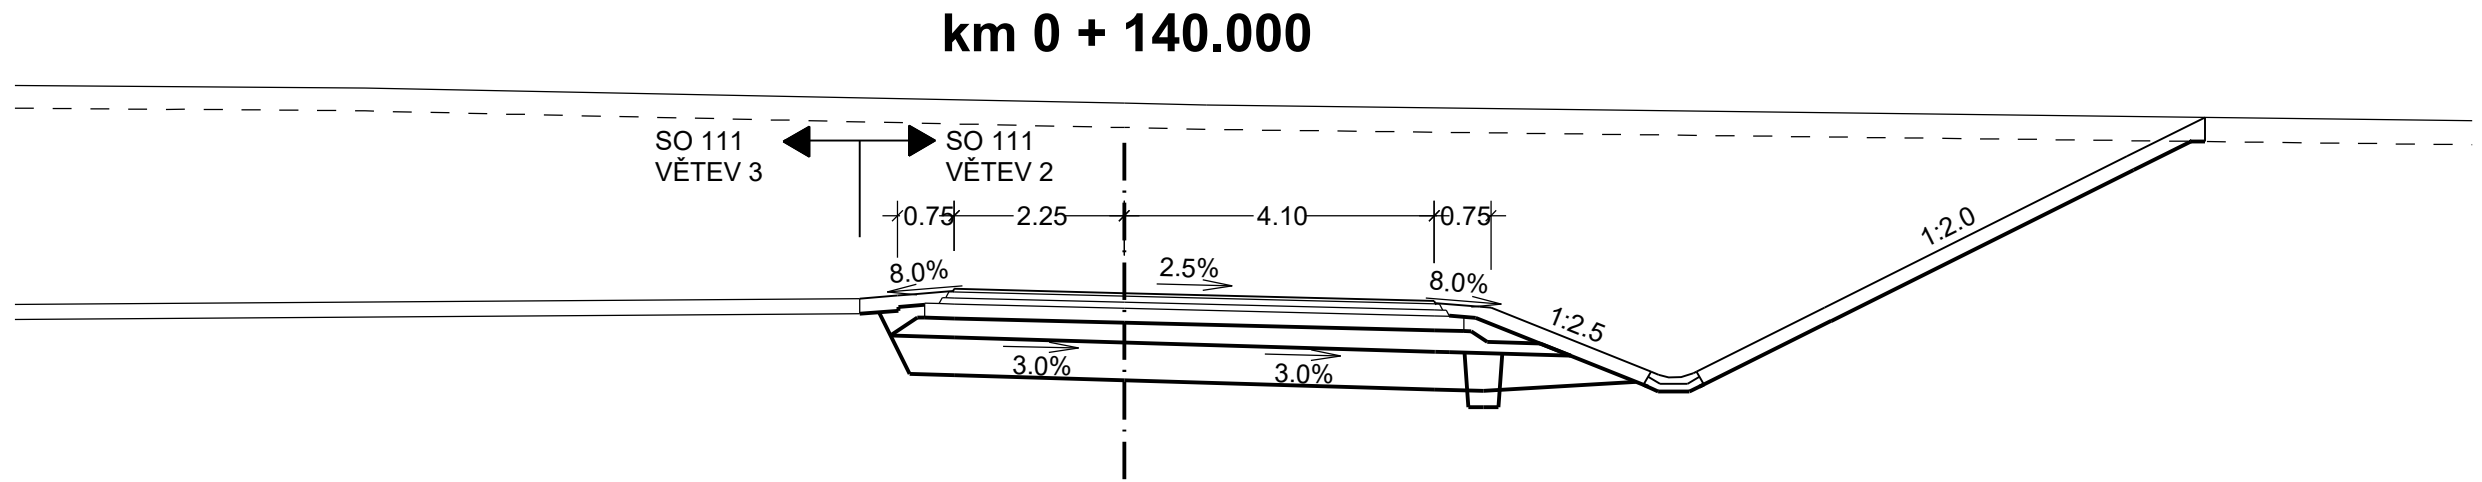

KÓTY NOVÉHO STAVU	S. R. 217 m
VZDÁLENOST OD OSY	-3.50 221.42 -3.00 221.46 -2.64 221.49 -2.27 221.52 -2.27 221.51 -2.25 221.55
KÓTY TERÉNU	0.00 224.00
VZDÁLENOST OD OSY	4.10 221.39 4.12 221.35 4.12 221.36 4.49 221.33 4.85 221.30 6.97 220.45 7.27 220.45 7.57 220.45 9.26 221.30 13.26 223.30 14.29 223.81 14.29 223.49

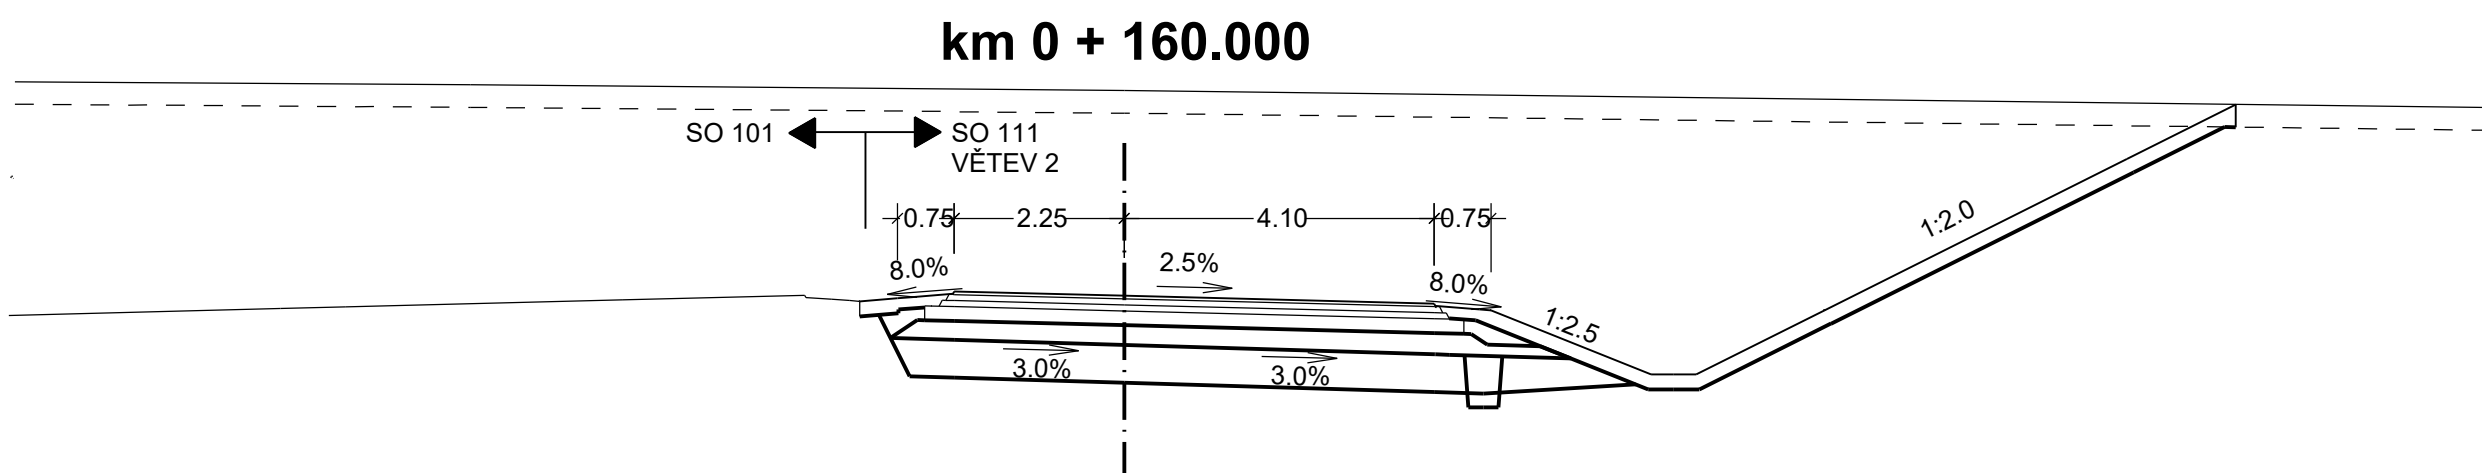

KÓTY NOVÉHO STAVU	S. R. 217 m
VZDÁLENOST OD OSY	-3.50 221.07 -3.00 221.11 -2.64 221.14 -2.27 221.17 -2.27 221.16 -2.25 221.20
KÓTY TERÉNU	-8.65 223.93
VZDÁLENOST OD OSY	4.10 221.04 4.12 221.00 4.12 221.01 4.49 220.98 4.85 220.95 6.97 220.11 7.27 220.11 7.57 220.11 9.26 220.95 13.26 222.95 14.70 223.67

Výškový systém Bpv

SO 111 MÚK Židněves

Objednatel:



Ředitelství silnic a dálnic s. p.
Čerčanská 2023/12, Krč, 140 00 Praha 4

Zhotovitel:



Valbek, spol. s r.o.
Vaňurova 505/17
460 07 Liberec 3

HIP:

ING. T. KLIMENT



Zhotovitel:
Valbek, spol. s r.o.
Vaňurova 505/17
460 07 Liberec 3

Příloha

I/16 MLADÁ BOLESLAV - MARTINOVICE

5.2

Vypracoval	ING. A. DUMANSKA	Zak. číslo	21-L113-001	
Zodp. projektant	ING. T. KLIMENT	Datum	02/2025	
Tech. kontrola	ING. M. HANŽL	Stupeň	PDPS	
Akce	I/16 MLADÁ BOLESLAV - MARTINOVICE		Počet formátů	6 x A4
			Měřítko	1:100
			Č. přílohy	Paré