
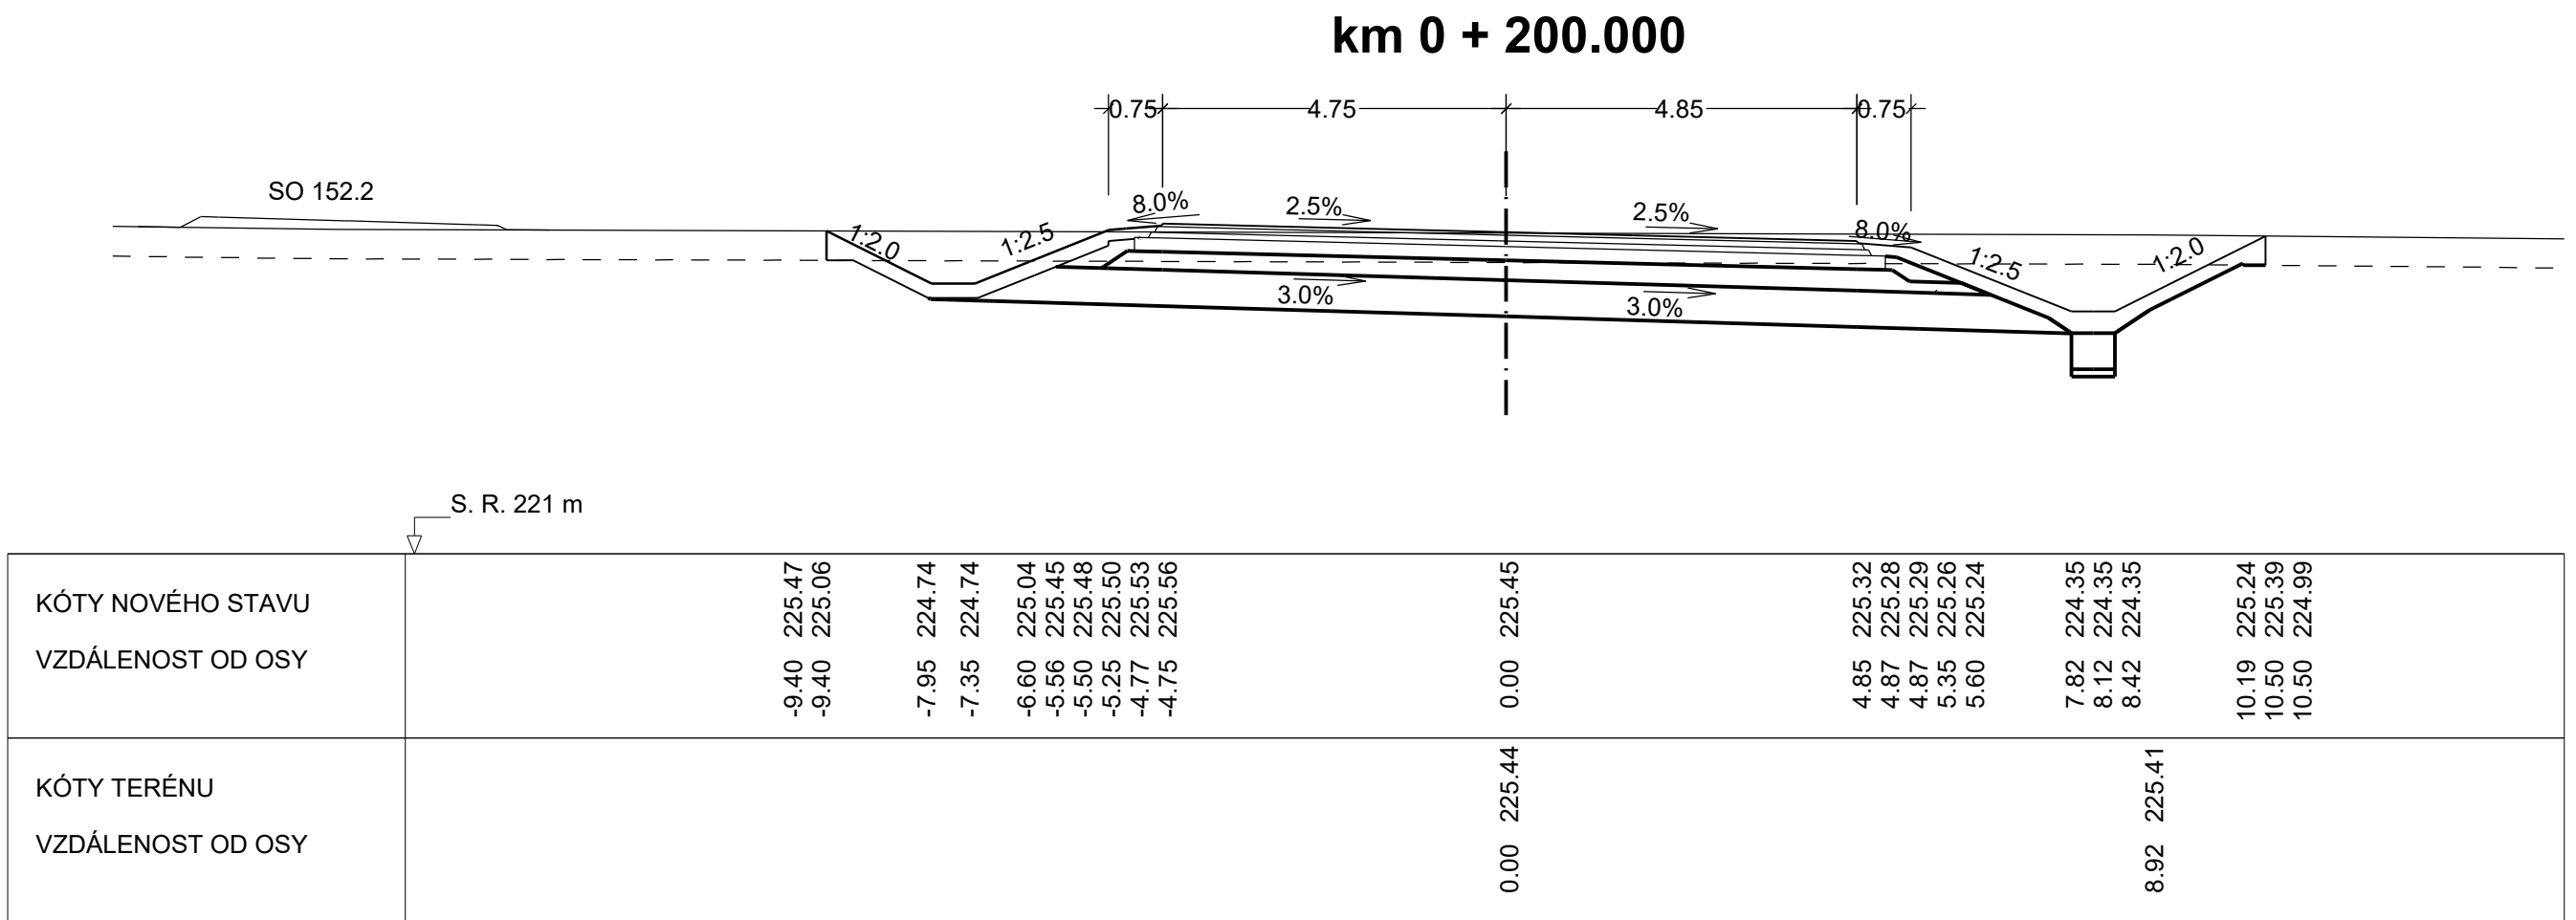
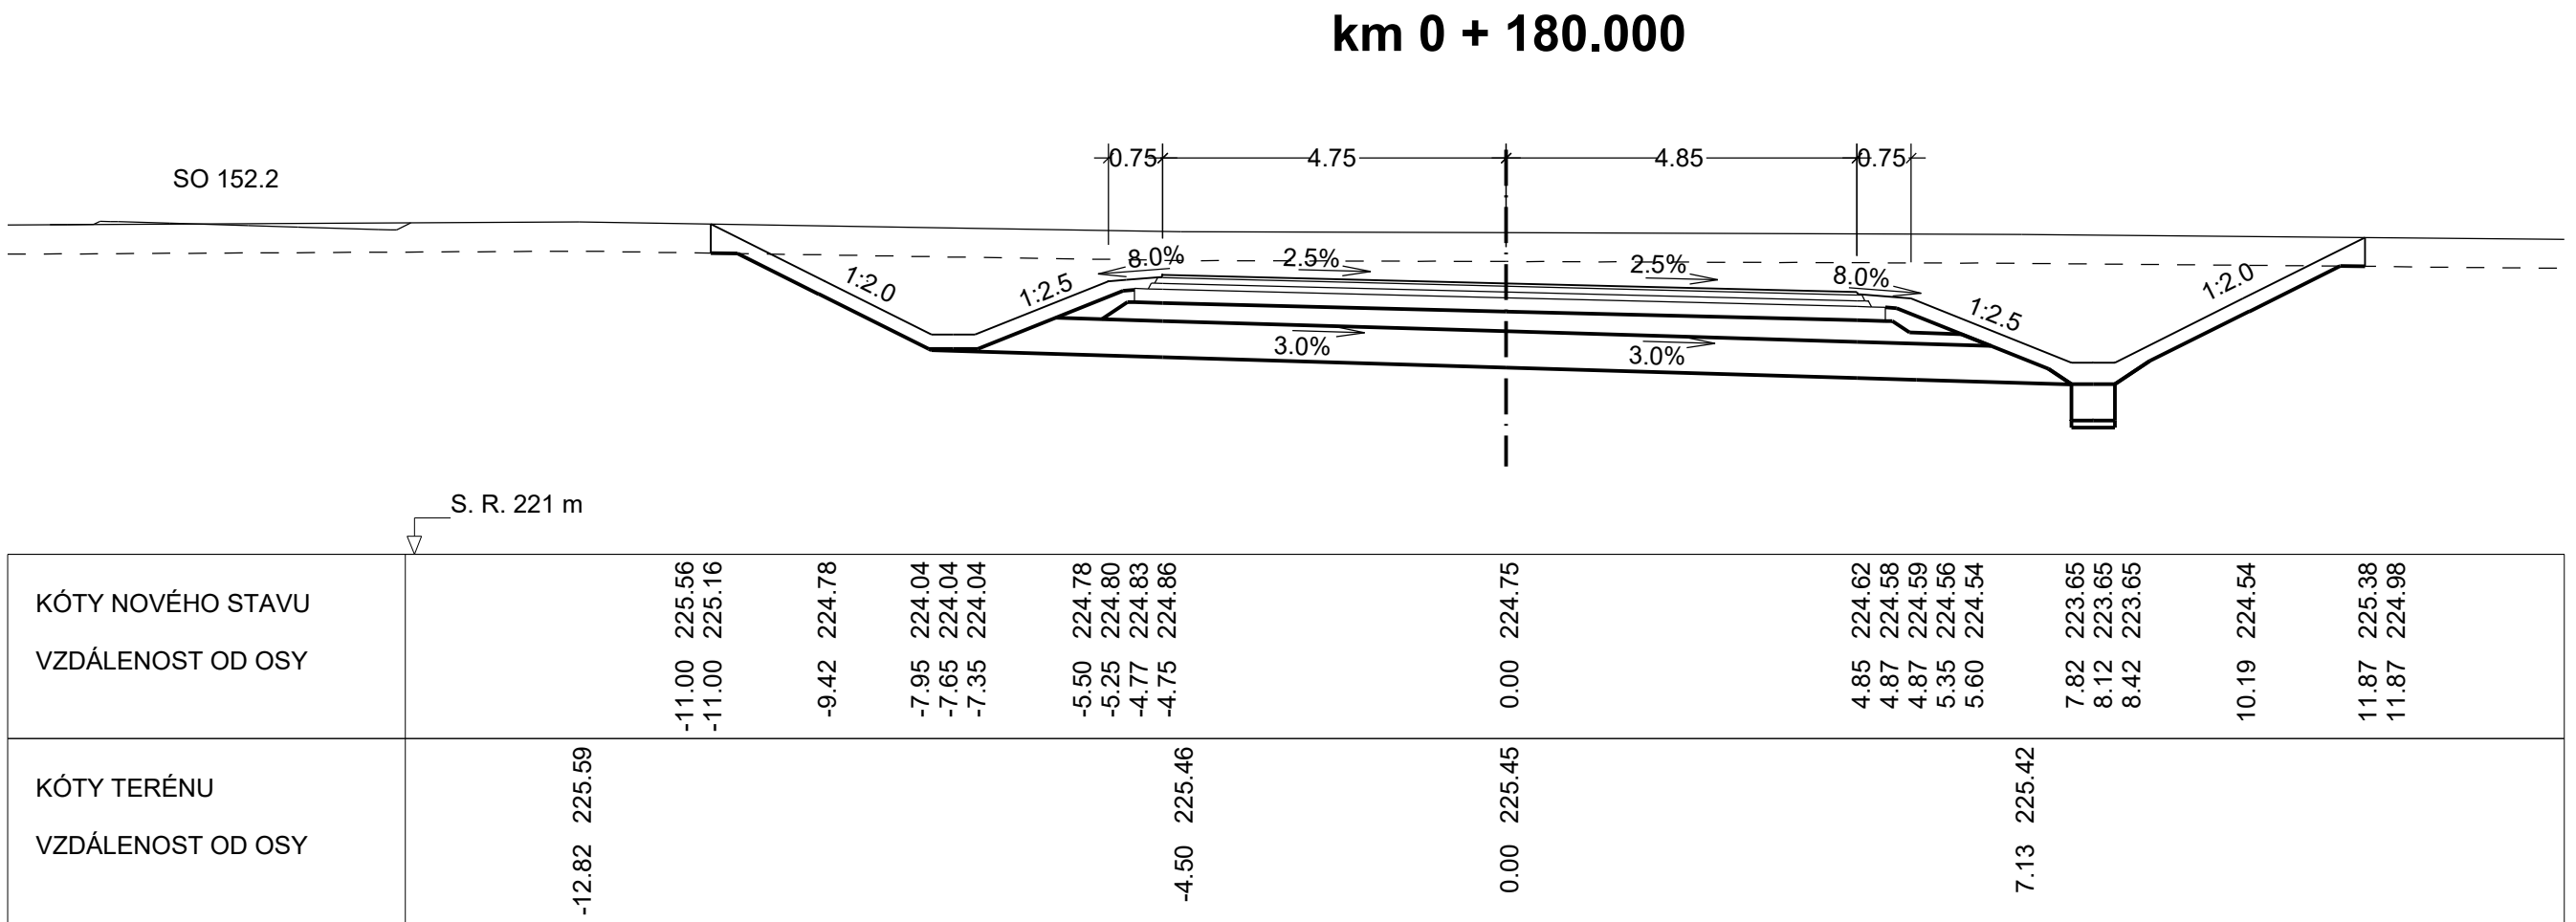
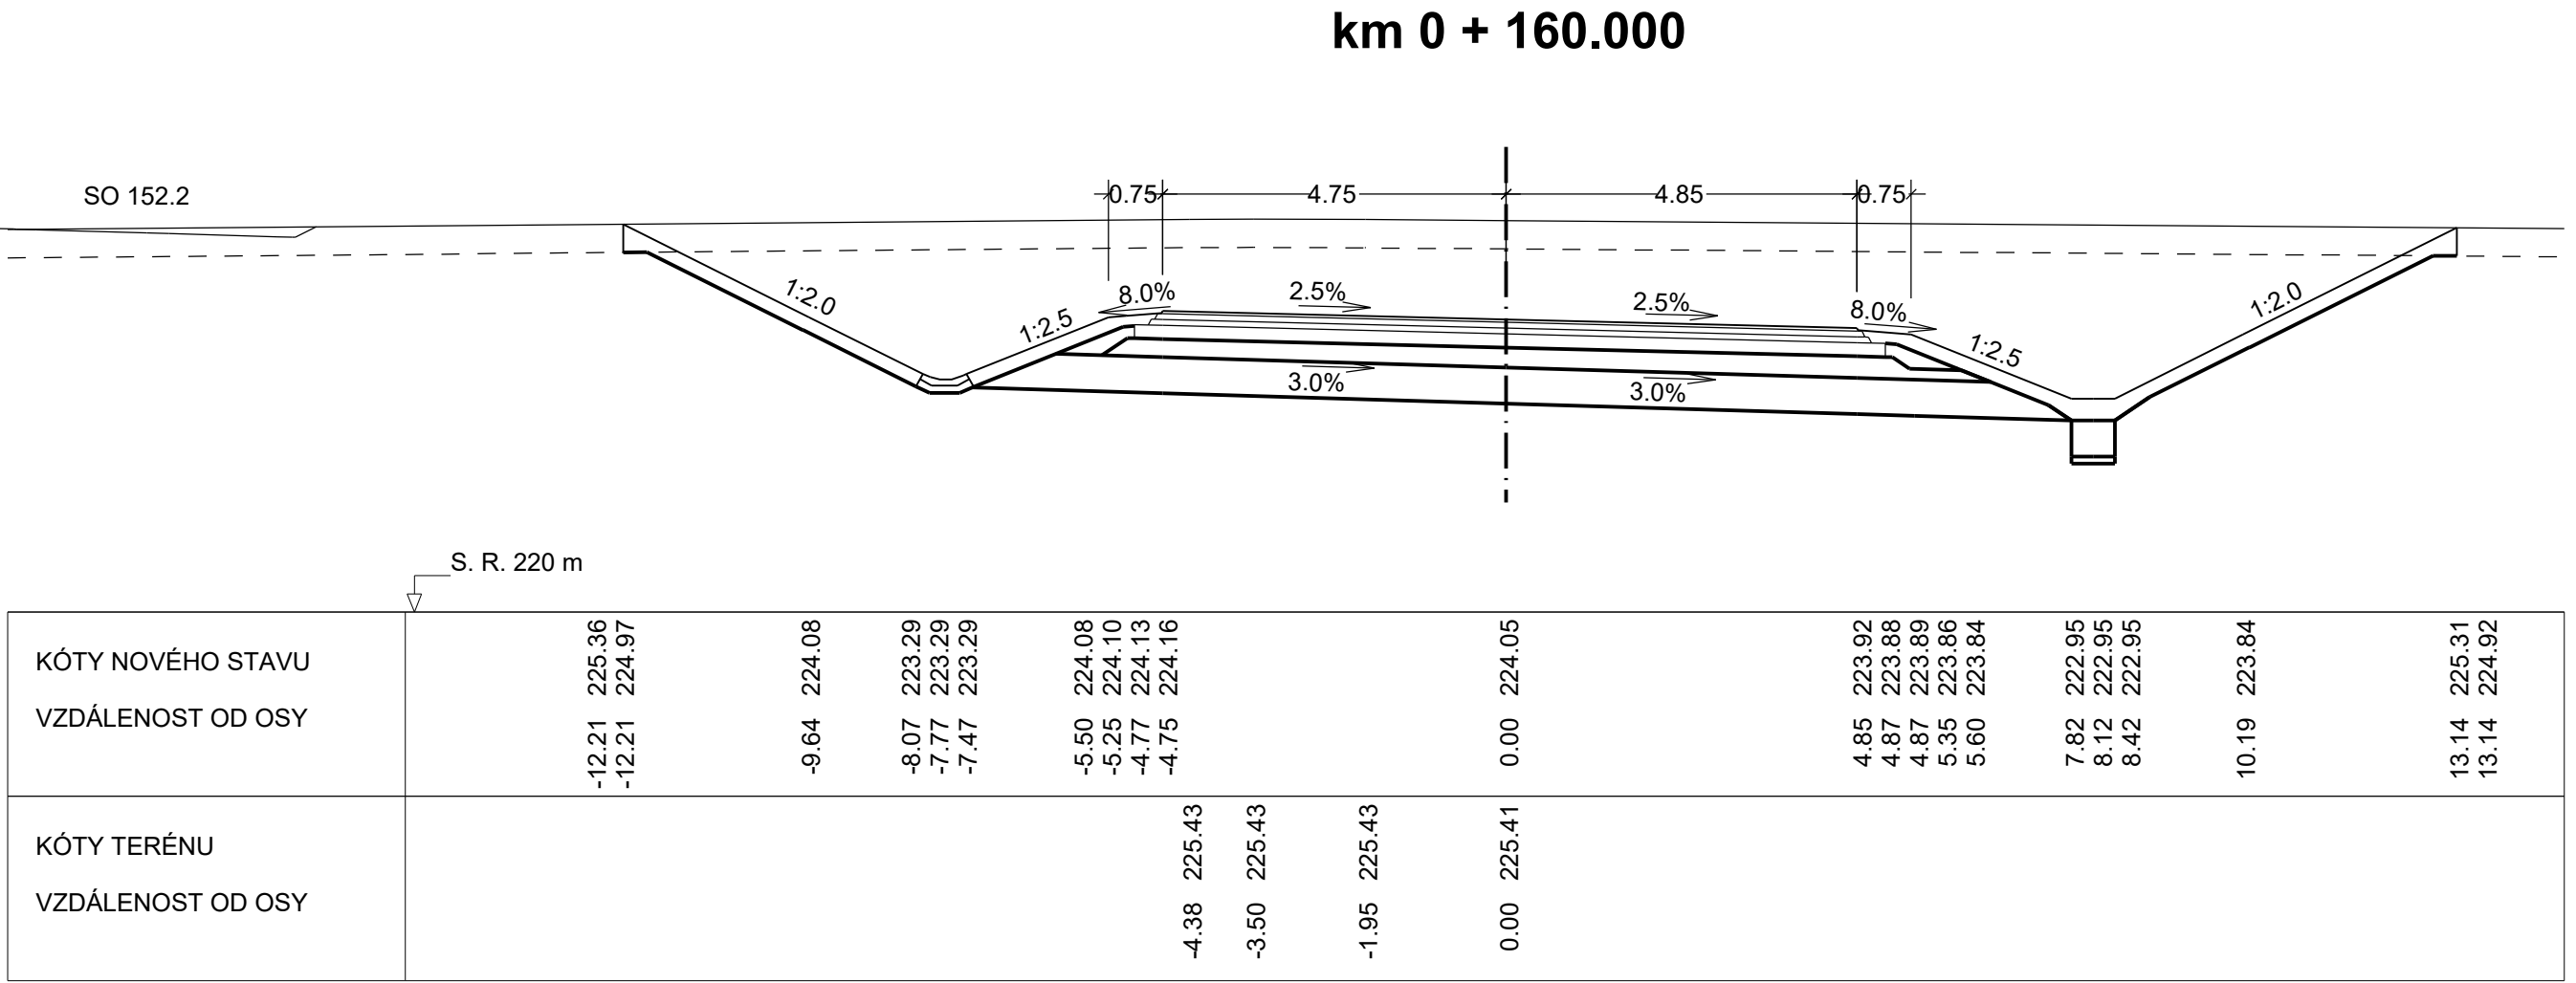
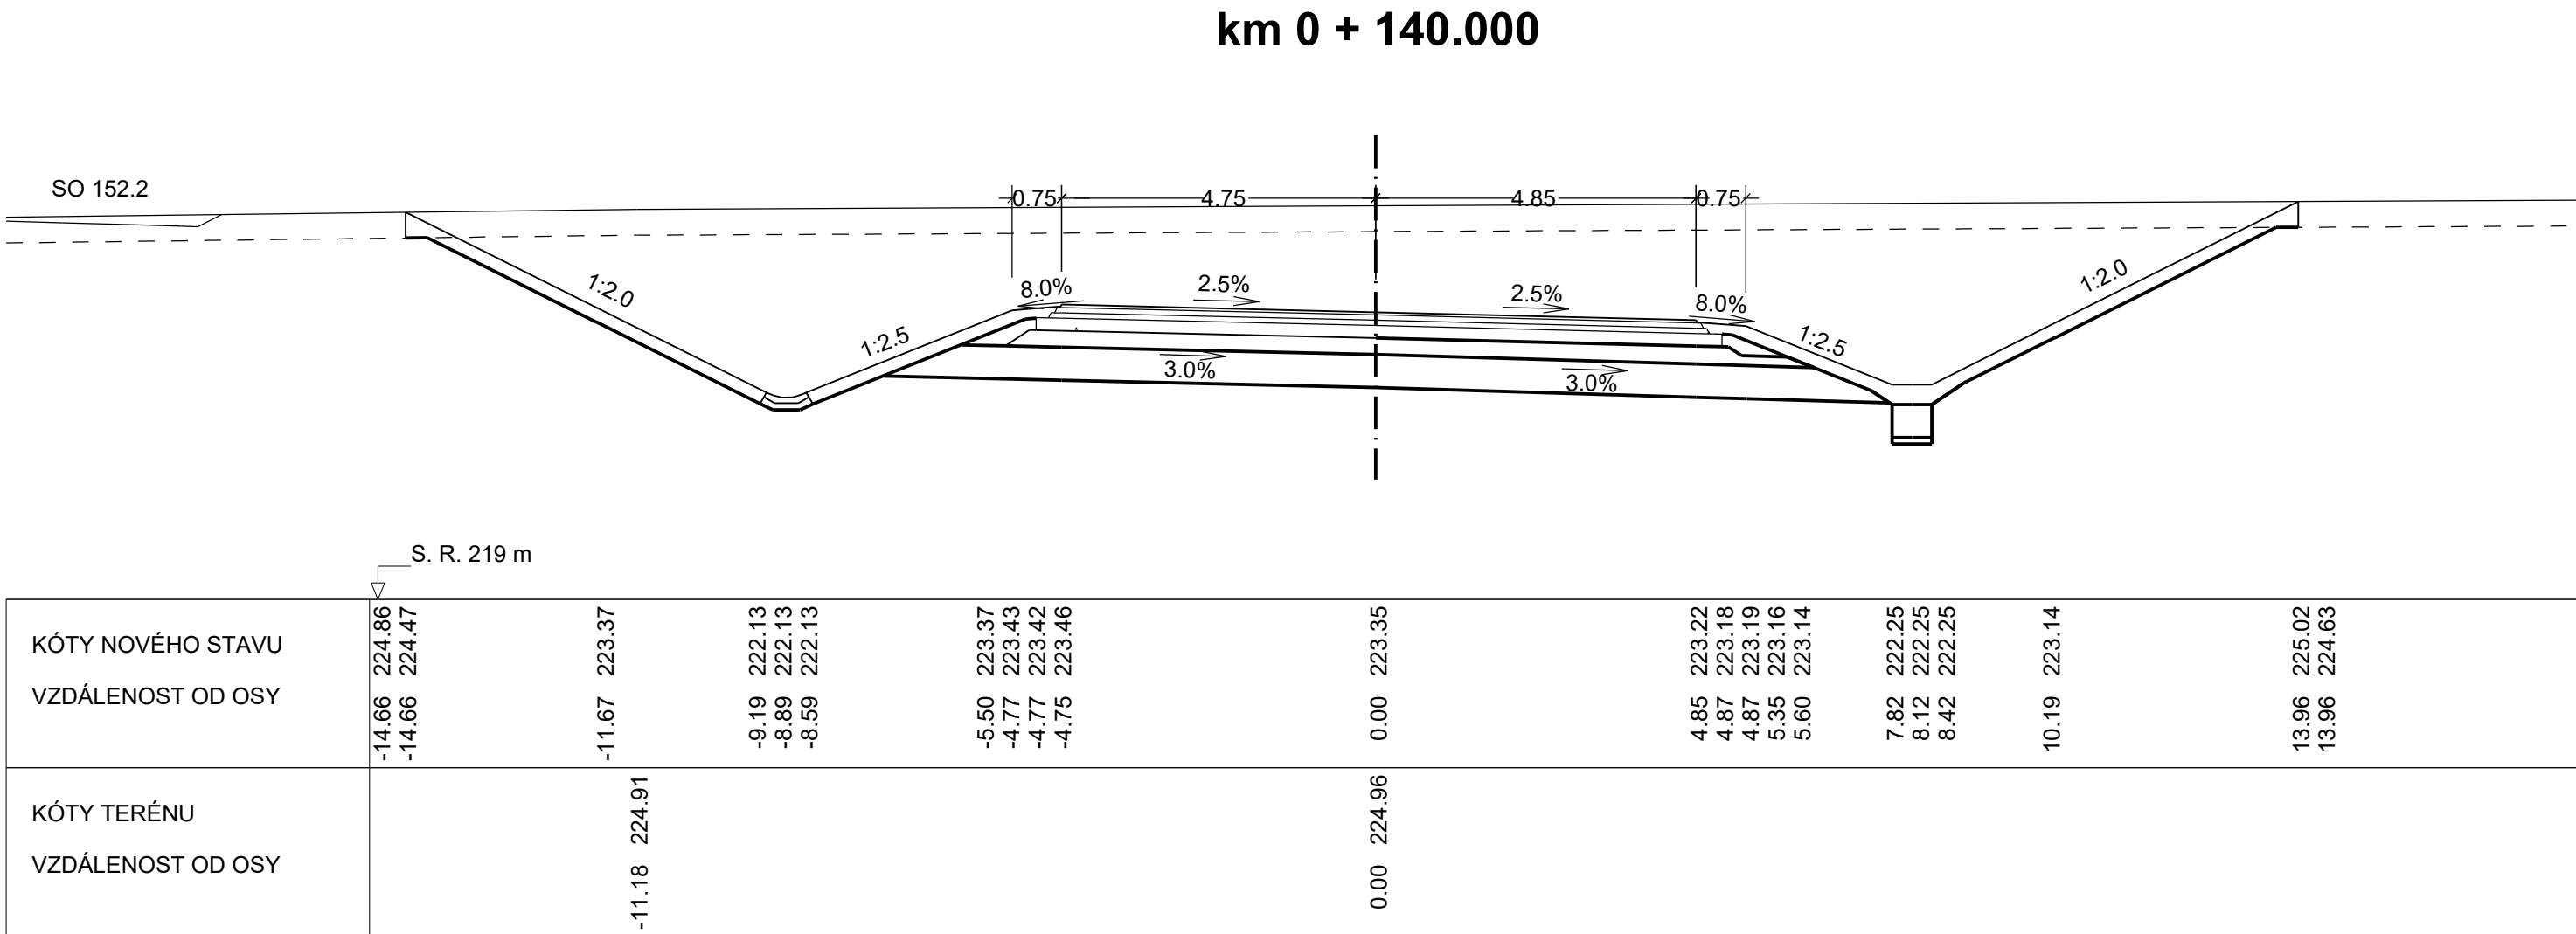
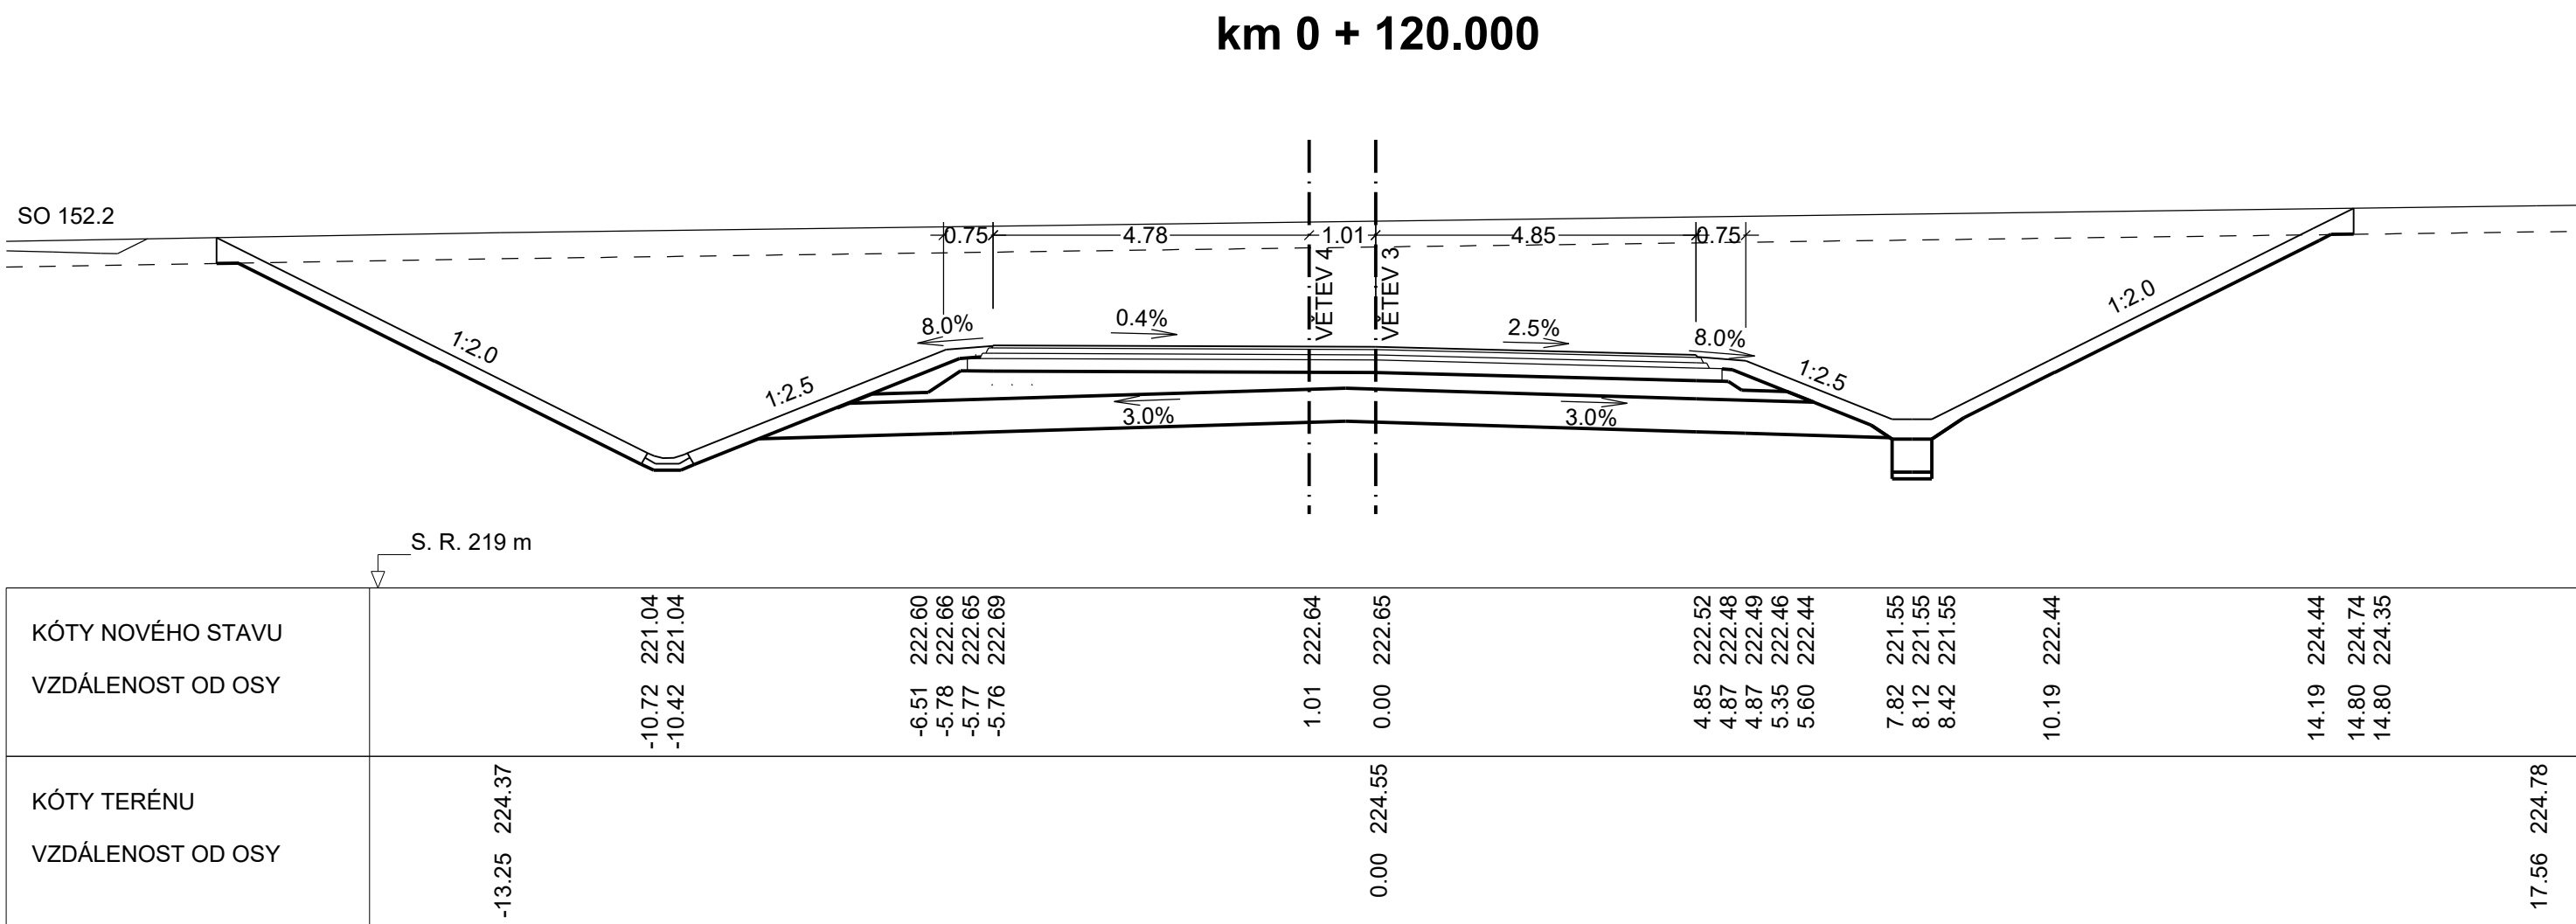
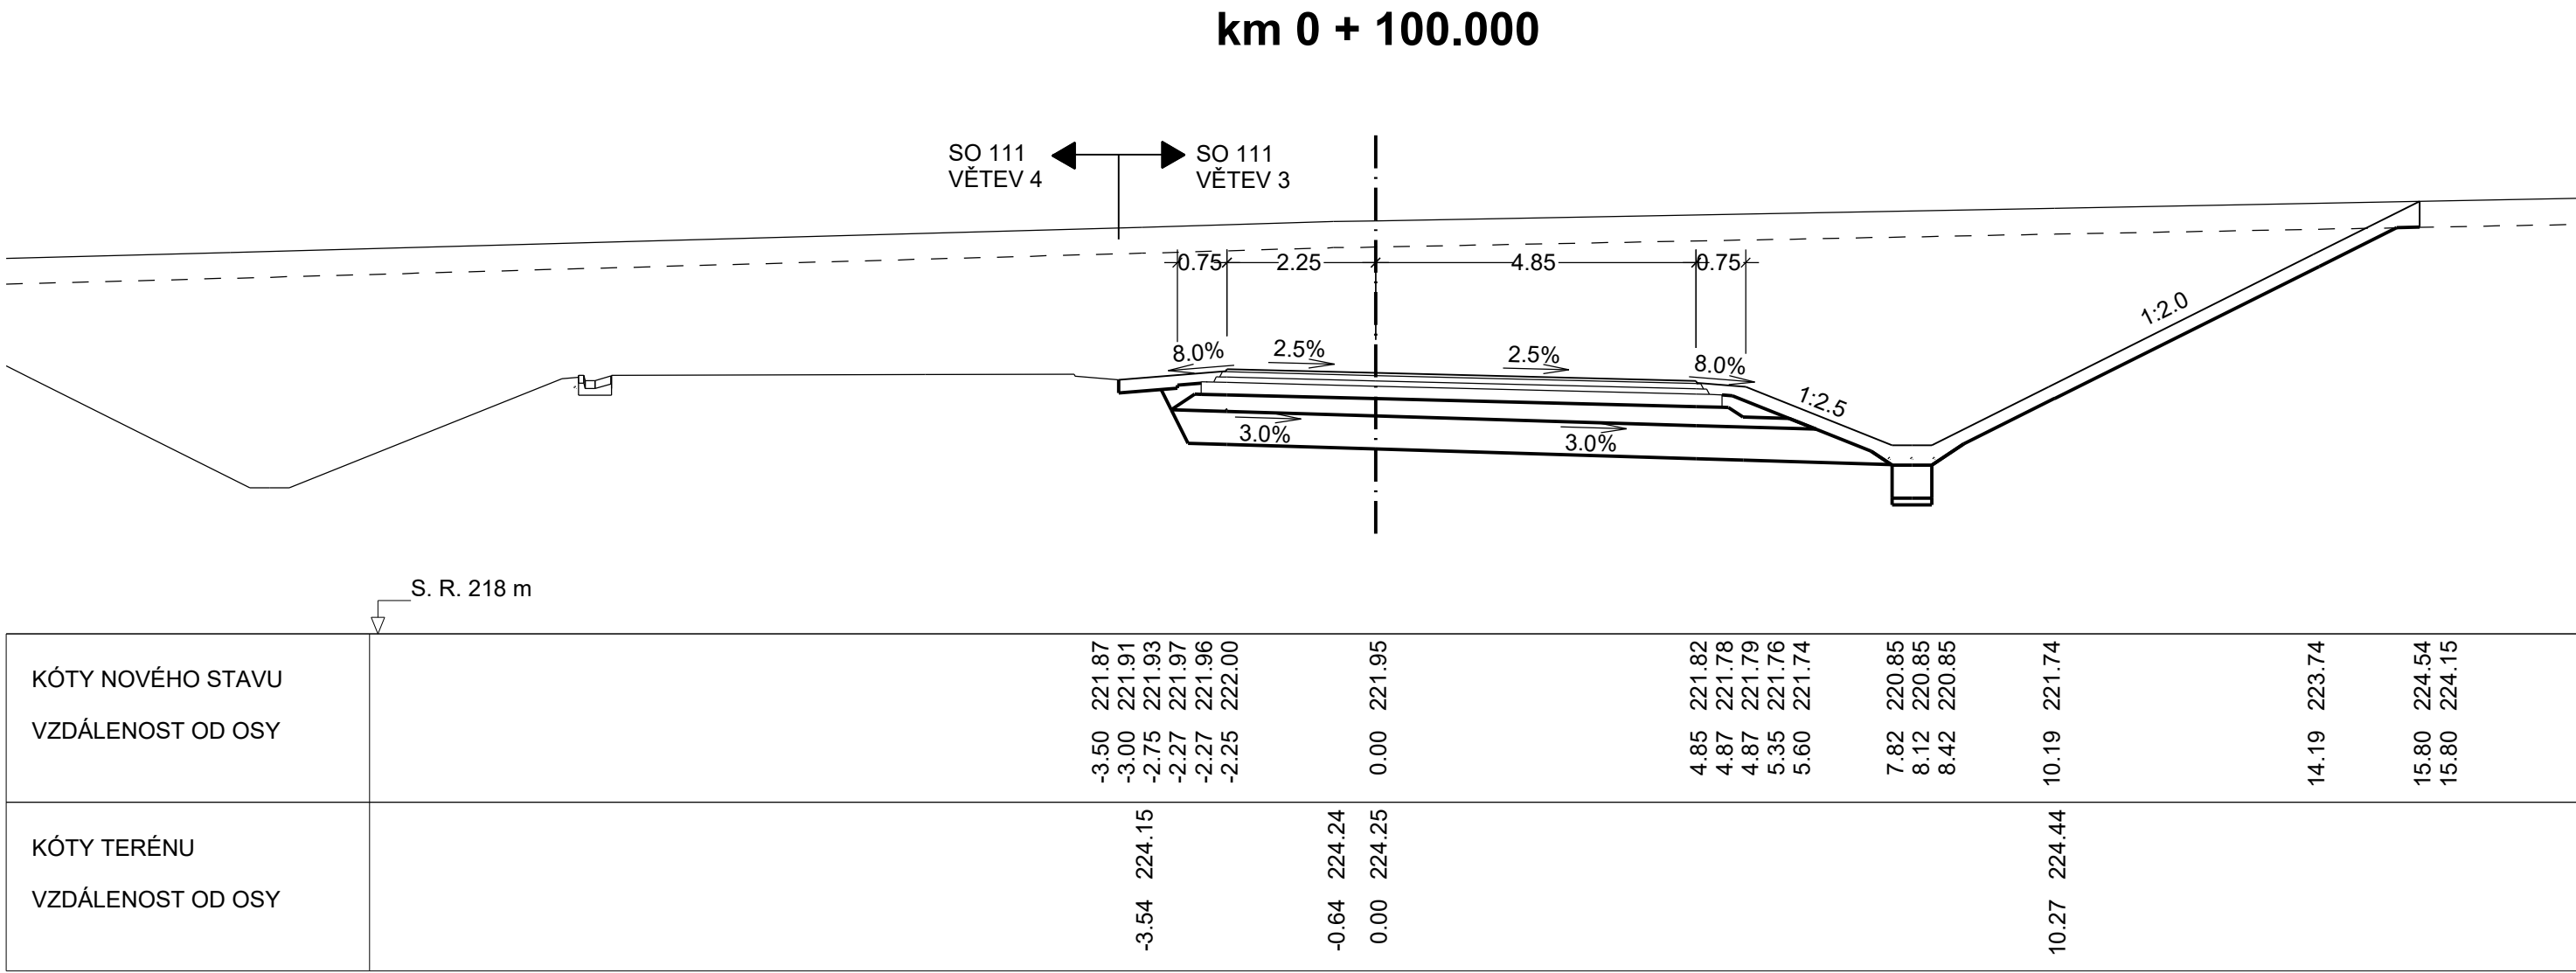
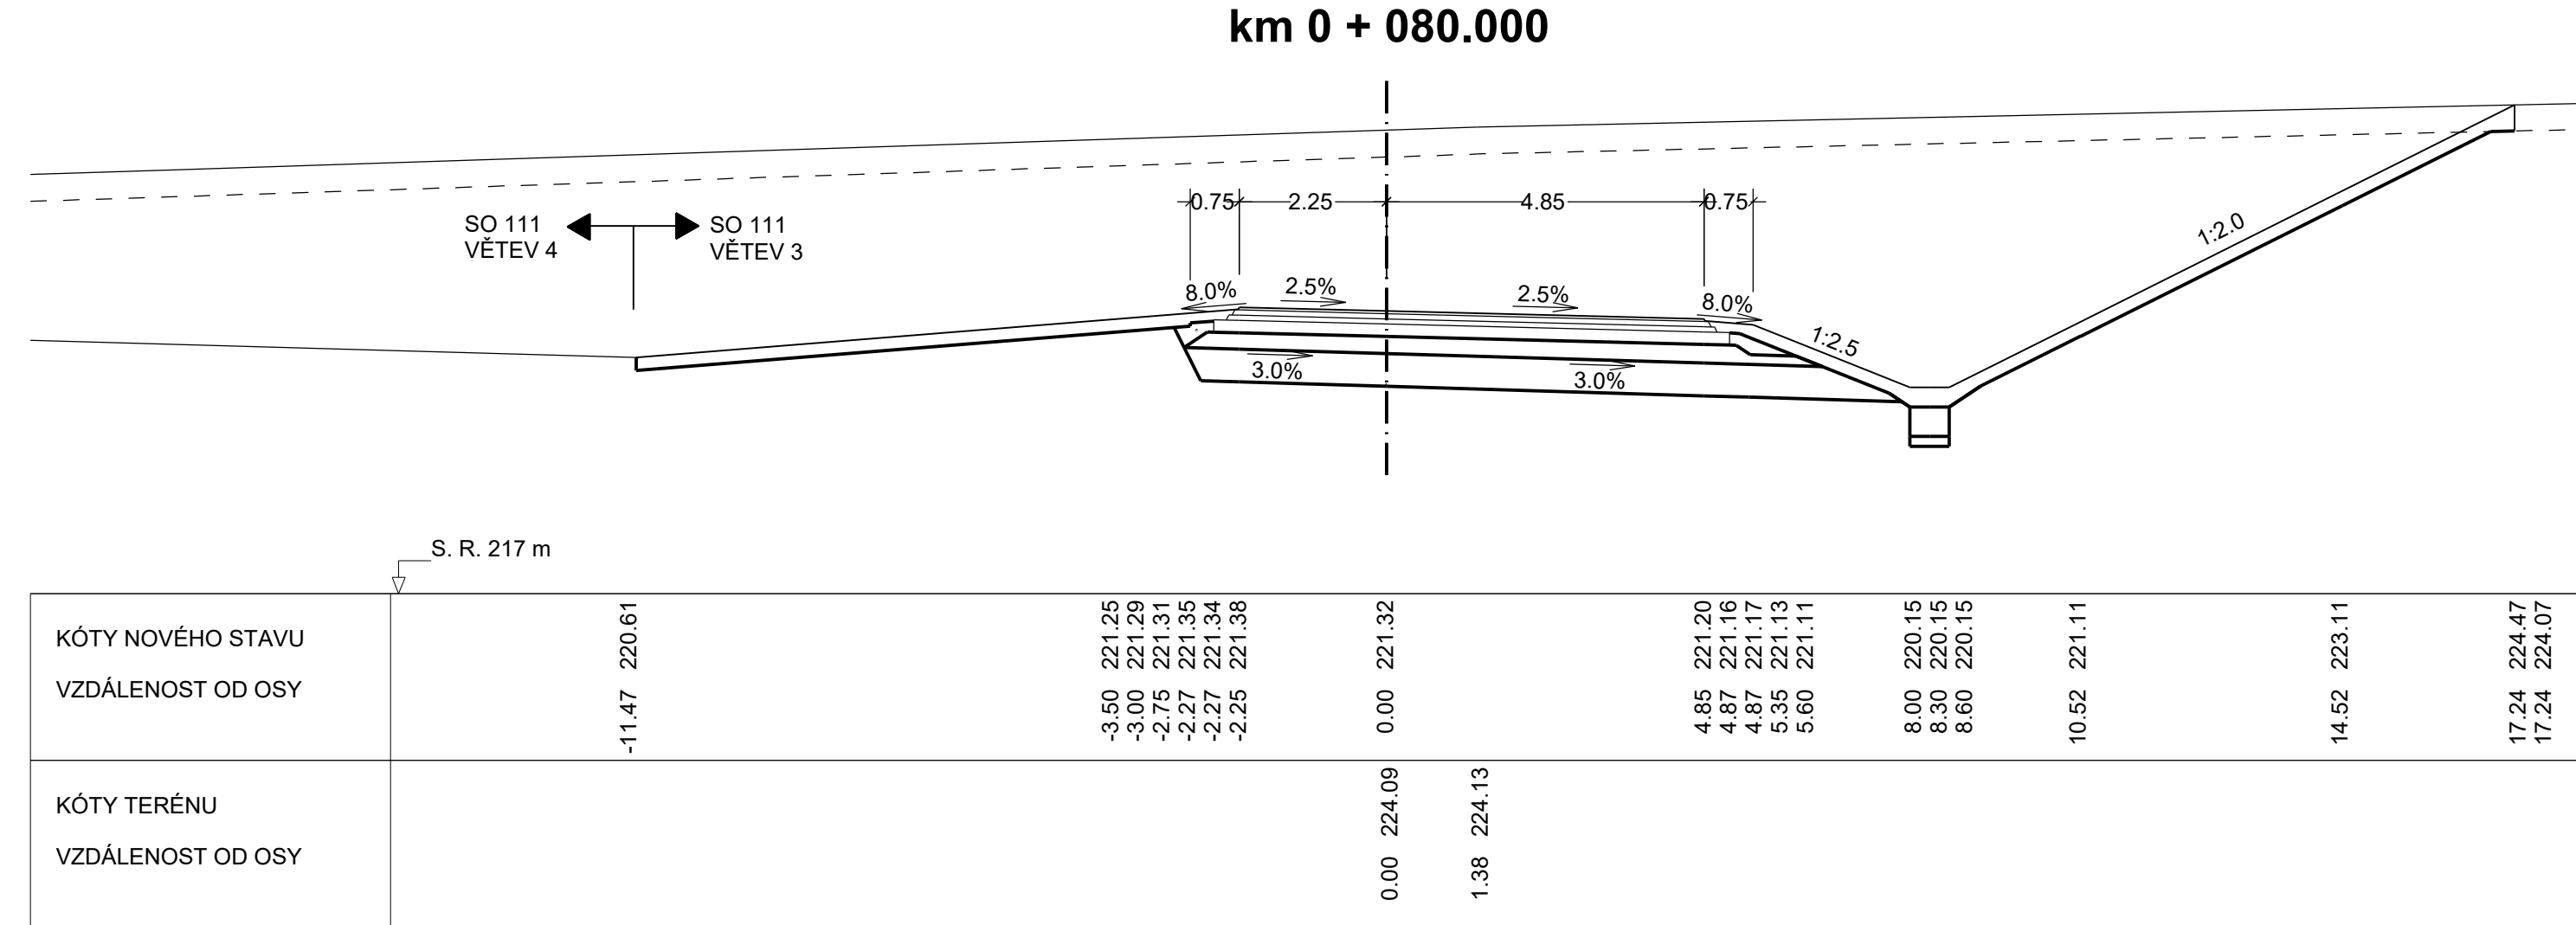
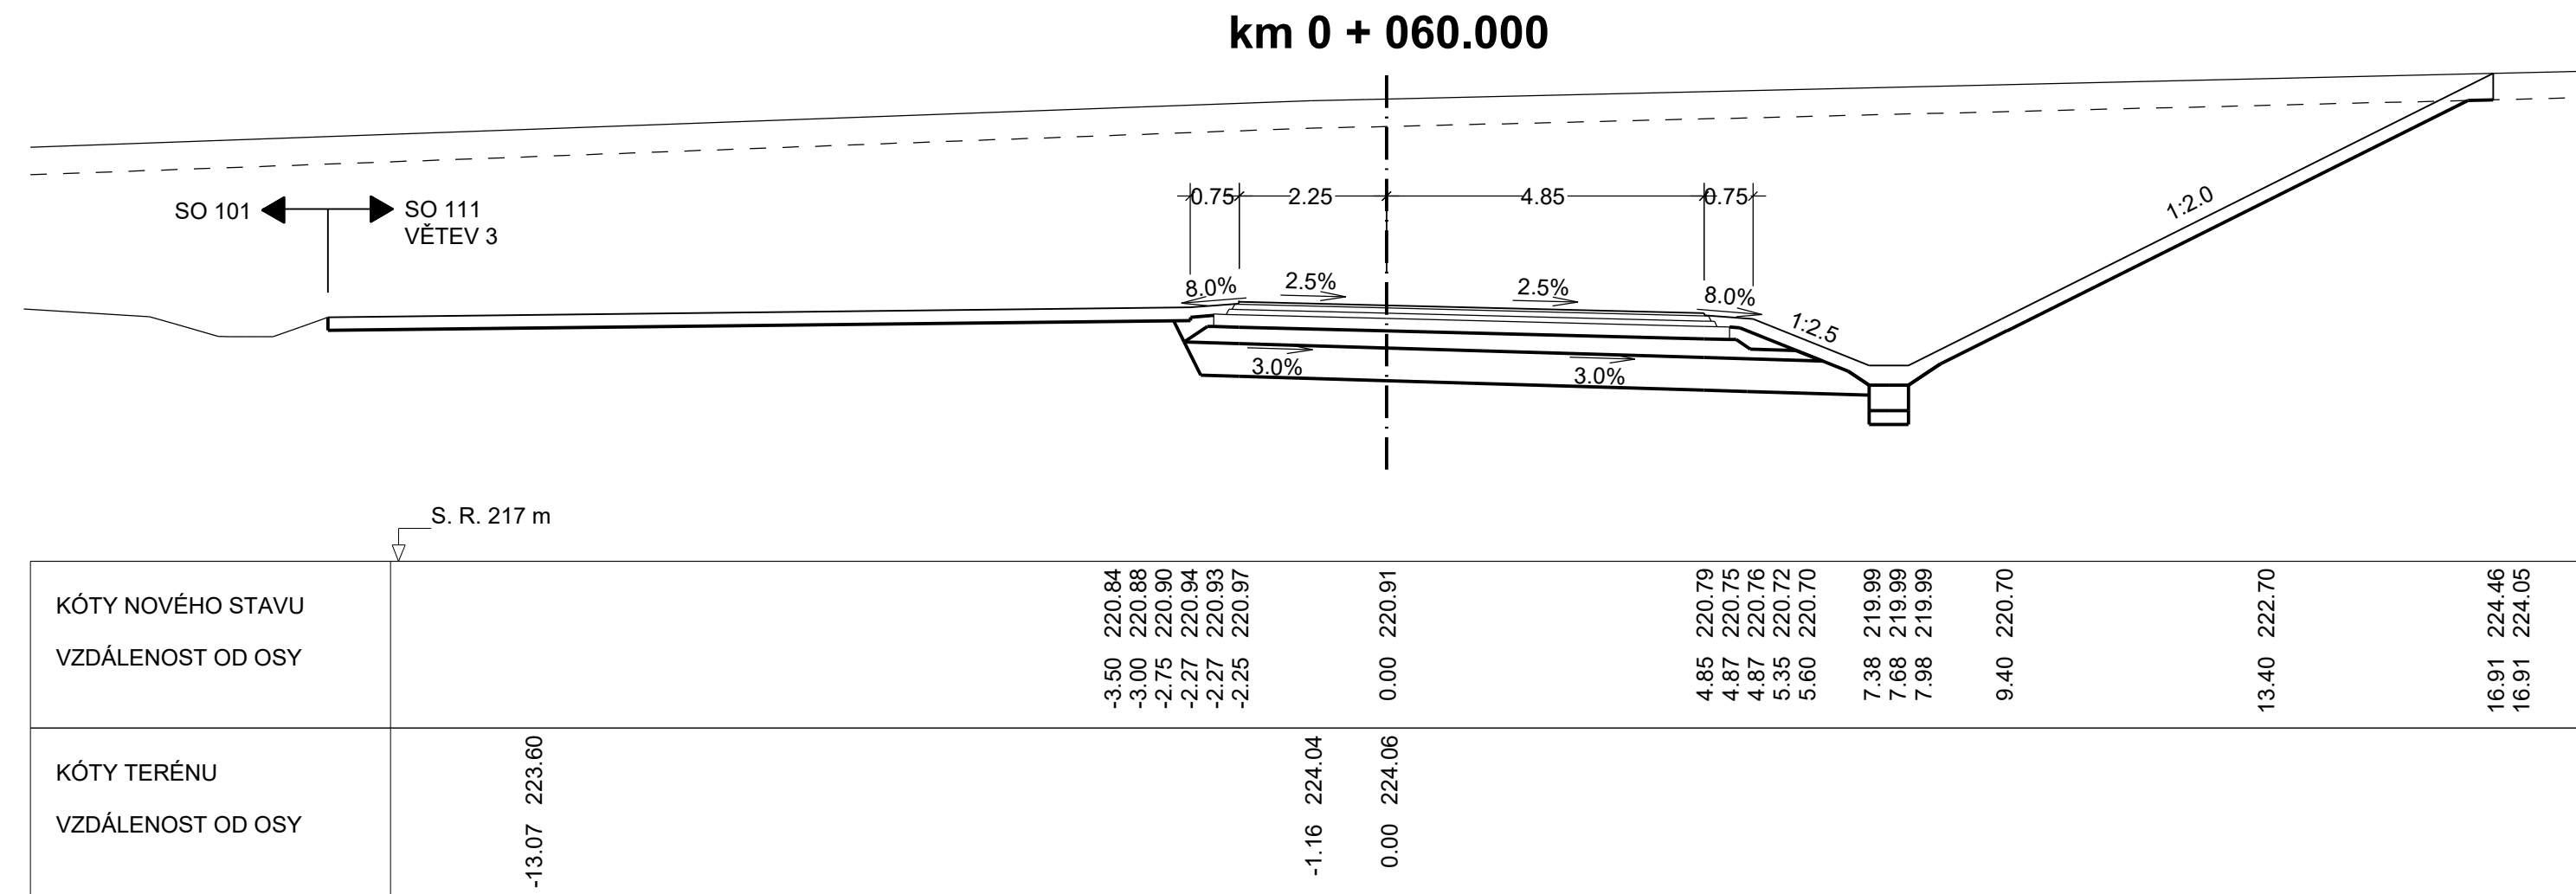


SO 111 - MÚK ŽIDNĚVES
PŘÍČNÉ ŘEZY VĚTEV 3 km 0,000 - km 0,200
M 1:100

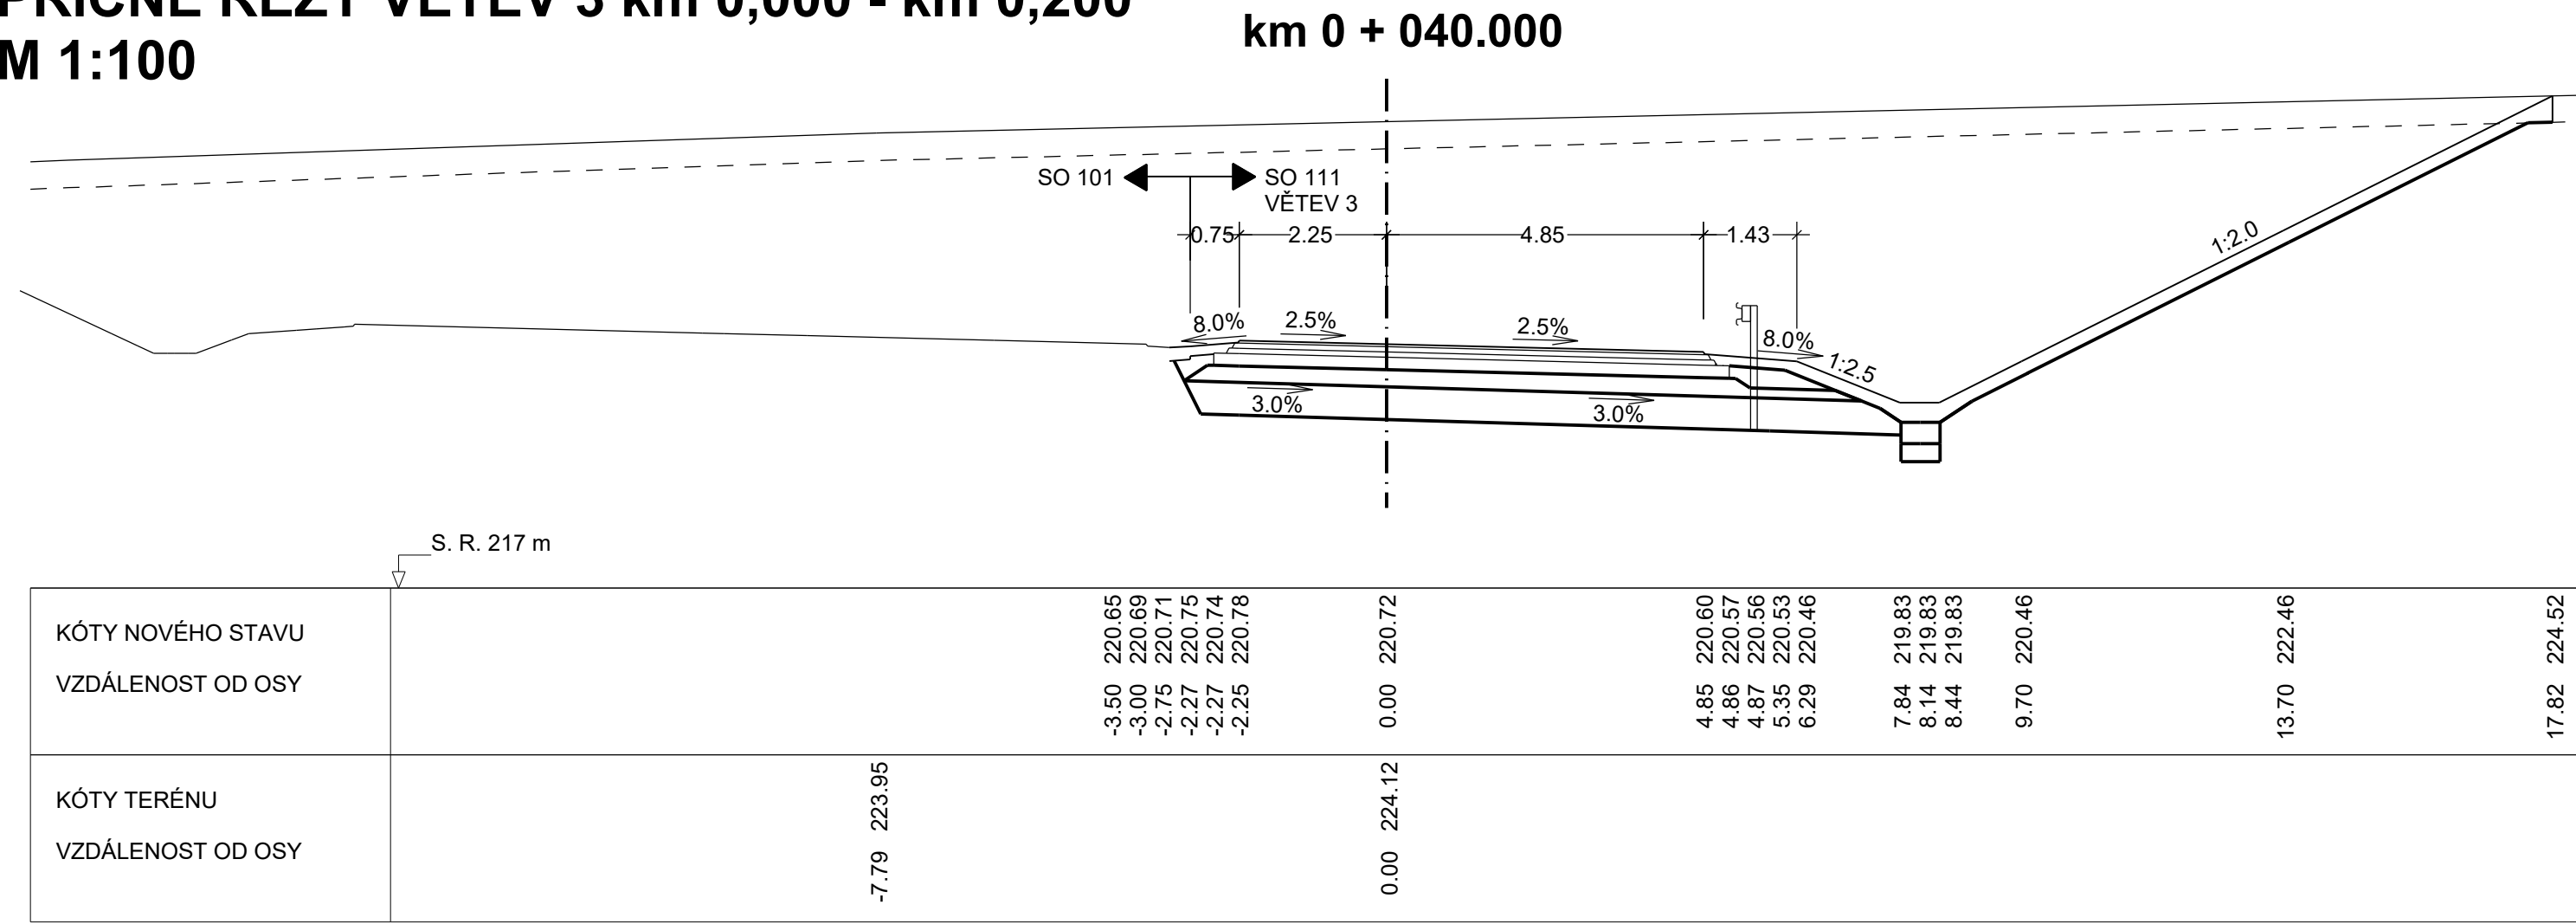

Výškový systém: BpV

SO 111 MÚK Židněves

Objednatel:
ŘEDITELSTVÍ SILNIC A DÁLNIC
Ředitelství silnic a dálnic s. p.
Čerčanská 2023/12, Krč, 140 00 Praha 4

Zhotovitel:
Valbek
Valbek, spol. s r.o.
Vaňurova 505/17
460 07 Liberec 3

Vypracoval: ING. A. DUMANSKA
Zodp. projektant: ING. T. KLIMENT
Tech. kontrola: ING. M. HANŽL
Akce: I/16 MLADÁ BOLESLAV - MARTINOVICE
Zhotovitel: Valbek, spol. s r.o.
Vaňurova 505/17
460 07 Liberec 3

Zak. číslo: 21-L113-001
Datum: 02/2025
Stupeň: PDPS
Počet formátů: 14 x A4
Měřítko: 1:100
Č. přílohy: Paré

5.3.1