
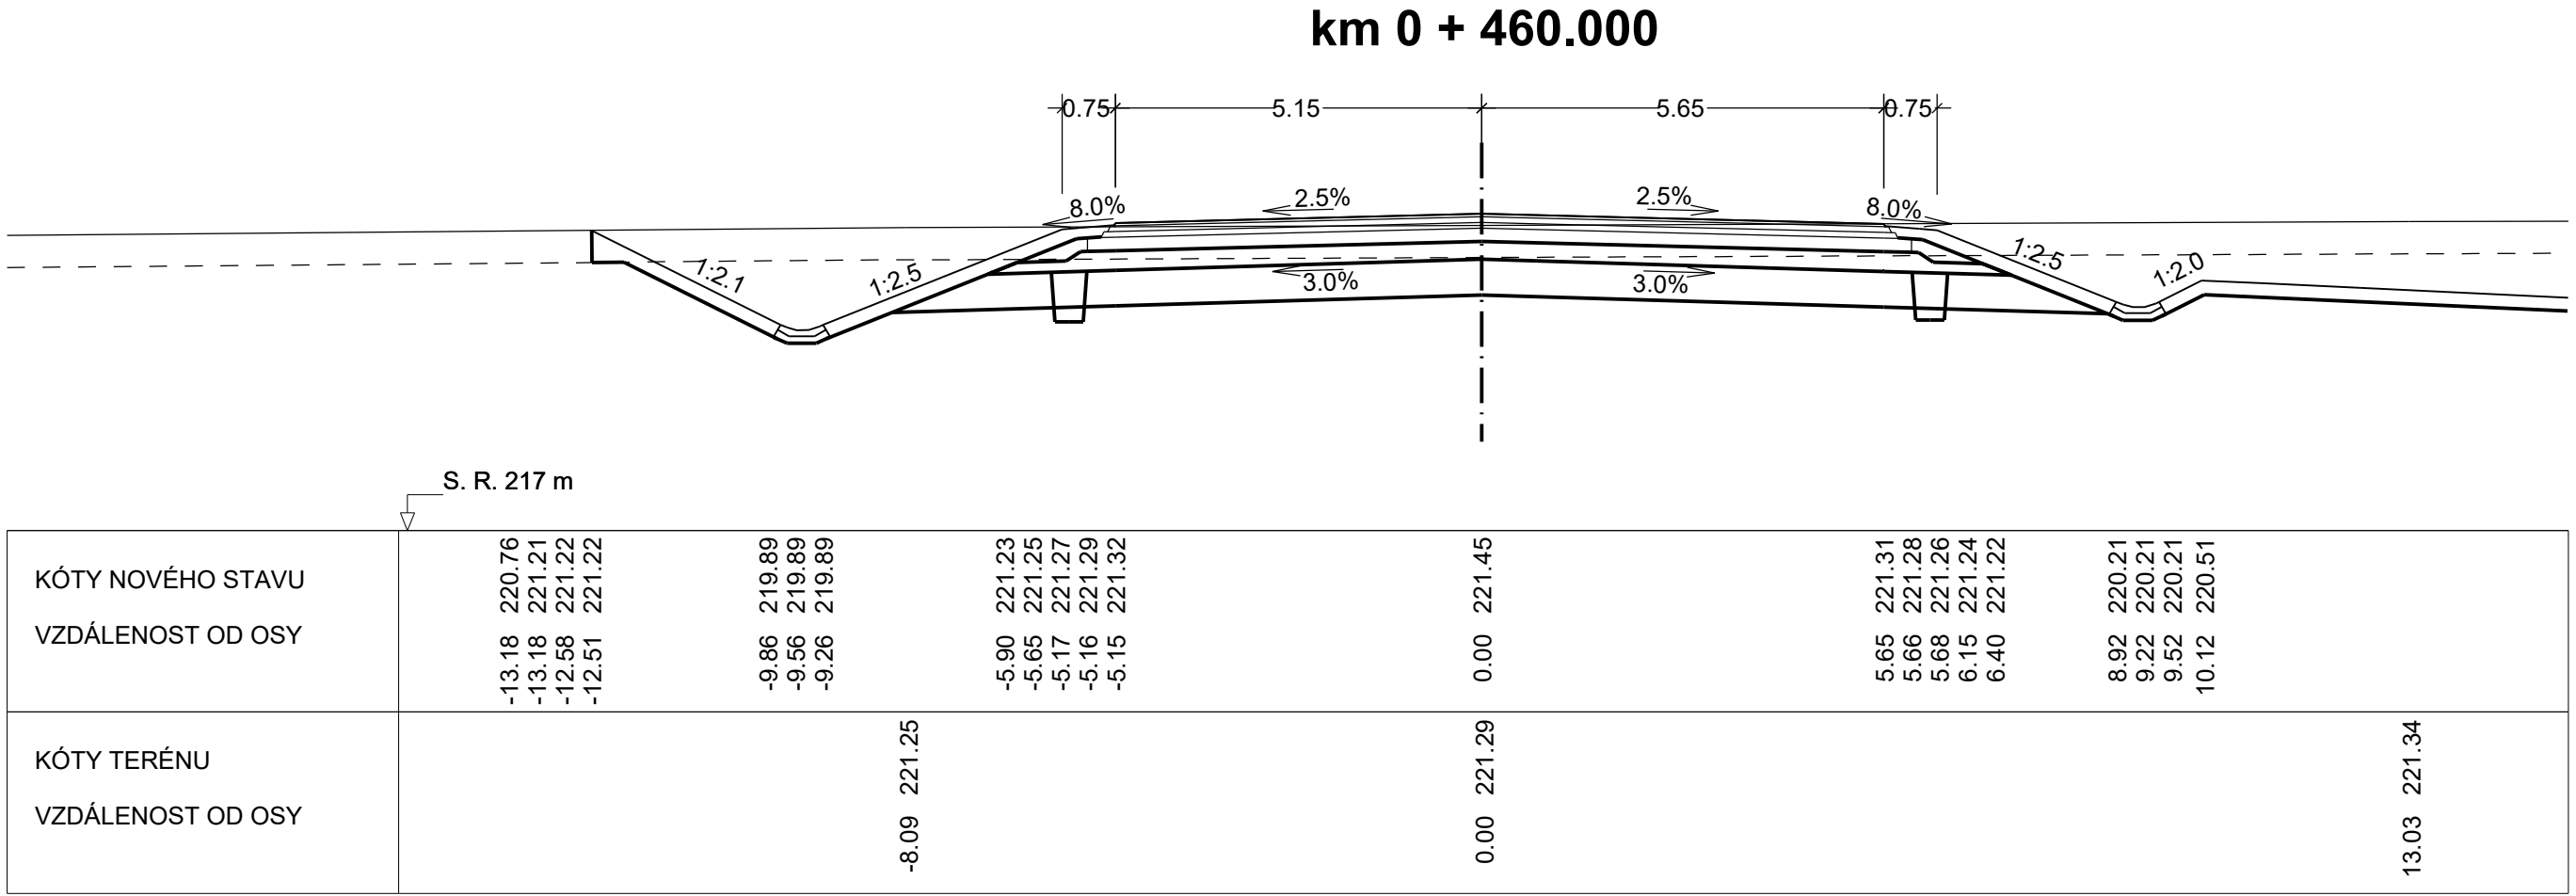
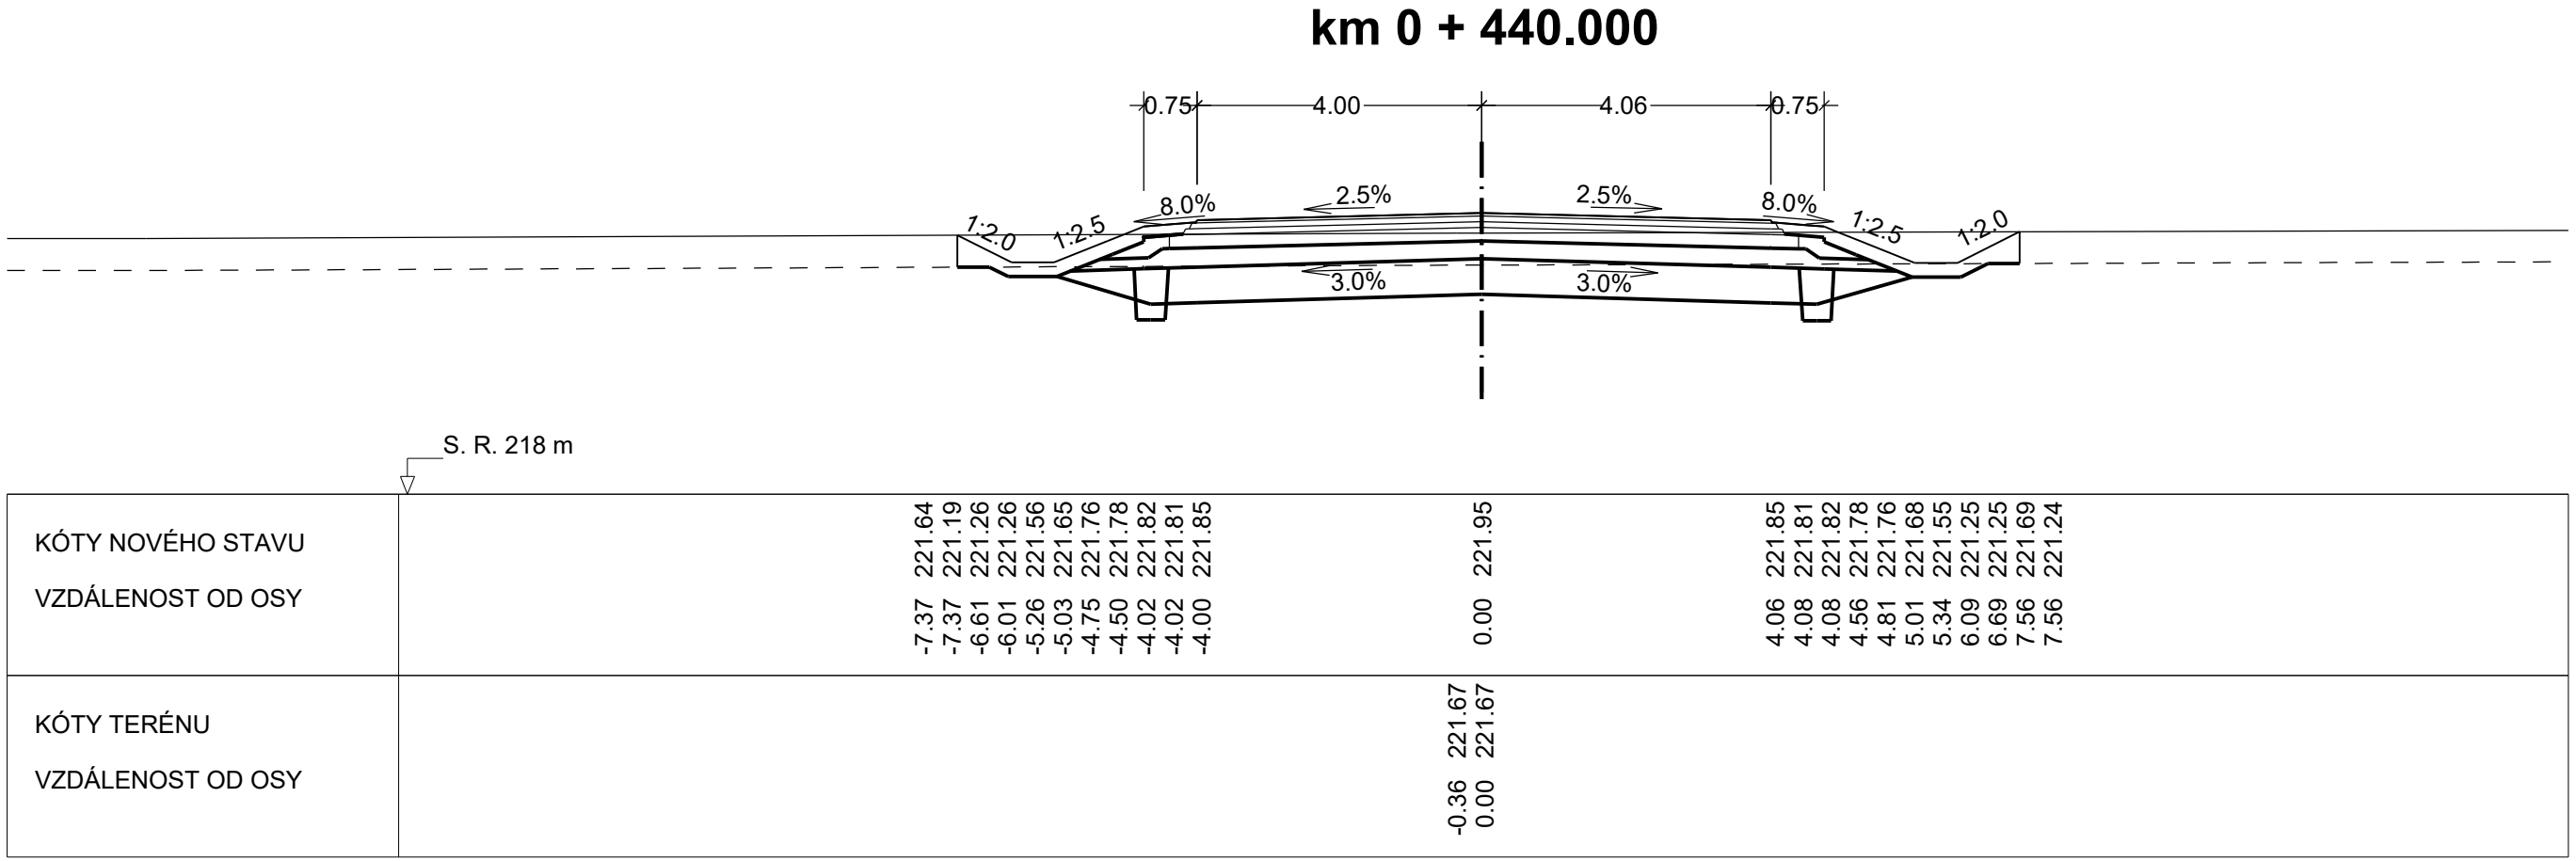
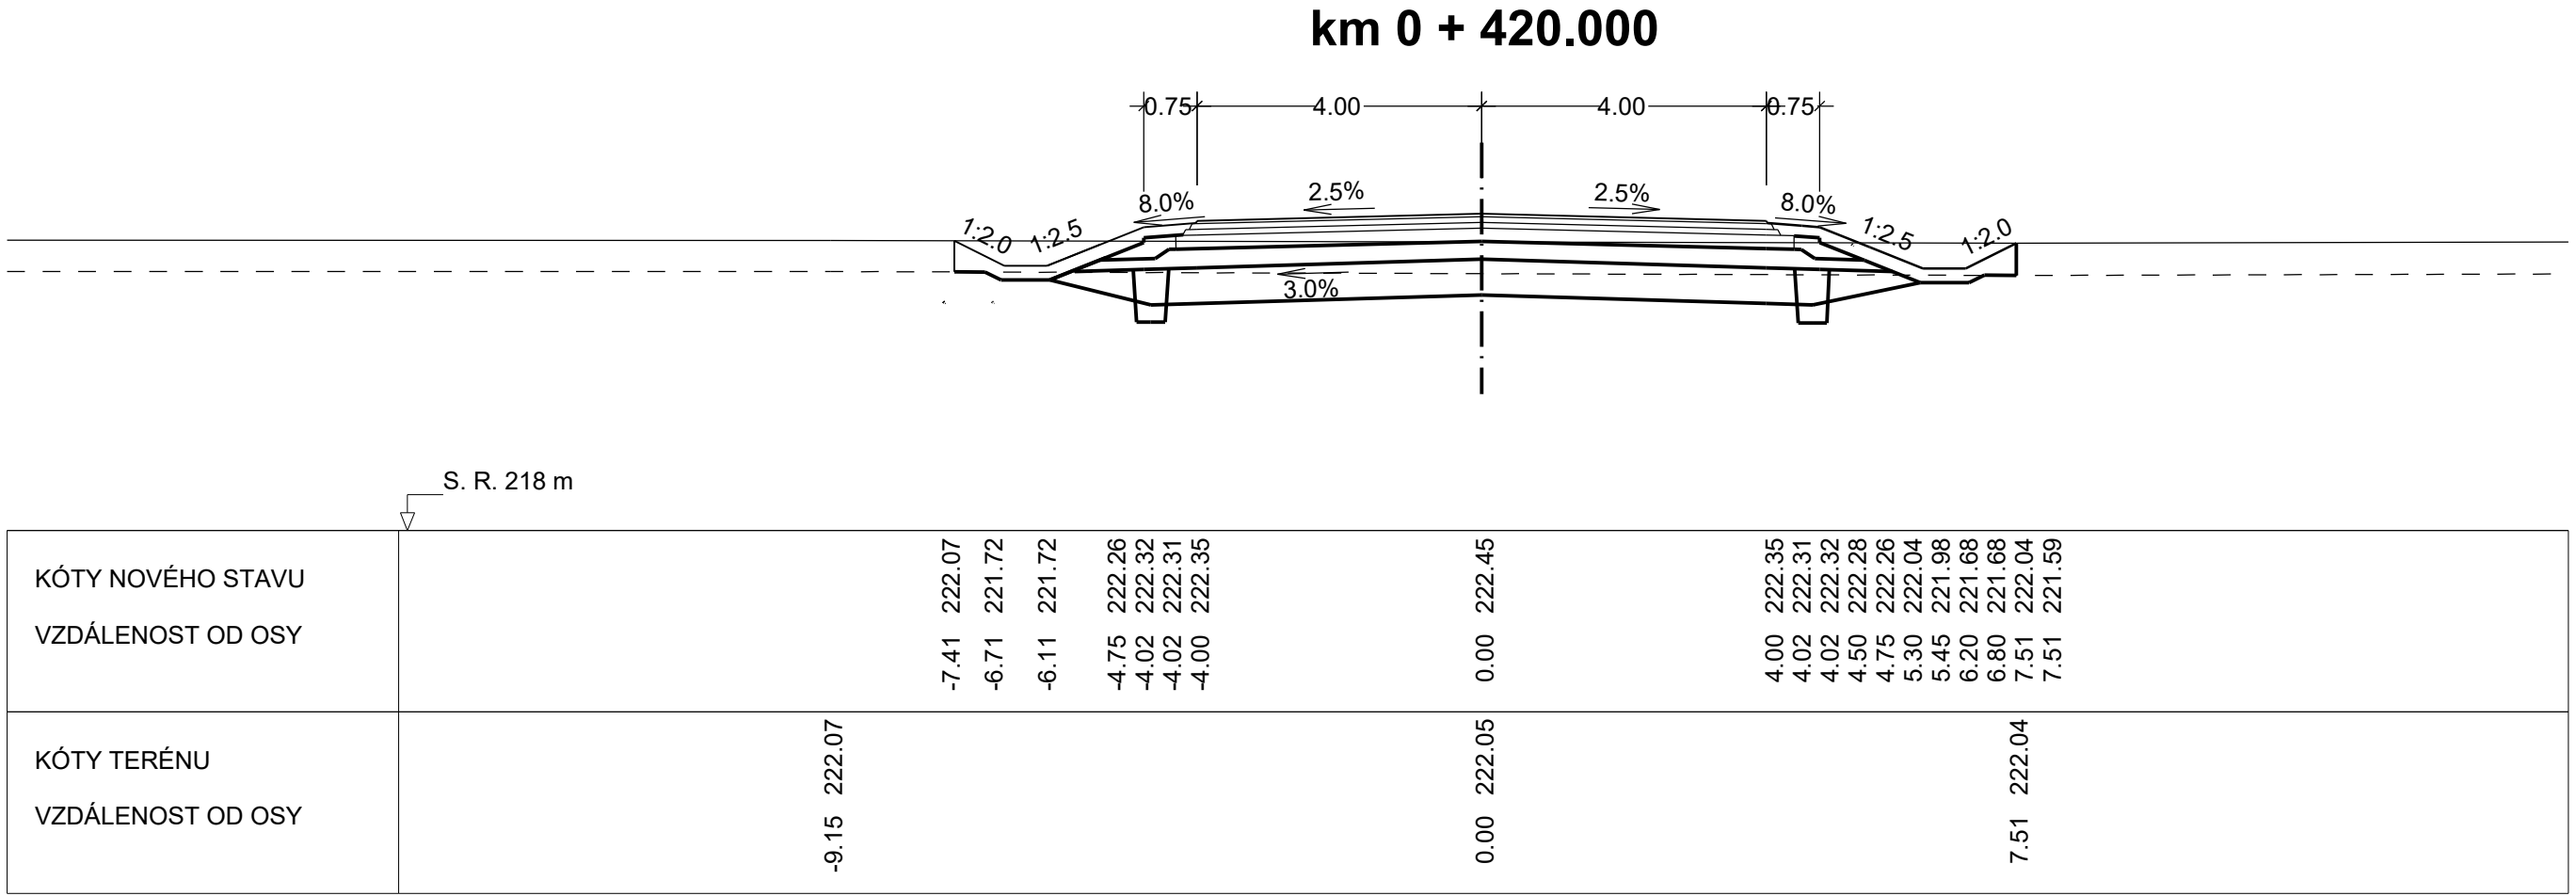
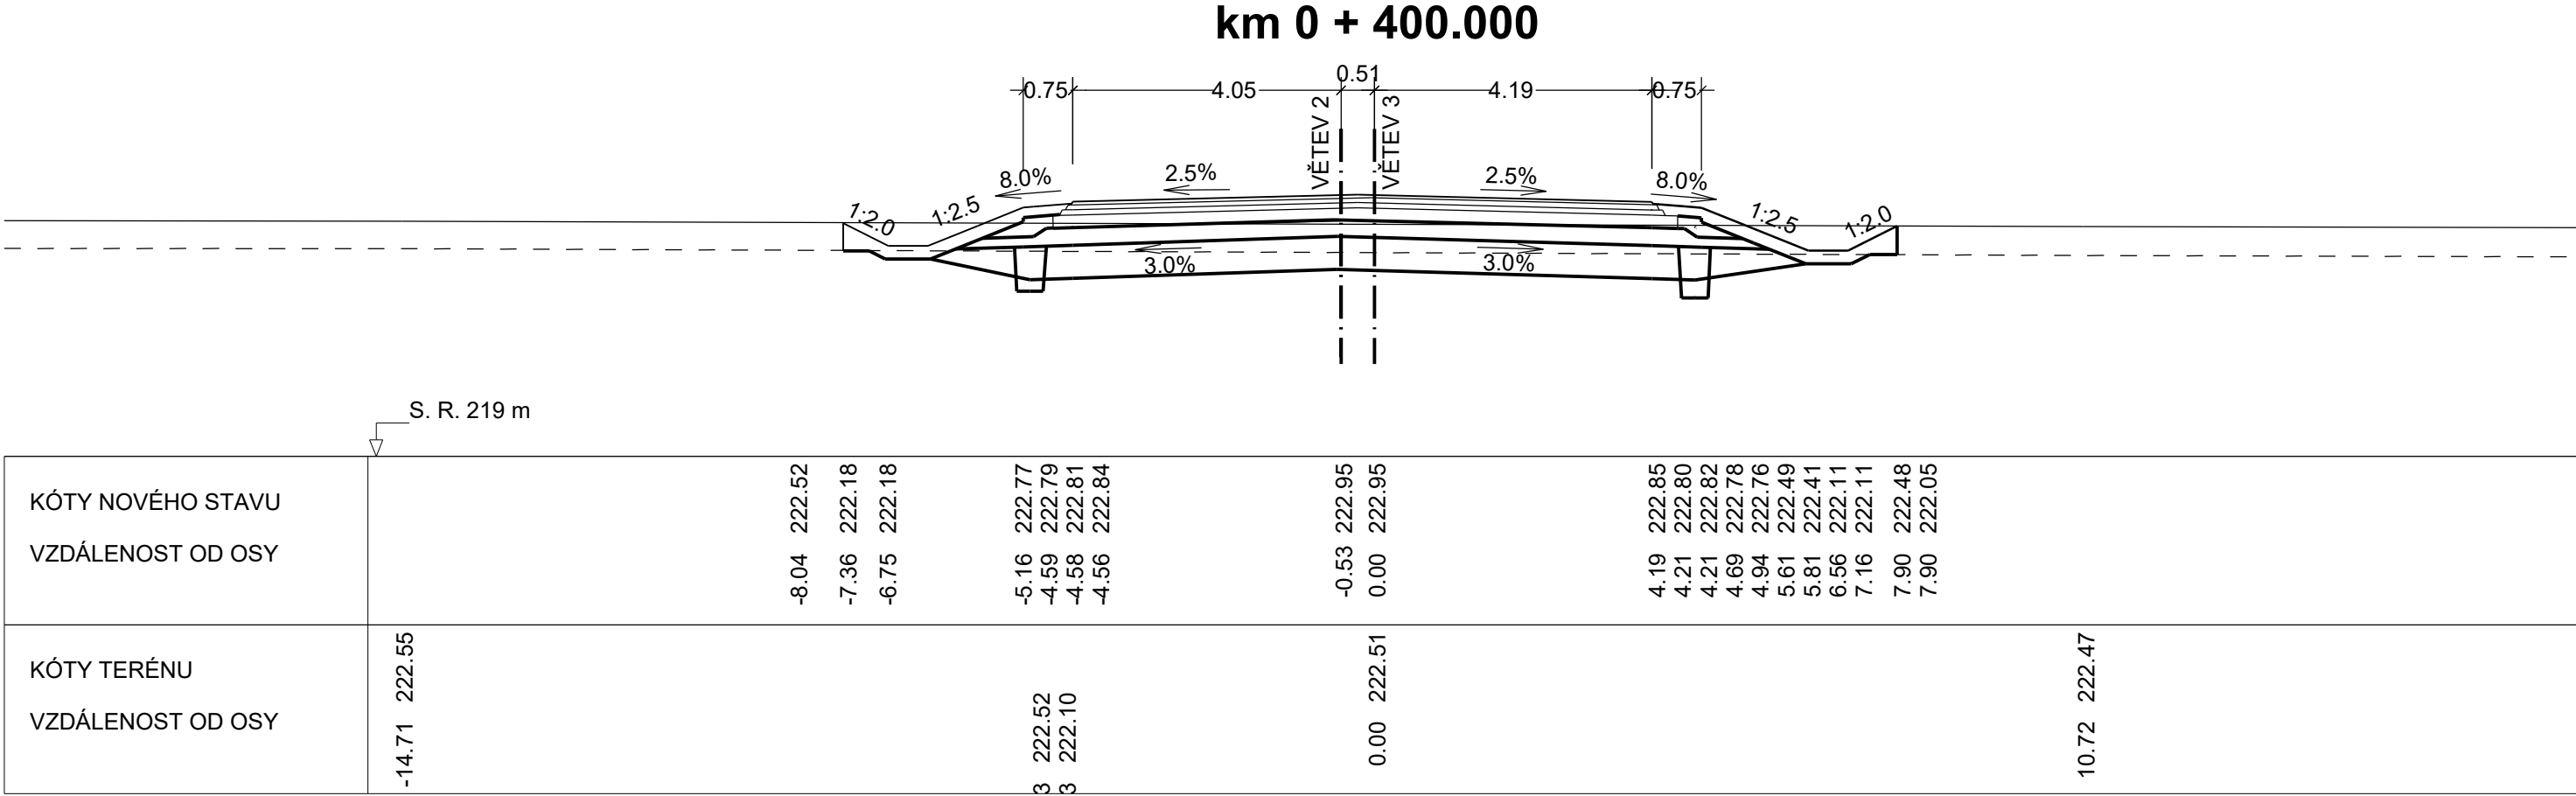
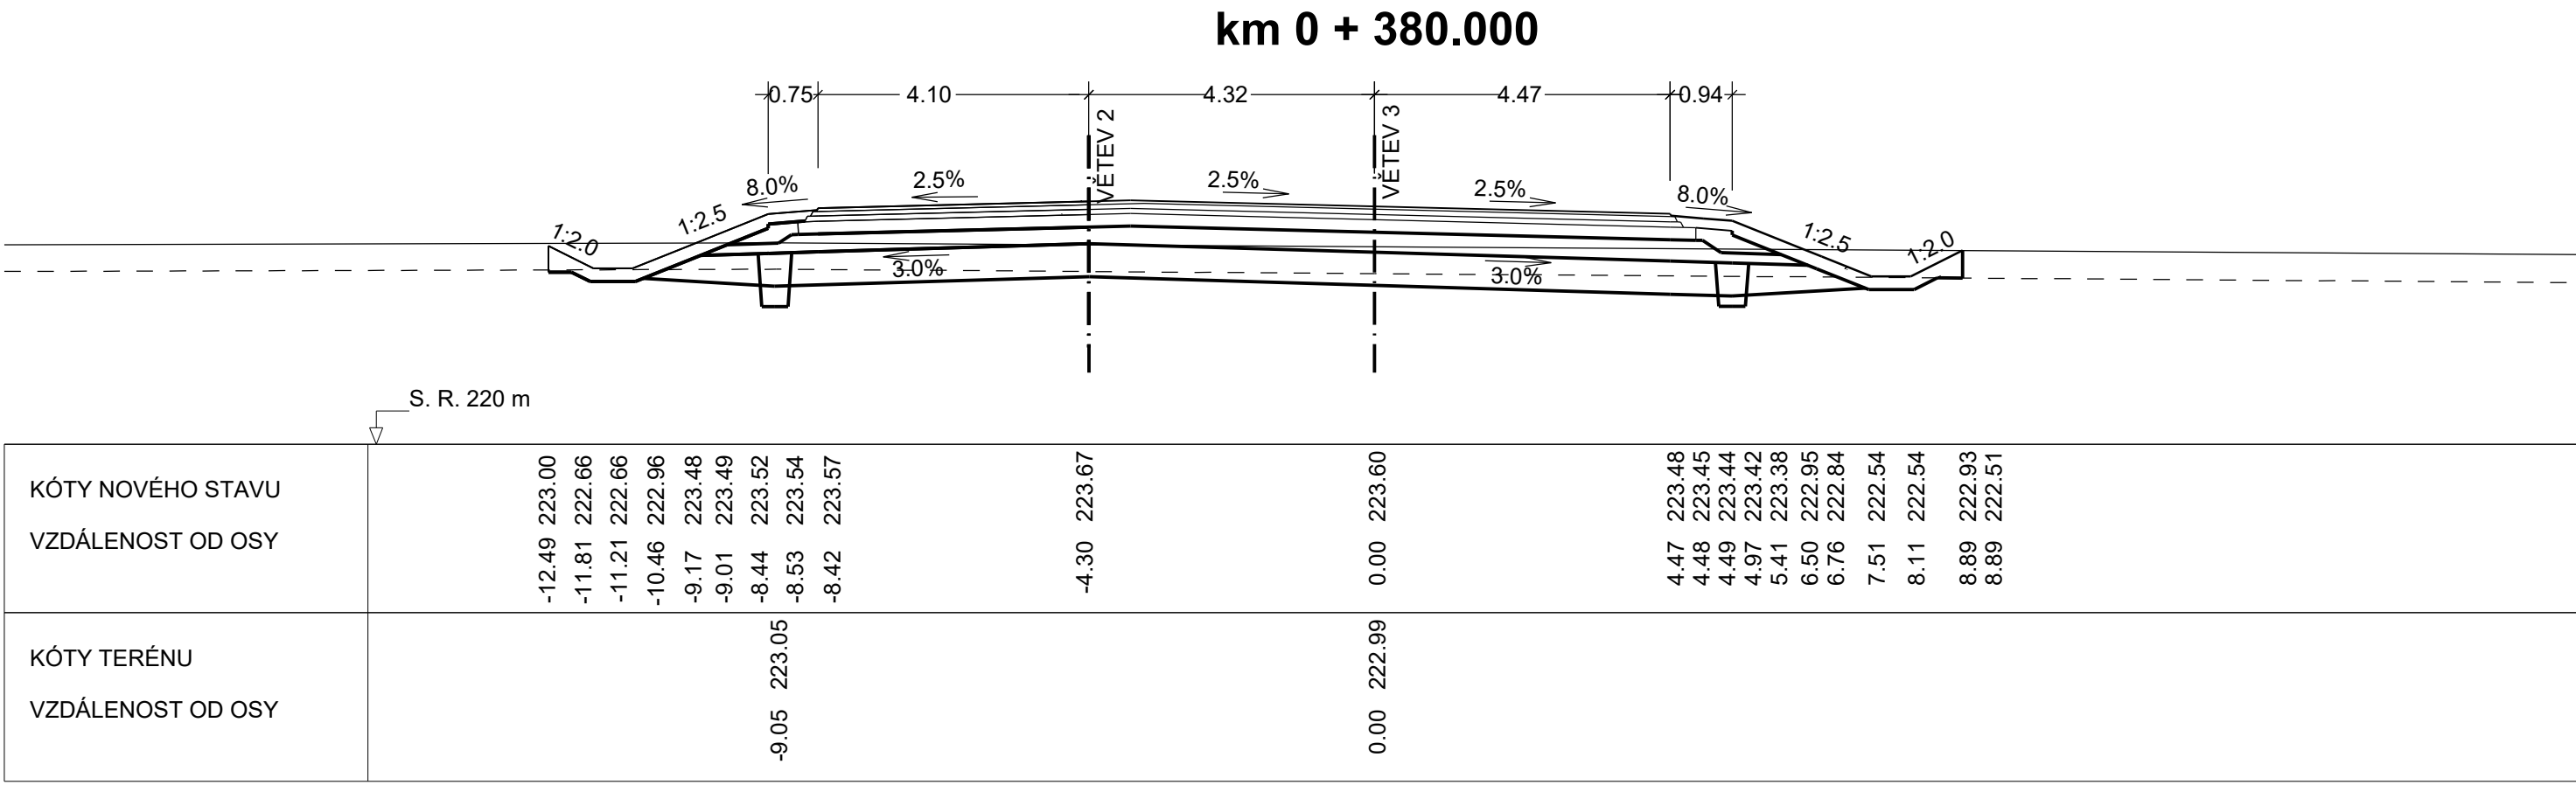
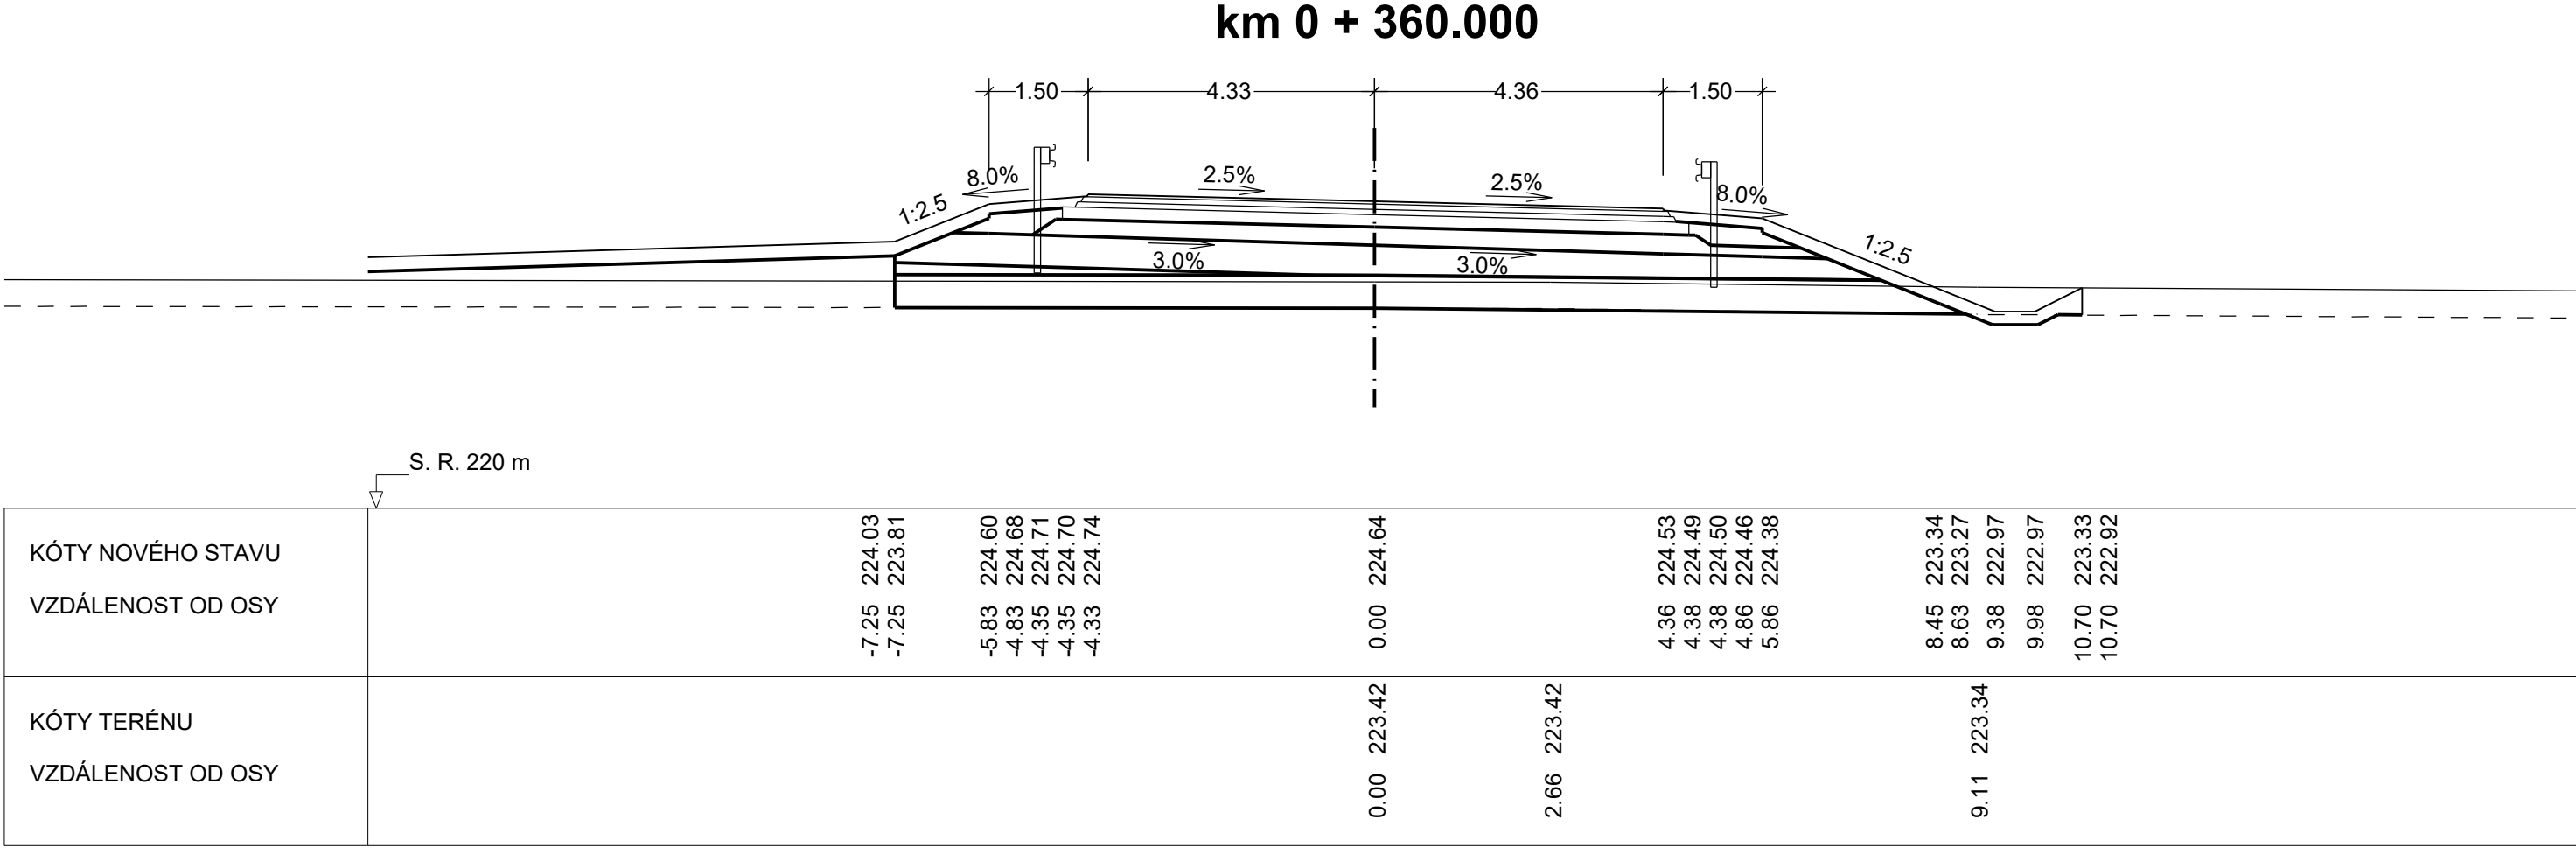
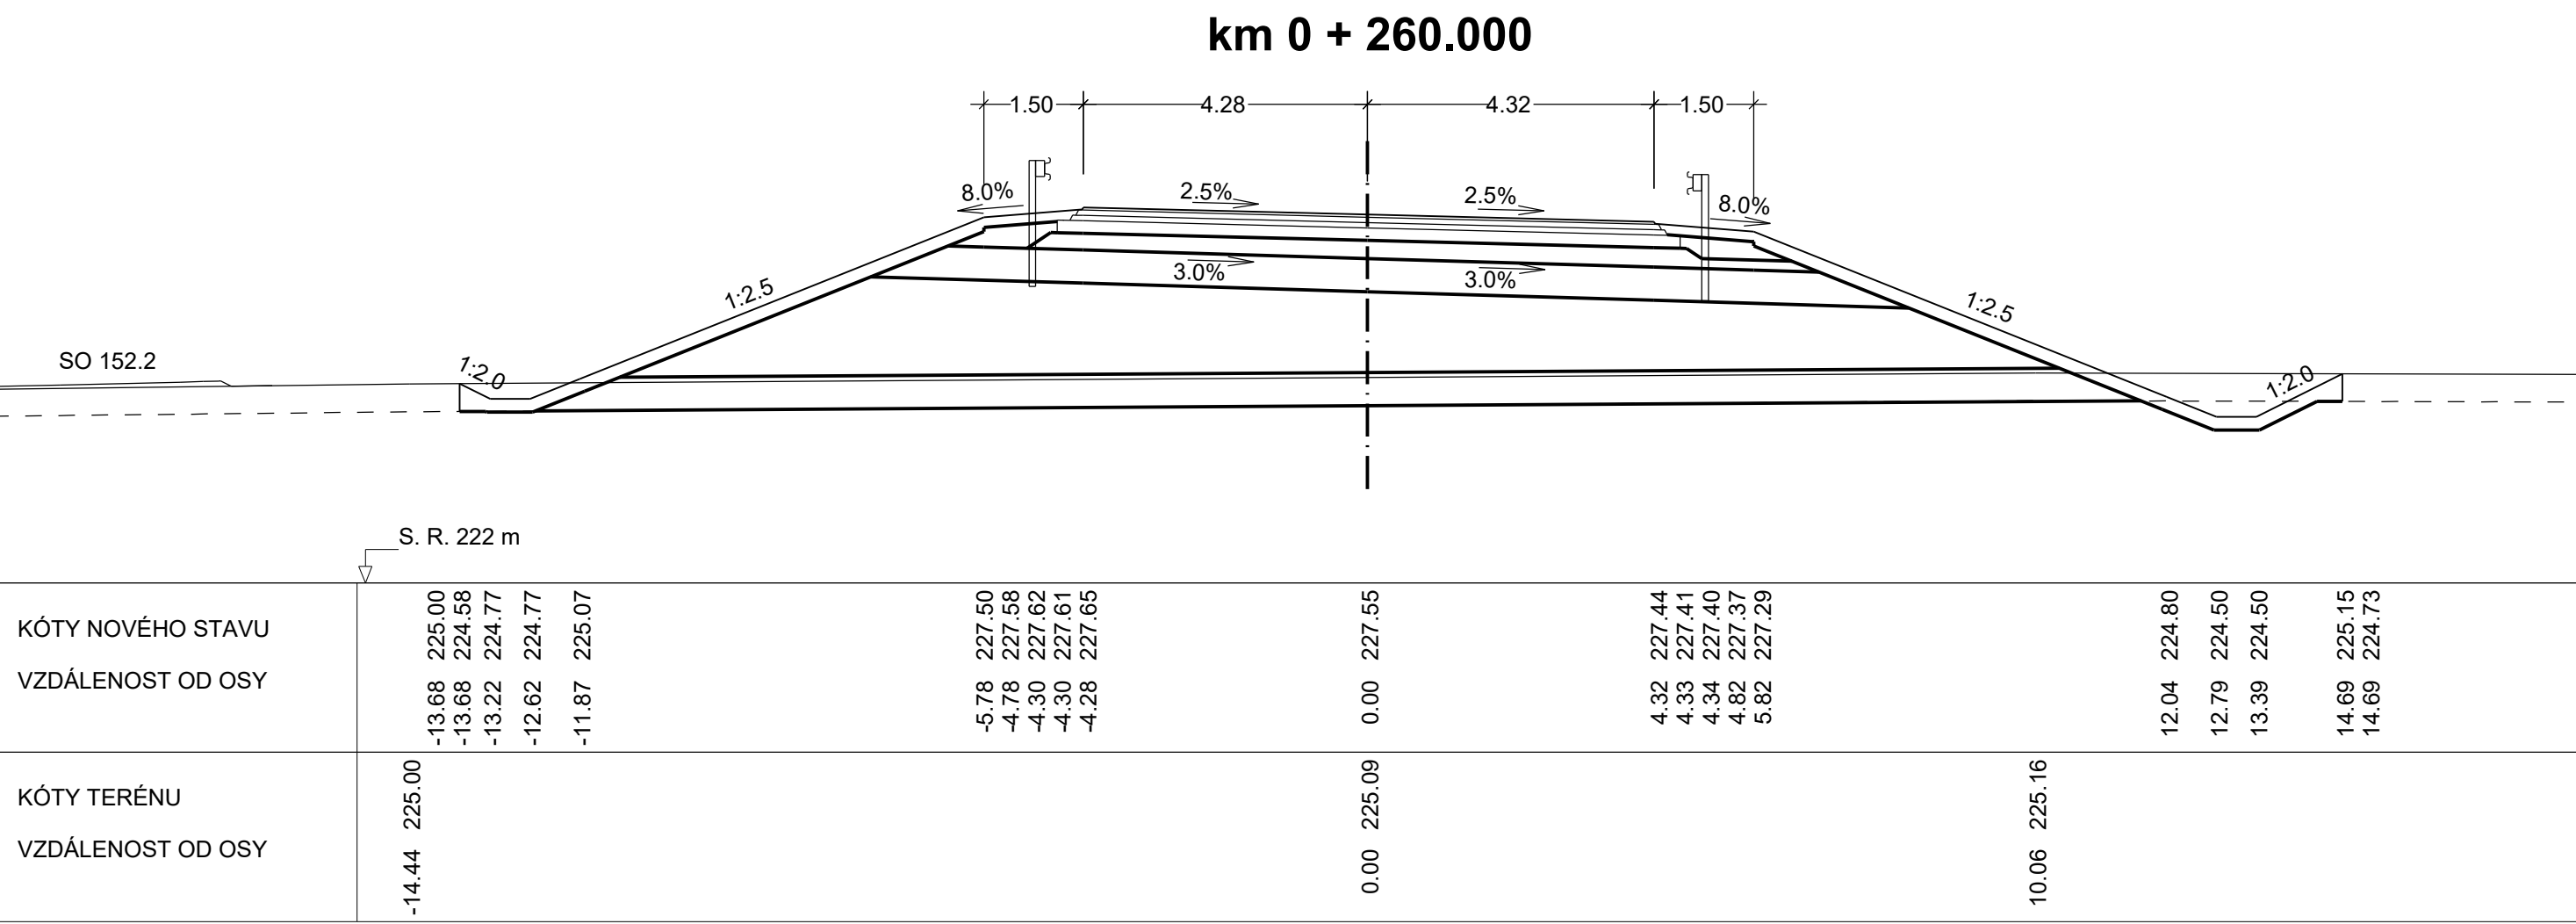
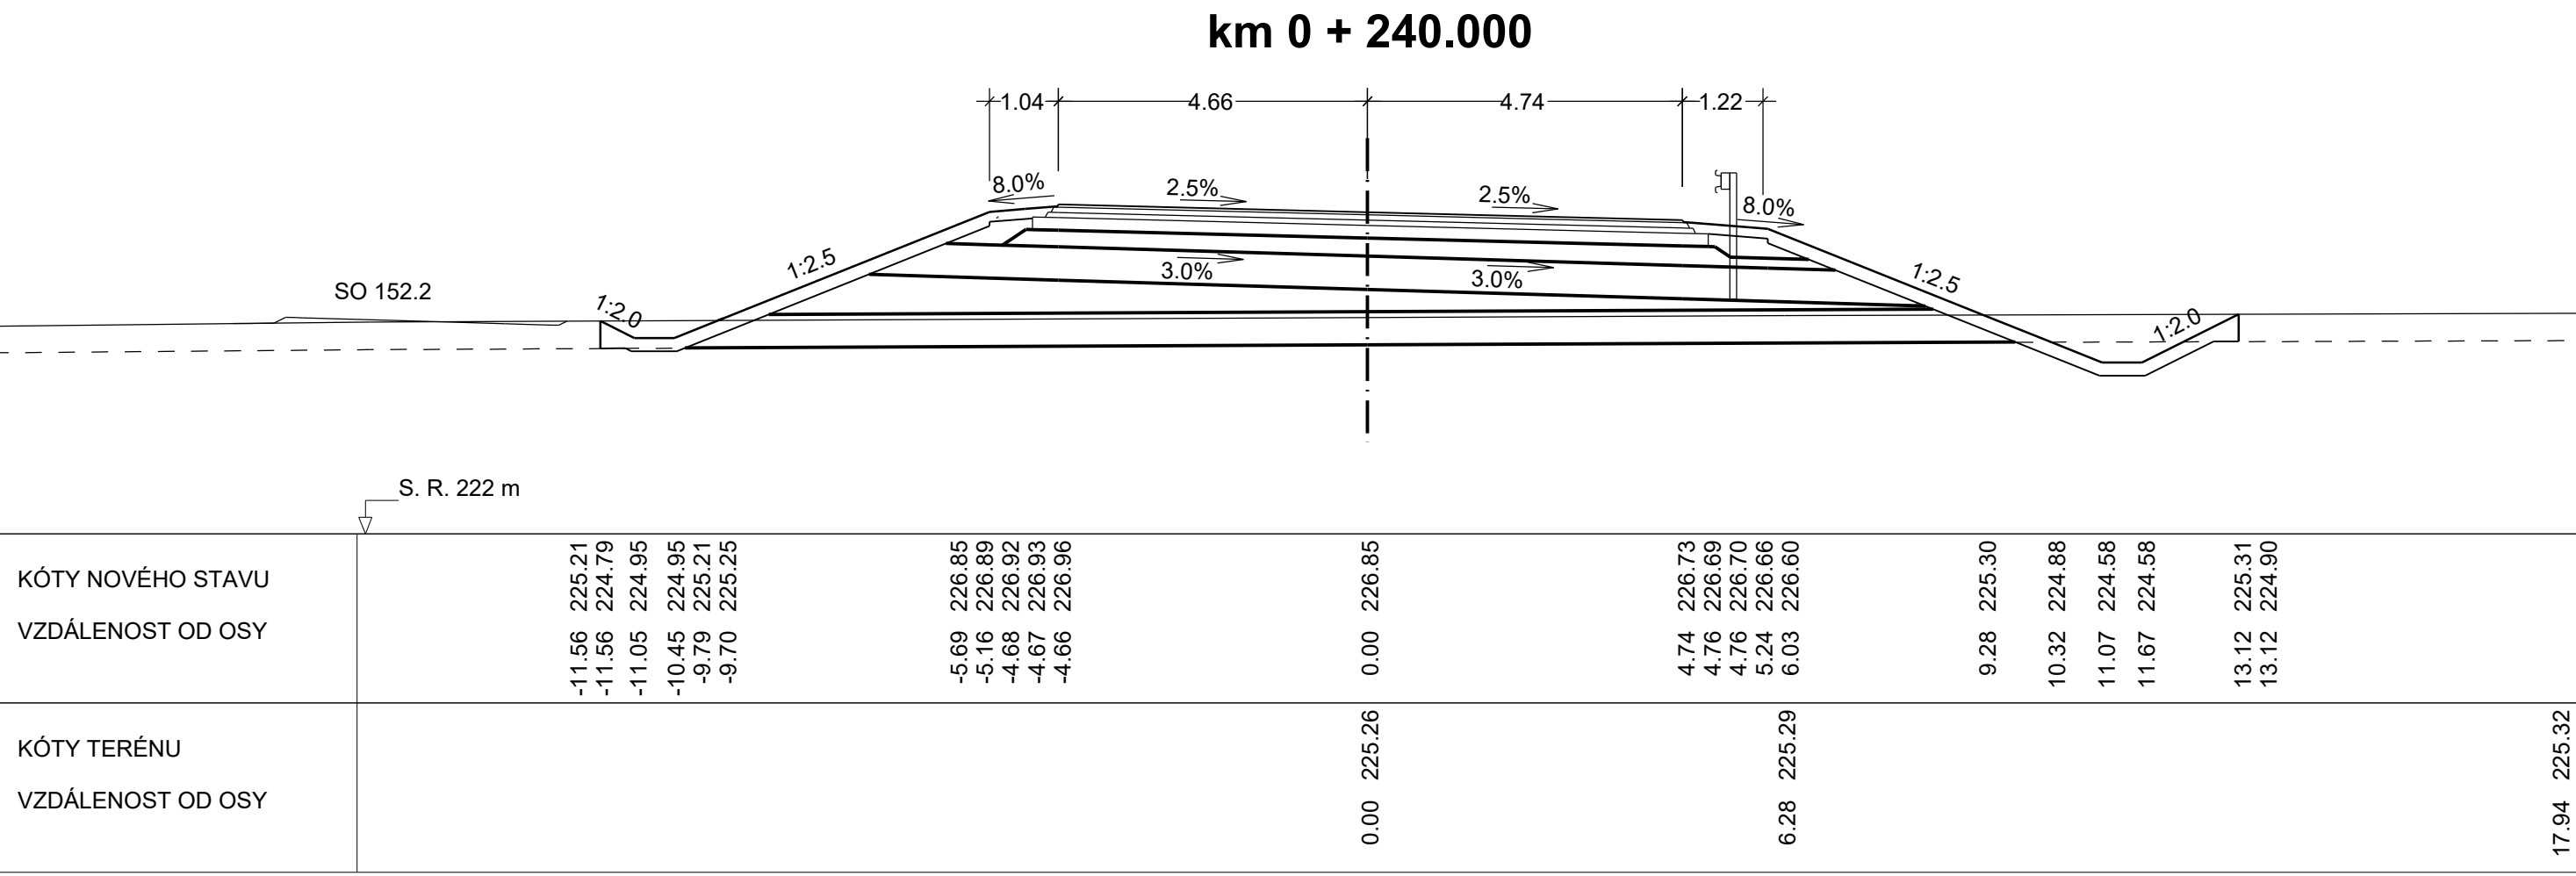


SO 111 - MÚK ŽIDNĚVES
PŘÍČNÉ ŘEZY VĚTEV 3 km 0,220 - km 0,460
M 1:100

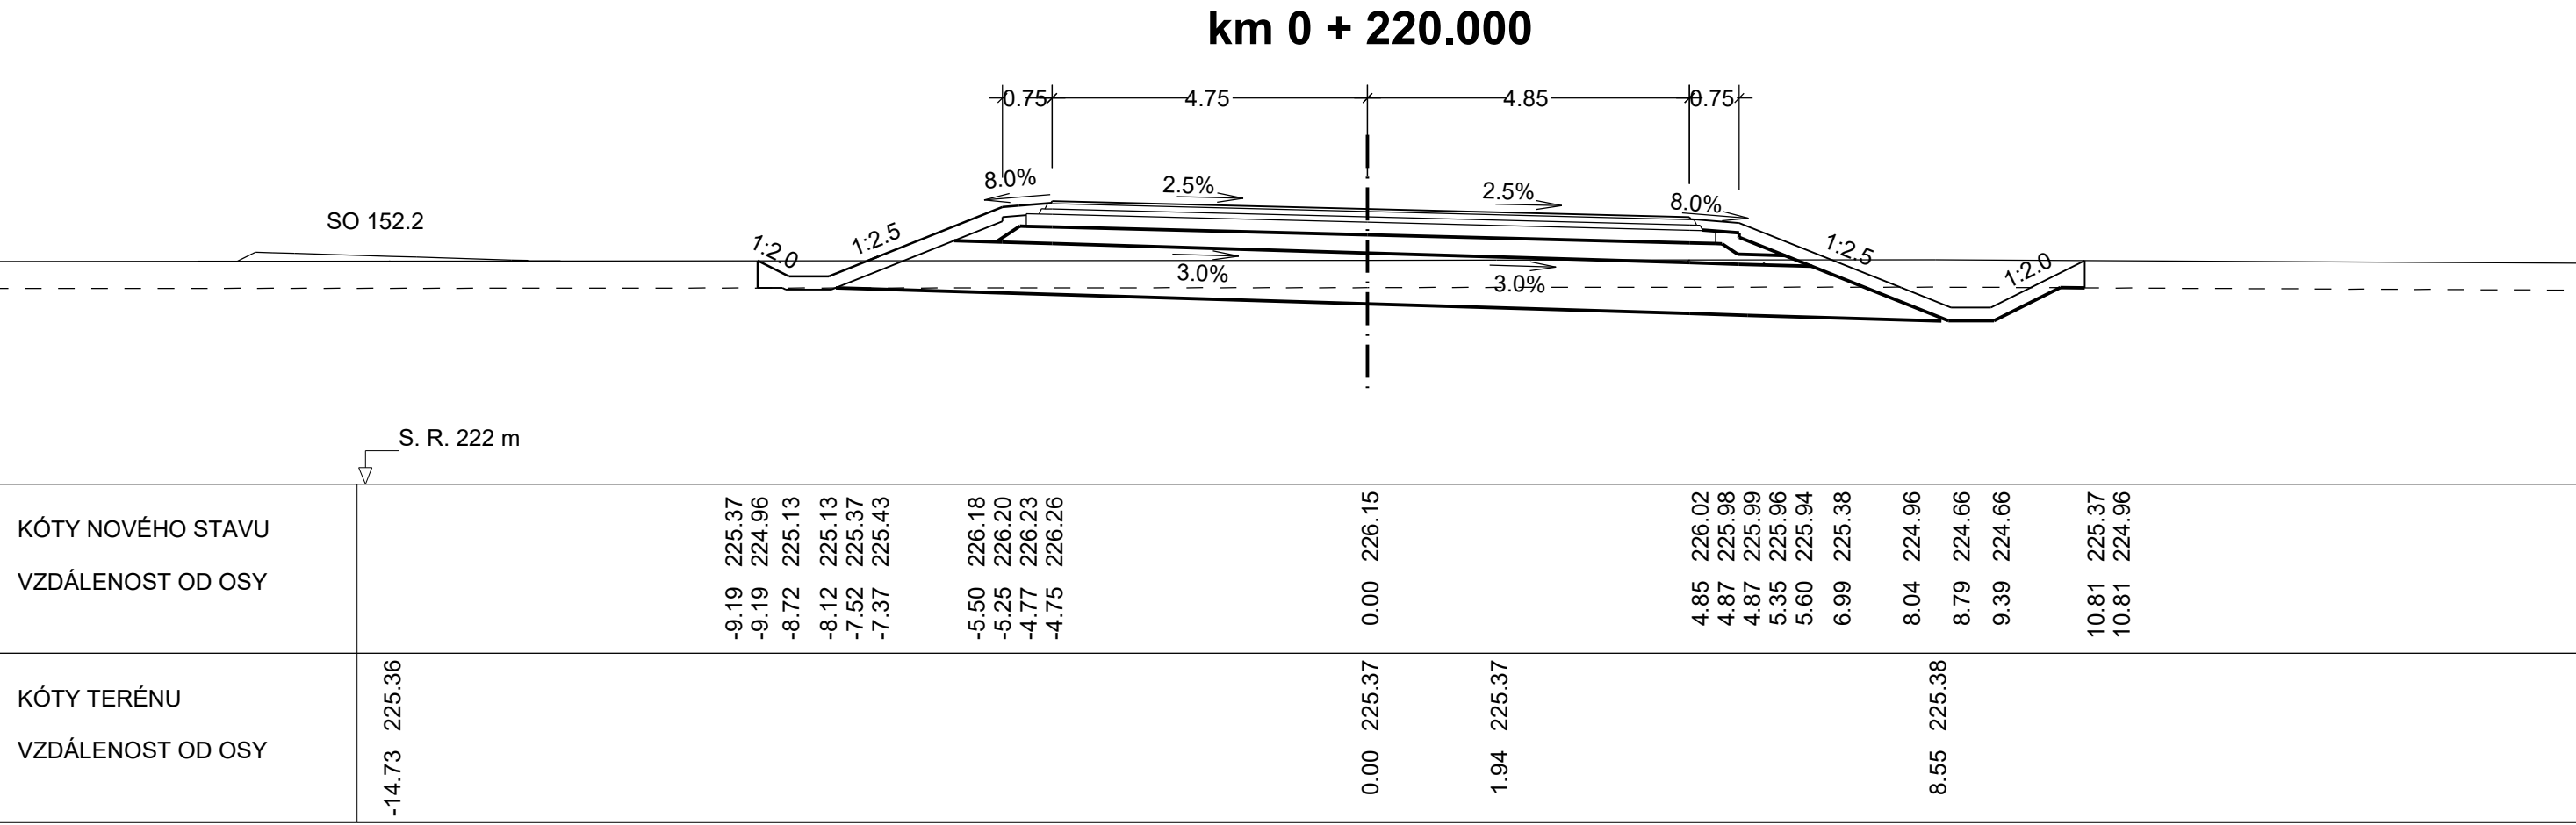

Výškový systém BpV

SO 111 MÚK Židněves

Objednatel:

**ŘEDITELSTVÍ
SILNIC
A DÁLNIC**

Ředitelství silnic a dálnic s. p.
Čerčanská 2033/12, Krč, 140 00 Praha 4

Zhotovitel:

**Valbek**

Valbek, spol. s r.o.
Vaňurova 505/17
460 07 Liberec 3

HIP:
ING. T. KLIMENT

**Valbek**

I/16 MLADÁ BOLESLAV - MARTINOVICE

Zhotovitel:
Valbek, spol. s r.o.
Vaňurova 505/17
460 07 Liberec 3

Příloha
PŘÍČNÉ ŘEZY VĚTEV 3
km 0,220 - km 0,460

5.3.2

Zak. číslo
21-L113-001
Datum
02/2025
Stupeň
PDPS
Počet formátů
14 x A4
Měřítko
1:100
Č. přílohy
Pare