




SO 111 - MÚK ŽIDNĚVES
PŘÍČNÉ ŘEZY VĚTEV 4
M 1:100

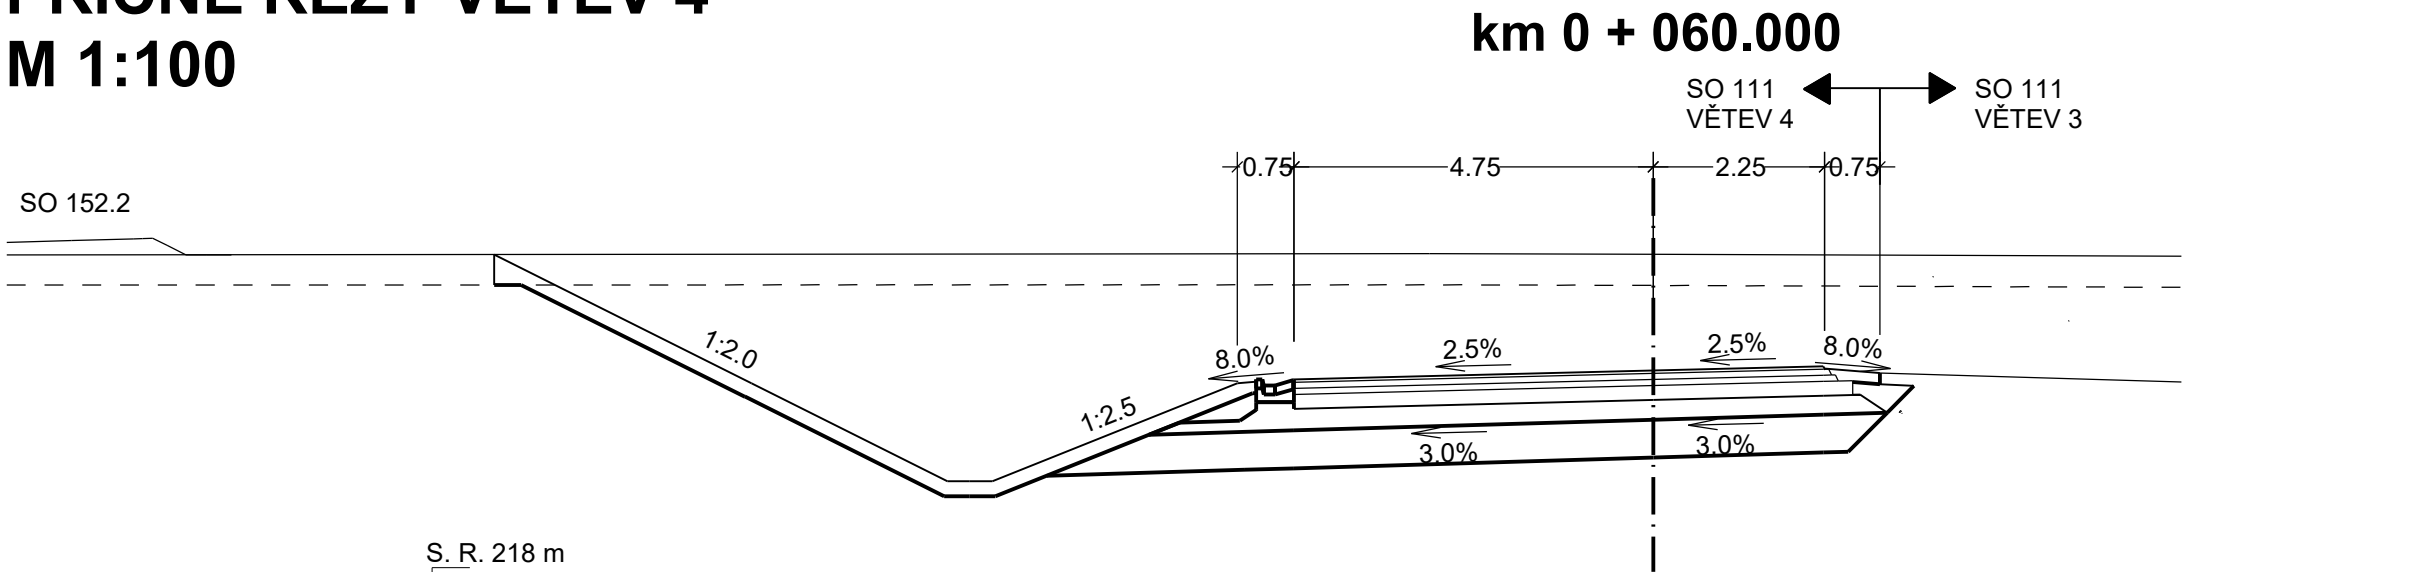

KÓTY NOVÉHO STAVU	222.64	222.24		220.94	219.64	219.64	220.94	220.94	221.11	221.16	221.13	221.08	221.04
VZDÁLENOST OD OSY	-15.33	-15.33		-11.93	-9.34	-9.04	-8.74	-5.50	0.00	2.25	2.27	3.00	3.50
KÓTY TERÉNU													
VZDÁLENOST OD OSY								-2.96	0.00				

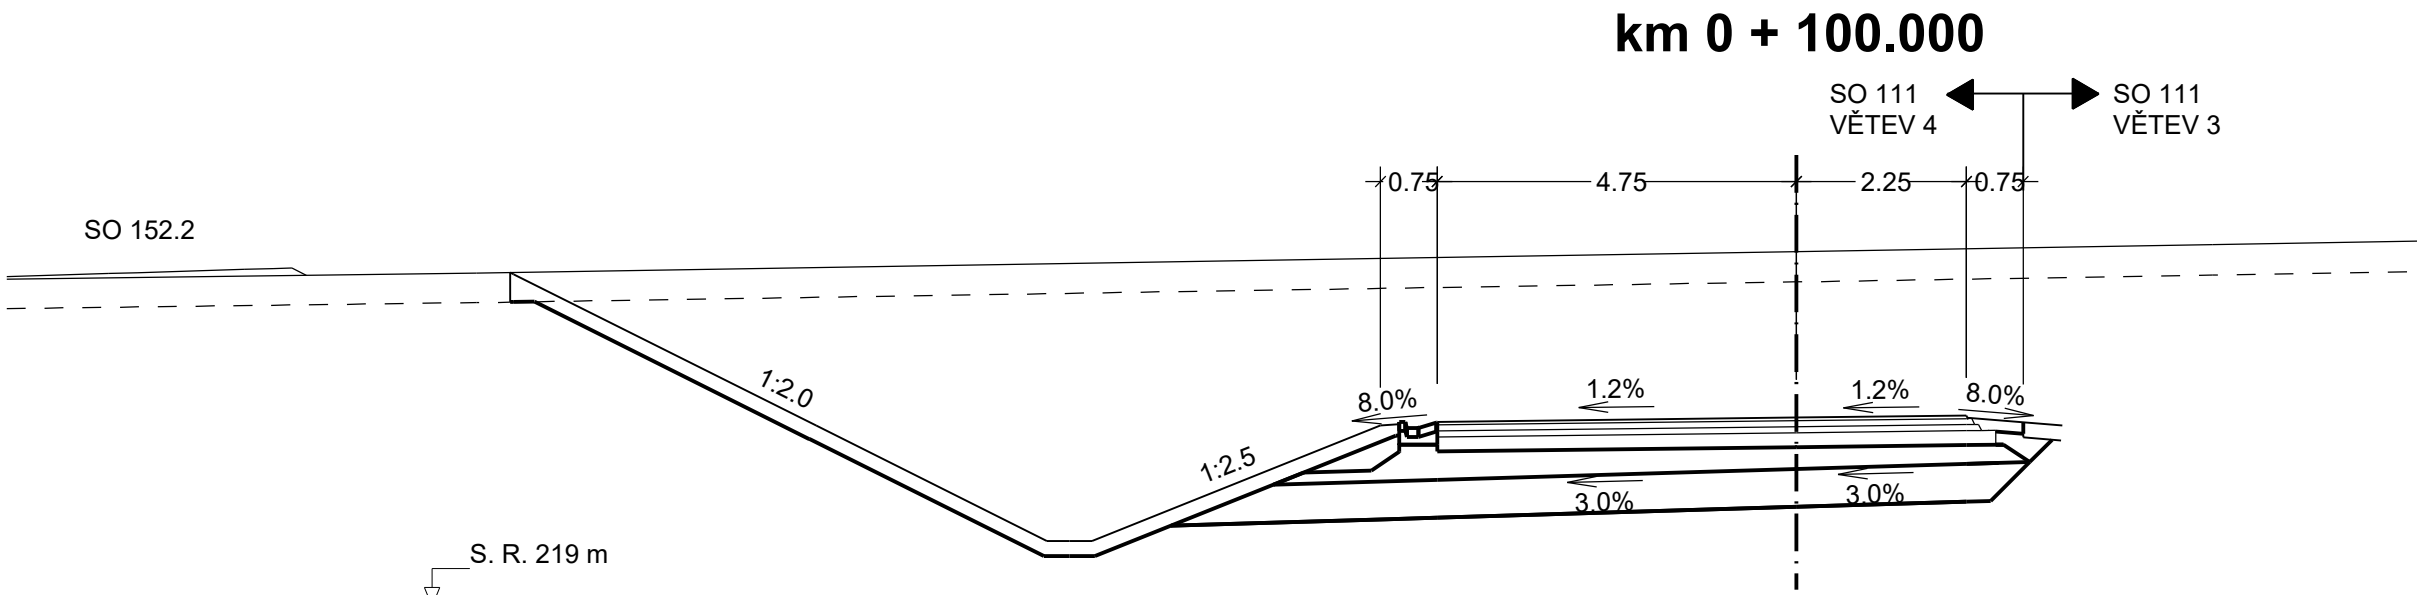

KÓTY NOVÉHO STAVU	223.41	223.02	223.39	221.39	219.86	219.86	219.86	221.39	221.49	221.52	221.48	221.49	221.43	221.39
VZDÁLENOST OD OSY	-17.01	-17.01	-16.96	-12.96	-9.91	-9.61	-9.31	-5.50	0.00	2.25	2.27	2.27	3.00	3.50
KÓTY TERÉNU														
VZDÁLENOST OD OSY	-17.46	223.40							0.00					5.51

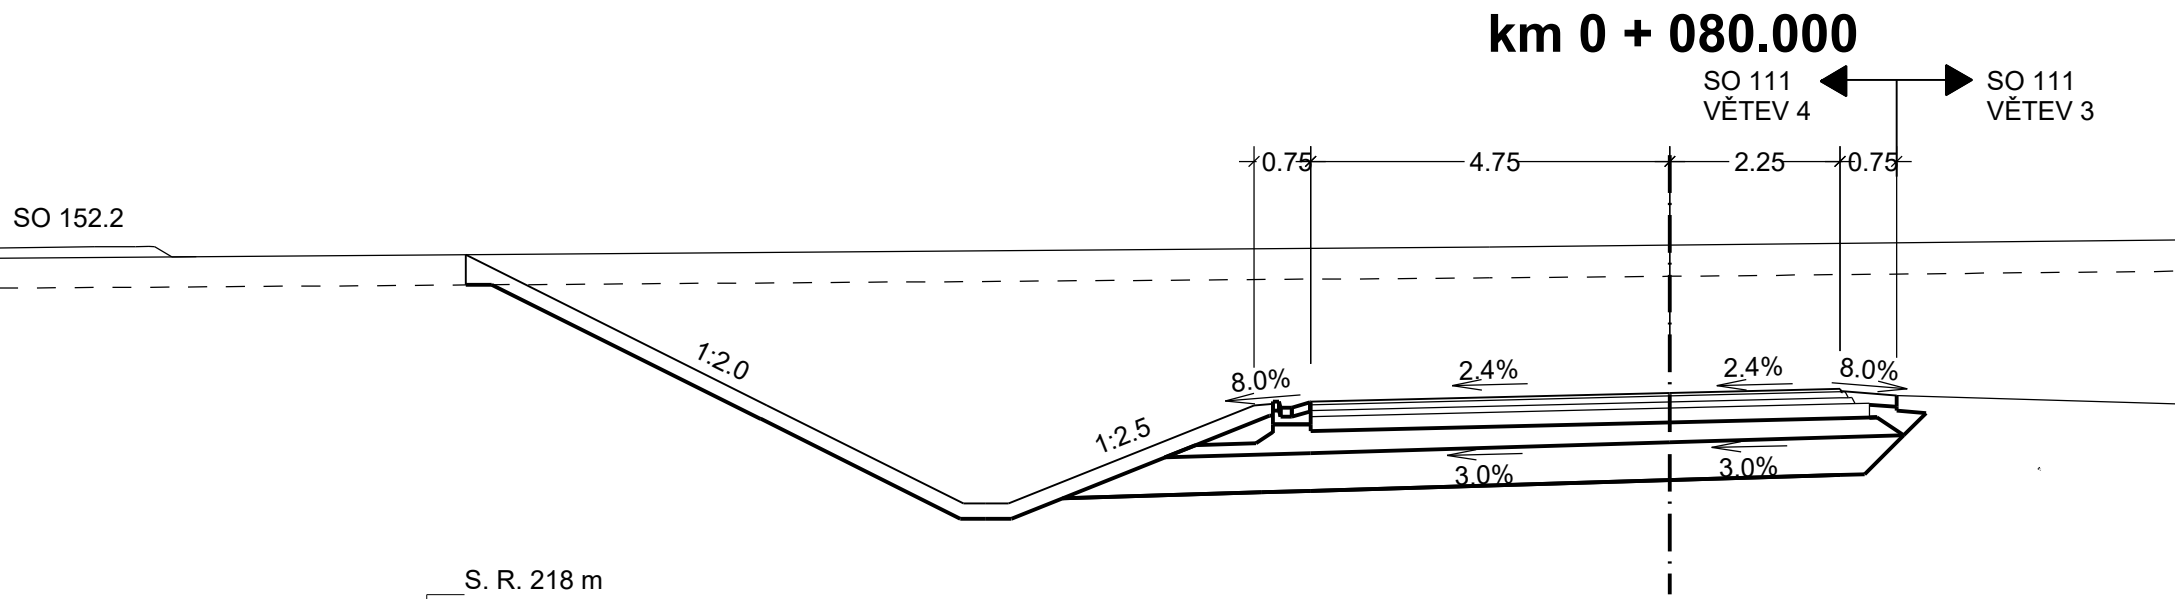

KÓTY NOVÉHO STAVU	223.00	222.60		221.00	219.70	219.70	221.00	221.02	221.05	221.00	221.17	221.22	221.18	221.19	221.13	221.09
VZDÁLENOST OD OSY	-15.93	-15.93		-11.94	-9.34	-9.04	-8.74	-5.50	-5.25	-4.75	0.00	2.25	2.27	2.27	3.00	3.50
KÓTY TERÉNU																
VZDÁLENOST OD OSY											-2.39	0.00				

Výškový systém: Bpv

SO 111 MÚK Židněves

Objednatel:



**ŘEDITELSTVÍ
SILNIC
A DÁLNIC**

Ředitelství silnic a dálnic s. p.
Čerčanská 2023/12, Krč, 140 00 Praha 4

Zhotovitel:



Valbek

Valbek, spol. s r.o.
Vaňurova 505/17
460 07 Liberec 3

HIP:

ING. T. KLIMENT

	Vypracoval	ING. A. DUMANSKA		Zak. číslo	21-L113-001
	Zodp. projektant	ING. T. KLIMENT		Datum	02/2025
	Tech. kontrola	ING. M. HANŽL		Stupeň	PDPS
	Akce I/16 MLADÁ BOLESLAV - MARTINOVICE			Počet formátů	4 x A4
				Měřítko	1 : 100
Zhotovitel: Valbek, spol. s r.o. Vaňurova 505/17 460 07 Liberec 3	Příloha	PŘÍČNÉ ŘEZY VĚTEV 4			5.4