
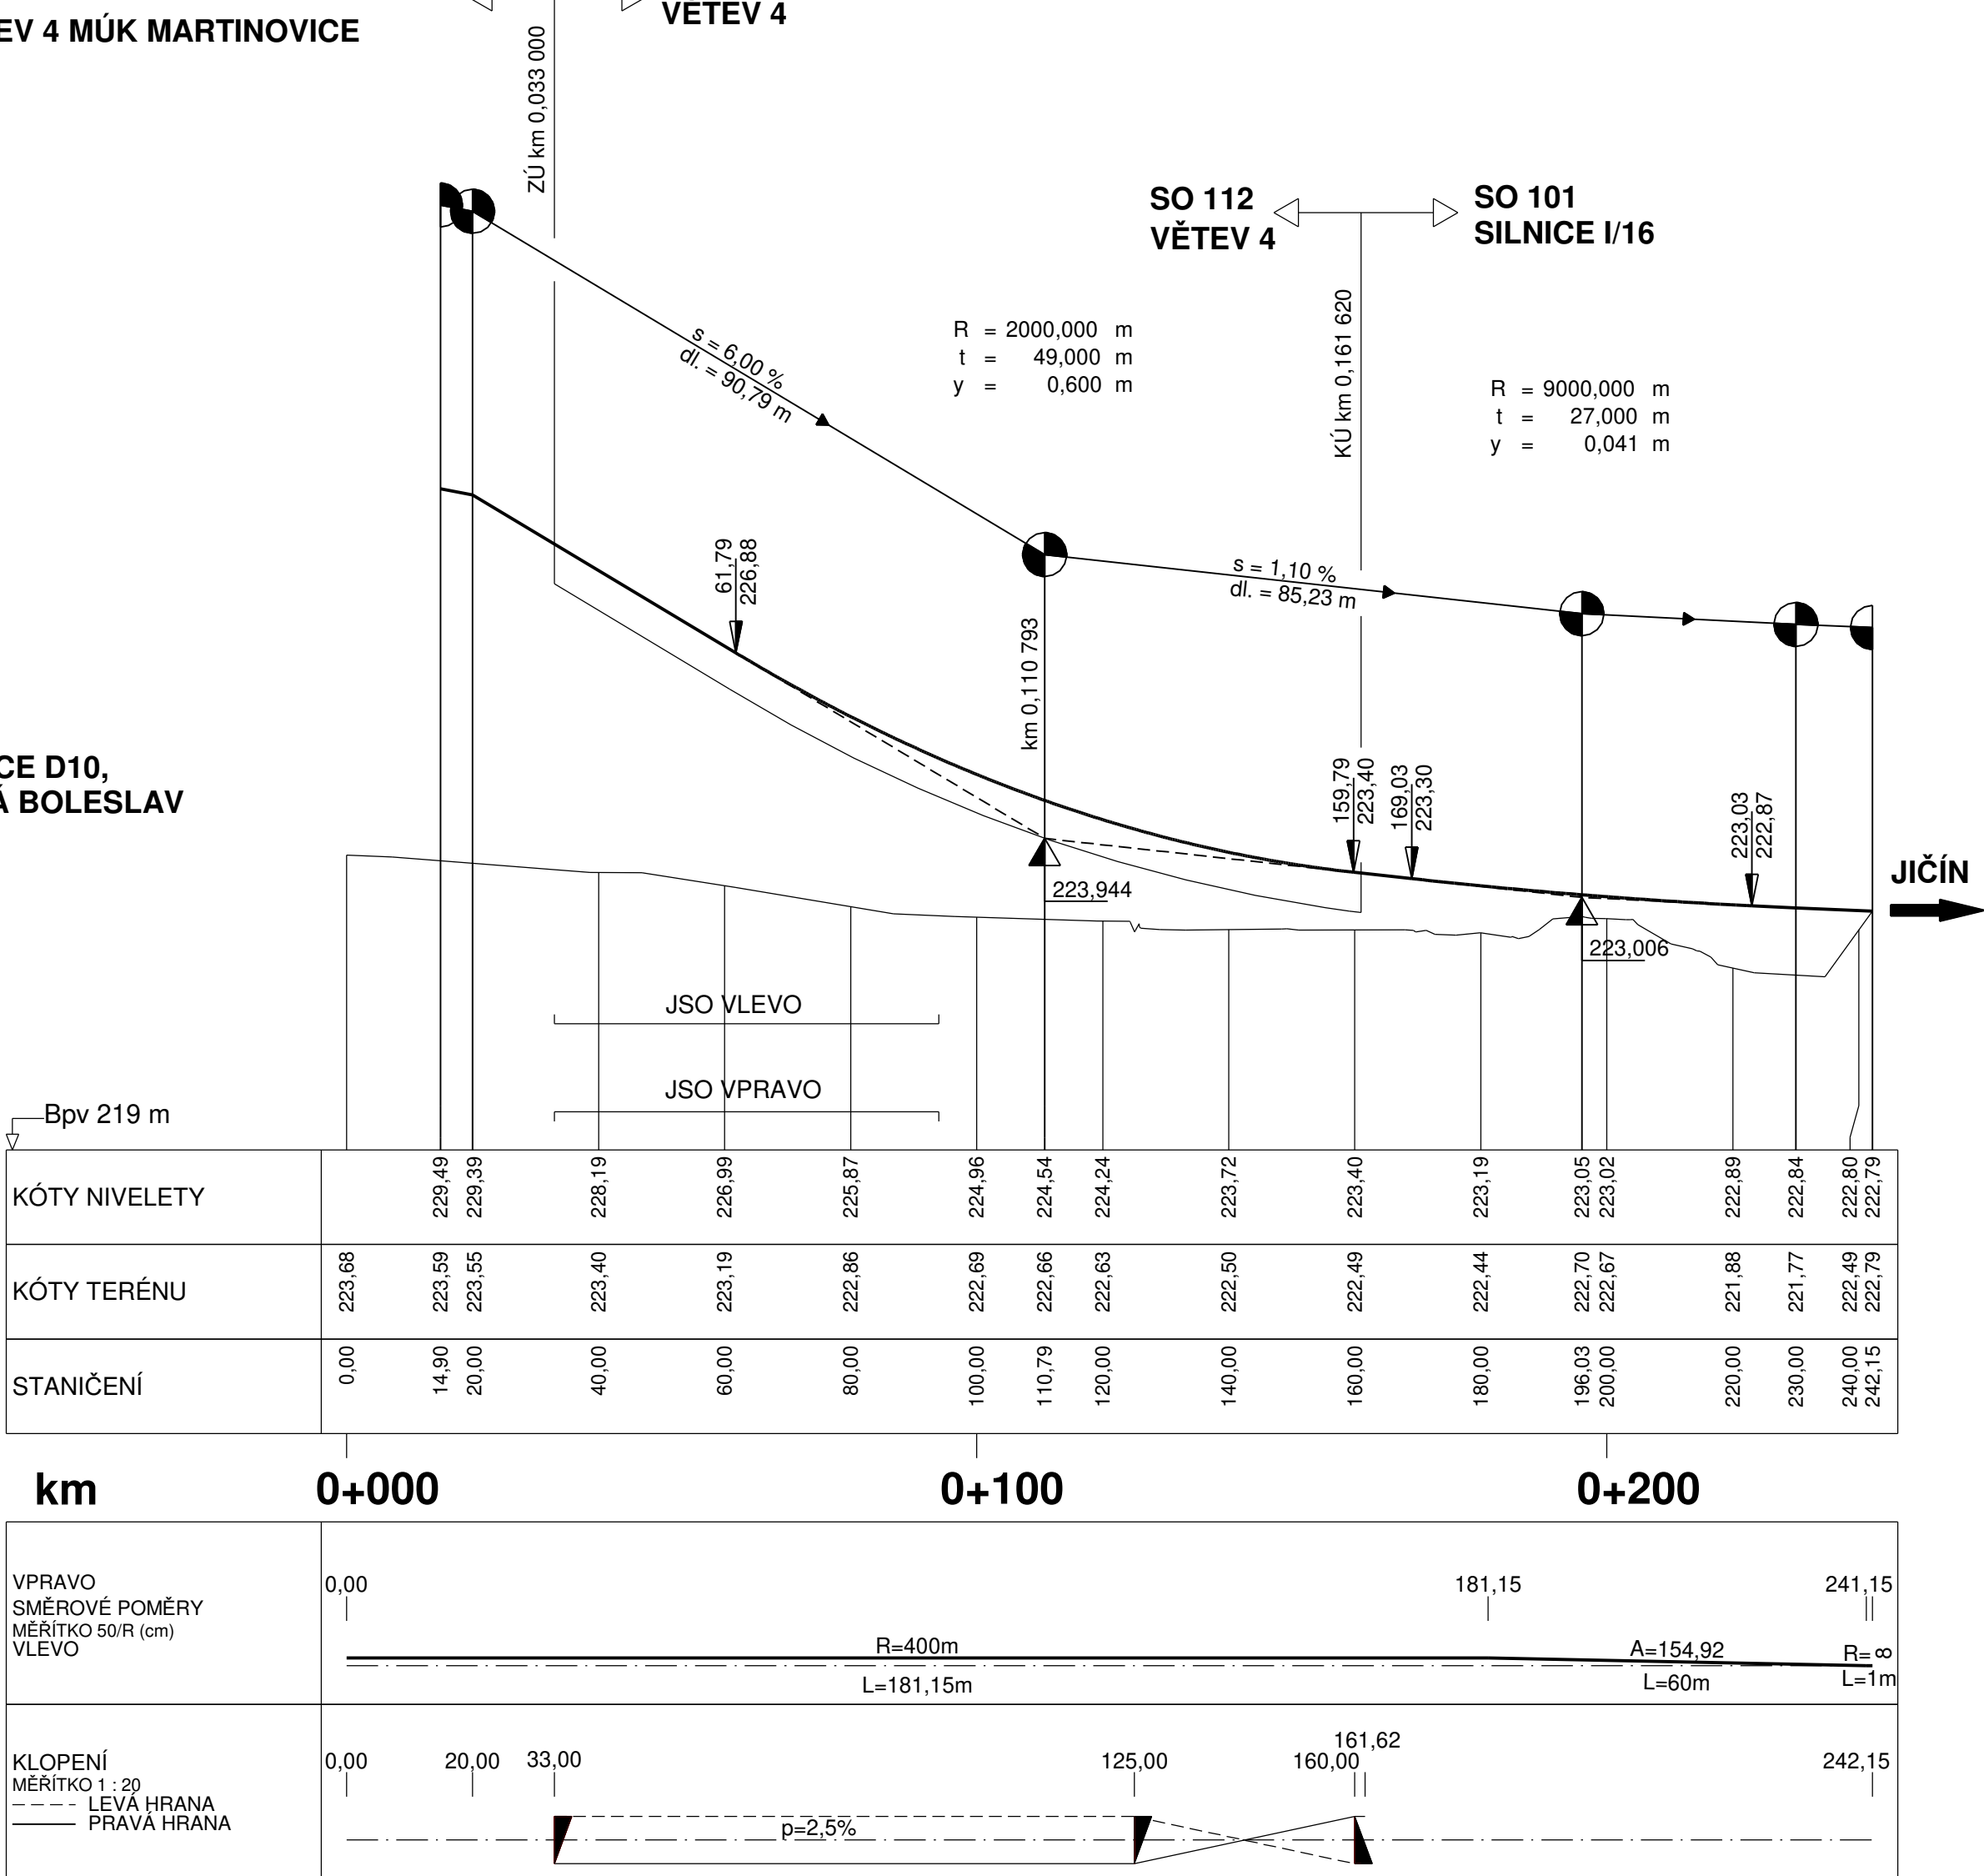
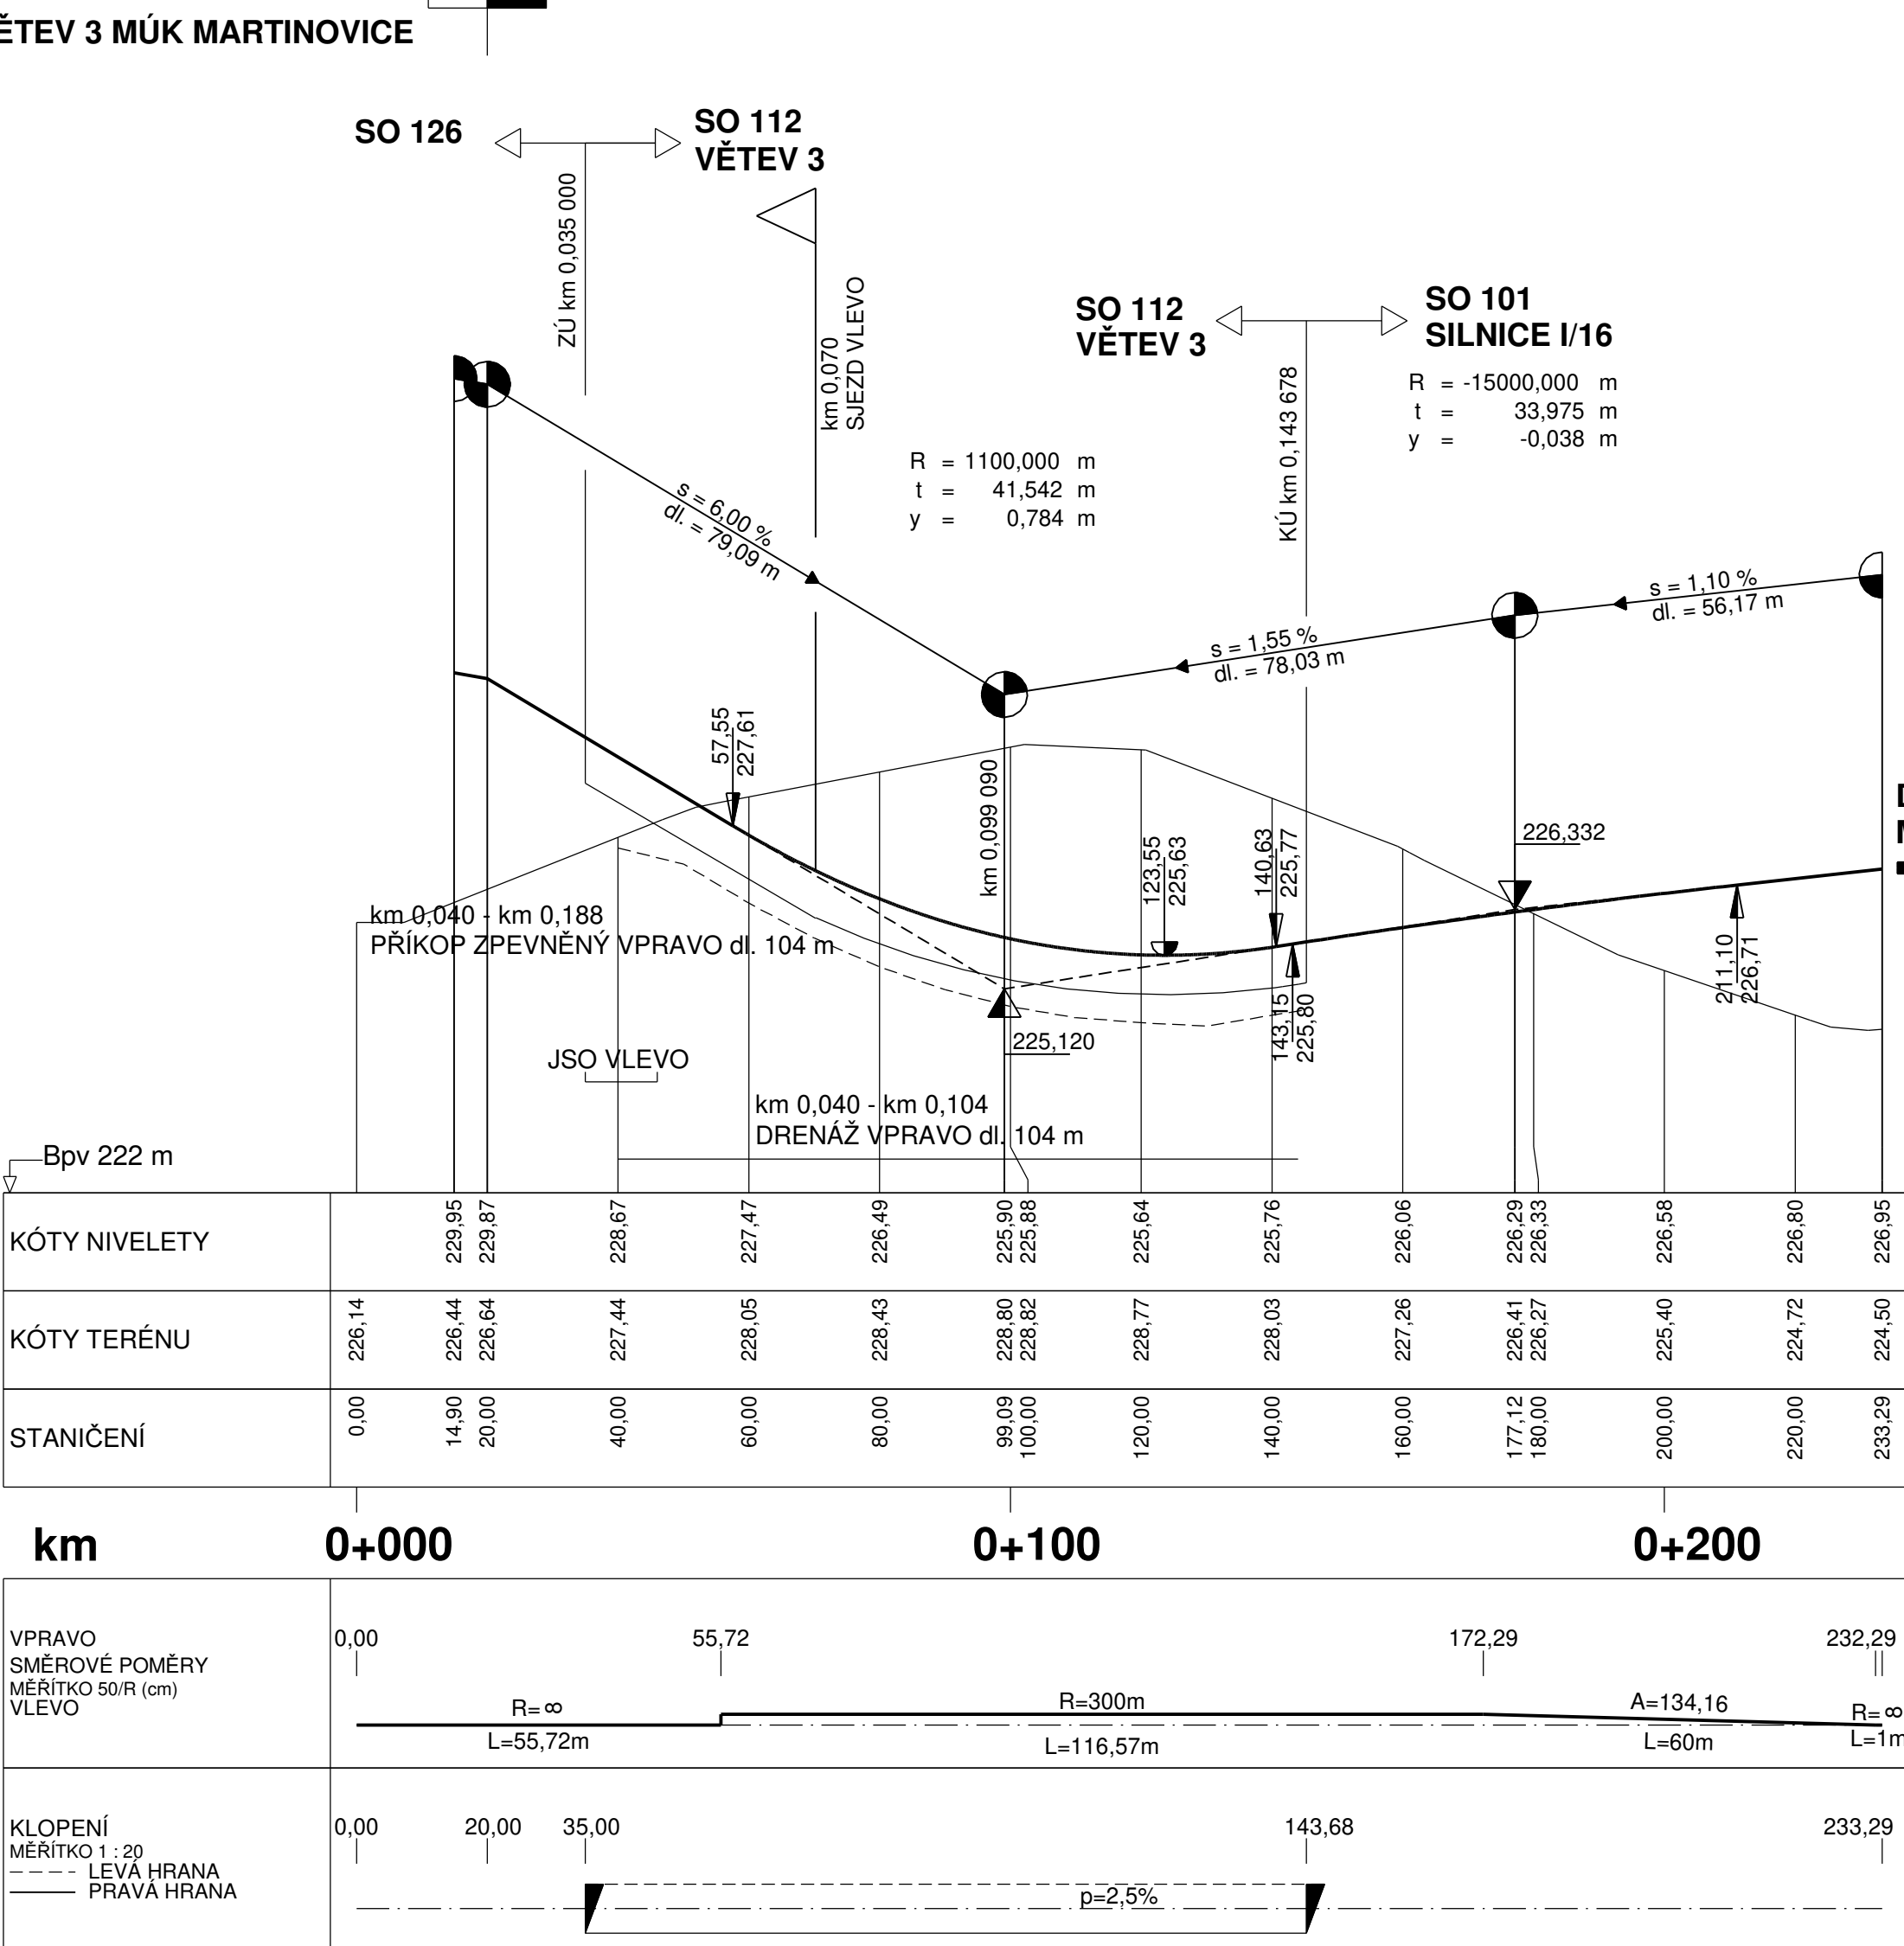
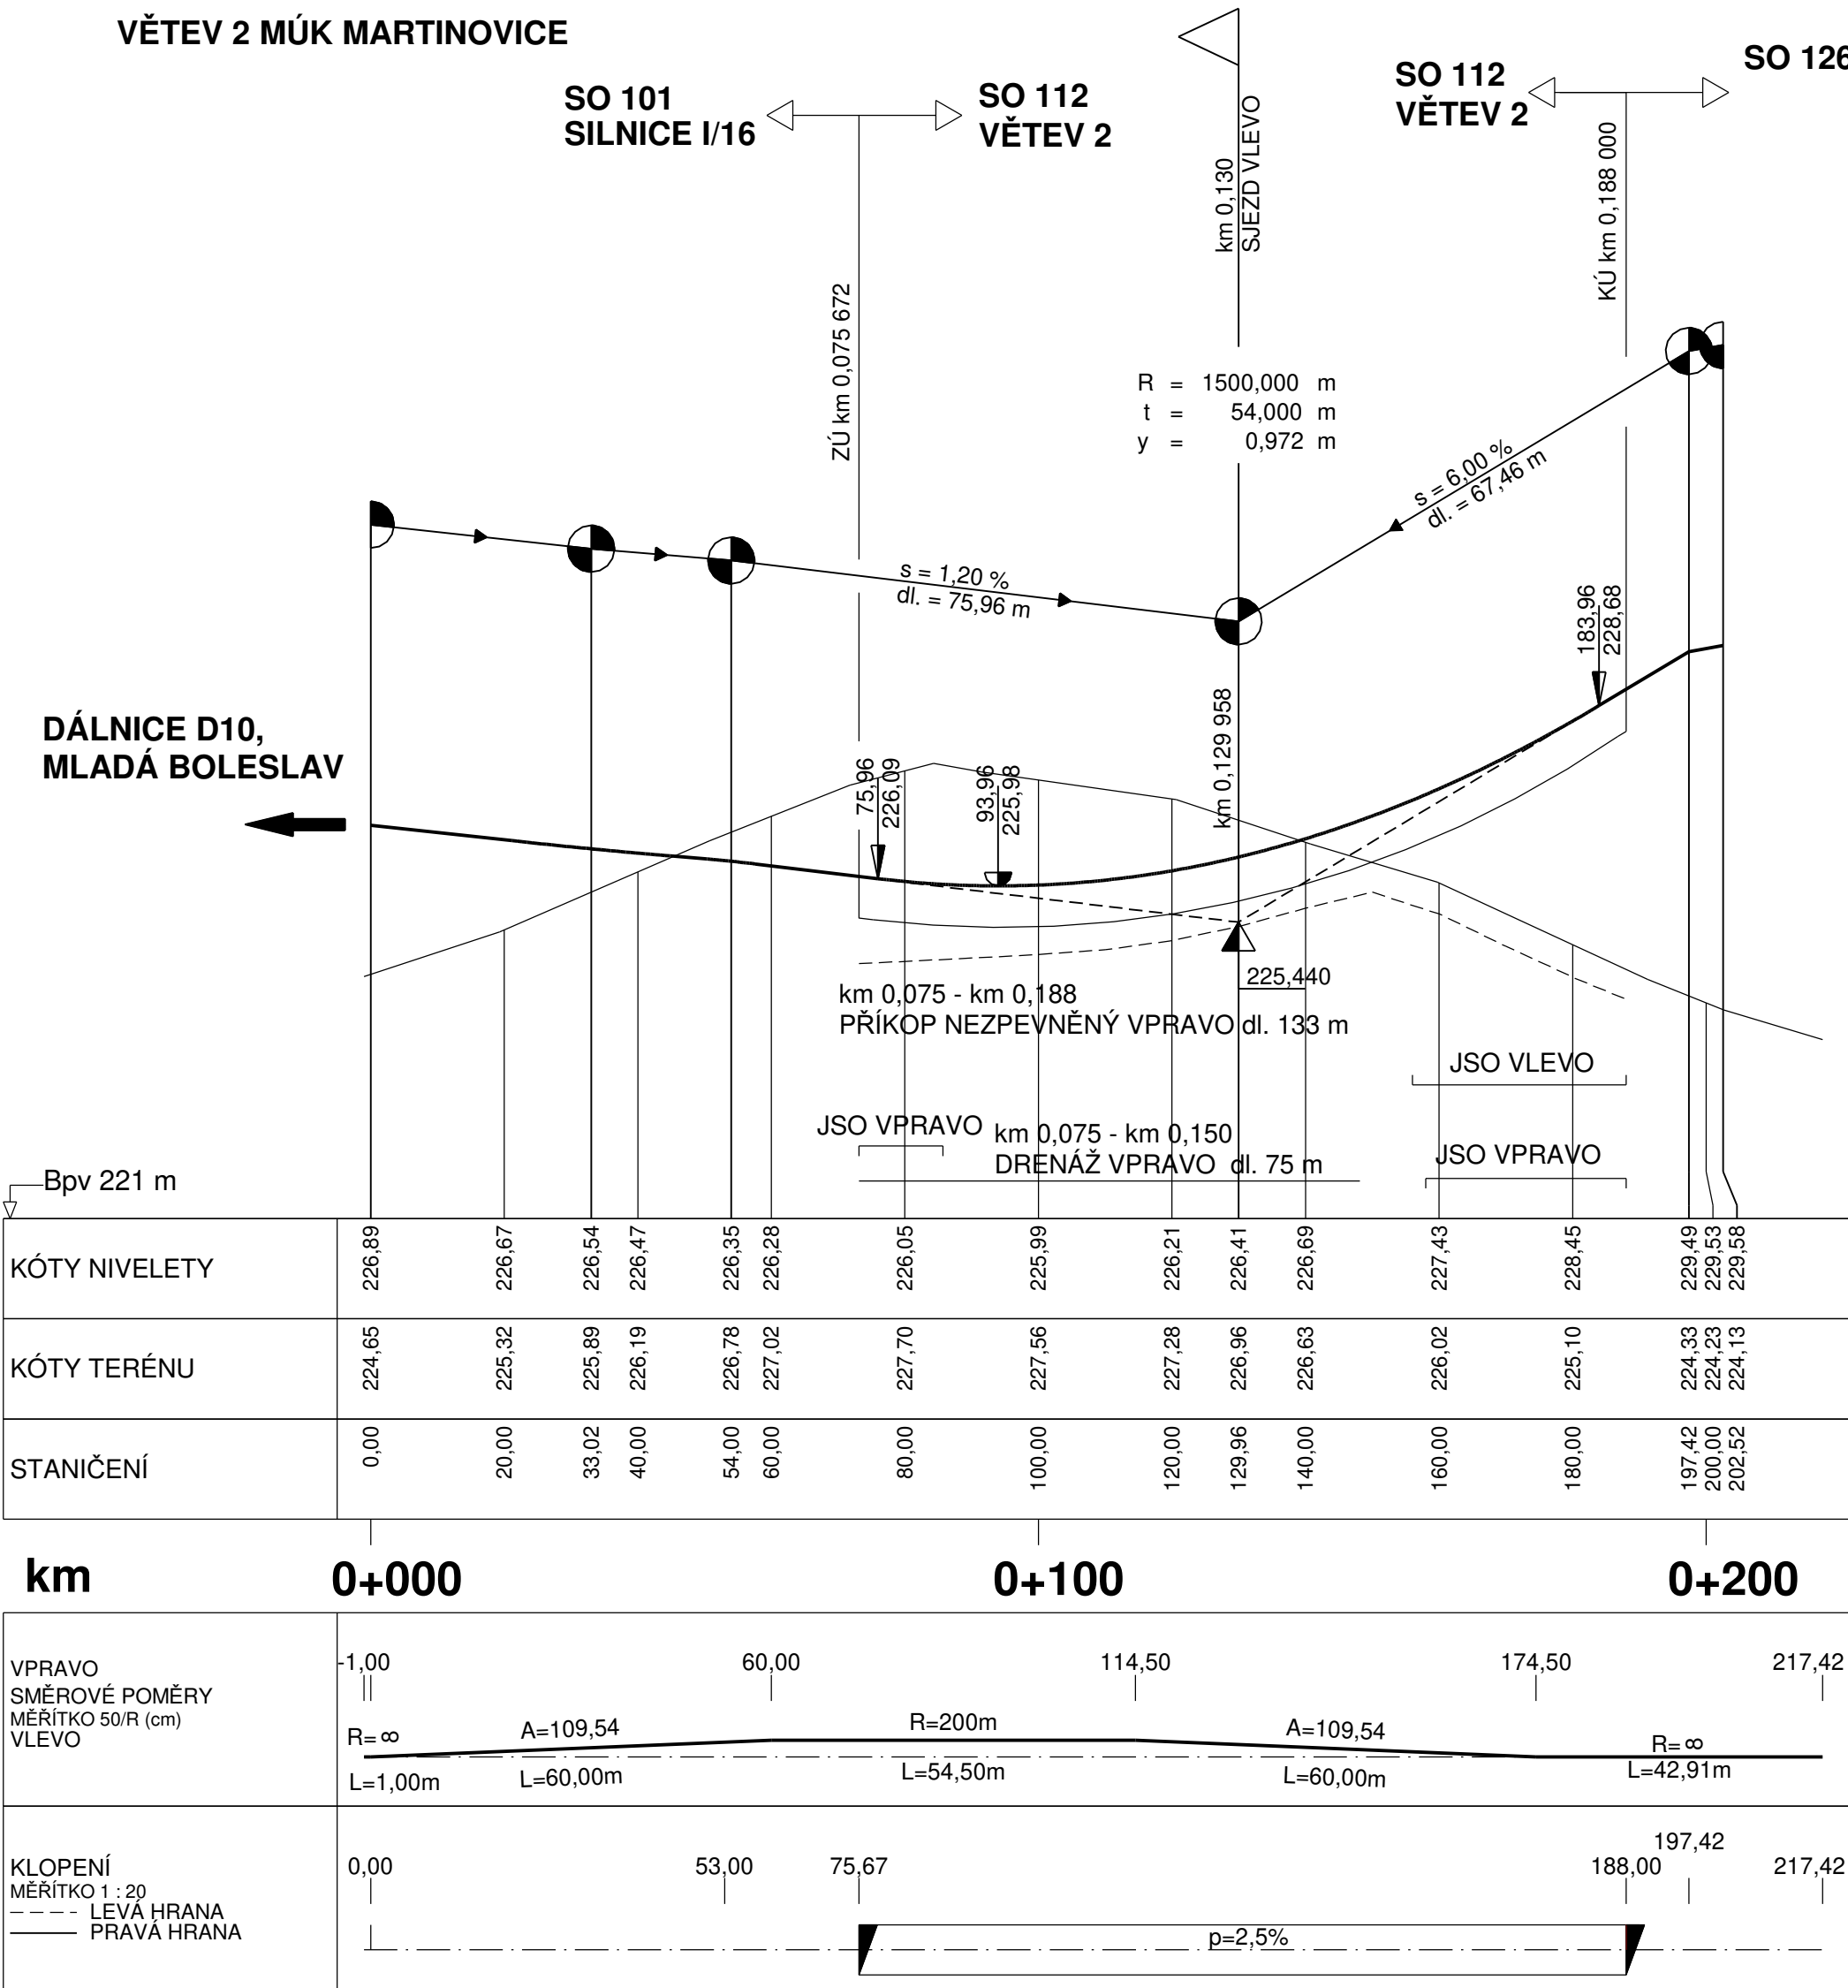


# SO 112 - MÚK MARTINOVICE

## PODÉLNÉ PROFILY M 1 : 1 000 / 100

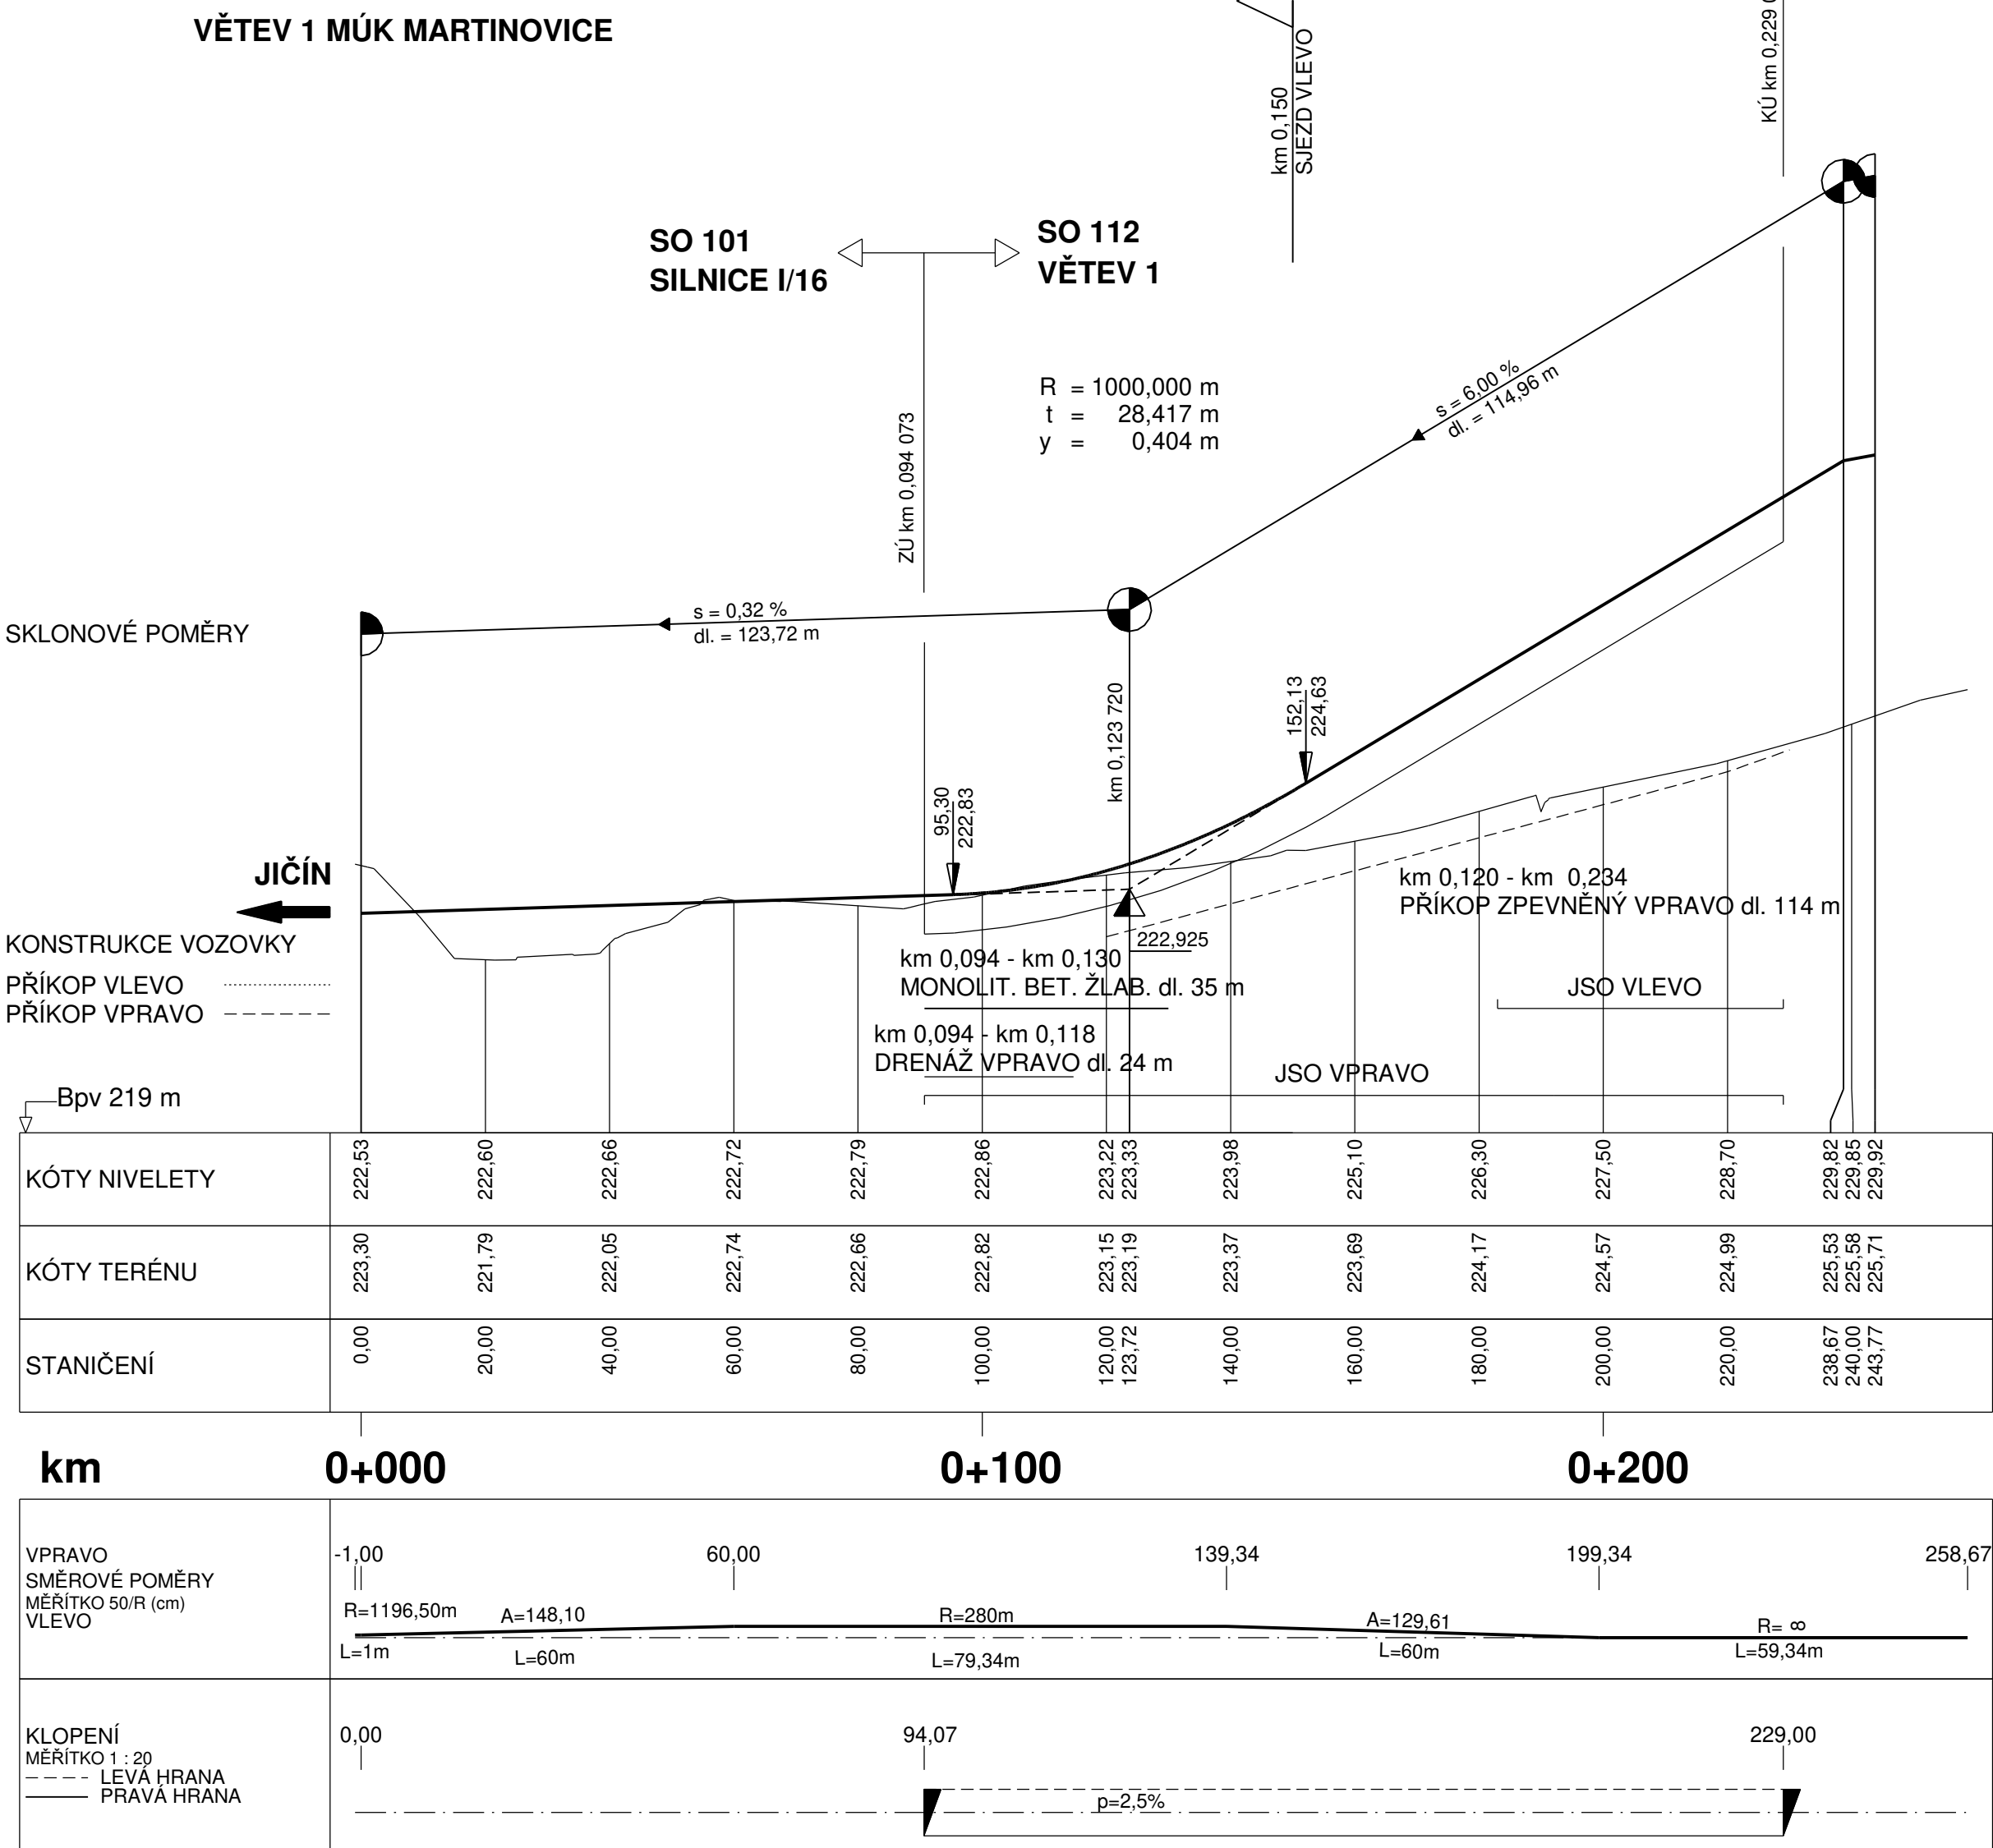

### Účelový systém Bpv

SO 112 MÚK MARTINOVICE

**Objednatel:**



**Ředitelství silnic a dálnic s. p.**  
Čerčanská 2023/12, Krč, 140 00 Praha 4

**Zhotovitel:**



**Valbek, spol. s r.o.**  
Vaňurova 505/17  
460 07 Liberec 3

|      |  |
|------|--|
| HIP: |  |
|------|--|

ING T KLIMEN

|                                                                                       |                                |                                   |  |               |               |
|---------------------------------------------------------------------------------------|--------------------------------|-----------------------------------|--|---------------|---------------|
|  | Vypracoval                     | M. KOŘINEK                        |  | Zak. číslo    | 21-L113-001   |
|                                                                                       | Zodp. projektant               | ING. T. KLIMENT                   |  | Datum         | 02/2025       |
|                                                                                       | Tech. kontrola                 | ING. M. HANŽL                     |  | Stupeň        | PDPS          |
|                                                                                       | Akce                           | I/16 MLADÁ BOLESLAV - MARTINOVICE |  | Počet formátů | 7x44          |
|                                                                                       |                                |                                   |  | Měřítko       | M1 : 1000/100 |
|                                                                                       |                                |                                   |  | Č. přílohy    | Paré          |
| Zhotovitel:<br>Valbek, spol. s r.o.<br>Raškovice 555/17<br>460 07 Liberec 3           | Příloha<br><br>PODÉLNÉ PROFILY |                                   |  | <b>3</b>      |               |