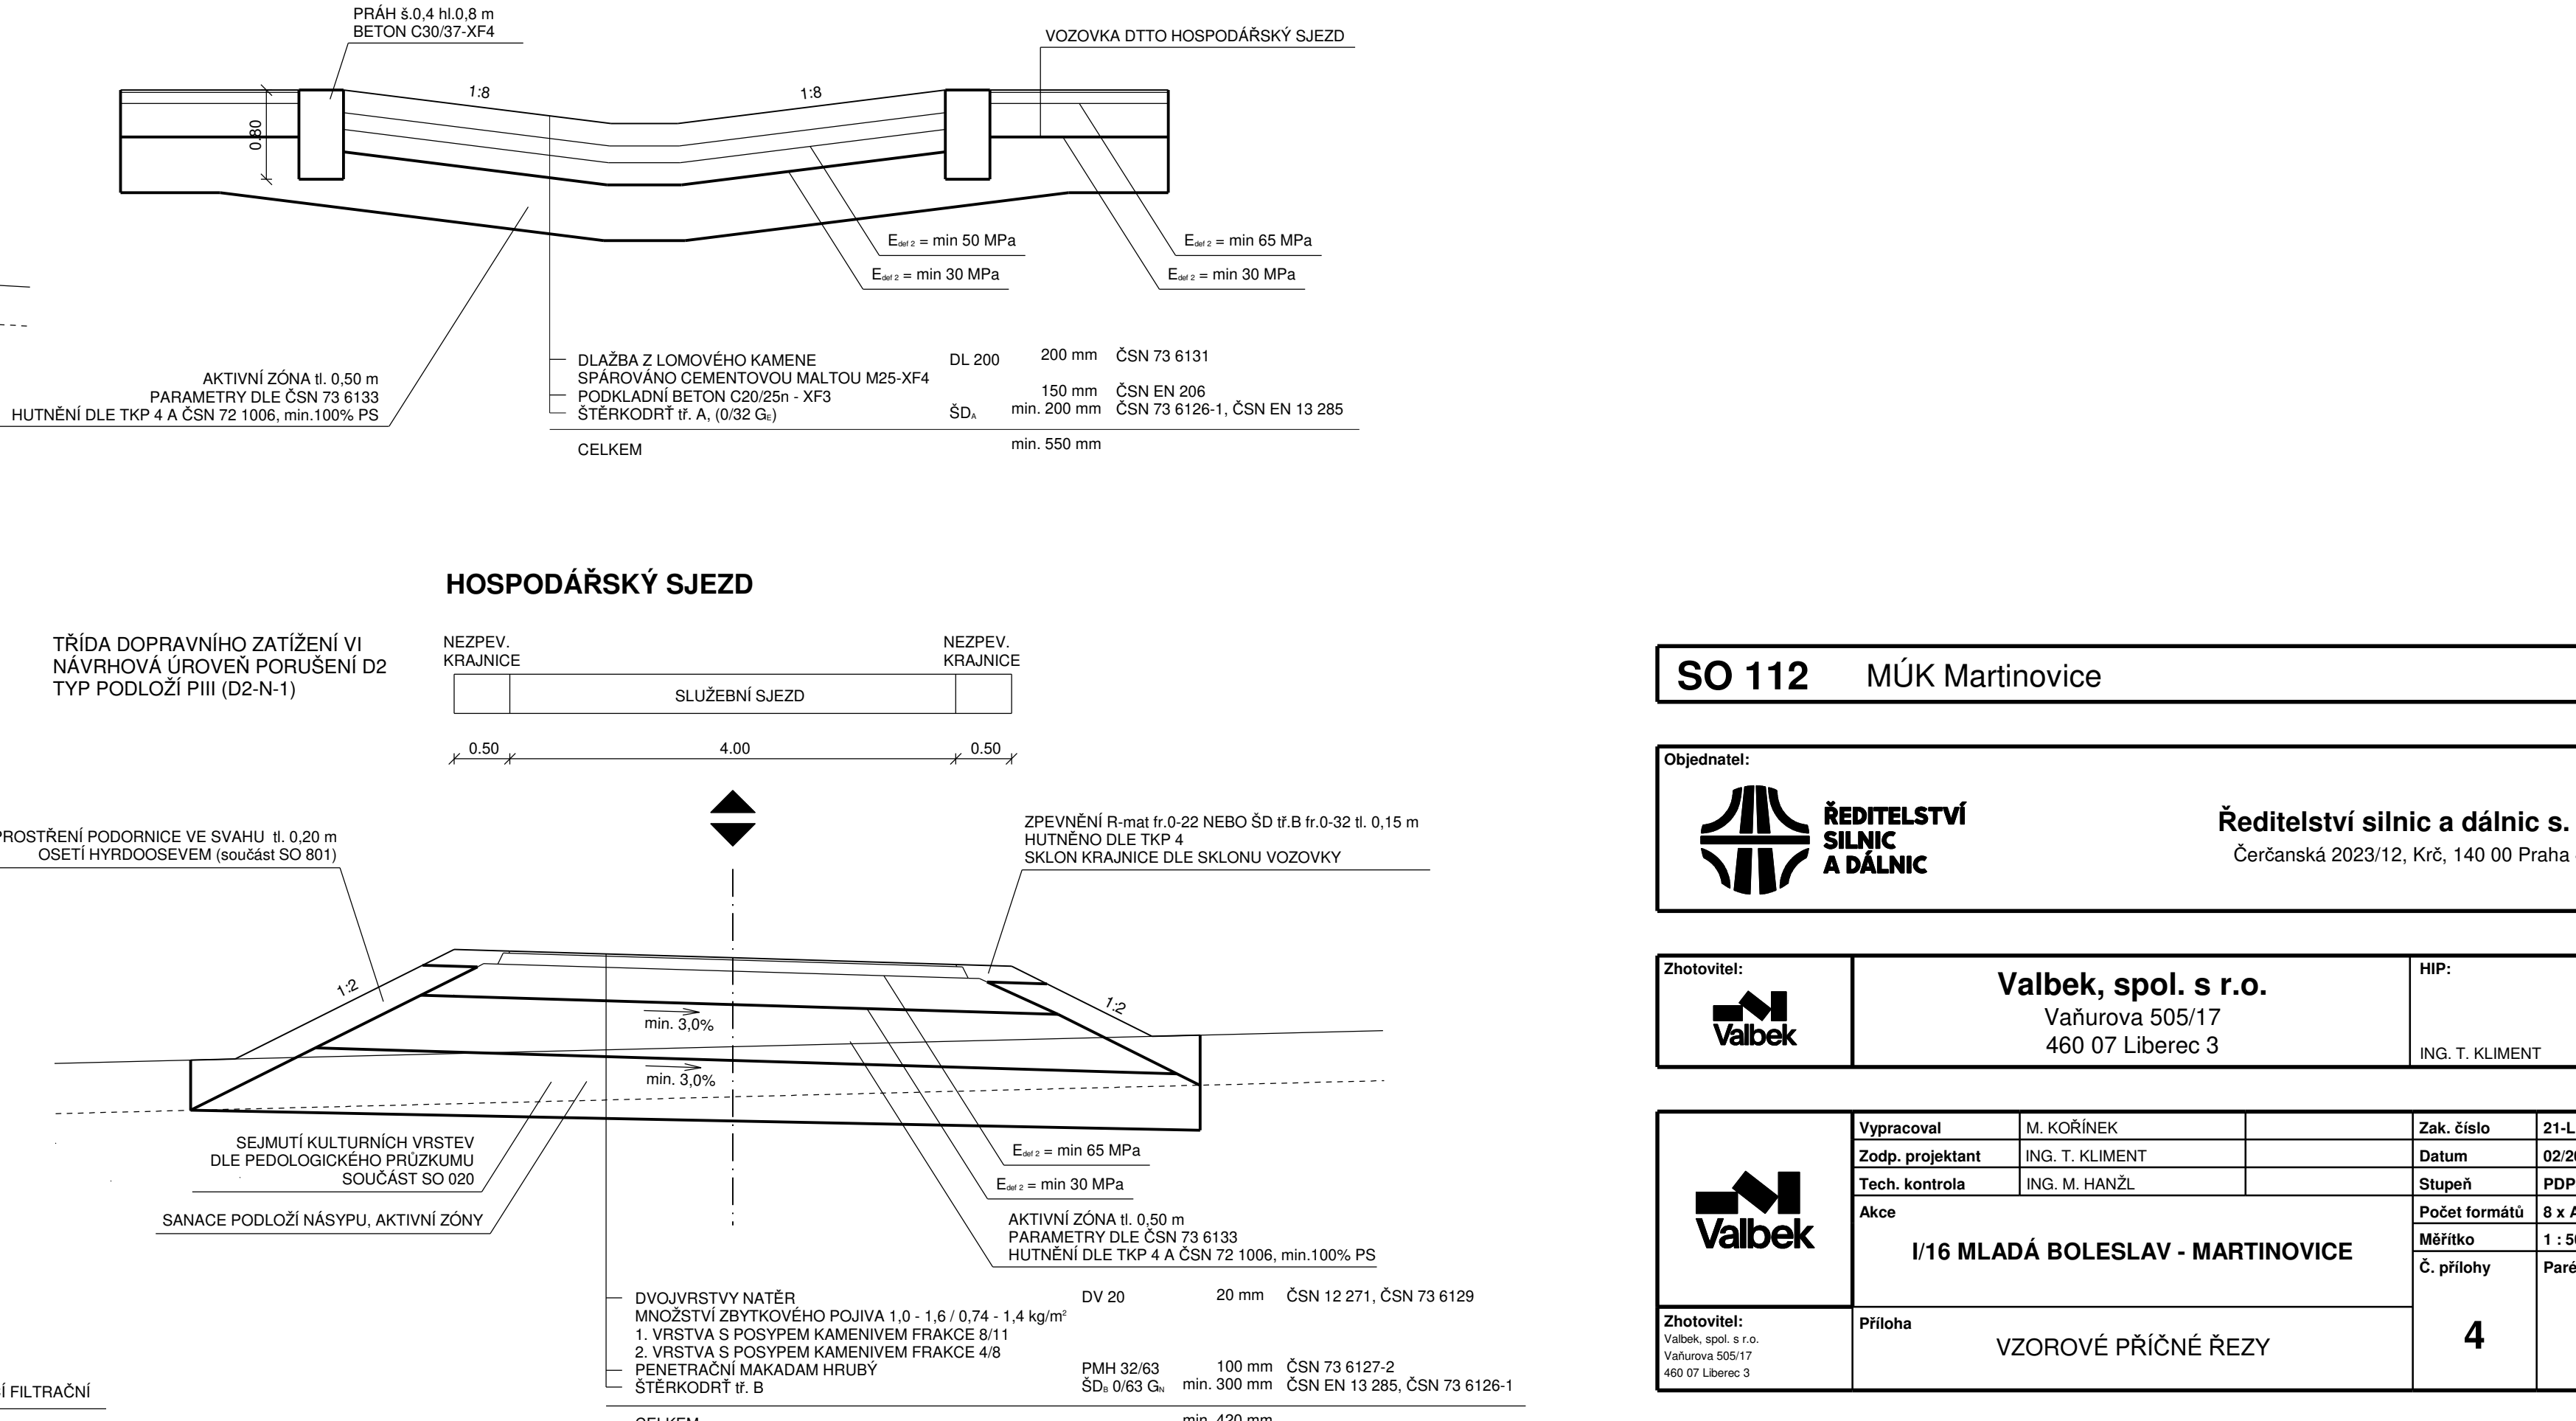
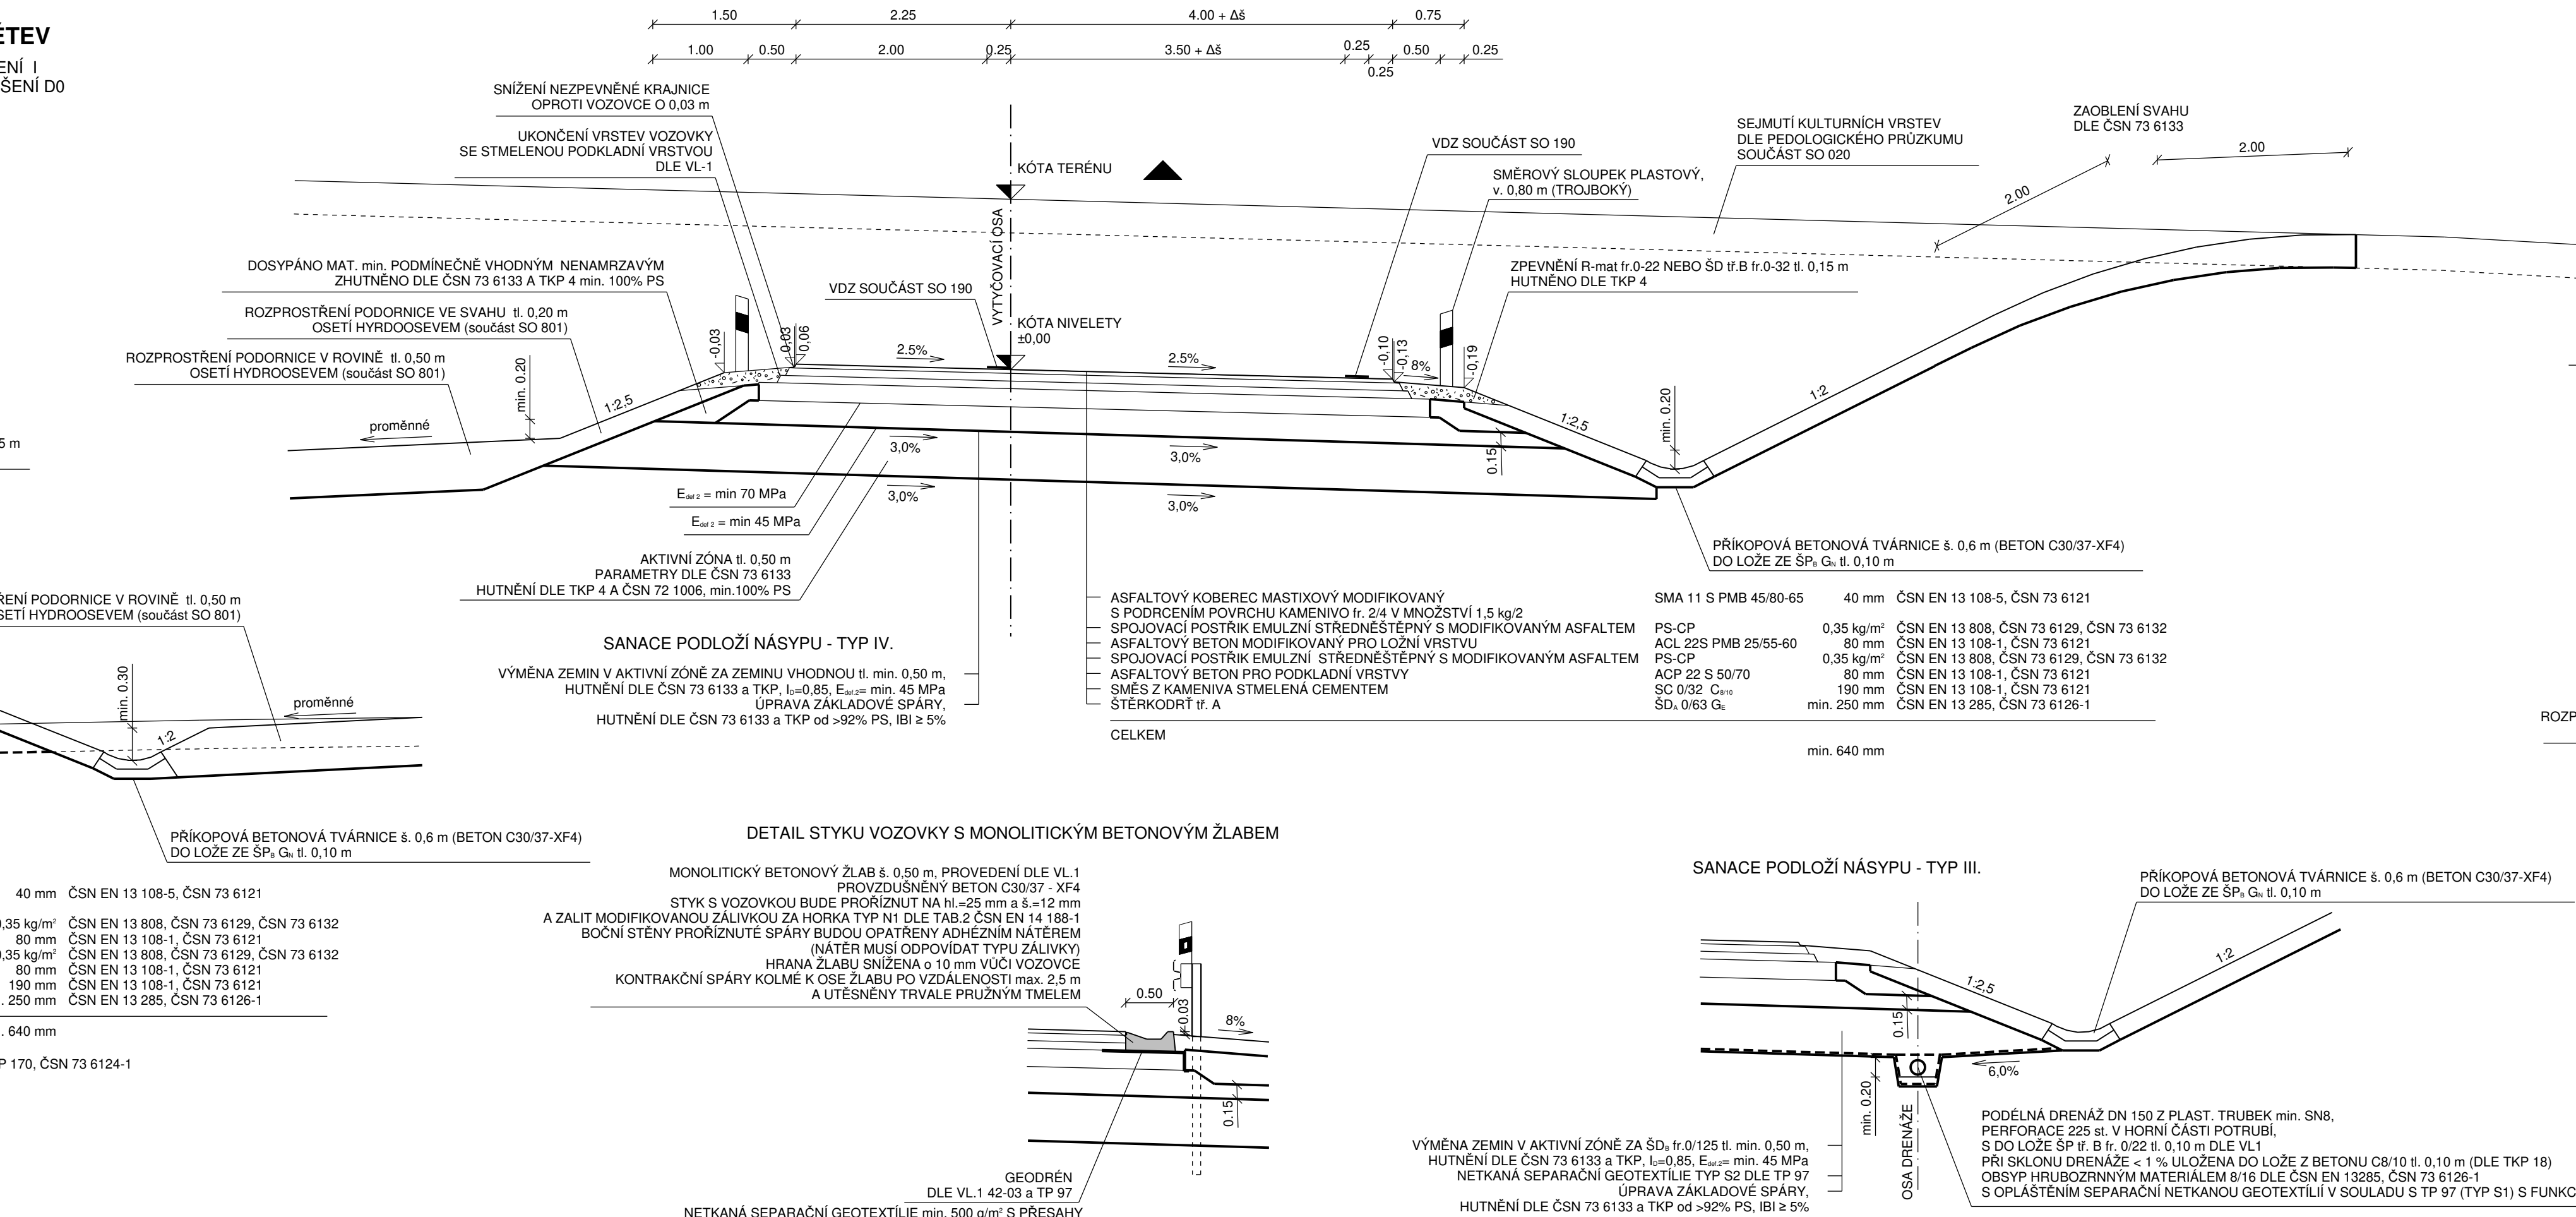
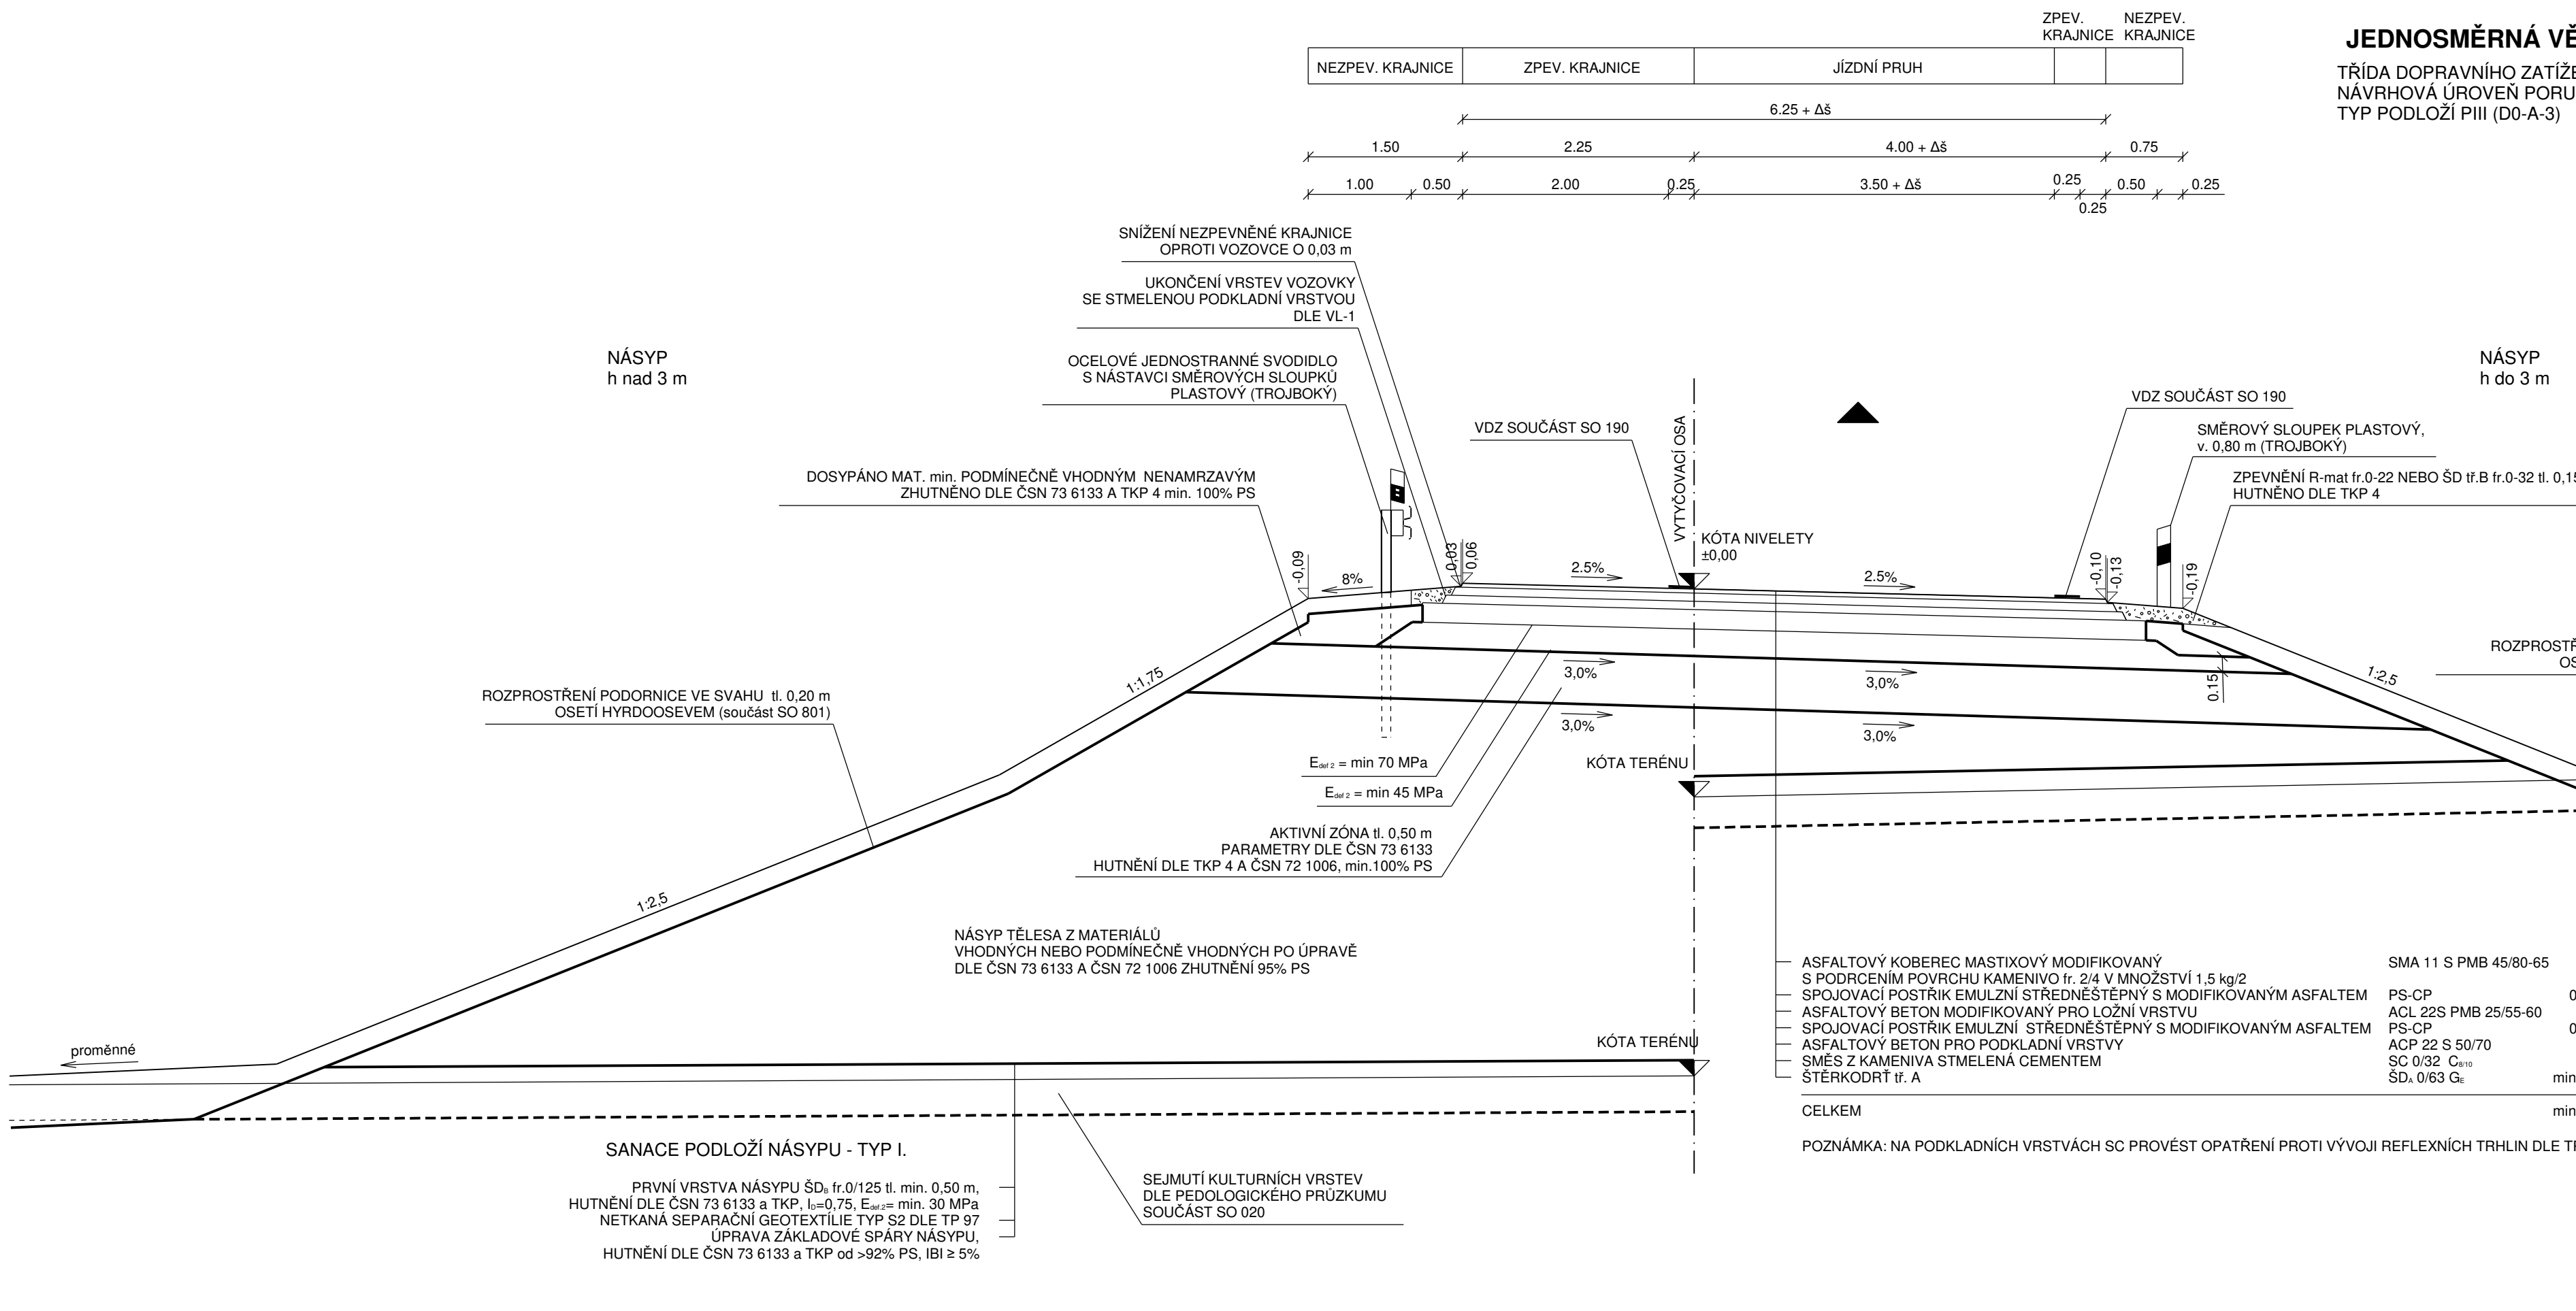


SO 112 - MÚK MARTINOVICE
VZOROVÉ PŘÍČNÉ ŘEZY M 1 : 50

SO 112 MÚK Martinovice

Objednatel:	
	Ředitelství silnic a dálnic s. Čerčanská 2023/12, Krč, 140 00 Praha

Zhotovitel:	Valbek, spol. s r.o. Vaňurova 505/17 460 07 Liberec 3	HIP: ING. T. KLIMENT
-------------	--	-----------------------------

	Vypracoval	M. KOŘÍNEK		Zak. číslo	21-L
	Zodp. projektant	ING. T. KLIMENT		Datum	02/20
	Tech. kontrola	ING. M. HANŽL		Stupeň	PDP
	Akce	I/16 MLADÁ BOLESLAV - MARTINOVICE		Počet formátů	8 x 4
Zhotovitel: Valbek, spol. s r.o. Valburova 505/17 460 07 Liberec 3	Příloha	VZOROVÉ PŘÍČNÉ ŘEZY		Měřitko	1 : 5
				Č. přílohy	Paré
				4	