



**SO 112 - MŮK MARTINOVCE
PŘÍČNÉ ŘEZY, VĚTEV č. 1, M 1 : 100**

PRÍČNE REZY, VĚTEV Č. 1, M 1 : 100

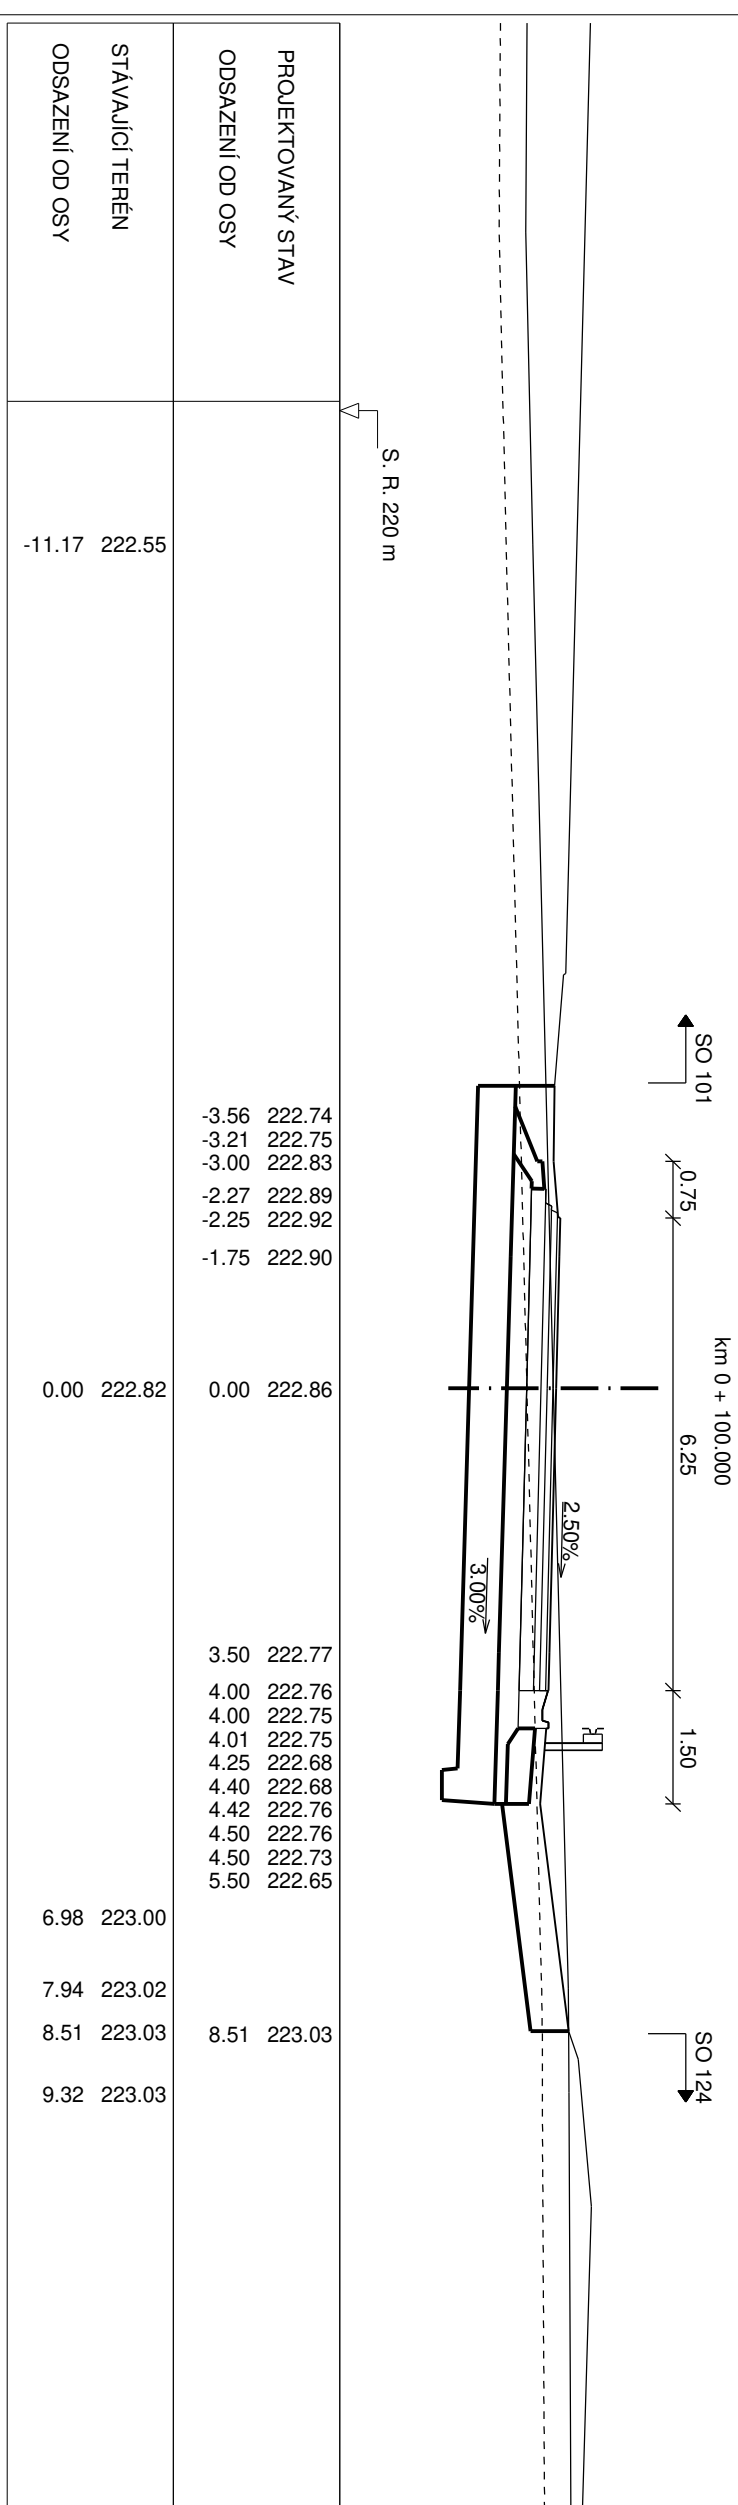


--	--

PROJEKT	STÁVA
ODSAZ	ODSAZ

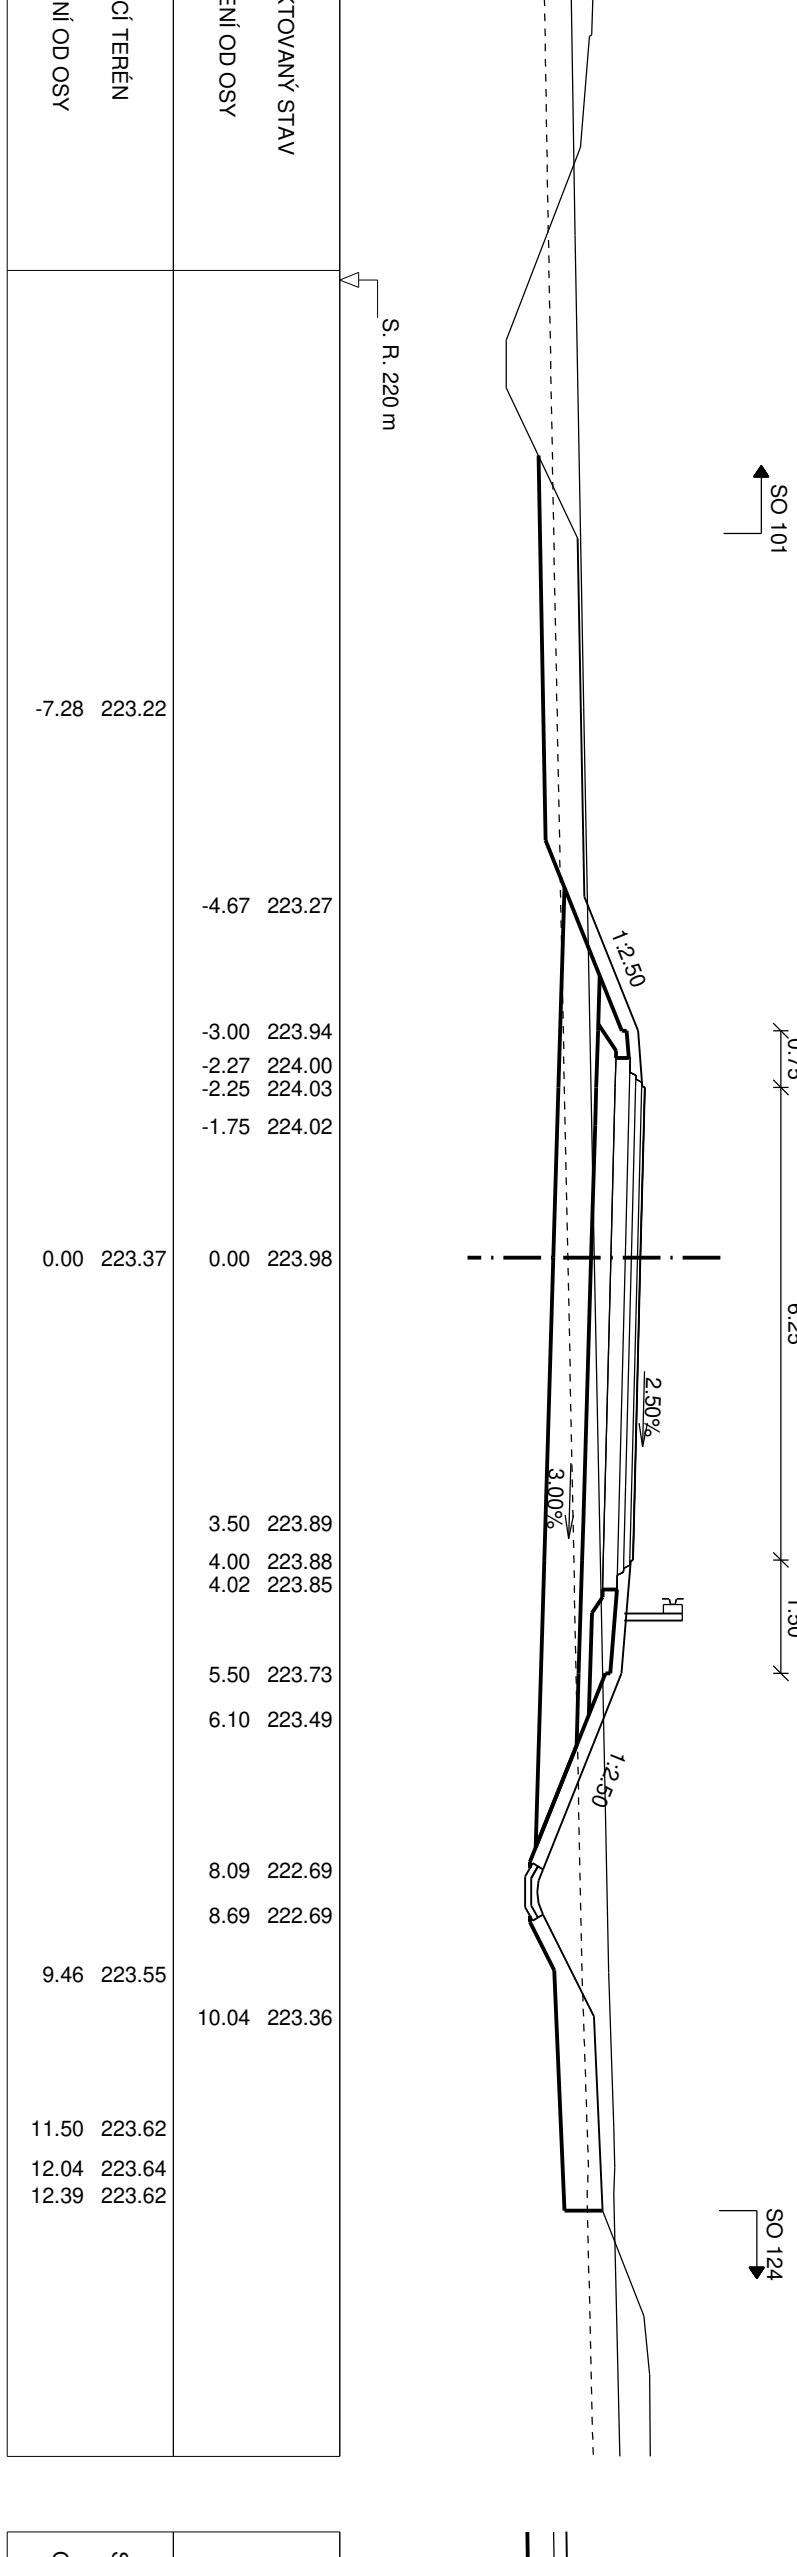


PROJEKTOVÝ ODSAZENÍ	
TÁVAJÍCÍ ODSAZENÍ	

MANÝSTAV	
OD OSY	
ERÉN	
D OSY	

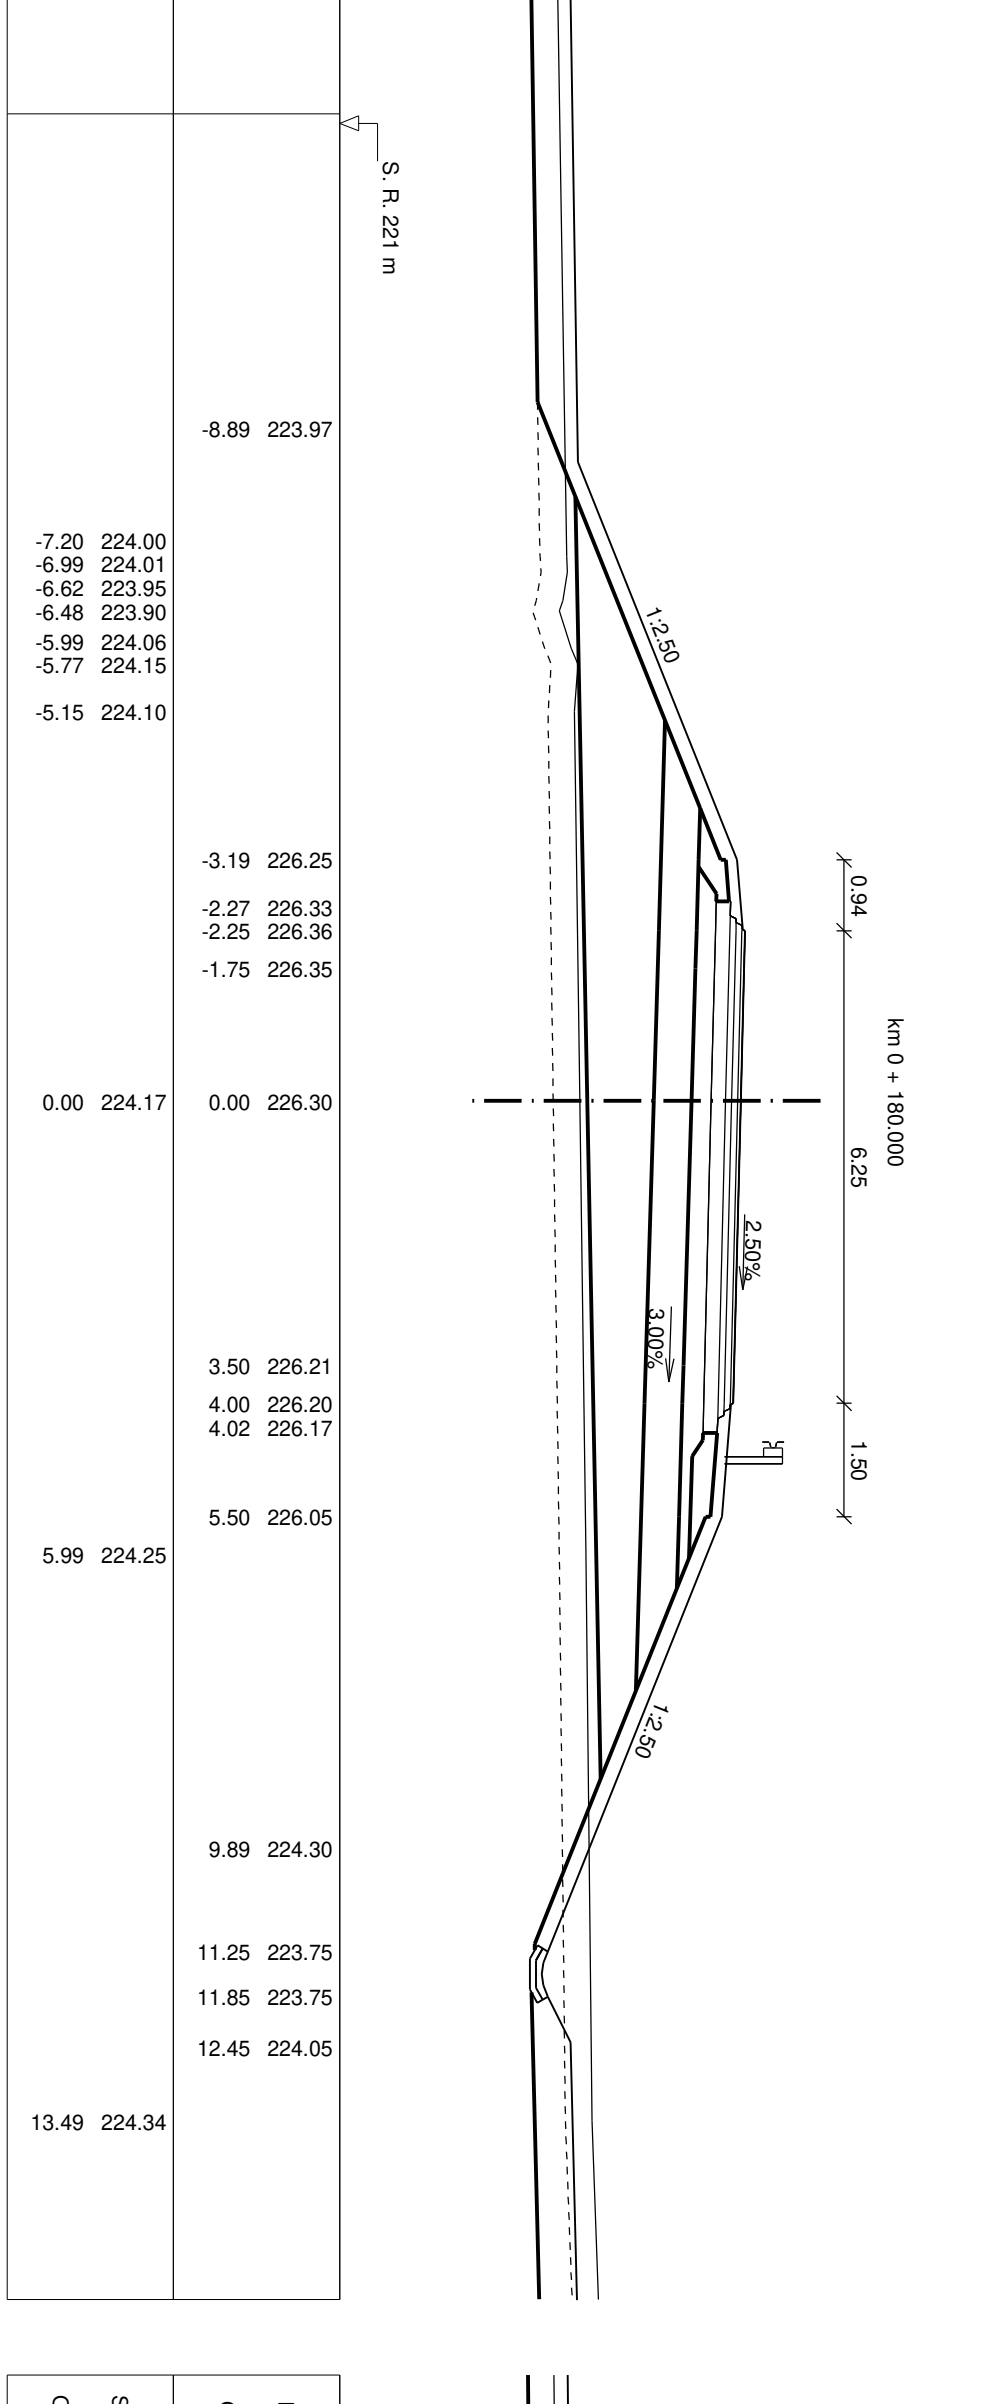

PROJEKT	
DSAZENÍ	
TRÁVAJÍCÍ T	
DSAZENÍ	

ANY STAV	DD OSY
ERÉN	DD OSY

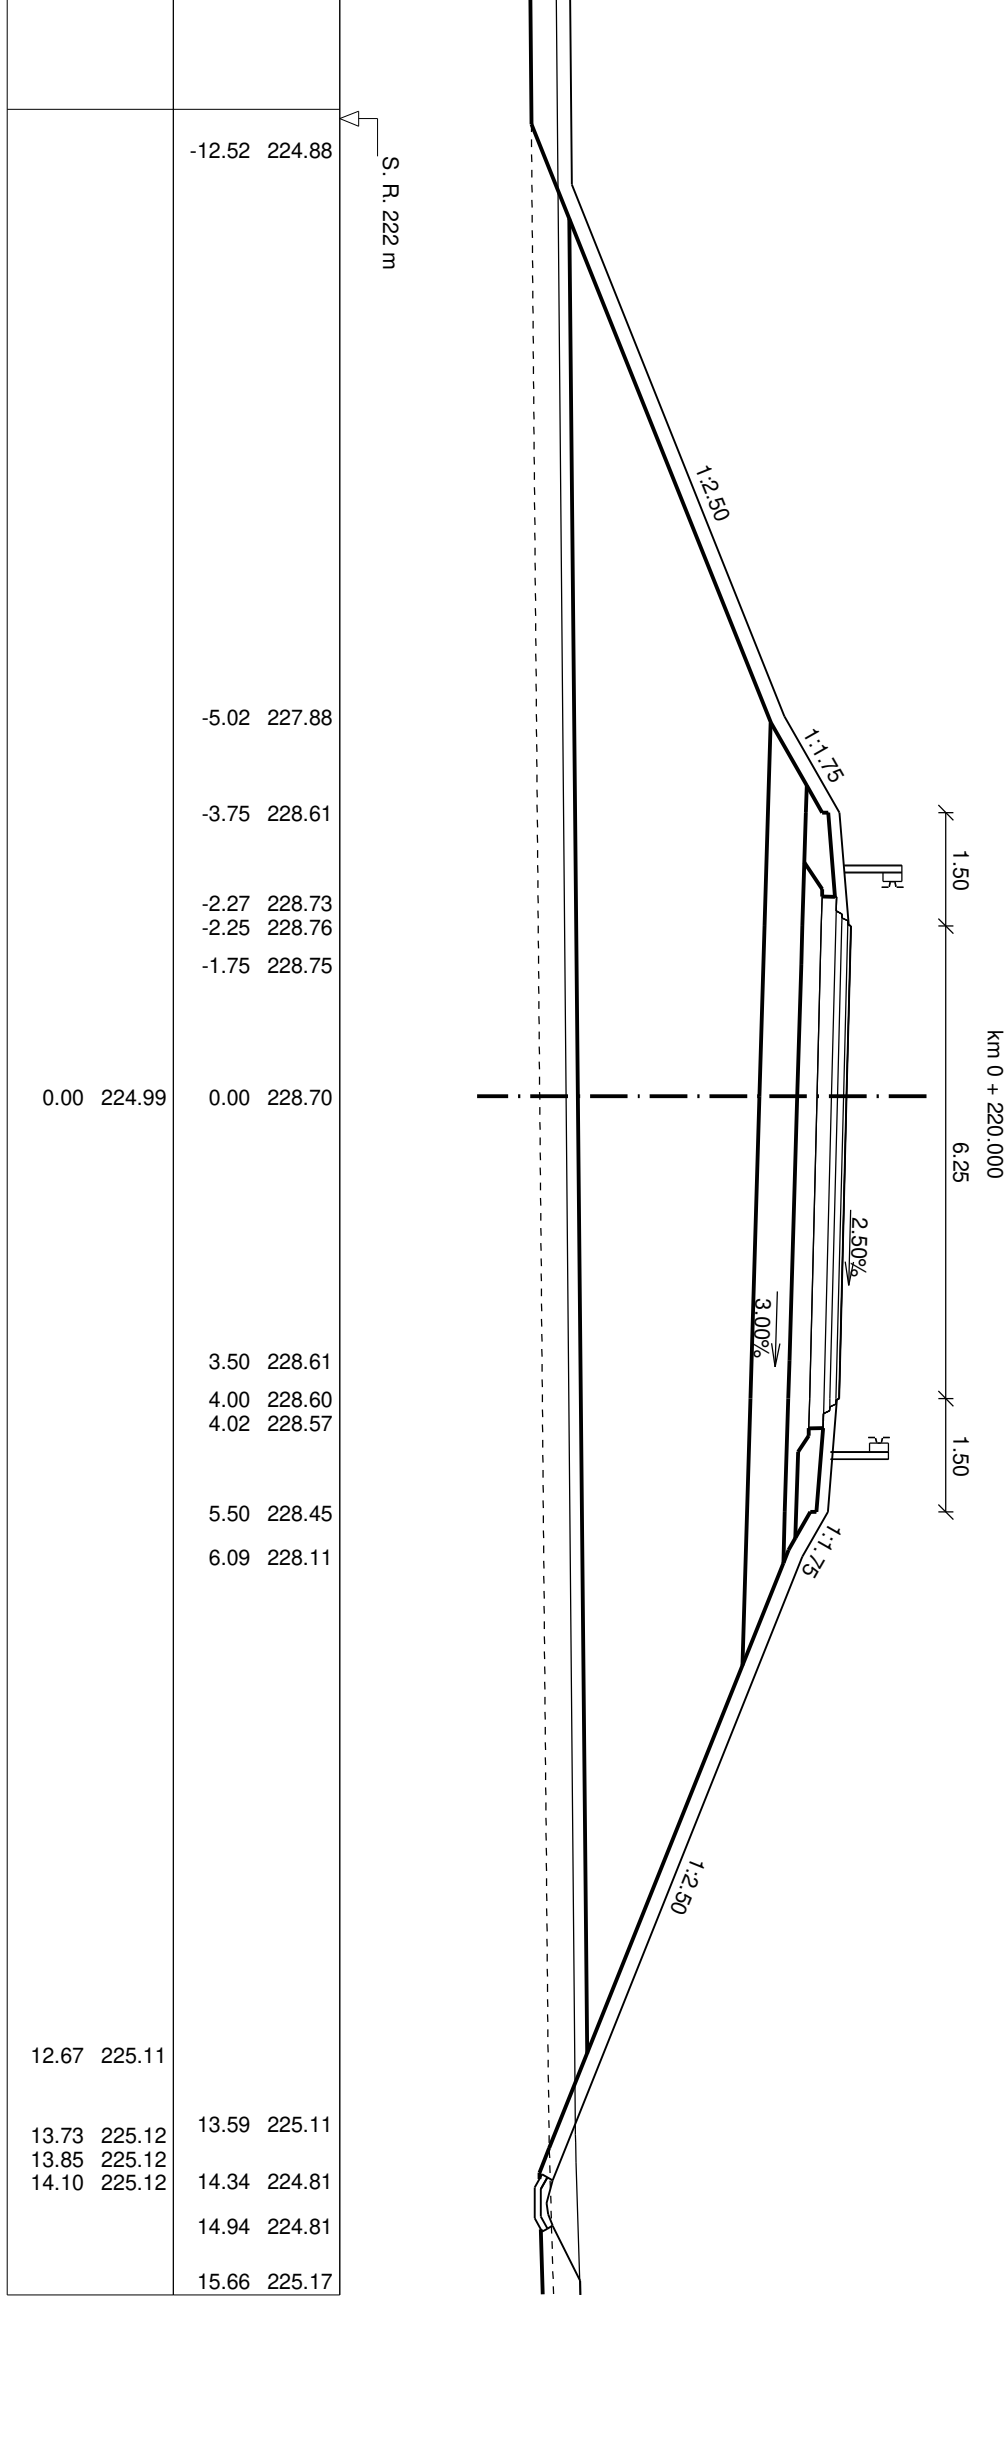

tém Bpv

12 MŮJ MARTINOV



Ředitelství silnic a dálnic s. r. o.
Čerčanská 2023/12, Krč, 140 00 Praha 4



Valbek, spol.

ORD

ING. T



č. priority	Podat formátu	Stupň	Datum	Zak. číslo
1	Měřitko	Plupně	02	21
2	Č. priority	Plupně	02	21

	Philon
--	--------

PRICNE REZY, VE