




SO 112 - MÚK MARTINOVICE
PŘÍČNÉ ŘEZY, VĚTEV č. 2, M 1 : 100

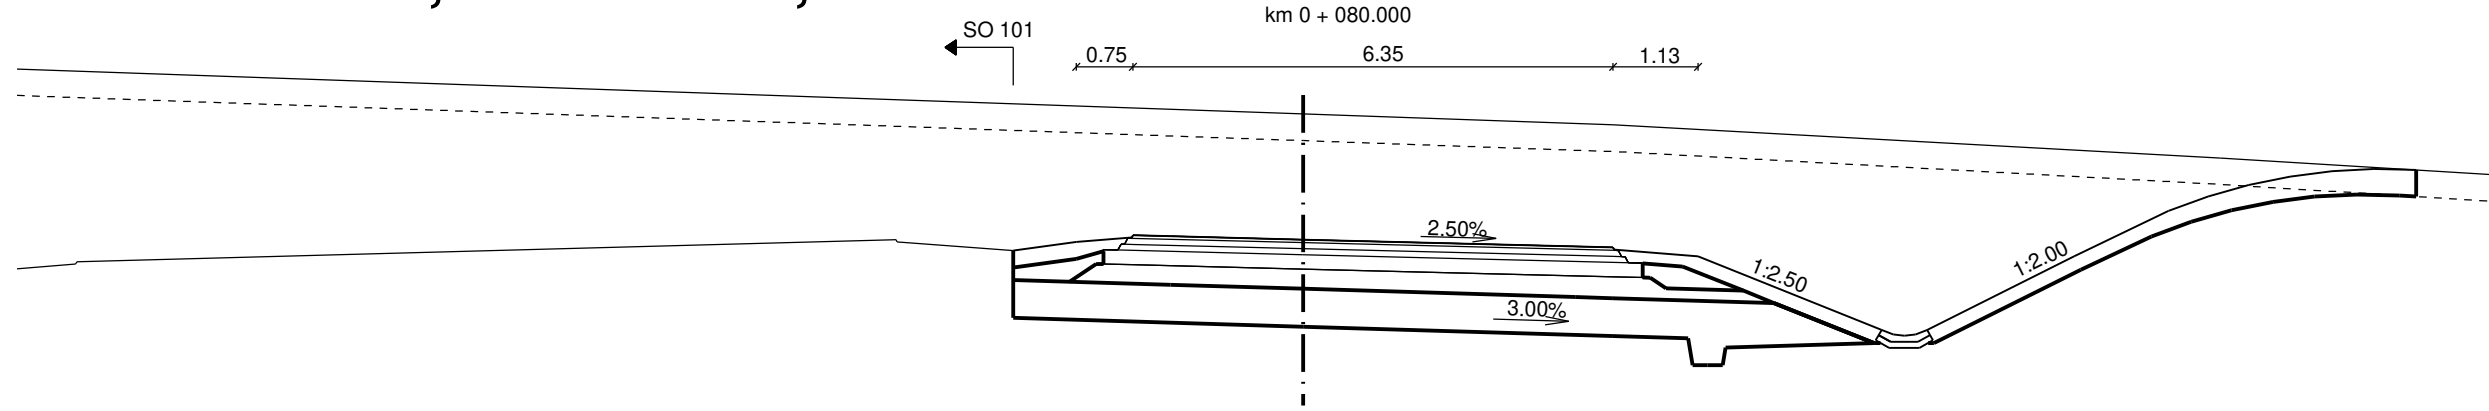


PROJEKTOVANÝ STAV	
ODSAZENÍ OD OSY	-3.00 226.01 -2.27 226.07 -2.25 226.10 -1.75 226.09 0.00 226.05 3.60 225.96 4.10 225.94 4.12 225.91 5.23 225.82 7.66 224.85 8.25 224.83 8.25 224.83 10.20 225.82 11.45 226.42 11.97 226.62 12.51 226.77 13.05 226.88 13.61 226.95 14.16 226.98 14.72 226.96
STÁVAJÍCÍ TERÉN	
ODSAZENÍ OD OSY	0.00 227.71 4.10 227.56 12.13 227.12

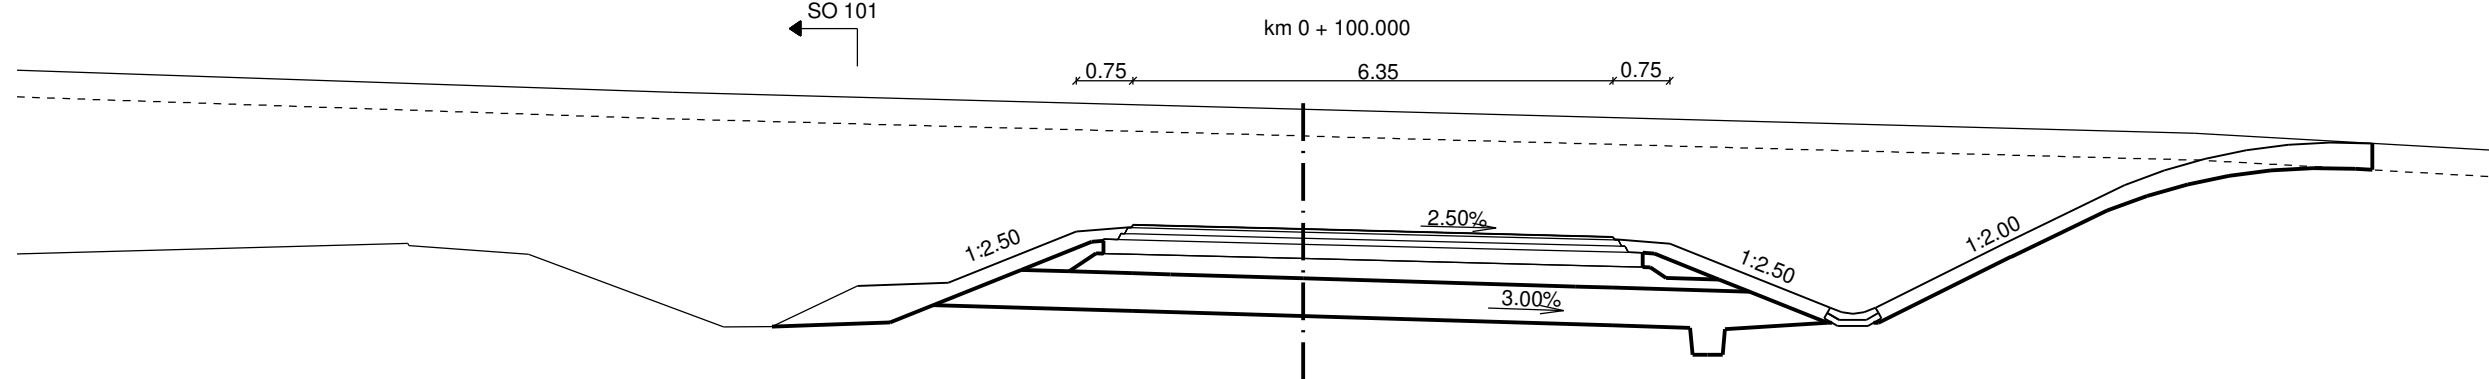


PROJEKTOVANÝ STAV	
ODSAZENÍ OD OSY	-10.48 227.87 -4.69 225.28 -3.00 225.96 -2.27 226.02 -2.25 226.05 -1.75 226.04 0.00 225.99 3.60 225.90 4.10 225.89 4.12 225.88 4.85 225.80 6.97 224.95 7.27 224.95 7.57 224.95 9.27 225.80 10.87 226.58 11.39 226.77 11.93 226.92 12.47 227.03 13.03 227.11 13.59 227.14 14.14 227.12
STÁVAJÍCÍ TERÉN	
ODSAZENÍ OD OSY	-8.34 227.80 0.00 227.58 11.79 227.26

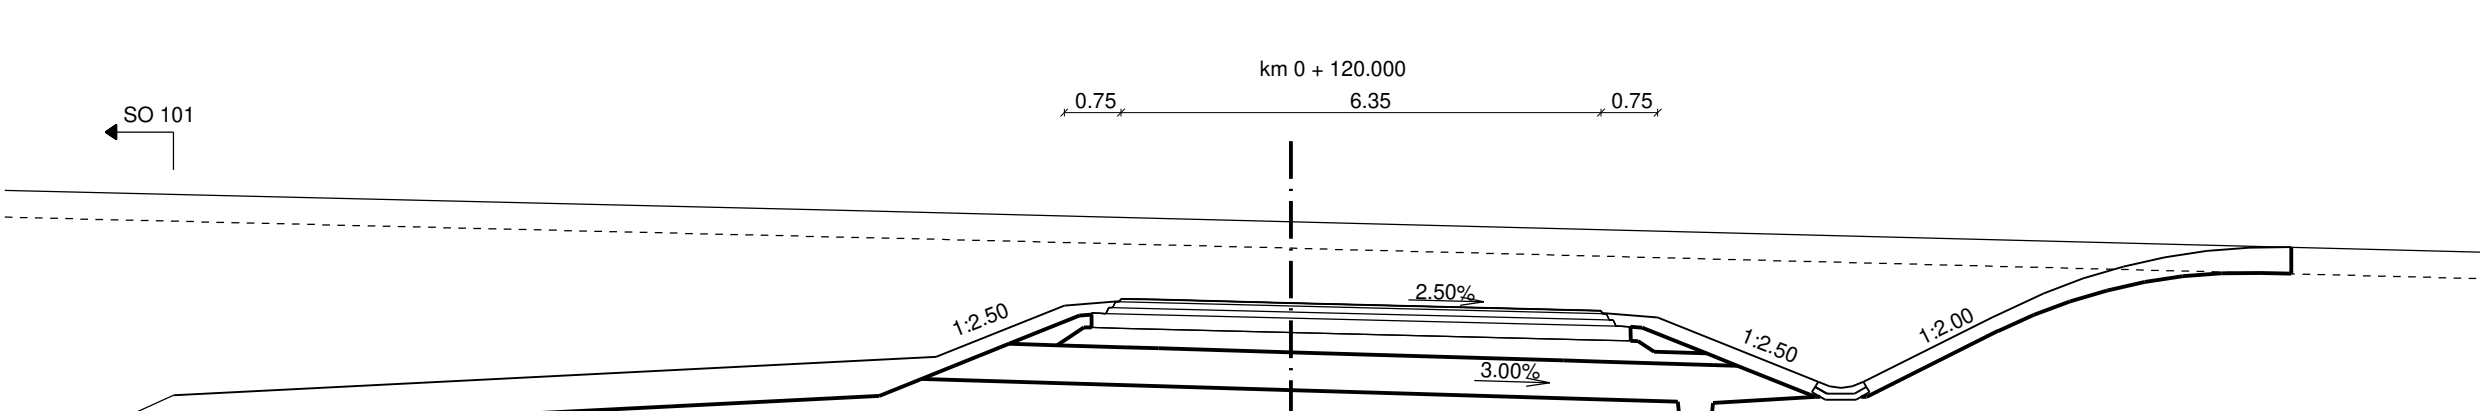


PROJEKTOVANÝ STAV	
ODSAZENÍ OD OSY	-4.69 225.50 -3.00 226.17 -2.27 226.23 -2.25 226.26 -1.75 226.25 0.00 226.21 3.60 226.12 4.10 226.10 4.12 226.07 4.85 226.01 6.97 225.17 7.27 225.17 7.57 225.17 9.27 226.01 9.95 226.33 10.48 226.53 11.01 226.69 11.56 226.81 12.11 226.89 12.67 226.94 13.23 226.94
STÁVAJÍCÍ TERÉN	
ODSAZENÍ OD OSY	-5.62 227.42 0.00 227.28

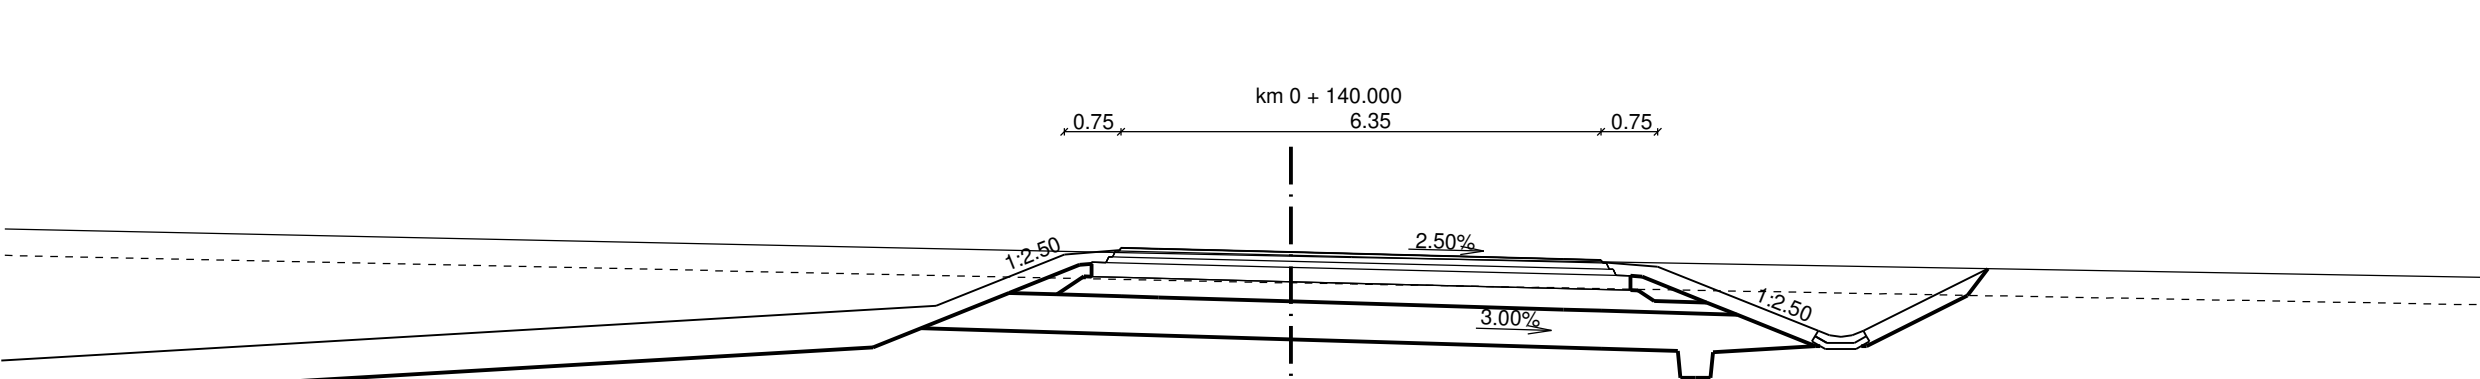

PROJEKTOVANÝ STAV	
ODSAZENÍ OD OSY	-4.69 225.98 -3.00 226.65 -2.27 226.71 -2.25 226.74 -1.75 226.73 0.00 226.69 3.60 226.60 4.10 226.58 4.12 226.55 4.85 226.50 6.97 225.65 7.27 225.65 7.57 225.65 9.22 226.47
STÁVAJÍCÍ TERÉN	
ODSAZENÍ OD OSY	0.00 226.63 0.80 226.62

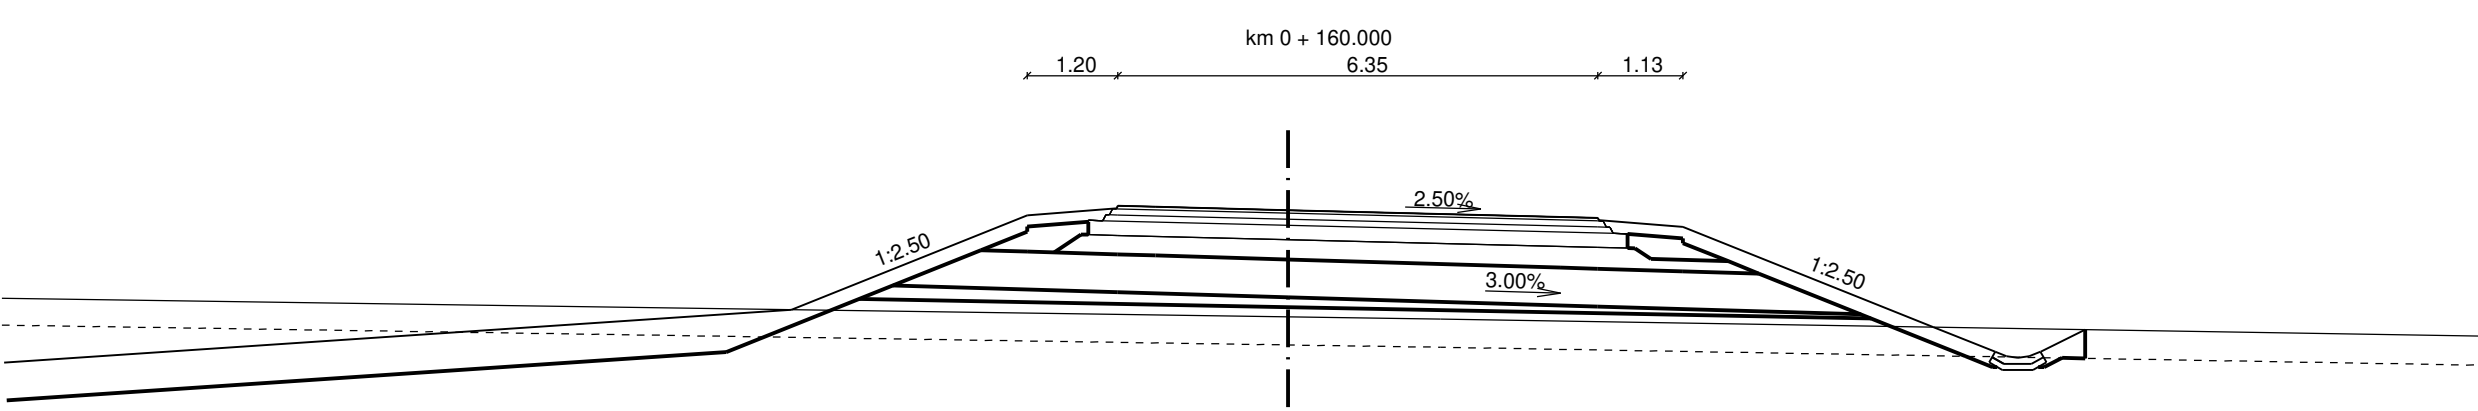

PROJEKTOVANÝ STAV	
ODSAZENÍ OD OSY	-6.57 226.12 -3.45 227.37 -2.27 227.46 -2.25 227.49 -1.75 227.48 0.00 227.43 3.60 227.34 4.10 227.33 4.12 227.30 5.23 227.21 8.53 225.89 9.35 225.56 9.95 225.56 10.55 225.86
STÁVAJÍCÍ TERÉN	
ODSAZENÍ OD OSY	0.00 226.02 2.02 226.00

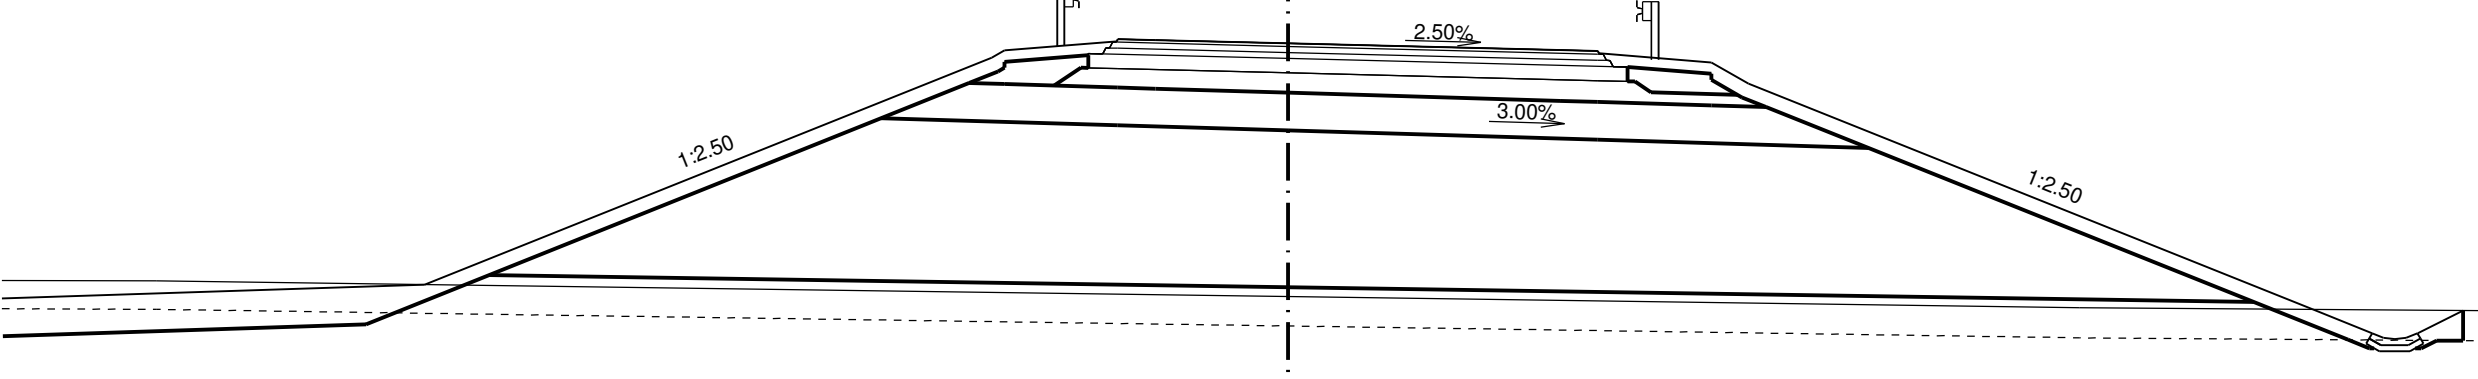

PROJEKTOVANÝ STAV	
ODSAZENÍ OD OSY	-11.42 225.26 -9.92 226.26 -3.75 226.36 -2.27 226.47 -2.25 226.50 -1.75 226.49 0.00 226.45 3.60 226.36 4.10 226.35 4.12 226.32 5.60 226.20 6.09 227.92 13.55 224.93 14.34 224.62 14.94 224.62 15.54 224.92
STÁVAJÍCÍ TERÉN	
ODSAZENÍ OD OSY	0.00 225.10 10.47 224.95

Výškový systém Bvp

SO 112 MÚK MARTINOVICE



**ŘEDITELSTVÍ
SILNIC
A DÁLNIC**

Ředitelství silnic a dálnic s. p.
Čerčanská 2023/12, Krč, 140 00 Praha 4



Valbek

Valbek, spol. s r.o.
Vaňurova 505/17
460 07 Liberec 3

HIP:
ING. T. KLIMENT



Valbek

I/16 MLADÁ BOLESLAV - MARTINOVICE

Příloha
PŘÍČNÉ ŘEZY, VĚTEV č. 2

Zak. číslo
21-LI13-001

Datum
02/2025

Stupeň
PDPS

Počet formátů
6xA4

Měřítko
1 : 100

Č. přílohy
Paré

5.2