SO 112 - MÚK MARTINOVICE
PŘÍČNÉ ŘEZY, VĚTEV č. 3, M 1 : 100

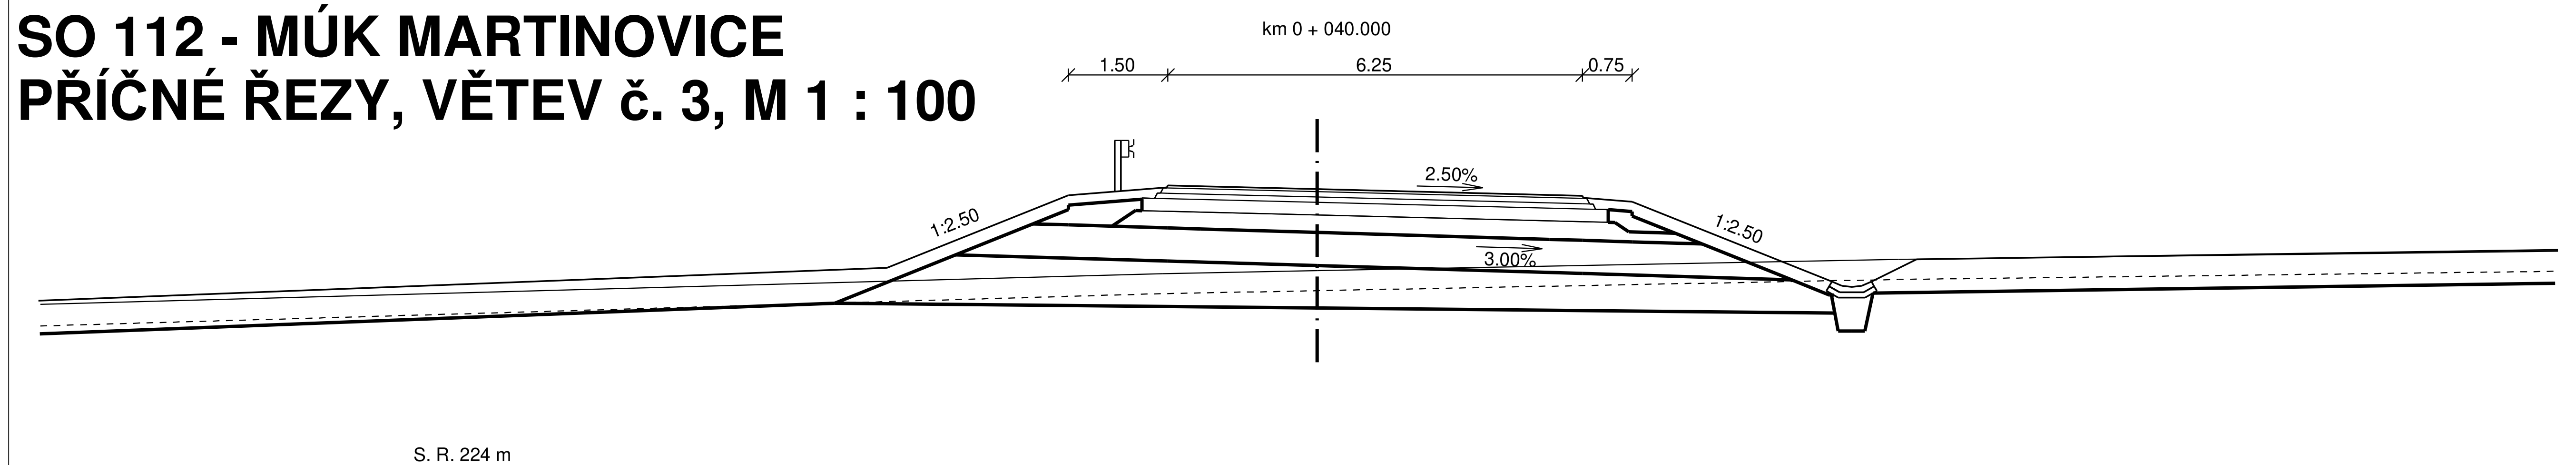
km 0 + 040.000
1.50
6.25
0.75
2.50%
3.00%
1:2.50
1:2.50
S. R. 224 m

ODSAZENÍ OD OSY	PROJEKTOVANÝ STAV	ODSAZENÍ OD OSY	STÁVAJÍCÍ TERÉN
-7.02	227.26		
-3.75	228.57		
		-2.34	227.39
-2.27	228.69		
-2.25	228.72		
-1.75	228.71		
0.00	228.67	0.00	227.44
3.50	228.58		
4.00	228.57		
4.02	228.54		
4.75	228.48		
7.01	227.57		
7.76	227.27		
8.36	227.27		
		8.77	227.61
9.04	227.61		

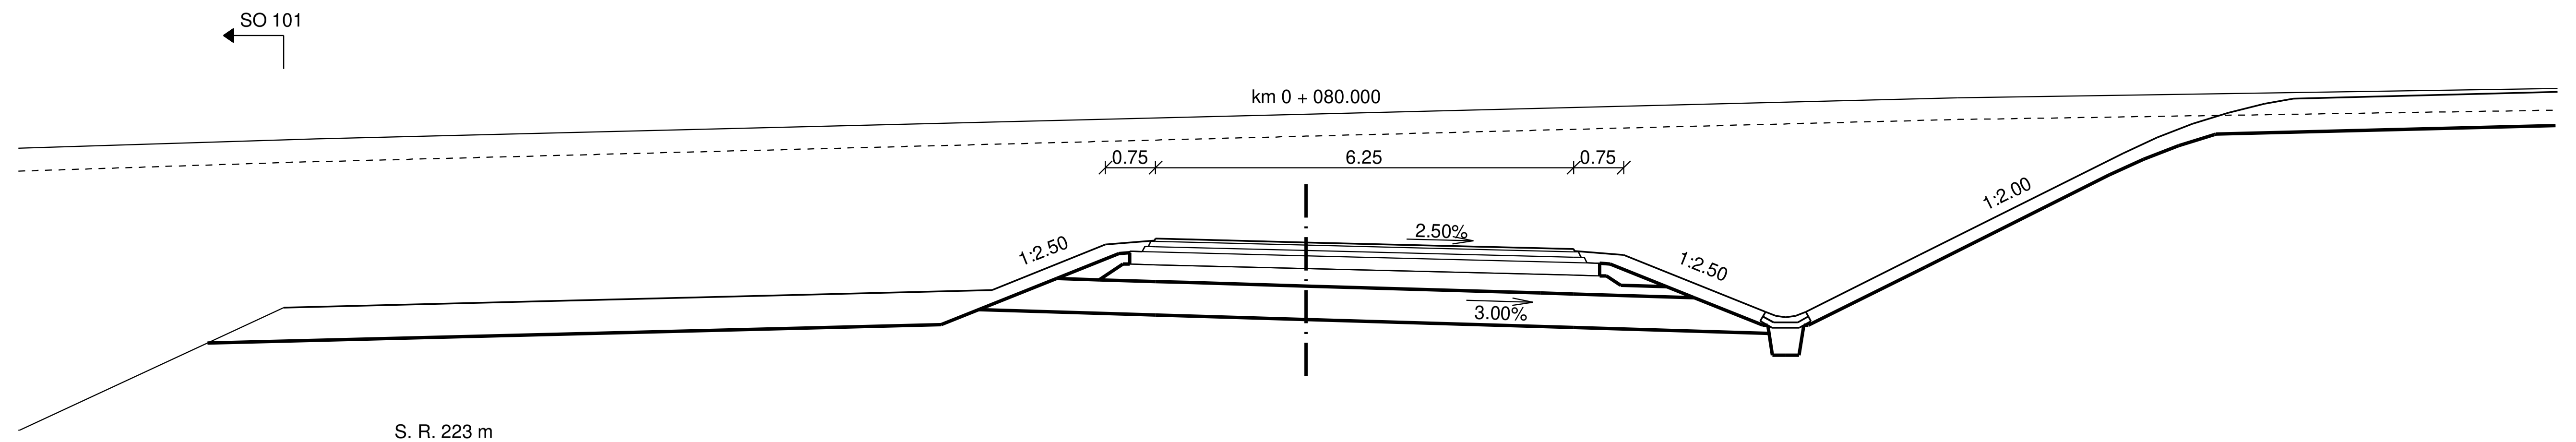
SO 101
km 0 + 080.000
0.75
6.25
0.75
1:2.50
2.50%
3.00%
1:2.50
1:2.00
S. R. 223 m

ODSAZENÍ OD OSY	PROJEKTOVANÝ STAV	ODSAZENÍ OD OSY	STÁVAJÍCÍ TERÉN
-4.69	225.78		
-3.00	226.46		
-2.27	226.52		
-2.25	226.55		
-1.75	226.54		
0.00	226.49	0.00	228.41
3.50	226.41		
4.00	226.39		
4.02	226.36		
4.75	226.31		
6.87	225.46		
7.17	225.46		
7.47	225.46		
9.17	226.31		
		9.75	228.66
12.21	227.83		
12.72	228.06		
13.25	228.27		
13.78	228.43		
14.33	228.57		
14.88	228.66		

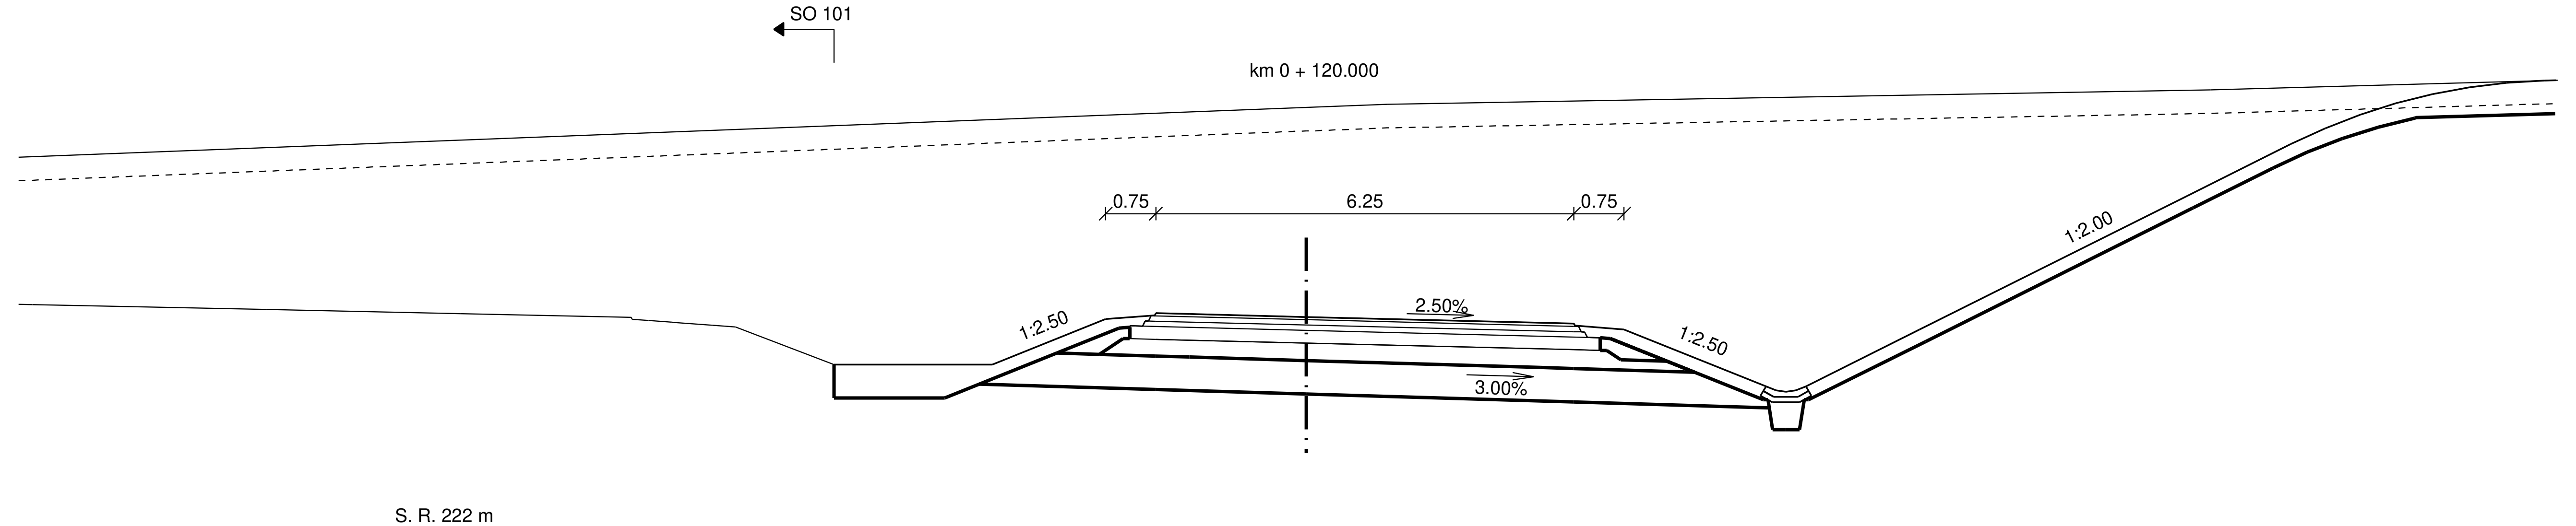
SO 101
km 0 + 120.000
0.75
6.25
0.75
1:2.50
2.50%
3.00%
1:2.50
1:2.00
S. R. 222 m

ODSAZENÍ OD OSY	PROJEKTOVANÝ STAV	ODSAZENÍ OD OSY	STÁVAJÍCÍ TERÉN
-7.06	224.93		
-4.69	224.93		
-3.00	225.61		
-2.27	225.66		
-2.25	225.69		
-1.75	225.68		
0.00	225.64	0.00	228.77
		1.21	228.82
3.50	225.55		
4.00	225.54		
4.02	225.51		
4.75	225.45		
6.87	224.60		
7.17	224.60		
7.47	224.60		
9.17	225.45		
13.17	227.45		
		13.52	229.04
14.72	228.23		
15.23	228.46		
15.76	228.67		
16.29	228.84		
16.84	228.97		
17.39	229.08		
17.95	229.14		
18.51	229.18		

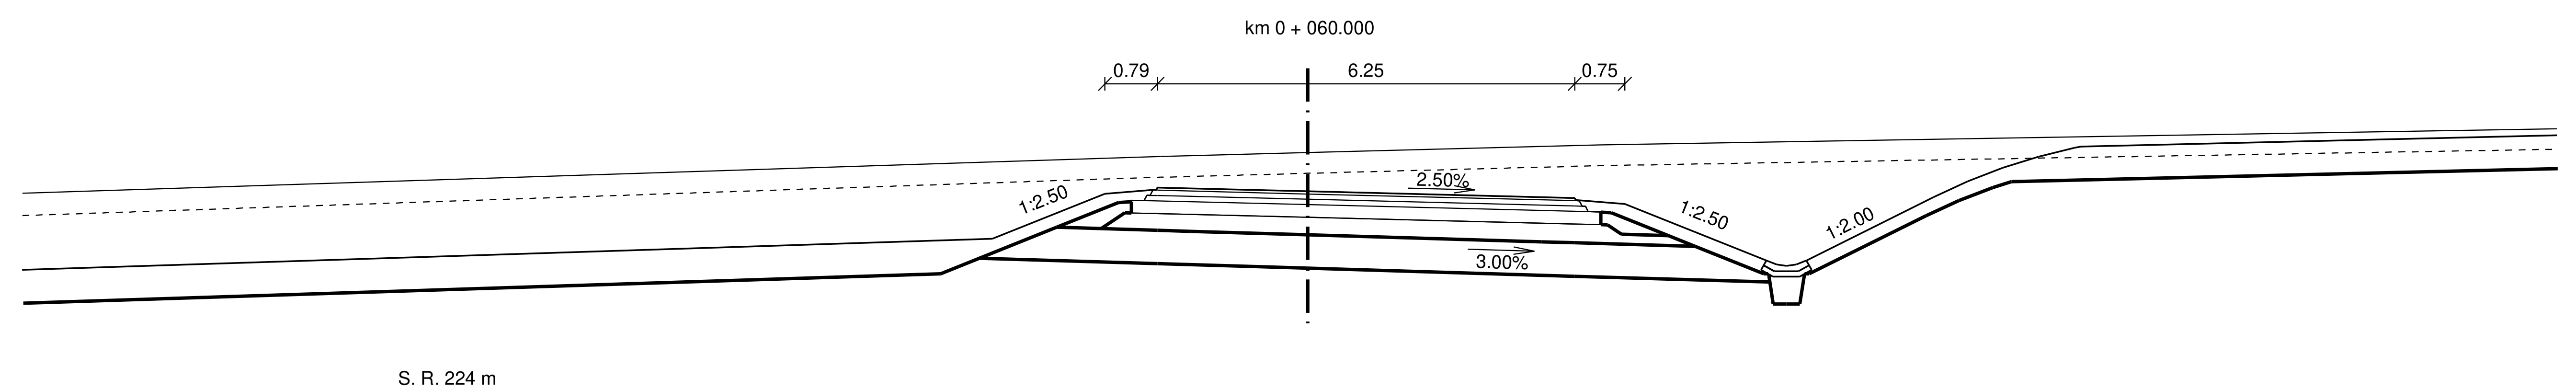
km 0 + 060.000
0.79
6.25
0.75
1:2.50
2.50%
3.00%
1:2.50
1:2.00
S. R. 224 m

ODSAZENÍ OD OSY	PROJEKTOVANÝ STAV	ODSAZENÍ OD OSY	STÁVAJÍCÍ TERÉN
-4.72	226.76		
-3.04	227.43		
-2.27	227.49		
		-2.21	227.99
-2.25	227.52		
-1.75	227.51		
0.00	227.47	0.00	228.05
3.50	227.38		
4.00	227.37		
4.02	227.34		
		4.38	228.16
4.75	227.28		
6.87	226.43		
7.17	226.43		
7.47	226.43		
9.17	227.28		
9.37	227.38		
9.88	227.62		
10.41	227.82		
10.94	227.99		
11.49	228.12		

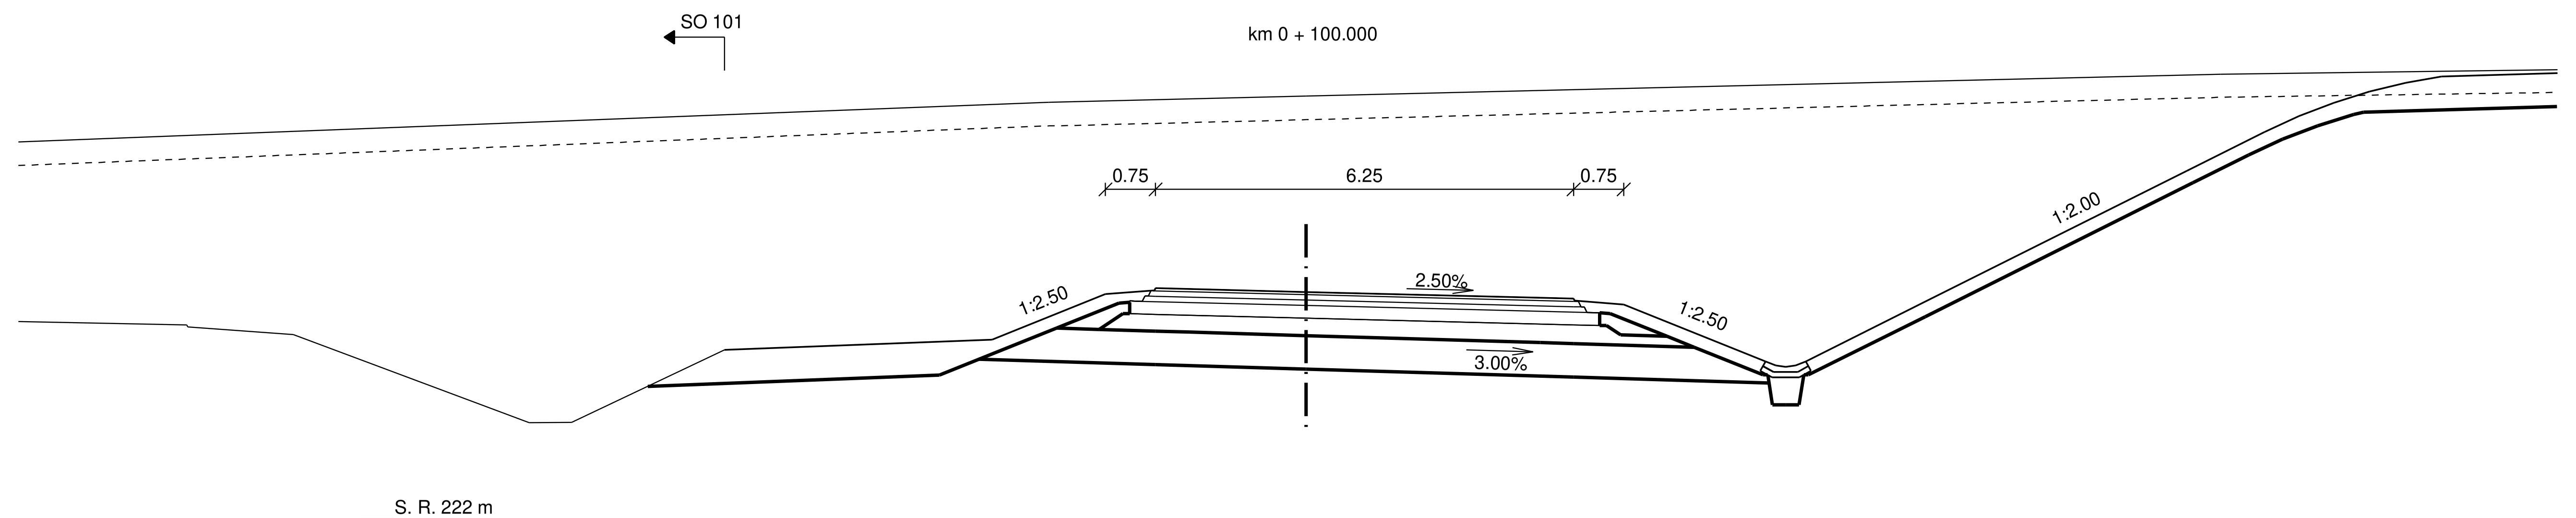
SO 101
km 0 + 100.000
0.75
6.25
0.75
1:2.50
2.50%
3.00%
1:2.50
1:2.00
S. R. 222 m

ODSAZENÍ OD OSY	PROJEKTOVANÝ STAV	ODSAZENÍ OD OSY	STÁVAJÍCÍ TERÉN
-4.69	225.17		
		-3.85	228.72
-3.00	225.85		
-2.27	225.91		
-2.25	225.94		
-1.75	225.93		
0.00	225.88	0.00	228.81
3.50	225.80		
4.00	225.78		
4.02	225.75		
4.75	225.70		
6.87	224.85		
7.17	224.85		
7.47	224.85		
9.17	225.70		
13.17	227.70		
		13.67	229.14
14.33	228.28		
14.84	228.51		
15.36	228.71		
15.90	228.88		
16.45	229.01		
17.00	229.11		

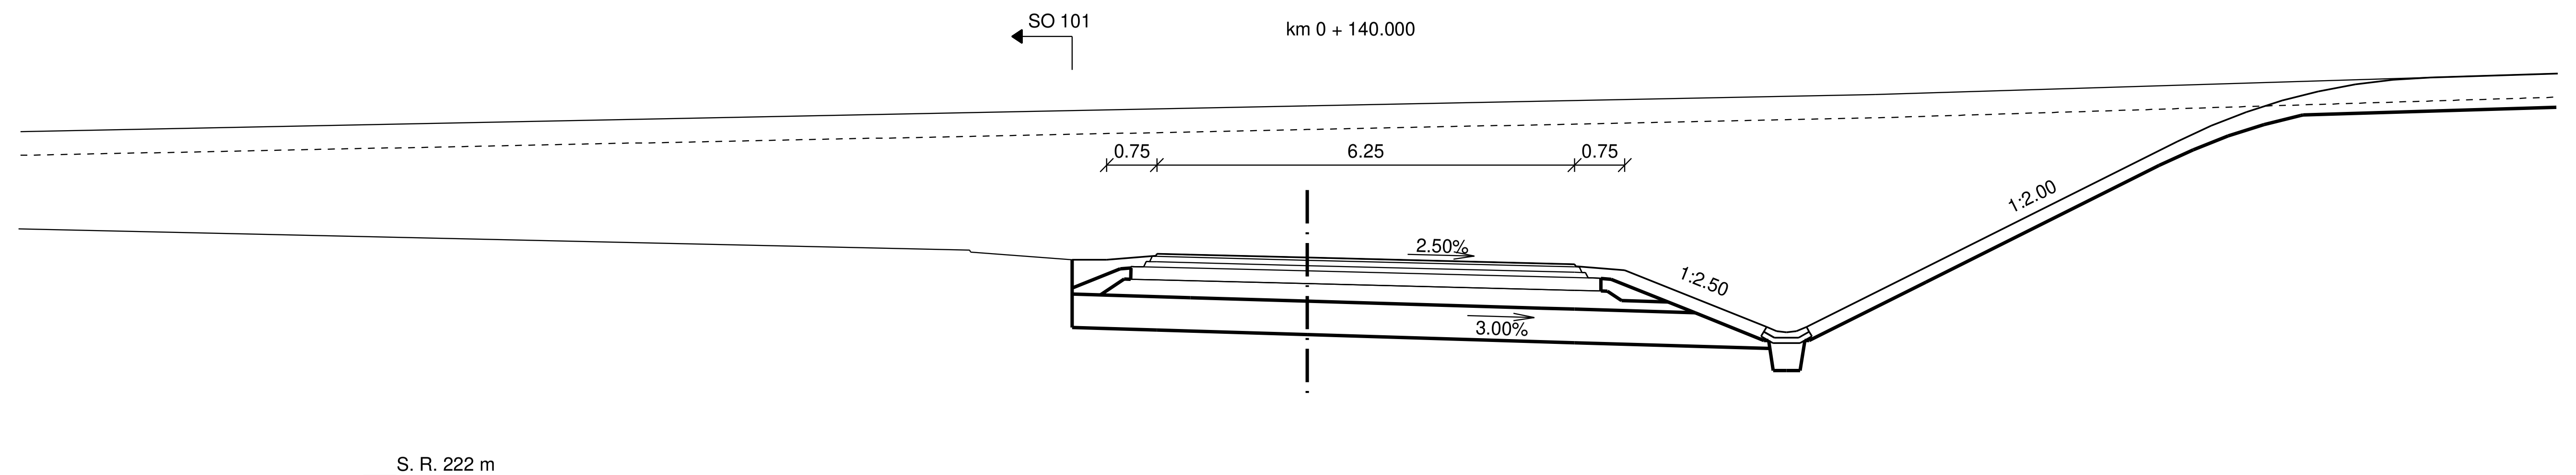
SO 101
km 0 + 140.000
0.75
6.25
0.75
1:2.50
2.50%
3.00%
1:2.50
1:2.00
S. R. 222 m

ODSAZENÍ OD OSY	PROJEKTOVANÝ STAV	ODSAZENÍ OD OSY	STÁVAJÍCÍ TERÉN
-3.00	225.72		
-2.27	225.78		
-2.25	225.81		
-1.75	225.80		
0.00	225.76	0.00	228.02
3.50	225.67		
4.00	225.66		
4.02	225.63		
4.75	225.57		
6.87	224.72		
7.17	224.72		
7.47	224.72		
		8.50	228.19
9.17	225.57		
13.01	227.49		
13.52	227.73		
14.05	227.93		
14.58	228.10		
15.13	228.24		
15.68	228.34		
16.24	228.41		
16.80	228.44		

Výškový systém Bvp

SO 112 MÚK MARTINOVICE

Objednatel:
ŘEDITELSTVÍ SILNIC A DÁLNIC
Ředitelství silnic a dálnic s. p.
Čerčanská 2023/12, Krč, 140 00 Praha 4

Zhotovitel:
Valbek
Valbek, spol. s r.o.
Vaňurova 505/17
460 07 Liberec 3

HIP:
ING. T. KLIMENT

Vypracoval	M. KOŘÍNEK	**Zak. číslo**	21-LI13-001
Zodp. projektant	ING. T. KLIMENT	**Datum**	02/2025
Tech. kontrola	ING. M. HANŽL	**Stupeň**	PDPS
Akce	I/16 MLADÁ BOLESLAV - MARTINOVICE	**Počet formátů**	7xA4
		Měřítko	1 :100
Příloha	PŘÍČNÉ ŘEZY, VĚTEV č. 3	**Č. přílohy**	5.3
		Paré	

Valbek
Zhotovitel:
Valbek, spol. s r.o.
Vaňurova 505/17
460 07 Liberec 3