




SO 112 - MÚK MARTINOVCE
PŘÍČNÉ ŘEZY, VĚTEV č. 4, M 1 : 100

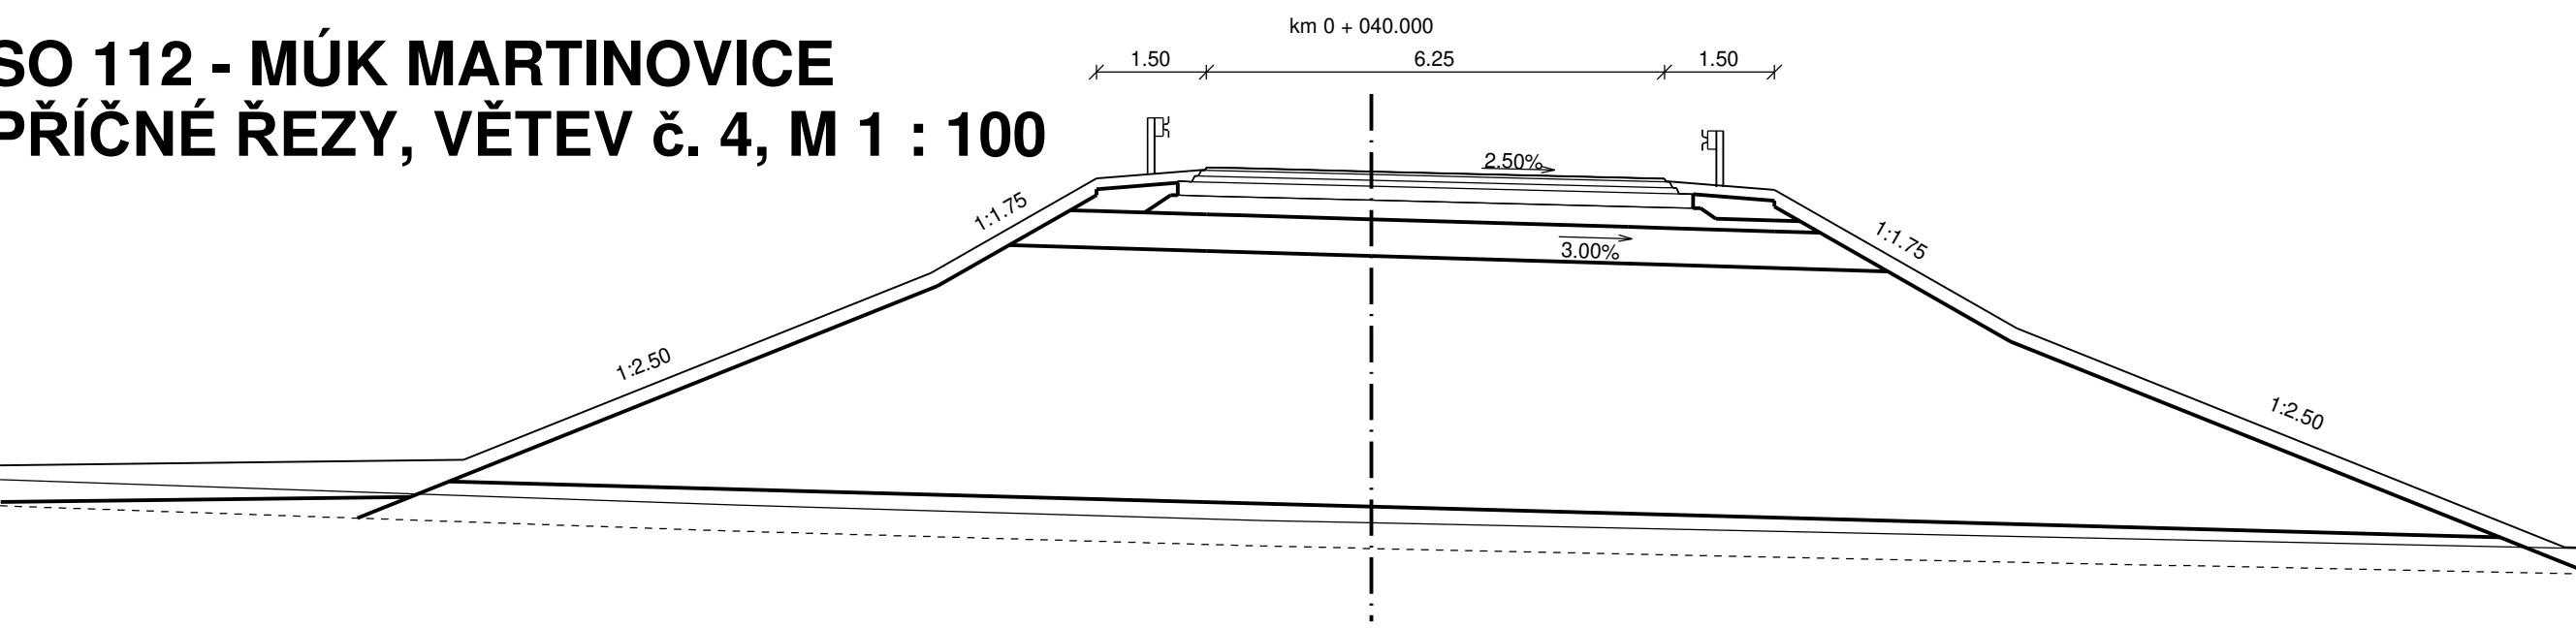


S. R. 221 m	
PROJEKTOVANÝ STAV	-12.39 224.26
ODSAZENÍ OD OSY	
	-6.01 226.81
	-3.75 228.10
	-2.27 228.22
	-2.25 228.25
	-1.75 228.24
	-1.48 223.43
	0.00 228.19
	3.59 228.10
	4.02 228.06
	4.02 228.06
	5.50 227.94
	8.81 226.05
	16.28 223.07

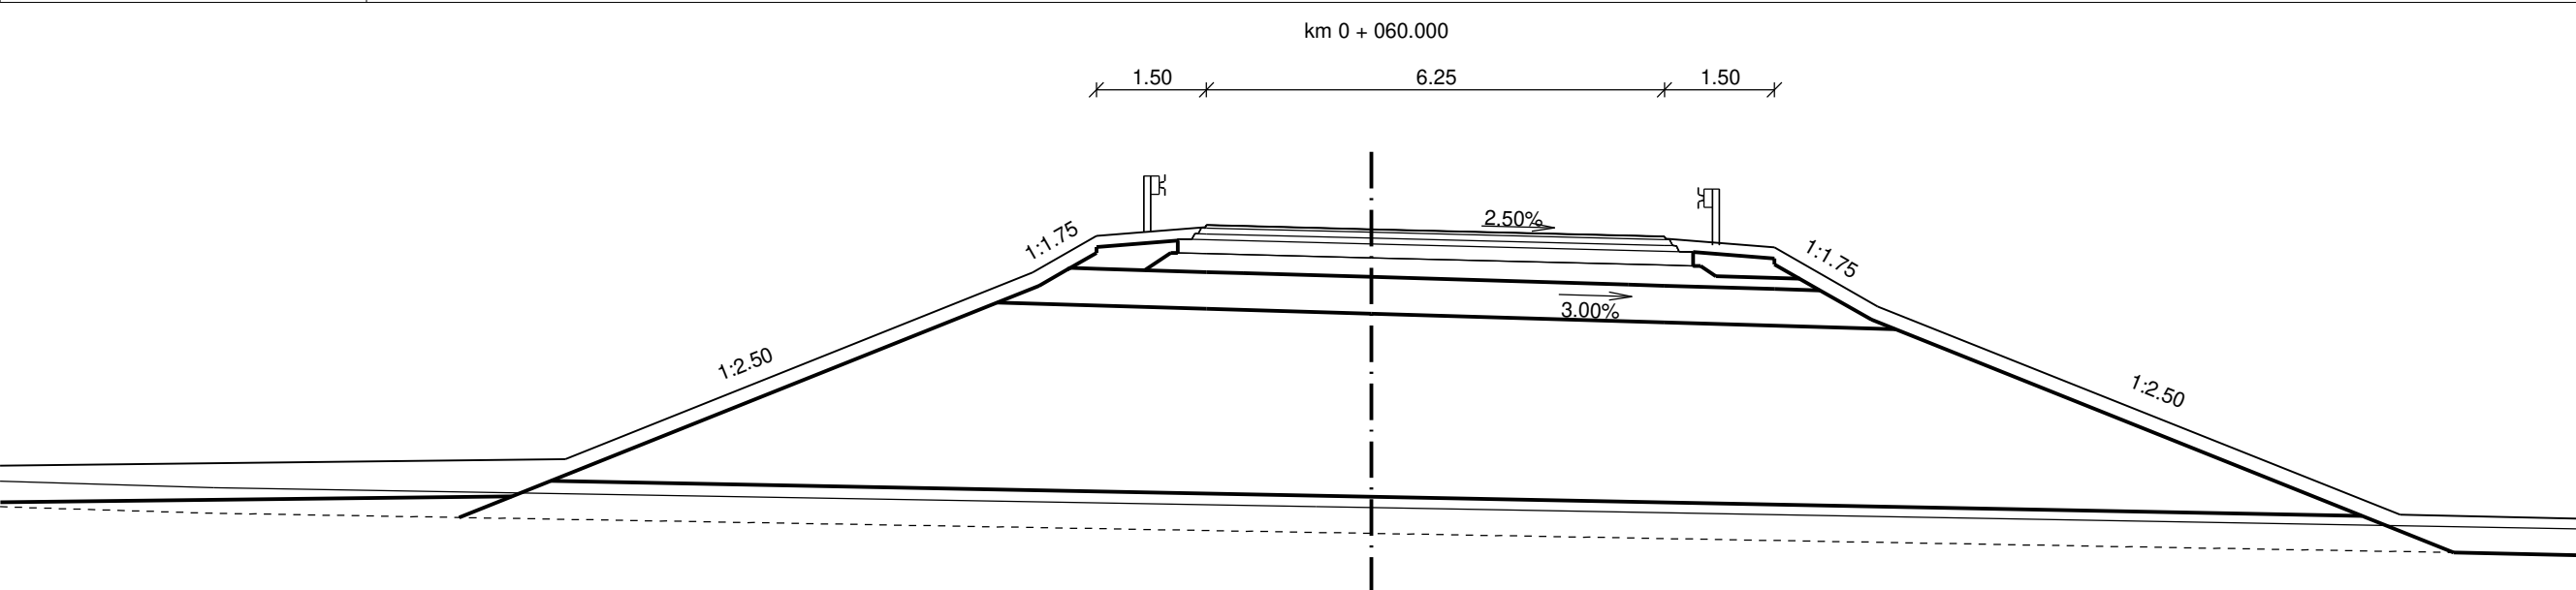



S. R. 220 m	
PROJEKTOVANÝ STAV	-10.99 223.85
ODSAZENÍ OD OSY	-4.62 226.40
	-3.75 226.90
	-2.27 227.02
	-2.25 227.05
	-1.75 227.04
	0.00 226.99
	3.50 226.90
	4.02 226.89
	4.02 226.89
	5.50 226.74
	6.91 225.94
	14.04 223.10
STÁVAJÍCÍ TERÉN	
ODSAZENÍ OD OSY	-0.75 223.21
	0.00 223.19

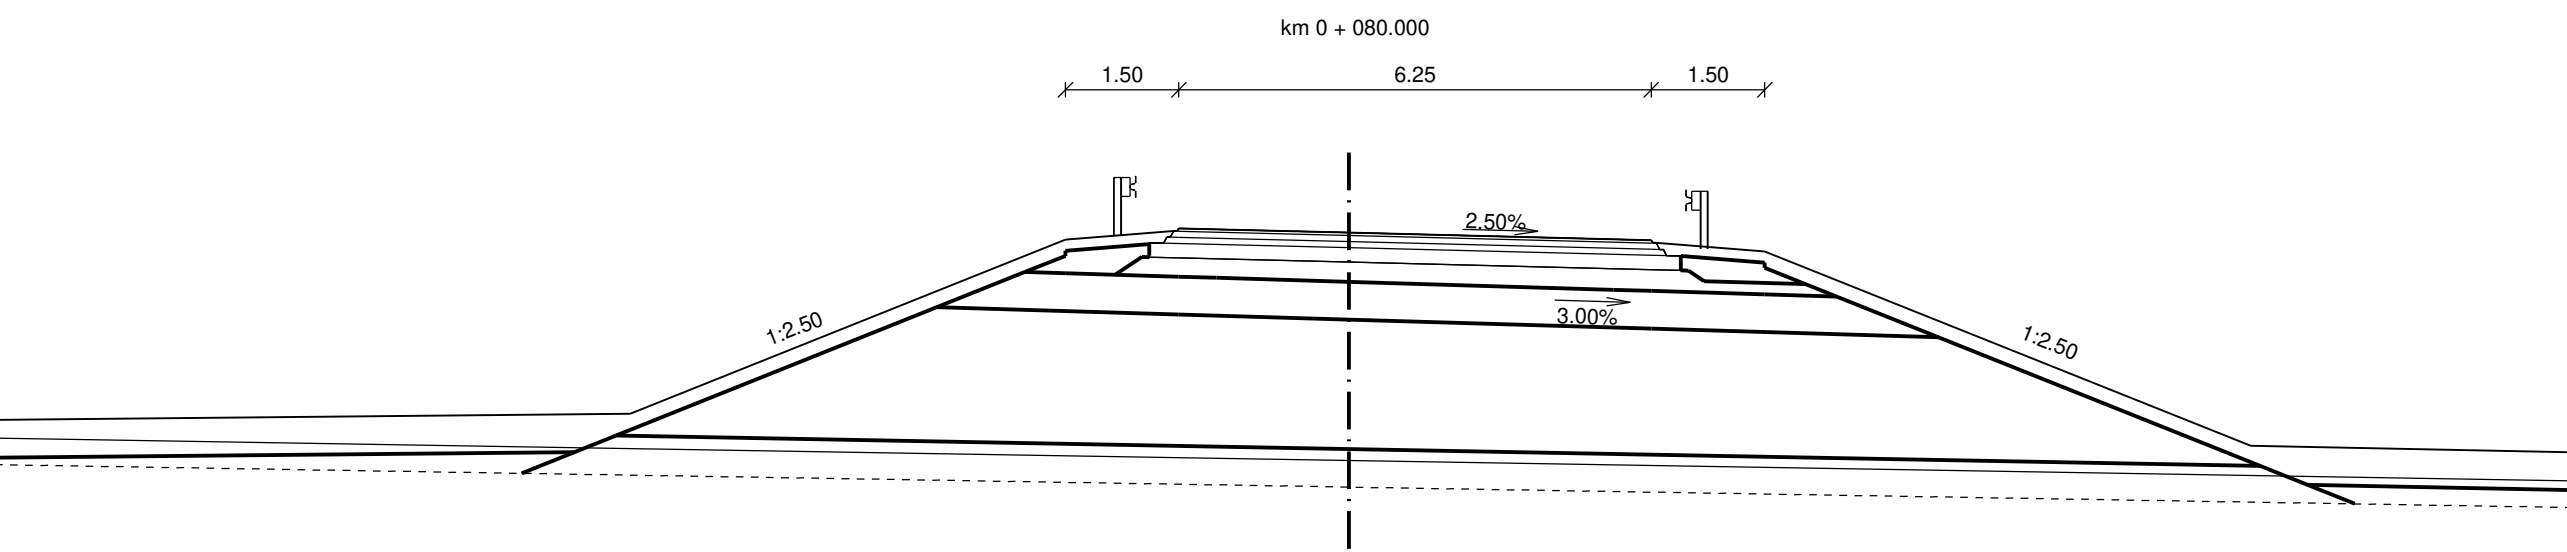


S. R. 220 m	
PROJEKTOVANÝ STAV	-3.50 223.48
SAZENÍ OD OSY	-3.75 225.78
	-3.25 225.90
	-3.45 225.80
	-1.75 223.92
	0.00 225.87
	3.50 225.79
	4.00 225.77
	4.02 225.74
	5.50 225.63
VAJÍCÍ TERÉN	7.42 222.74
SAZENÍ OD OSY	11.93 223.05

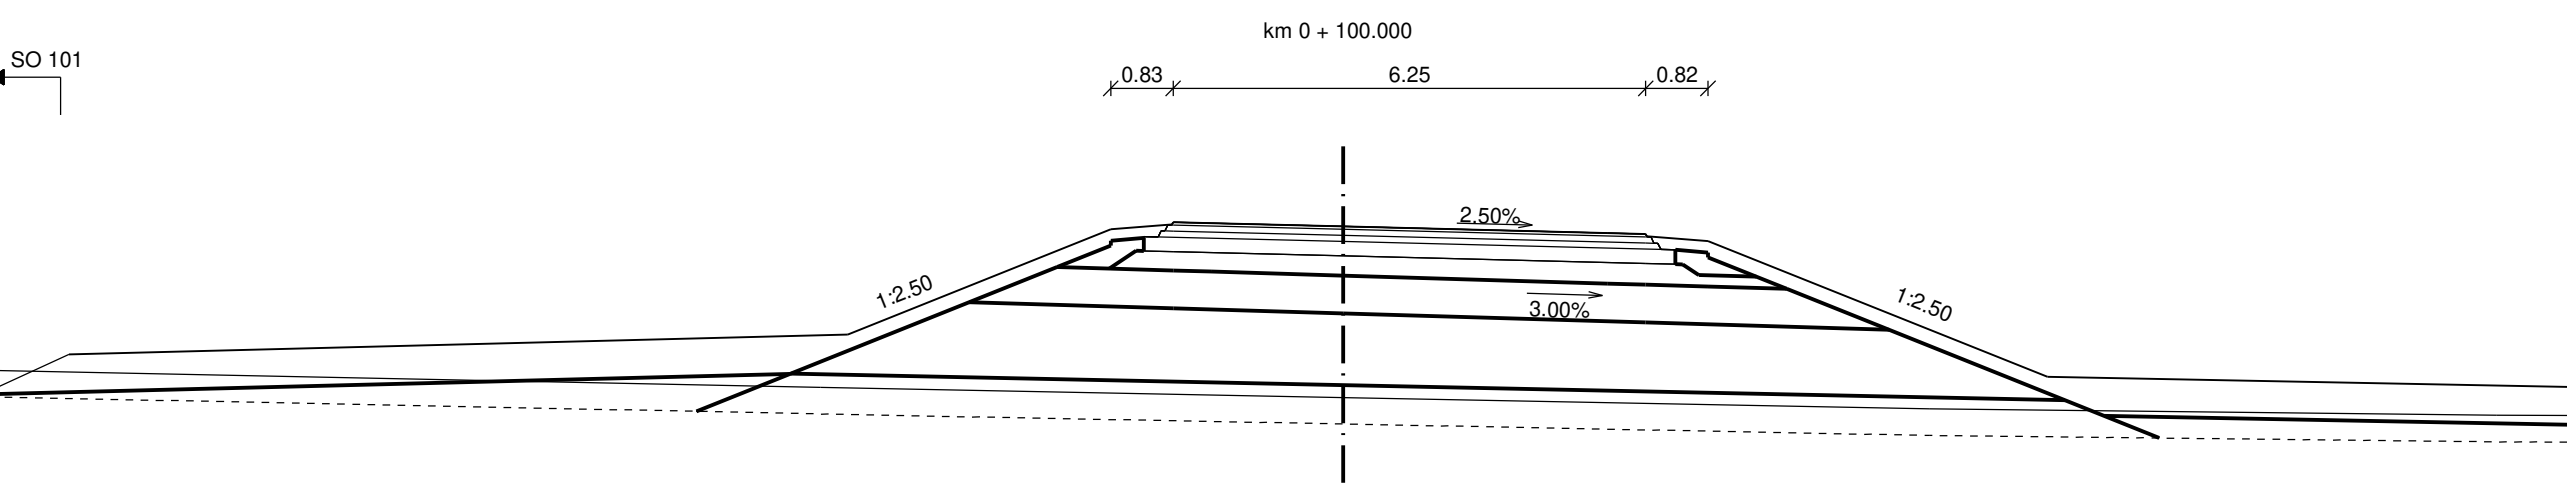

S. R. 220 m	
JEKTOVANÝ STAV	
AZENÍ OD OSY	-8,24 223,30 3,08 224,92 2,97 224,96 2,25 225,01 -1,75 225,00 0,00 224,96 3,50 224,87 4,00 224,86 4,02 224,83 4,83 224,76 9,32 222,96
VAJÍCÍ TERÉN	
AZENÍ OD OSY	-6,92 222,83 0,00 222,69 7,75 222,54 15,26 222,46

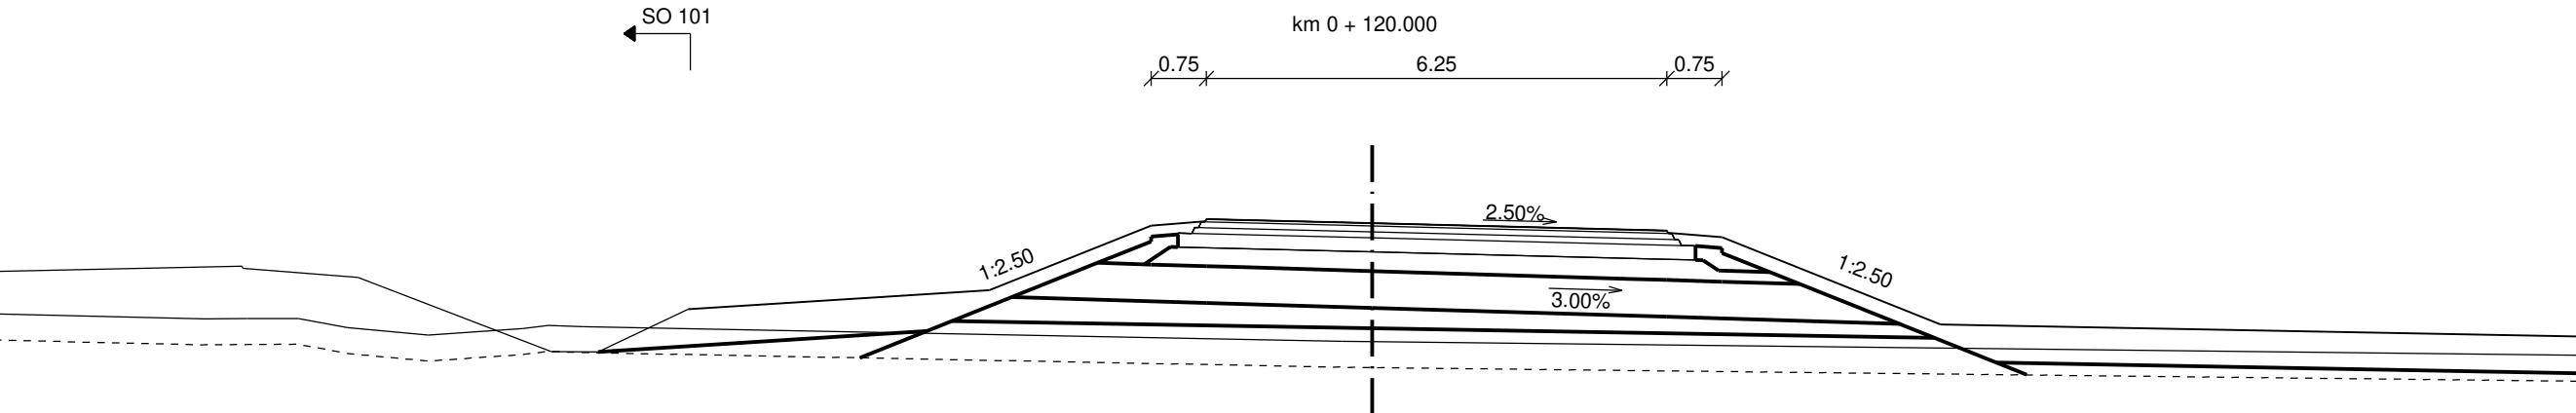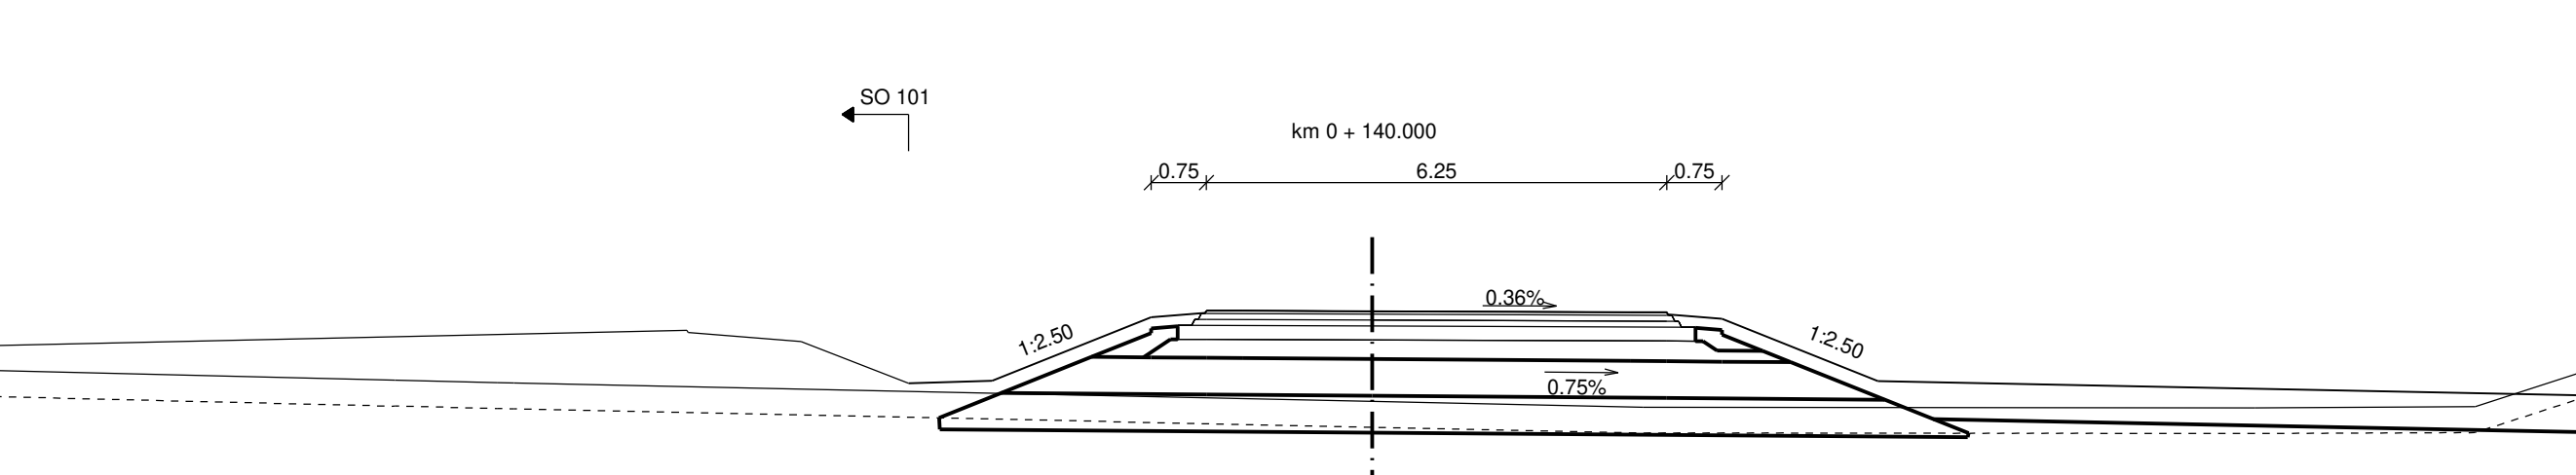[illegible]

S. R. 220 m	
PROJEKTOVANÝ STAV	
ODSAZENÍ OD OSY	-5.16 222.76 3.00 223.64 -2.97 223.70 -2.25 223.73 -1.75 223.73 0.00 223.72
STÁVAJÍCÍ TERÉN	
ODSAZENÍ OD OSY	13.26 222.78 1.88 222.75 1.65 222.75 3.88 222.42 1.98 222.41 4.98 222.42

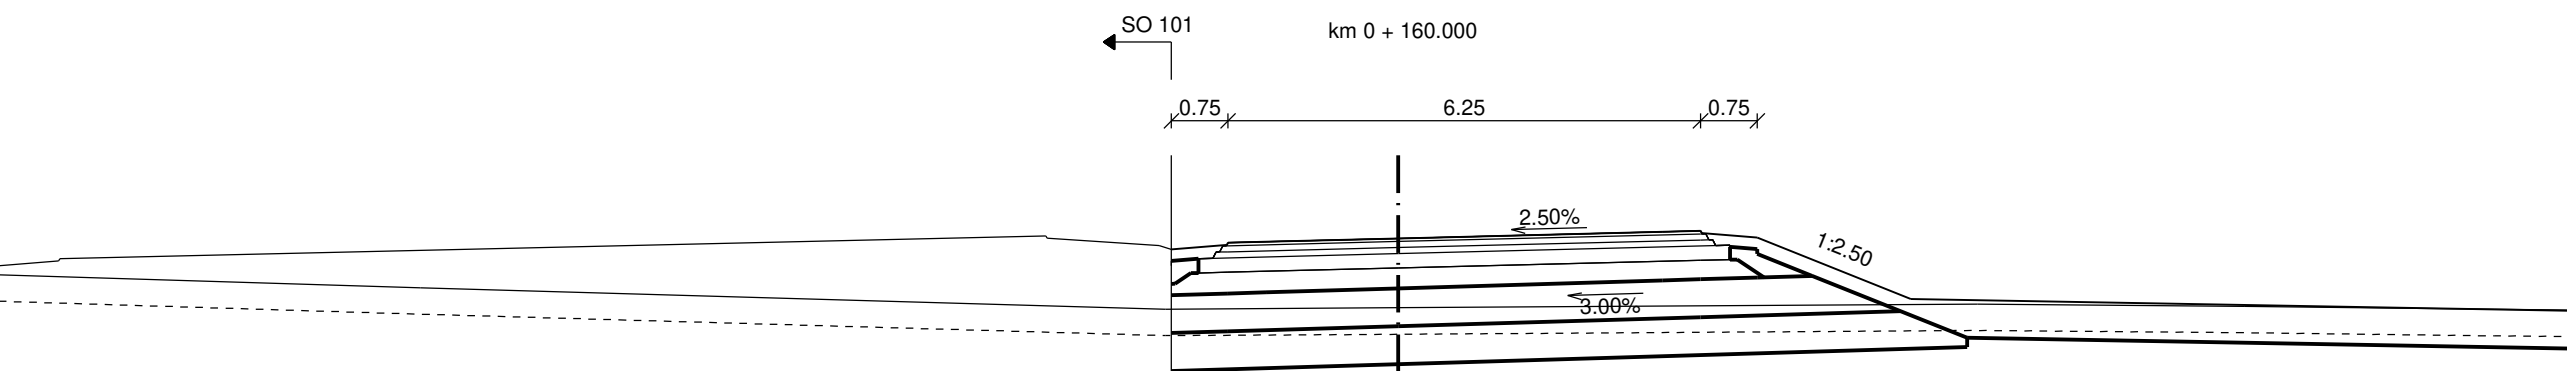

	S. R. 220 m	
PROJEKTOVANÝ STAV		
ODSAZENÍ OD OSY		-3,00 223,26 -2,27 223,32 -2,25 223,35 -1,75 223,36 0,00 223,40 3,50 223,49 4,00 223,50 4,02 223,47 4,75 223,41 6,78 222,60
STÁVAJÍCÍ TERÉN	-15,93 222,75	
ODSAZENÍ OD OSY		-3,08 222,47 0,00 222,49 7,67 222,54 11,20 222,51 14,50 222,47

Výškový systém B

SO 112 MÚK MARTINOVCE

Objedn



Ředitelství silnic a dálnic s. r. o.
Čerčanská 2023/12, Krč, 140 00 Praha 4


Zhotov



Valbek, spol. s r.
Vaňurova 505/17
460 07 Liberec 3

	HIP:
--	------

ING. T. KLIME

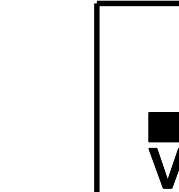

Vypracoval	M. KOŘÍNEK
Zodp. projektant	ING. T. KLIMENT
Tech. kontrola	ING. M. HANŽL

	Zak. číslo	21
--	------------	----

	Datum	02

	Stupeň	PD
	První stupeň	První stupeň

Počet formátů	8x
Měřítko	1:1

Č. přílohy	Pa
------------	----

Příloha	PŘÍČNÉ ŘEZY, VĚTEV
---------	--------------------

	5
--	---