


SO 121 - PŘELOŽKA SILNICE V km 2,200
SITUACE, M 1 : 1 000

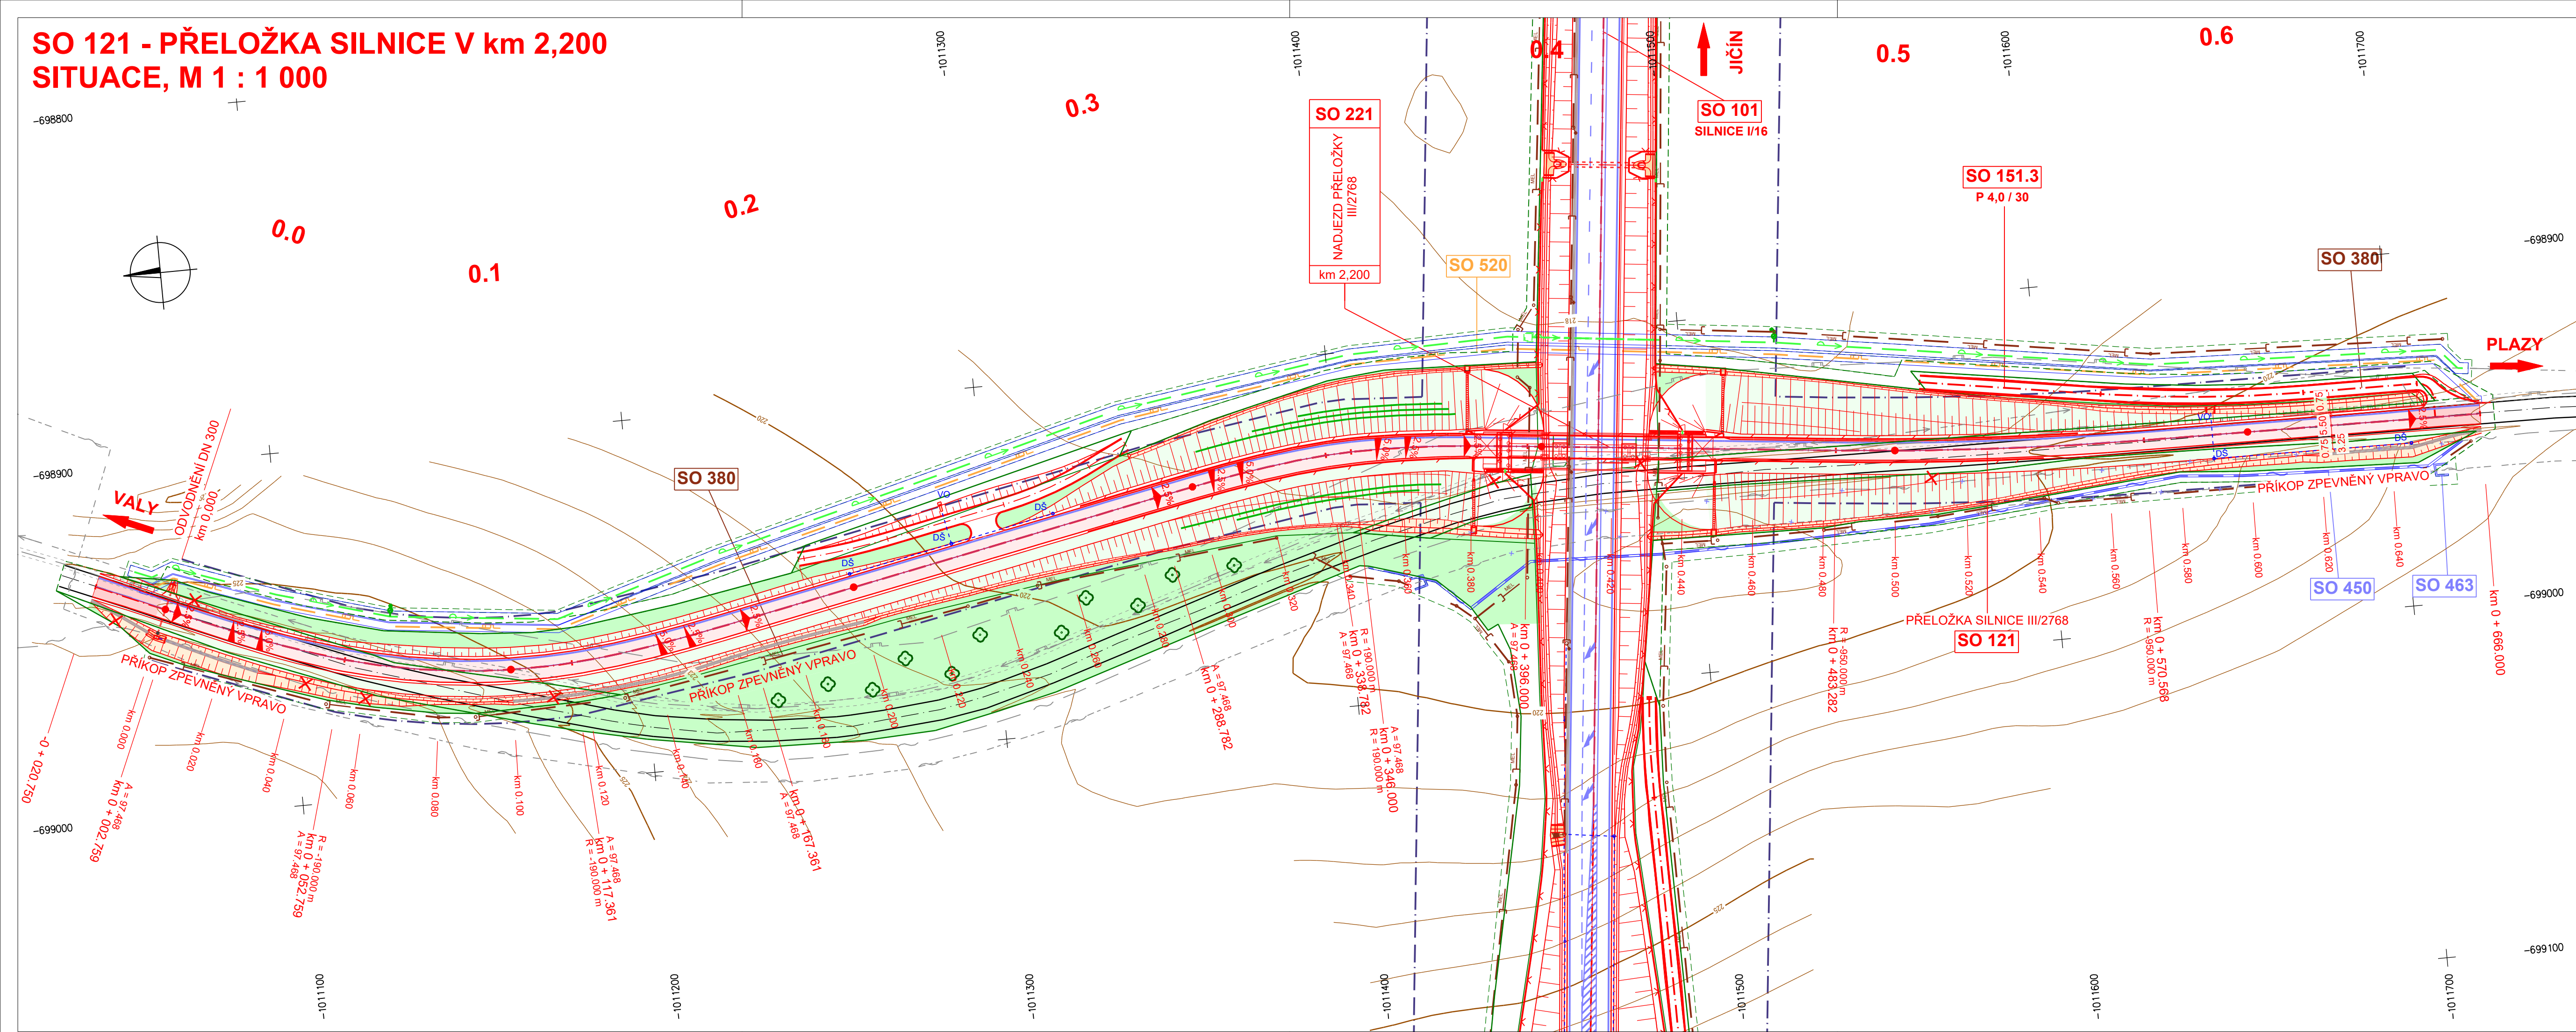

LEGENDA:	
PLOCHY	VOZOVKA - ASFALTOVÝ KRYT
	VOZOVKA - FRÉZOVANÁ
	VOZOVKA - POLNÍ CESTY
	CHODNÍK
	DLAŽBA VOZOVKY
	SWAHY VÝKOPU
	SWAHY NÁSYPU
	VEGETAČNÍ ÚPRAVY
	OBVOD STAVBY
	TRVALÝ ZÁBOR
	DOČASNÝ ZÁBOR
NOVÉ IS	DEŠŤOVÁ KANALIZACE
	MELIORACE
	VÝTLAK
	VODOVOD
	NADZEMNÍ VEDENÍ NN
	NADZEMNÍ VEDENÍ VN
	PODZEMNÍ VEDENÍ NN
	PODZEMNÍ SDĚLOVACÍ VEDENÍ
	PLYNOVOD - STL
	STÁVAJÍCÍ IS - INFORMATIVNÍ ZÁKRES
STÁVAJÍCÍ IS - INFORMATIVNÍ ZÁKRES	PODZEMNÍ VEDENÍ NN
	PODZEMNÍ VEDENÍ VN
	NADZEMNÍ VEDENÍ NN
	NADZEMNÍ VEDENÍ VN
	NADZEMNÍ VEDENÍ VVN
	DEŠŤOVÁ KANALIZACE
	PLYNOVOD - STL
	PODZEMNÍ SDĚLOVACÍ VEDENÍ
	VODOVOD

Souřadnicový systém: S-JSTK
Výškový systém Bpv

SO 121Přeložka silnice v km 2,200

Objednatel:



ŘEDITELSTVÍ
SILNIC
A DÁLNIC

Ředitelství silnic a dálnic s. p.
Čerčanská 2023/12, Krč, 140 00 Praha 4

Zhotovitel:



Valbek

Valbek, spol. s r.o.

Vaňurova 505/17
460 07 Liberec 3

HIP:

ING. T. KLIMENT



Valbek

Ypracoval

ING. A. DUMANSKA

Zodp. projektant

ING. T. KLIMENT

Tech. kontrola

ING. M. HANŽL

Akce

I/16 MLADÁ BOLESLAV - MARTINOVICE

Zhotovitel:

Valbek, spol. s r.o.
Vaňurova 505/17
460 07 Liberec 3

Příloha

SITUACE

Zak. číslo

21-L113-001

Datum

02/2025

Stupeň

PDPS

Počet formátů

5 x A4

Měřitko

1 : 1 000

Č. přílohy

Paré

2