


SO 121 - PŘELOŽKA SILNICE III/2768 V km 2,200
PODÉLNÝ PROFIL, M 1 : 1 000 / 100

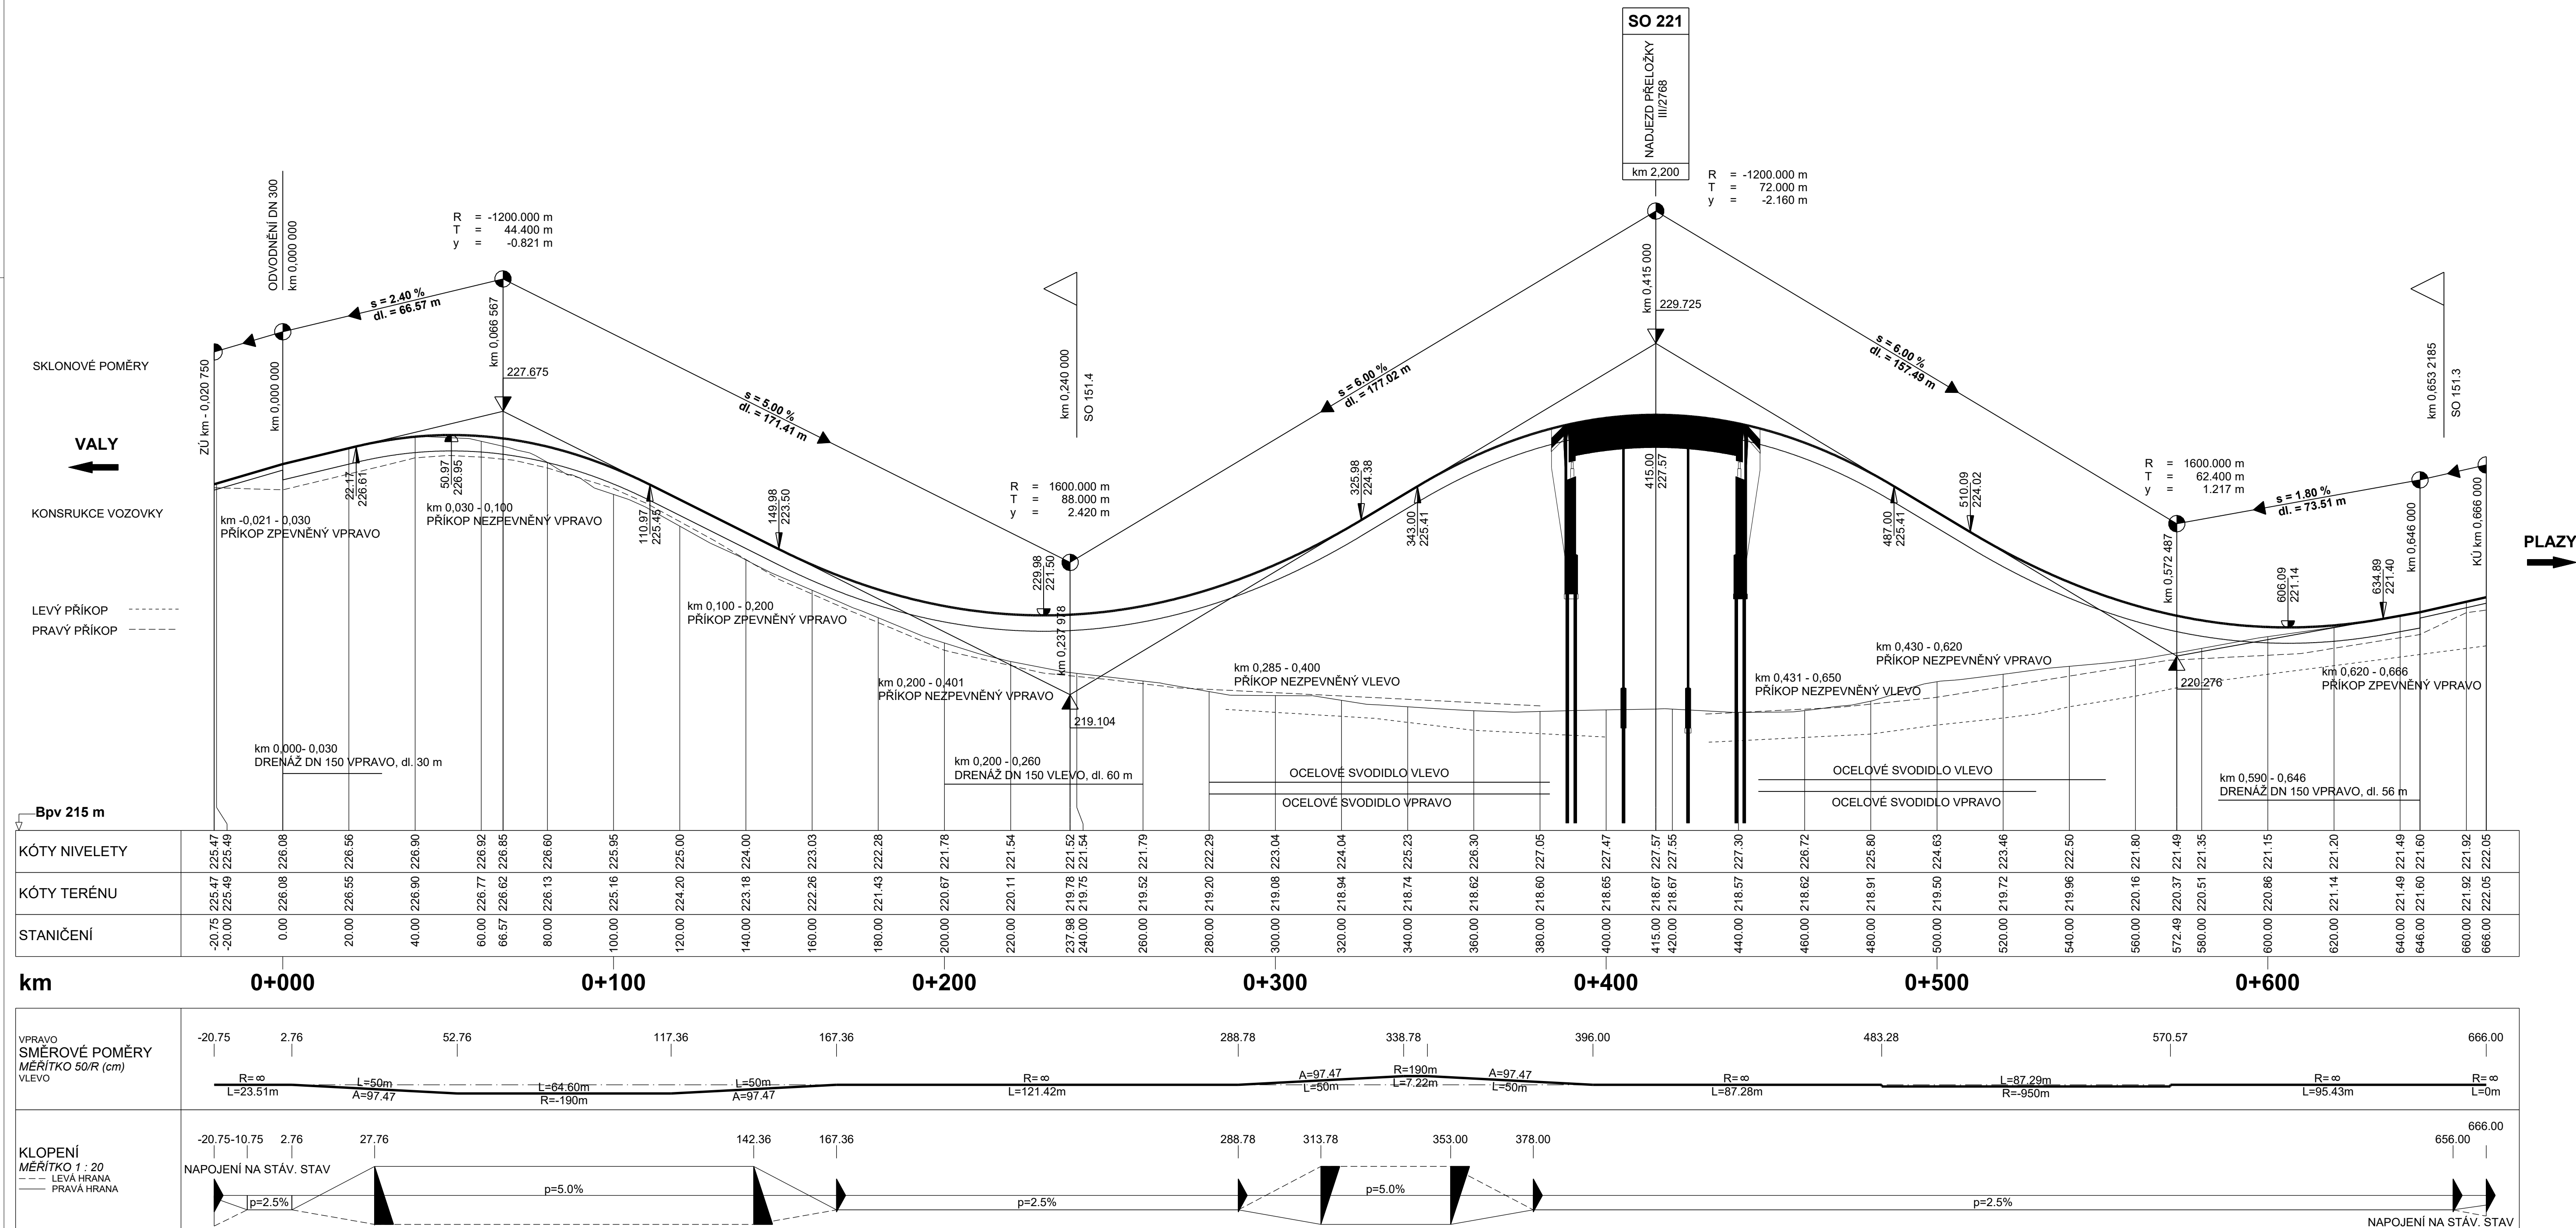

Výškový systém Bpv

SO 121	Přeložka silnice III/2768 v km 2,200
---------------	--------------------------------------



Ředitelství silnic a dálnic s. p.
Čerčanská 2023/12, Krč, 140 00 Praha 4

Zhotovitel:



Valbek, spol. s r.o.
Vaňurova 505/17
460 07 Liberec 3

	HIP:
--	------

ING. T. KLIMENT



Vypracoval	ING. A. DUMANSKA
Zodp. projektant	ING. T. KLIMENT
Tech. kontrola	ING. M. HANŽL
Akce	
I/16 MLADÁ BOLESLAV - MA	

Zak. číslo	21-LI13-001
Datum	02/2025
Stupeň	PDPS
Počet formátů	18 x A4
Měřítko	1 : 1000/100
Č. přílohy	Paré

Zhotovitel:
Valbek, spol. s
Vaňurova 505/
460 07 Liberec

Příloha	PODÉLNÝ PROFIL
---------	----------------

3