

SO 121 - PŘELOŽKA SILNICE III/2768 V km 2,200
VZOROVÉ PŘÍČNÉ ŘEZY, M 1:50


NÁVRHOVÁ KATEGORIE S 6,5/60
NÁŠYP

TŘÍDA DOPRAVNÍHO ZATÍŽENÍ IV
NÁVRHOVÁ ÚROVEŇ PORUŠENÍ D1
TYP PODLOŽÍ PIII (D1-A-2)

VALY

PLAZY

NÁŠYP
h nad 3 m

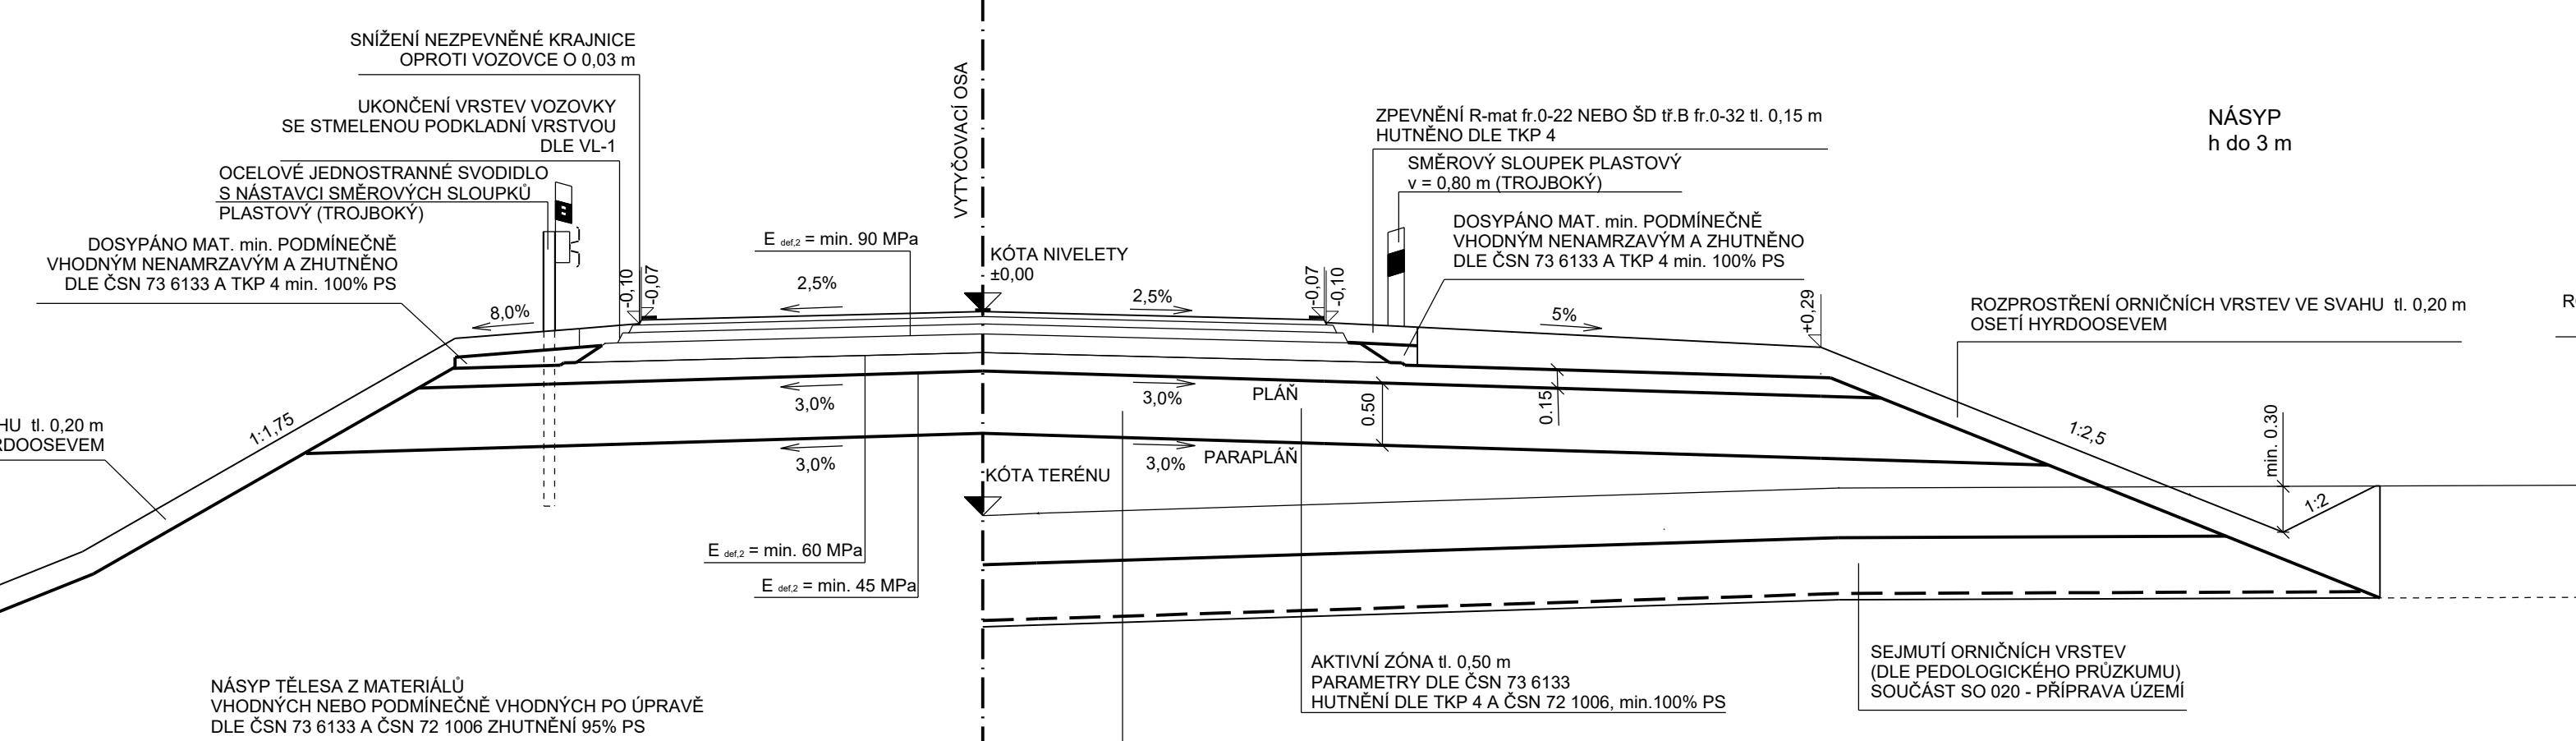

proměnné

ROZPROSTŘENÍ ORNIČNÍCH VRSTEV V ROVINĚ II. 0,90 m
OŠETI HYDROOSEVEM

SANACE PODLOŽÍ NÁŠYPU - TYP I


PRVNÍ VRSTVA NÁŠYPU ŠD₁ fr. 0/125 II. min. 0,50 m,
HUTNĚNÍ DLE ČSN 73 6133 A TKP 4 min. 100% PS
NETKANÁ SEPARAČNÍ GEOTEXTILIE TYP S2 DLE TP 97
UPRAVA ZÁKLADOVÉ SPÁRY NÁŠYPU
HUTNĚNÍ DLE ČSN 73 6133 A TKP 4 min. 92% PS, IBI ≥ 5%

NÁVRHOVÁ KATEGORIE S 6,5/60
NÁŘEZ

TŘÍDA DOPRAVNÍHO ZATÍŽENÍ IV
NÁVRHOVÁ ÚROVEŇ PORUŠENÍ D1
TYP PODLOŽÍ PIII (D1-A-2)

VALY

PLAZY

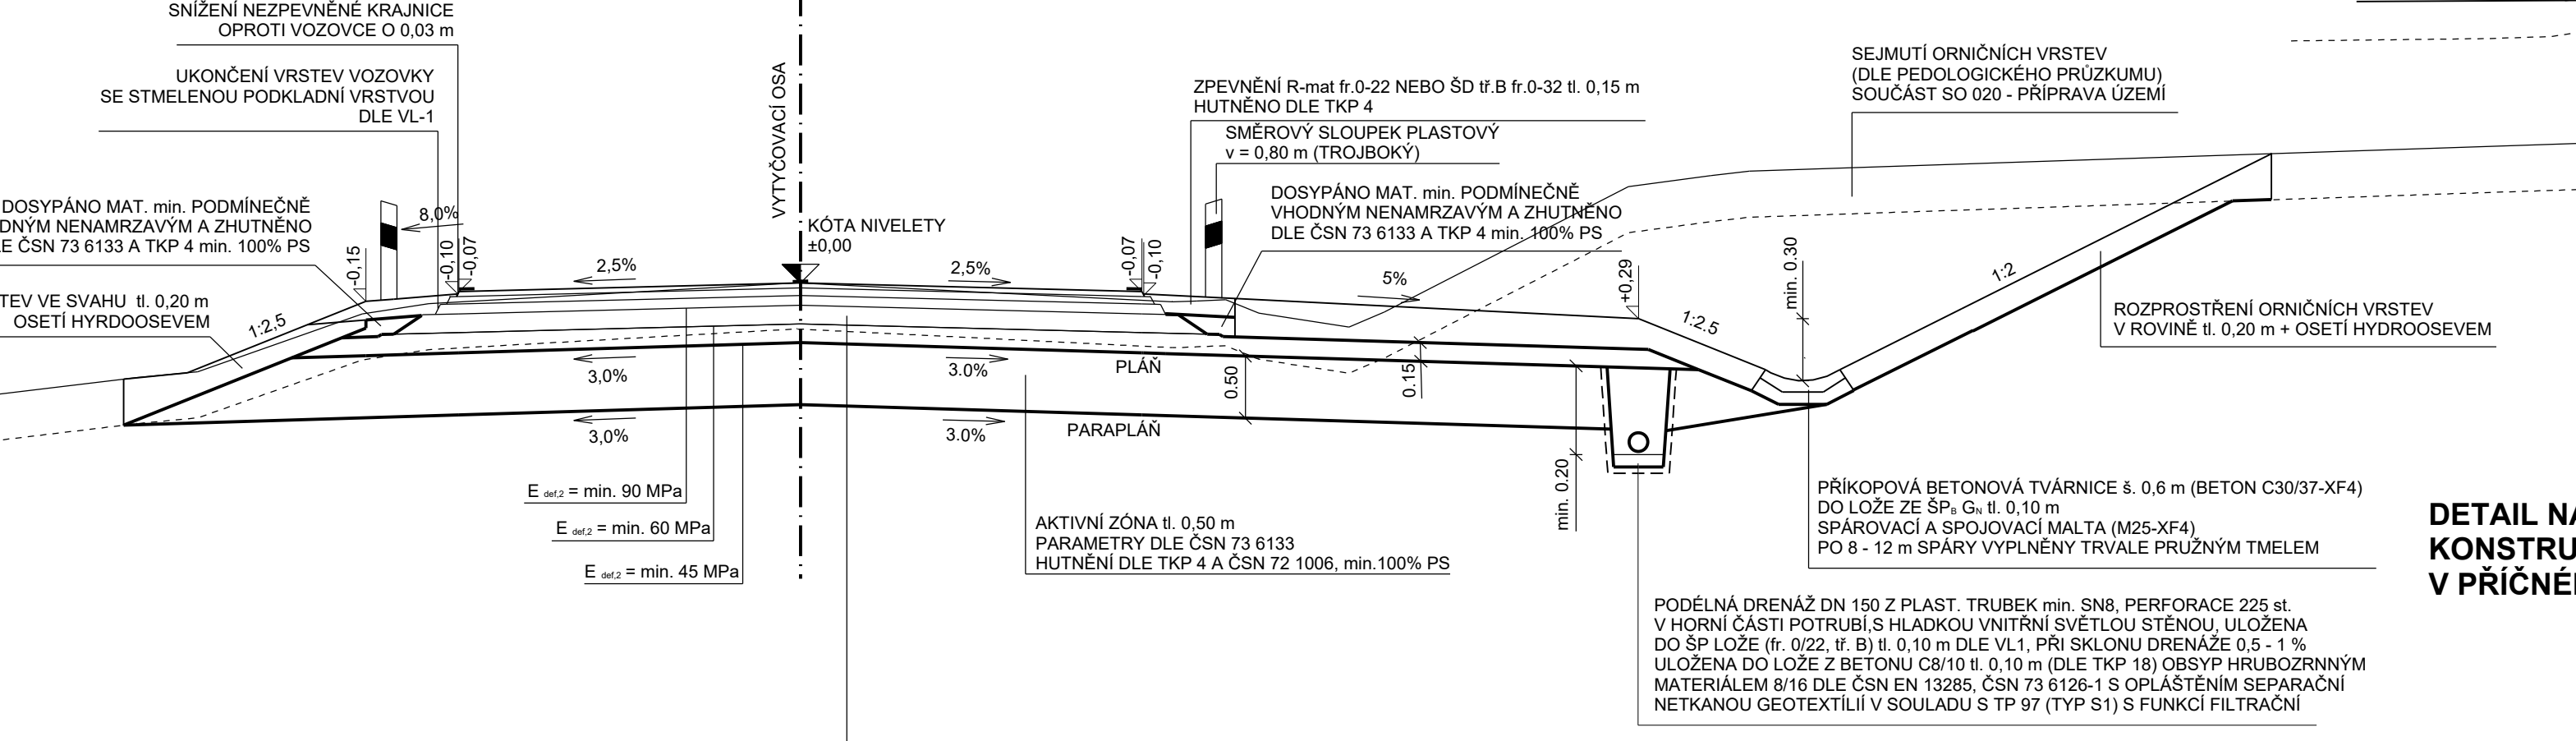


proměnné

ROZPROSTŘENÍ ORNIČNÍCH VRSTEV V ROVINĚ II. 0,90 m
OŠETI HYDROOSEVEM


SANACE PODLOŽÍ NÁŠYPU - TYP I

PRVNÍ VRSTVA NÁŠYPU ŠD₁ fr. 0/125 II. min. 0,50 m,
HUTNĚNÍ DLE ČSN 73 6133 A TKP 4 min. 100% PS
NETKANÁ SEPARAČNÍ GEOTEXTILIE TYP S2 DLE TP 97
UPRAVA ZÁKLADOVÉ SPÁRY NÁŠYPU
HUTNĚNÍ DLE ČSN 73 6133 A TKP 4 min. 92% PS, IBI ≥ 5%


ODVODNĚNÍ DN 300 V km 0,000

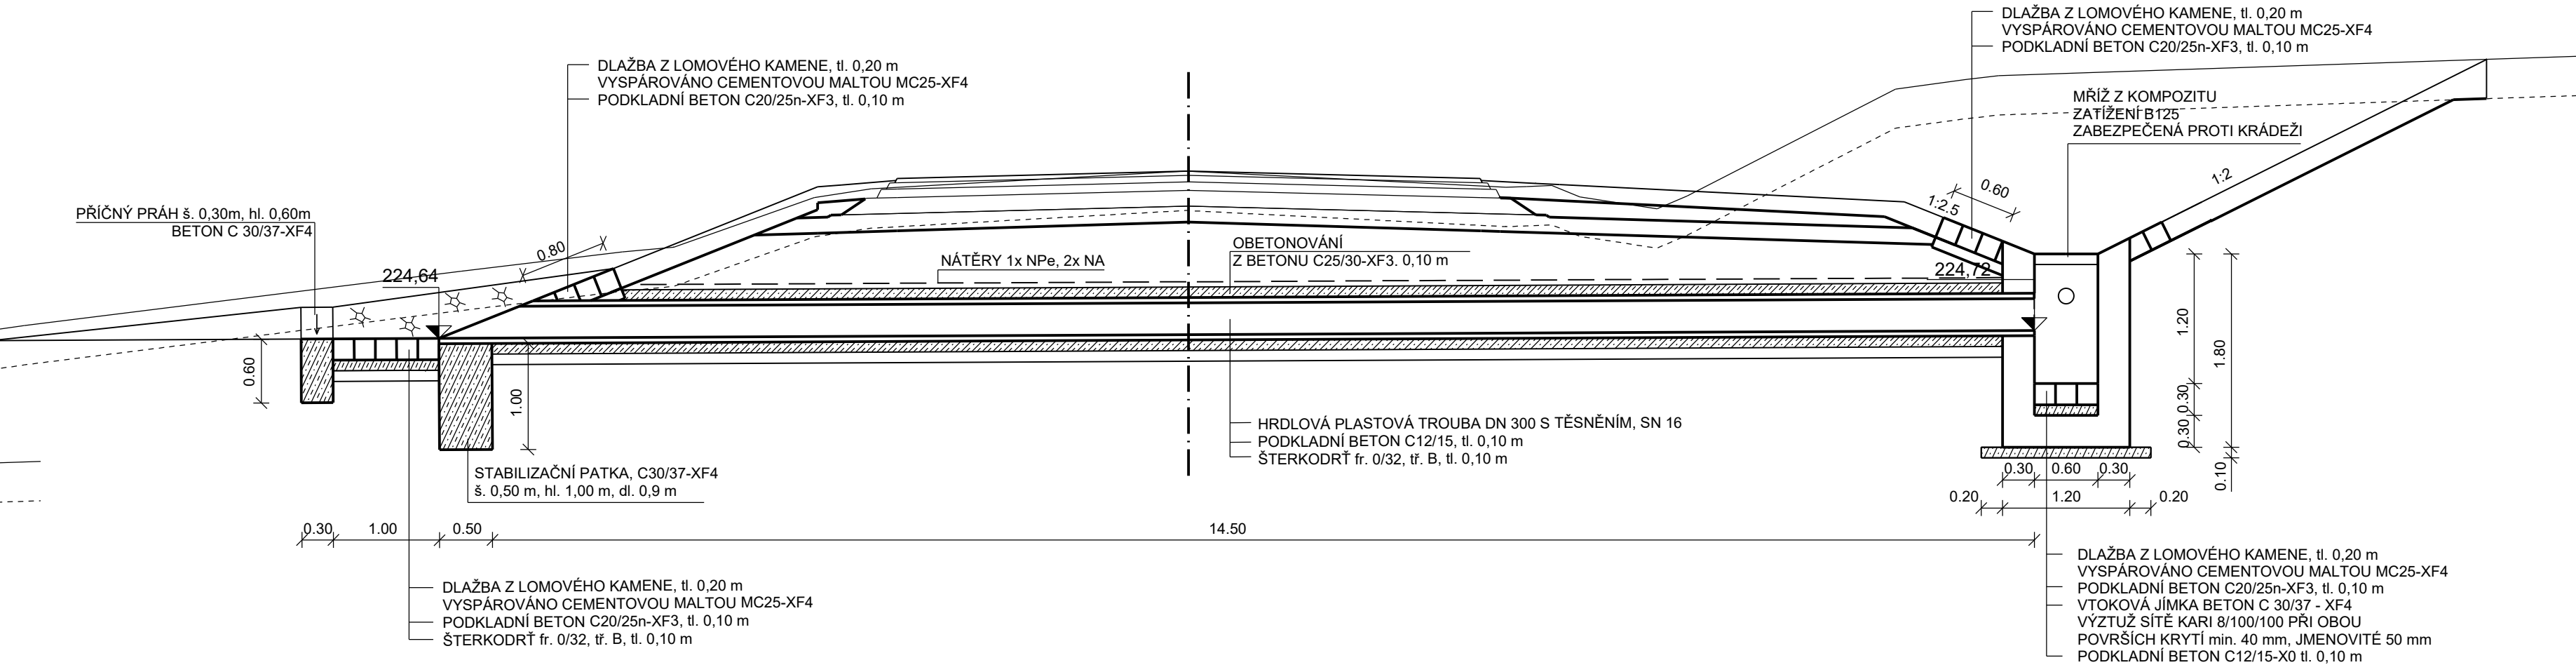


DETAIL NAPOJENÍ NOVÉ
KONSTRUKCE NA STÁVAJÍCÍ
V PŘÍČNÉM SMĚRU

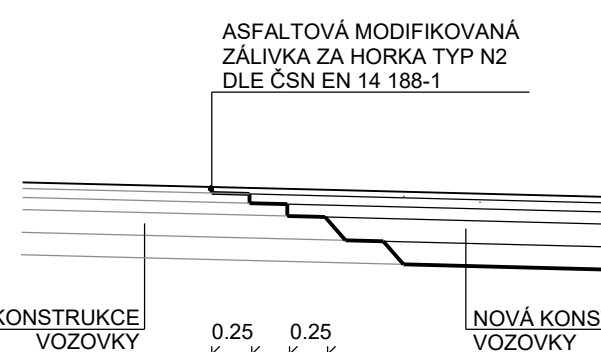

DETAIL NAPOJENÍ NOVÉ
KONSTRUKCE NA STÁVAJÍCÍ
V PÓDĚLNÉM SMĚRU

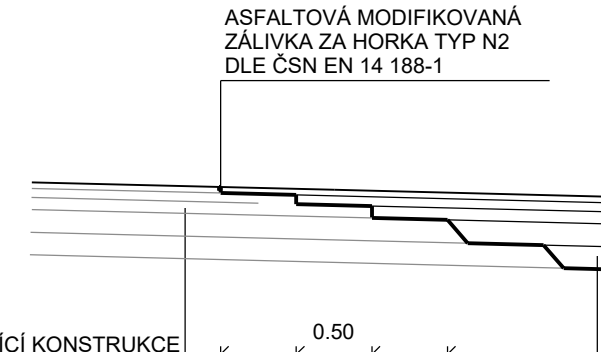

DETAIL VÝUSTĚNÍ DRENÁŽE M 1 : 100

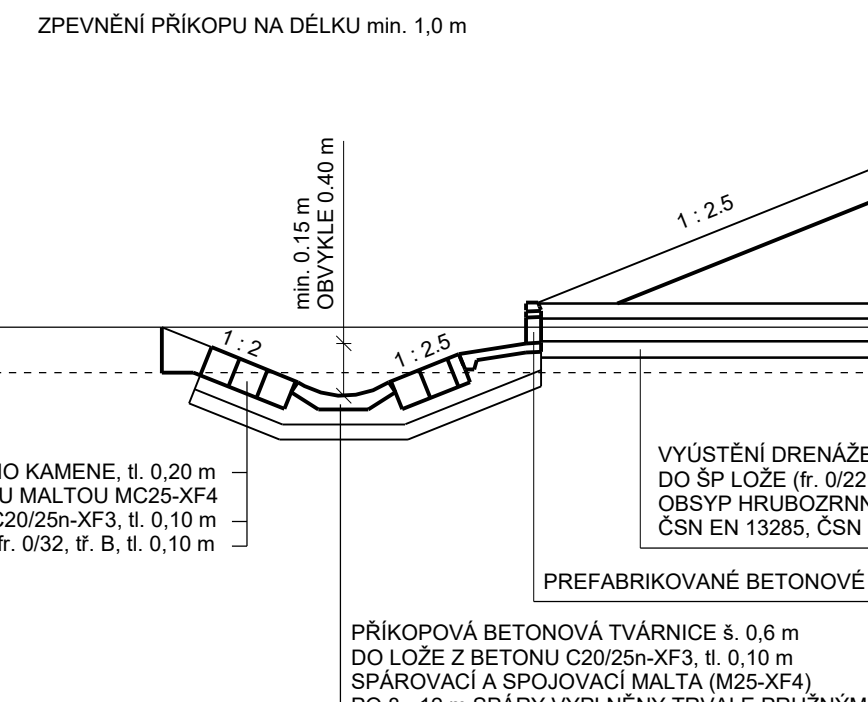

POZNÁMKY:

- SPÁRY DLAŽBY Z LOMOVÉHO KAMENE VYPLNĚNÉ CEMENTOVOU MALTOU M25 - XF4 II. 0,20 m
- VŠECHNY BETONOVÉ PRVKY, KTERÉ PŘÍJÍDOU DO STYKU SE ZEMINOU MUSÍ BÝT OPATŘENY NÁTĚRY: 1x NP6 A 2x NA
- VYTÝČENÍ BUDE PROVEDENO DLE TKP1 A SOUVISEJÍCÍCH PŘEDPISŮ
- SKLONY SVAHŮ JSOU URČENY SKLONEM SILNIČNÍHO TĚLESA A PŘÍLEHLÝCH PŘÍKOPŮ
- VÝZTUŽ JIMKY KARI ŠÍŘ 8/100/100, KRYTÍ min. 40 mm, JMENOVITĚ 50 mm
- OCELOVÁ STUPADLA DODATEČNĚ KOTVENÁ
- POTRUBÍ MUSÍ BÝT UV STABILNÍ

SO 121 Přeložka silnice III/2768 v km 2,200

Objednatel: Ředitelství silnic a dálnic s. p.
Čerčanská 2023/12, Krč, 140 00 Praha 4

Zhotovitel: Valbek, spol. s r.o.
Vahurova 505/17
460 07 Liberec 3

Valbek, spol. s r.o.
Vahurova 505/17
460 07 Liberec 3

Ing. T. KLIMENT

Ing. A. DUMANSKA
Ing. T. KLIMENT
Ing. M. HANŽL

Zak. číslo 21-L113-001
Datum 02/2025
Stupeň PDPS
Počet formátů 9 x A4
Měřítko 1 : 50
Č. přílohy Paré

Příloha
VZOROVÉ PŘÍČNÉ ŘEZY

4