SO 121 - PŘELOŽKA SILNICE V km 2,200
PŘÍČNÉ ŘEZY km 0,300 - km 0,480
M 1:100

km 0 + 300.000

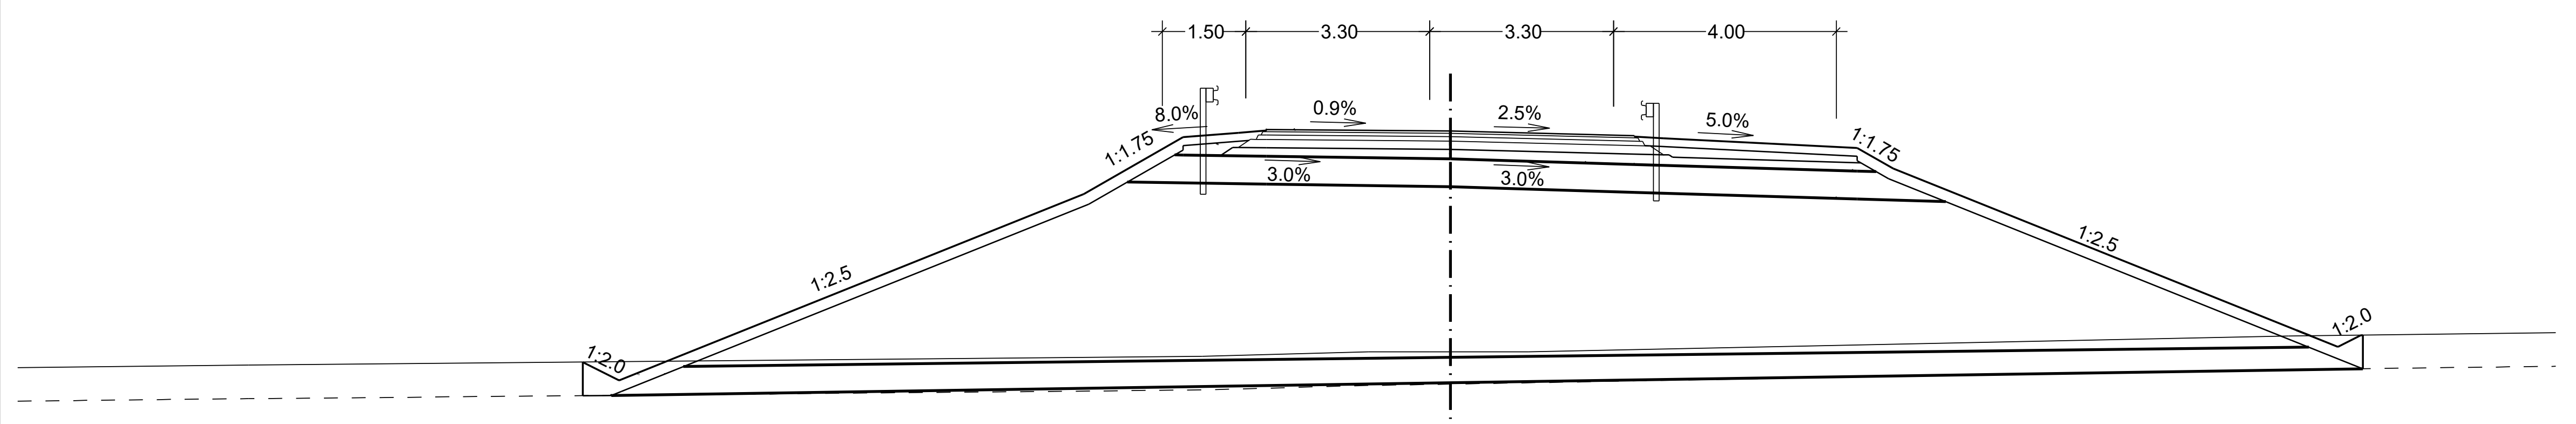

S. R. 216 m

PROJEKTOVANÝ STAV	218.89	218.29	218.57	218.87	218.91	221.91	222.93	223.00	223.02	223.04	223.06	223.04	222.95	222.93	222.91	222.91	222.73	222.36	219.47	219.36	219.17	219.37	219.37	218.77
ODSAZENÍ OD OSY	-15.58	-15.58	-14.93	-14.18	-14.08	-6.58	-4.80	-3.81	-3.32	-3.31	-3.30	0.00	3.30	3.31	3.32	3.82	7.30	7.95	15.18	15.45	15.93	16.34	16.38	16.38

STÁVAJÍCÍ TERÉN	219.00	219.08	219.08	219.08	219.36
ODSAZENÍ OD OSY	-4.09	-1.10	0.00	1.77	15.42

km 0 + 340.000

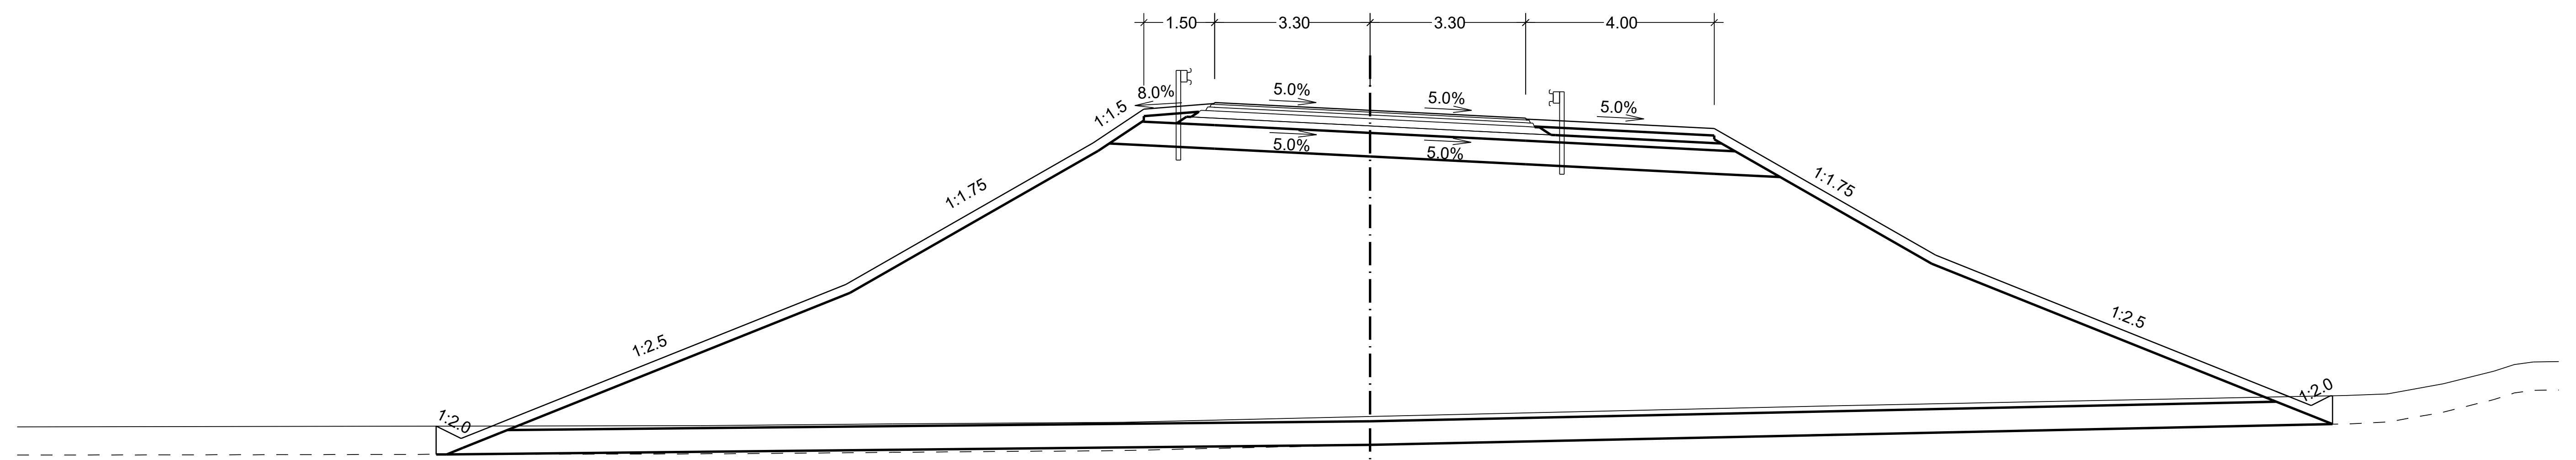

S. R. 215 m

PROJEKTOVANÝ STAV	218.53	217.93	218.27	218.53	218.57	221.53	224.53	225.25	225.33	225.35	225.37	225.39	225.23	225.06	225.04	225.02	225.01	224.84	222.15	219.27	219.15	218.97	219.17	219.17	218.57
ODSAZENÍ OD OSY	-19.81	-19.81	-19.29	-18.62	-18.54	-11.12	-5.87	-4.80	-3.80	-3.32	-3.31	-3.30	0.00	3.30	3.31	3.32	3.84	7.30	12.00	19.21	19.50	19.96	20.37	20.42	20.42

STÁVAJÍCÍ TERÉN	218.54	218.58	218.61	218.74	218.96	219.18	219.22	219.43	219.70	219.84	219.89
ODSAZENÍ OD OSY	-14.22	-10.13	-5.23	0.00	9.75	20.69	21.58	22.77	23.84	24.27	24.68

km 0 + 460.000

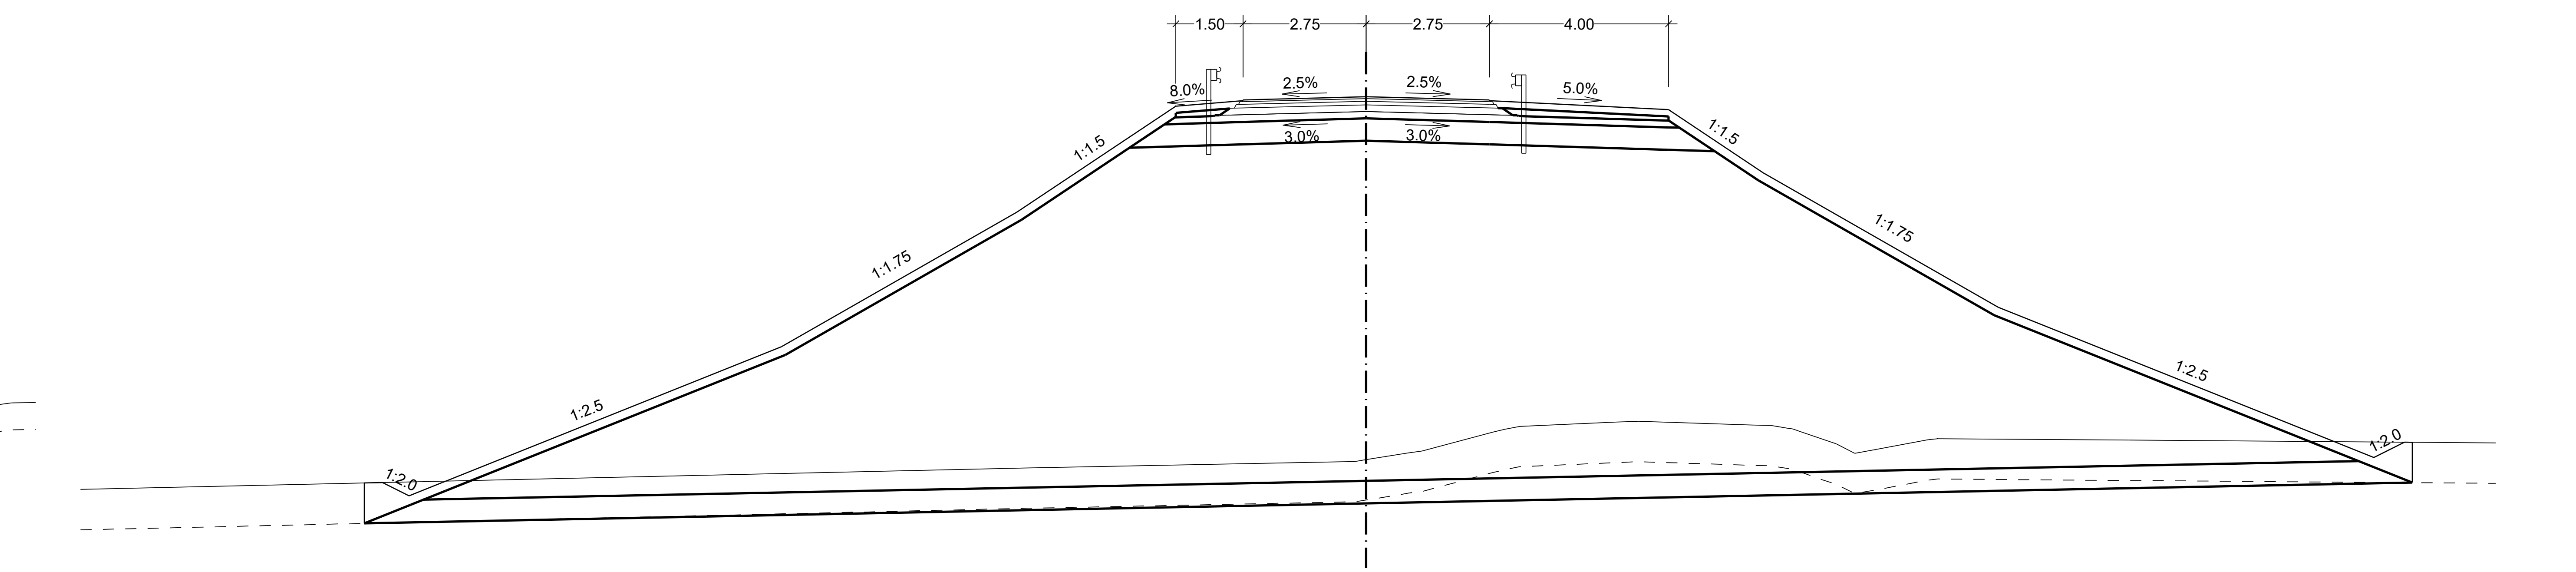

S. R. 215 m

PROJEKTOVANÝ STAV	217.20	218.10	218.11	217.82	218.12	218.14	221.14	224.14	226.51	226.59	226.61	226.63	226.65	226.72	226.65	226.63	226.61	226.61	226.43	225.03	222.03	219.03	218.97	218.67	219.01	219.01	218.11
ODSAZENÍ OD OSY	-22.37	-22.37	-21.96	-21.37	-20.62	-20.55	-13.05	-7.80	-4.25	-3.27	-2.77	-2.76	-2.75	0.00	2.75	2.76	2.77	3.27	6.75	8.86	14.11	21.61	21.75	22.50	23.18	23.36	23.36

STÁVAJÍCÍ TERÉN	218.44	218.58	218.62	218.78	218.82	219.24	219.30	219.37	219.46	219.48	219.40	219.39	219.33	219.31	219.25	218.98	218.77	218.85	219.07	219.09	219.06
ODSAZENÍ OD OSY	-7.56	-0.25	0.00	0.96	1.24	2.83	3.10	3.43	5.59	6.08	8.64	9.04	9.42	9.52	9.70	10.50	10.91	11.39	12.55	12.76	17.03

km 0 + 320.000

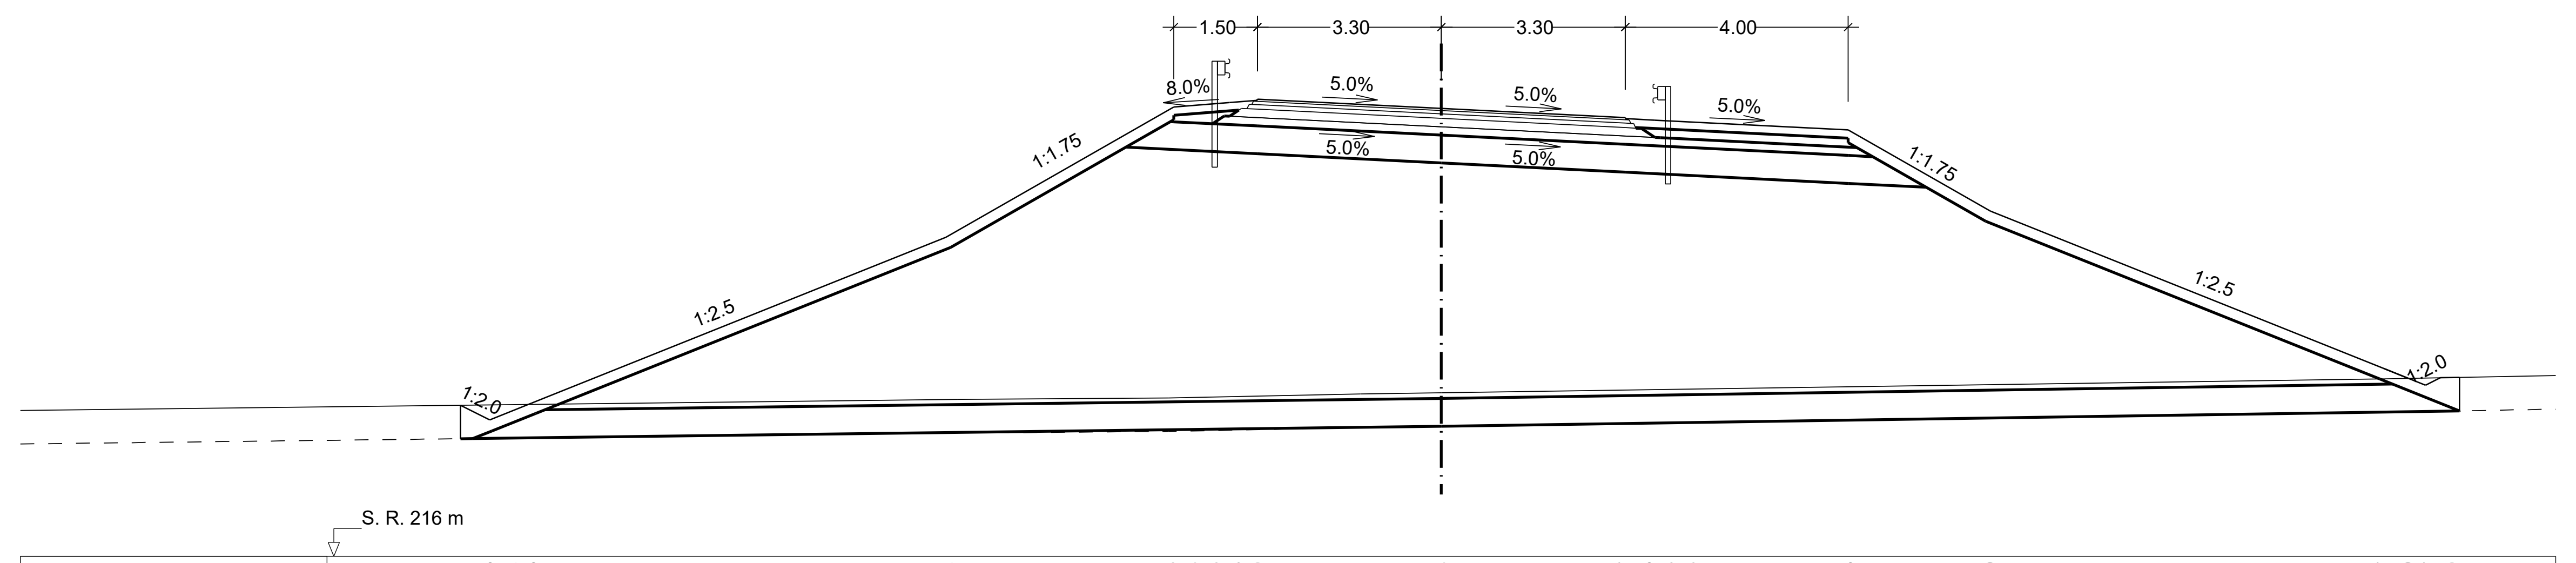

S. R. 216 m

PROJEKTOVANÝ STAV	218.71	218.11	218.45	218.72	218.75	221.72	224.06	224.14	224.16	224.18	224.20	224.04	223.87	223.85	223.83	223.83	223.65	222.19	219.37	219.19	219.07	219.20	219.21	218.61
ODSAZENÍ OD OSY	-17.60	-17.60	-17.08	-16.39	-16.33	-8.89	-4.80	-3.80	-3.32	-3.31	-3.30	0.00	3.30	3.31	3.32	3.84	7.30	9.85	16.91	17.35	17.66	17.93	18.27	18.27

STÁVAJÍCÍ TERÉN	218.81	218.84	218.91	218.94	219.18
ODSAZENÍ OD OSY	-8.67	-4.89	-1.45	0.00	16.93

km 0 + 360.000

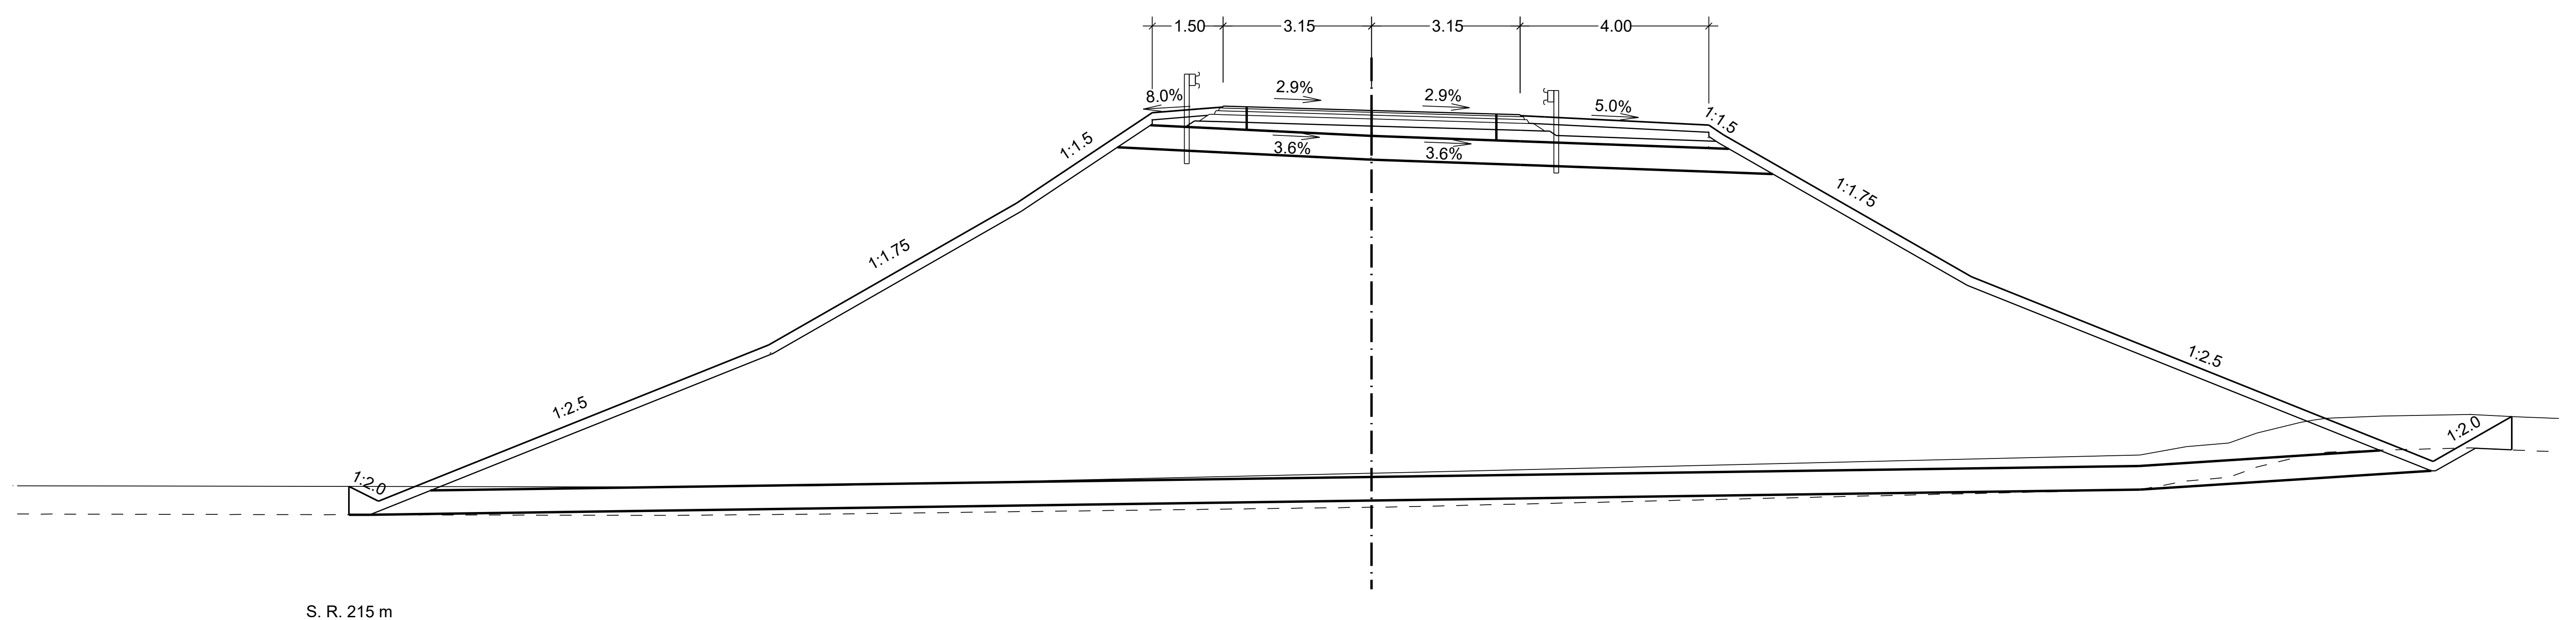

S. R. 215 m

KÓTY NOVÉHO STAVU	218.34	217.74	218.03	218.33	218.34	221.34	224.34	226.26	226.34	226.36	226.38	226.40	226.30	226.21	226.19	226.17	226.17	225.99	225.78	222.78	219.78	219.17	218.87	219.82	219.11
VZDÁLENOST OD OSY	-21.67	-21.67	-21.05	-20.30	-20.28	-12.78	-7.53	-4.65	-3.65	-3.17	-3.16	-3.15	0.00	3.15	3.16	3.17	3.67	7.15	7.46	12.71	20.21	21.75	22.50	24.16	24.16

KÓTY TERÉNU	218.33	218.36	218.62	218.63	219.00	219.18	219.26	219.47	219.70	219.75	219.79	219.83	219.87	219.82
VZDÁLENOST OD OSY	-14.98	-11.46	0.00	0.61	16.28	17.27	18.16	18.76	19.70	19.97	20.24	21.42	23.28	24.29

km 0 + 480.000

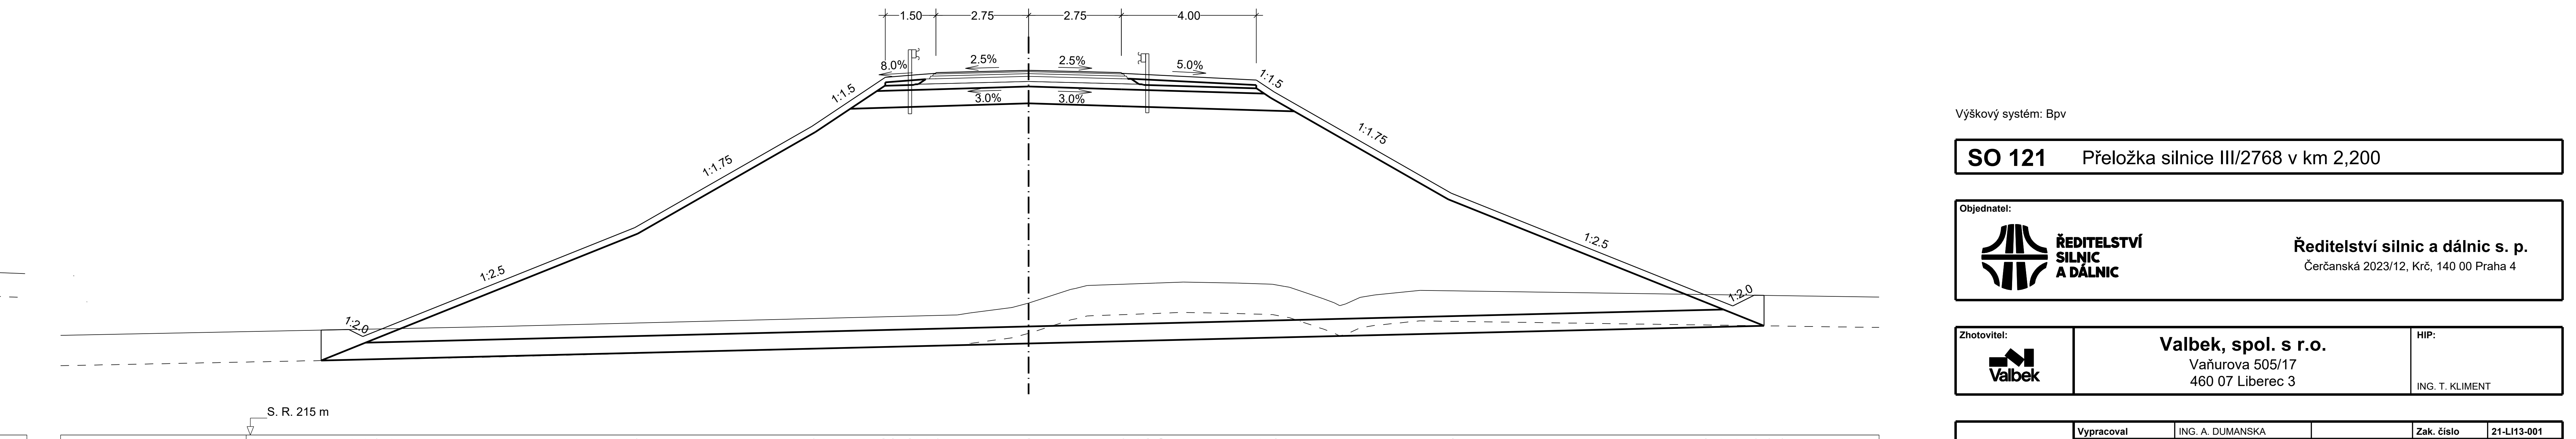

S. R. 215 m

PROJEKTOVANÝ STAV	217.21	218.11	218.12	217.92	218.14	218.22	221.14	224.14	225.60	225.67	225.70	225.72	225.74	225.80	225.74	225.72	225.70	225.69	225.52	225.16	222.16	219.16	219.12	218.82	219.14	219.14	218.24
ODSAZENÍ OD OSY	-20.98	-20.98	-20.16	-19.75	-19.18	-19.00	-11.68	-6.43	-4.25	-3.27	-2.77	-2.76	-2.75	0.00	2.75	2.76	2.77	3.27	6.75	7.28	12.53	20.03	20.13	20.88	21.51	21.81	21.81

STÁVAJÍCÍ TERÉN	218.21	218.56	218.62	218.78	218.91	219.31	219.34	219.43	219.50	219.53	219.50	219.47	219.47	219.40	219.38	219.27	219.04	218.92	218.83	218.88	219.08	219.15	219.29
ODSAZENÍ OD OSY	-16.10	-2.11	-1.74	-0.49	0.00	1.25	1.38	1.74	3.76	4.59	6.19	7.22	7.23	7.58	7.73	8.06	8.73	9.06	9.23	9.40	9.83	10.27	11.61

Výškový systém: Bpv

SO 121 Přeložka silnice III/2768 v km 2,200

Objednatel:

ŘEDITELSTVÍ SILNIC A DÁLNIC

Ředitelství silnic a dálnic s. p.
Čerčanská 2023/12, Krč, 140 00 Praha 4

Zhotovitel:

Valbek

Valbek, spol. s r.o.
Vaňurova 505/17
460 07 Liberec 3

HIP:
ING. T. KLIMENT

Vypracoval	ING. A. DUMANSKA		Zak. číslo	21-LI13-001
Zodp. projektant	ING. T. KLIMENT		Datum	02/2025
Tech. kontrola	ING. M. HANŽL		Stupeň	PDPS
Akce			Počet formátů	18 x A4
I/16 MLADÁ BOLESLAV - MARTINOVICE			Měřítko	1 : 100
			Č. přílohy	Paré
Příloha	PŘÍČNÉ ŘEZY km 0,300 - km 0,480		5.2	

Zhotovitel:
Valbek, spol. s r.o.
Vaňurova 505/17
460 07 Liberec 3