SO 121 - PŘELOŽKA SILNICE V km 2,200
PŘÍČNÉ ŘEZY km 0,500 - km 0,640
M 1:100

km 0 + 500.000

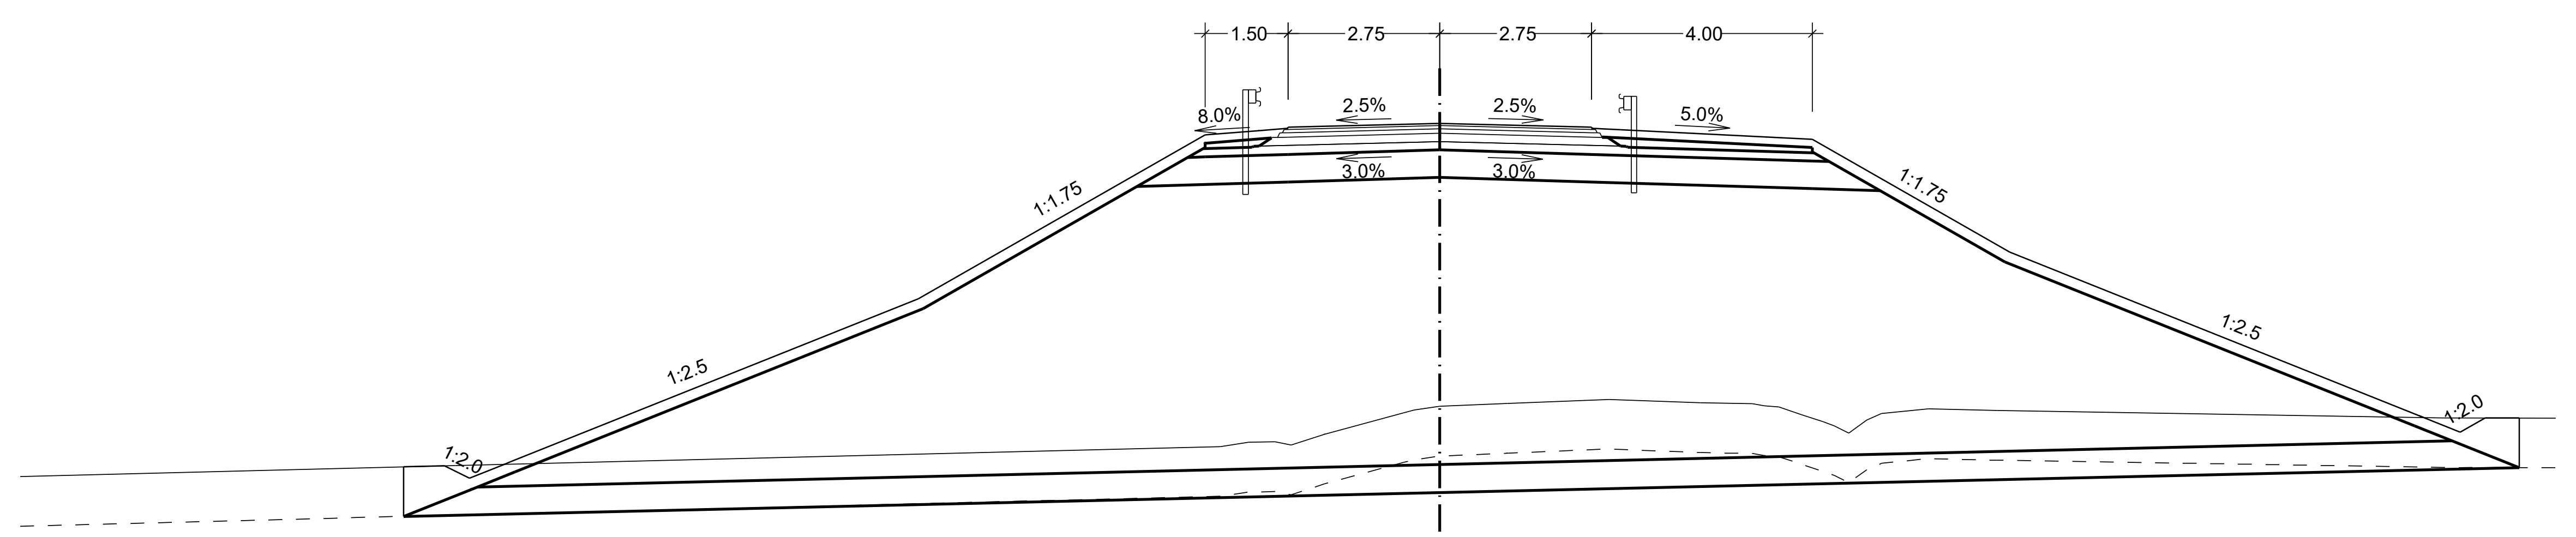

S. R. 215 m

PROJEKTOVANÝ STAV	217.50	218.40	218.42	218.19	218.45	218.49	221.45	224.42	224.50	224.52	224.54	224.56	224.63	224.56	224.54	224.52	224.51	224.34	222.29	219.33	219.29	219.03	219.29	219.28	218.38
ODSAZENÍ OD OSY	-18.78	-18.78	-18.03	-17.58	-16.95	-16.83	-9.45	-4.25	-3.27	-2.77	-2.76	-2.75	0.00	2.75	2.76	2.77	3.27	6.75	10.33	17.74	17.83	18.49	18.94	19.56	19.56

STÁVAJÍCÍ TERÉN	218.42	218.77	218.85	218.85	218.80	218.99	219.38	219.43	219.50	219.55	219.62	219.56	219.54	219.54	219.51	219.48	219.35	219.22	219.14	219.01	219.25	219.37	219.45	219.42	219.29
ODSAZENÍ OD OSY	-17.84	-3.98	-3.47	-2.99	-2.69	-2.09	-0.66	-0.46	0.00	1.22	3.07	4.72	5.66	5.71	5.88	6.15	6.55	6.94	7.15	7.41	7.74	8.00	8.85	10.09	18.17

km 0 + 520.000

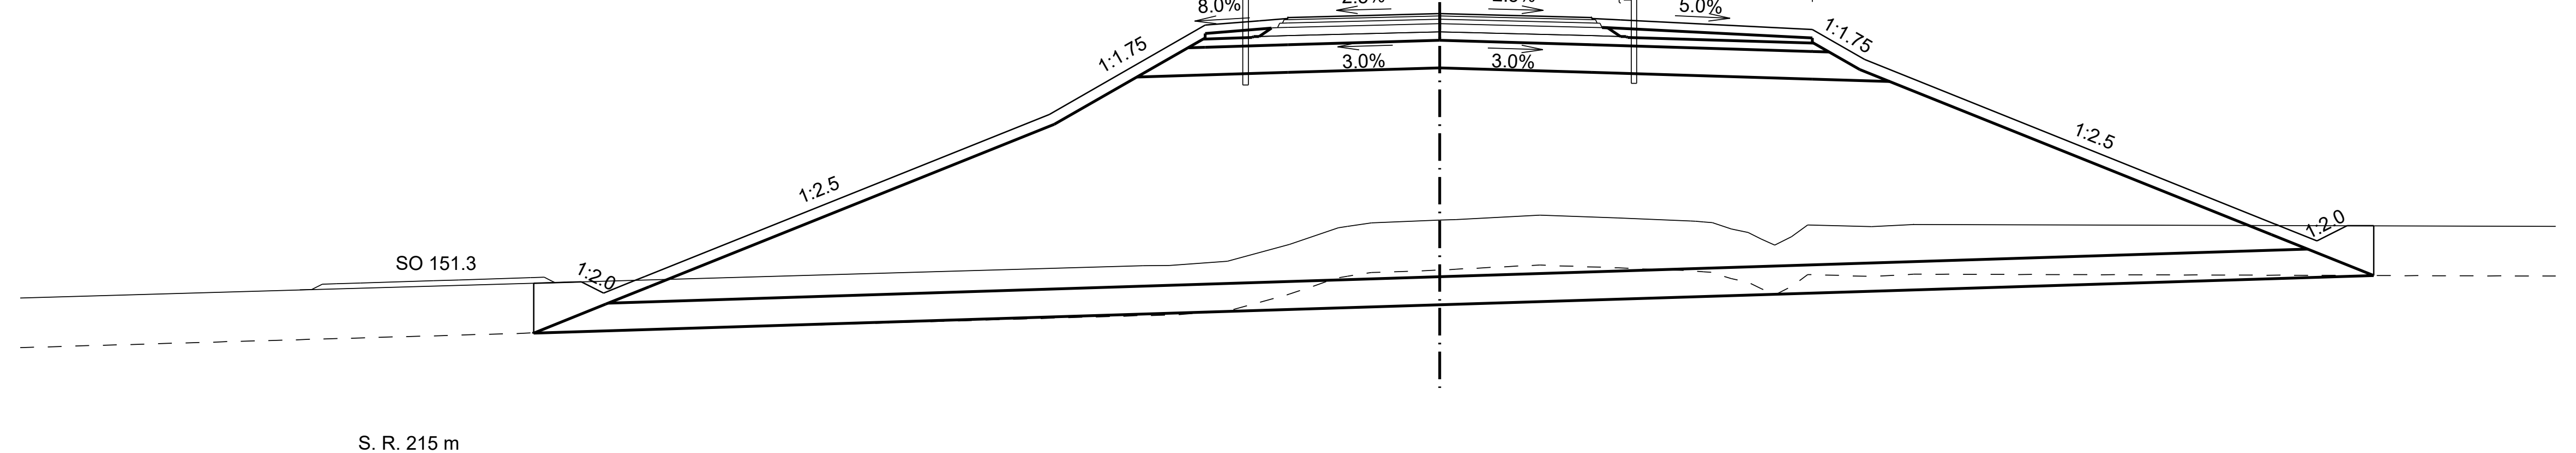

S. R. 215 m

PROJEKTOVANÝ STAV	217.68	218.58	218.61	218.40	218.63	218.70	221.63	223.25	223.33	223.35	223.37	223.39	223.46	223.39	223.37	223.35	223.34	223.17	222.63	219.65	219.63	219.35	219.62	219.62	218.72
ODSAZENÍ OD OSY	-16.42	-16.42	-15.56	-15.15	-14.57	-14.40	-7.07	-4.25	-3.27	-2.77	-2.76	-2.75	0.00	2.75	2.76	2.77	3.27	6.75	7.70	15.14	15.20	15.89	16.44	16.92	16.92

STÁVAJÍCÍ TERÉN	218.90	218.90	218.98	219.28	219.58	219.61	219.67	219.72	219.73	219.81	219.76	219.71	219.70	219.69	219.68	219.56	219.50	219.38	219.27	219.42	219.64	219.60	219.65
ODSAZENÍ OD OSY	-5.38	-4.90	-3.85	-2.72	-1.84	-1.67	-1.24	0.00	0.29	1.82	3.23	4.54	4.63	4.78	4.94	5.28	5.58	5.82	6.07	6.37	6.66	7.83	8.59

km 0 + 540.000

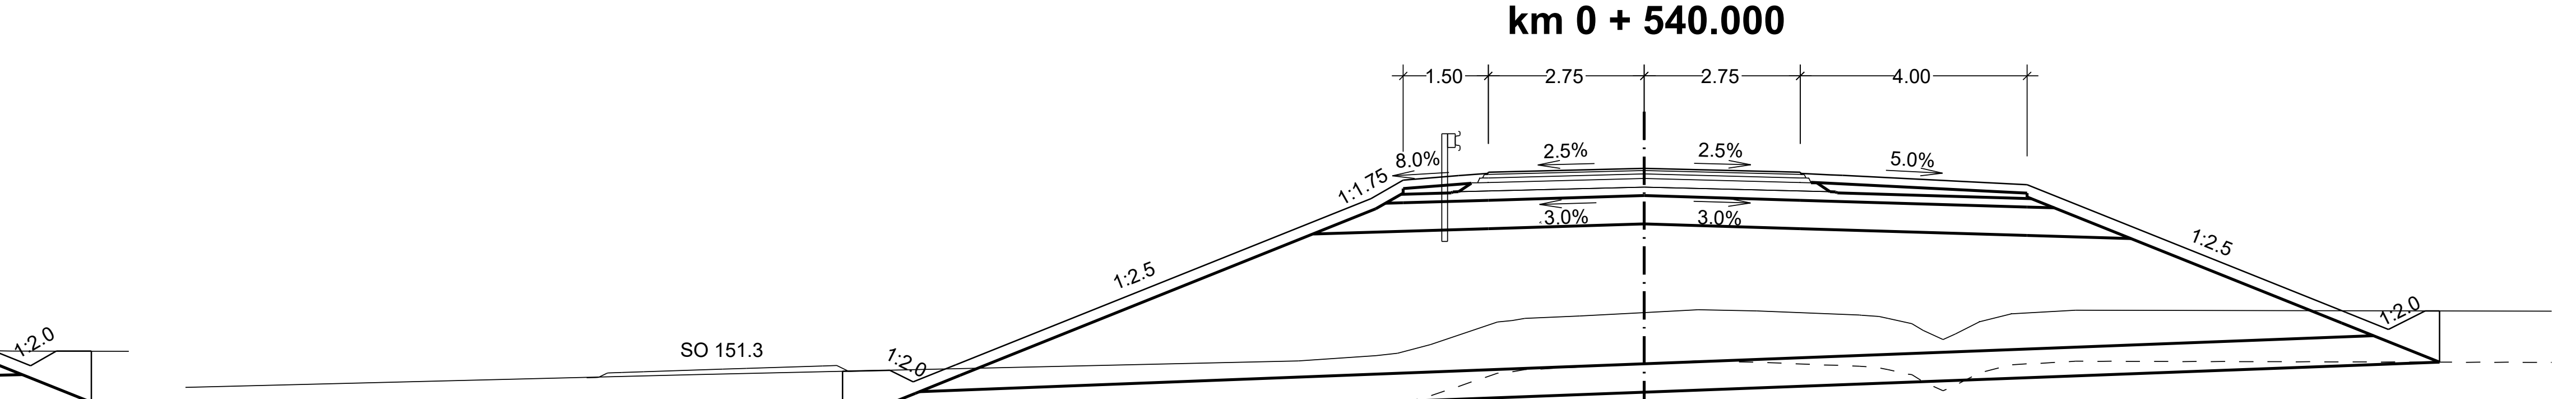

S. R. 215 m

PROJEKTOVANÝ STAV	218.03	218.93	218.95	218.74	218.97	219.04	221.97	222.30	222.37	222.40	222.42	222.44	222.50	222.44	222.42	222.40	222.39	222.38	222.22	220.00	219.97	219.67	219.99	219.99	219.09
ODSAZENÍ OD OSY	-14.13	-14.13	-13.30	-12.89	-12.32	-12.14	-4.82	-4.25	-3.27	-2.77	-2.76	-2.75	0.00	2.75	2.76	2.77	3.27	3.50	6.75	12.30	12.37	13.12	13.77	14.02	14.02

STÁVAJÍCÍ TERÉN	218.87	219.11	219.21	219.25	219.40	219.80	219.82	219.86	219.91	219.96	220.01	219.99	219.92	219.92	219.91	219.89	219.86	219.77	219.65	219.49	219.59	219.81	219.95	220.01
ODSAZENÍ OD OSY	-16.75	-6.10	-4.73	-4.35	-3.77	-2.59	-2.33	-2.11	-1.13	0.00	0.95	1.99	3.79	3.83	4.02	4.14	4.29	4.72	4.92	5.27	5.48	5.91	6.47	7.60

km 0 + 560.000

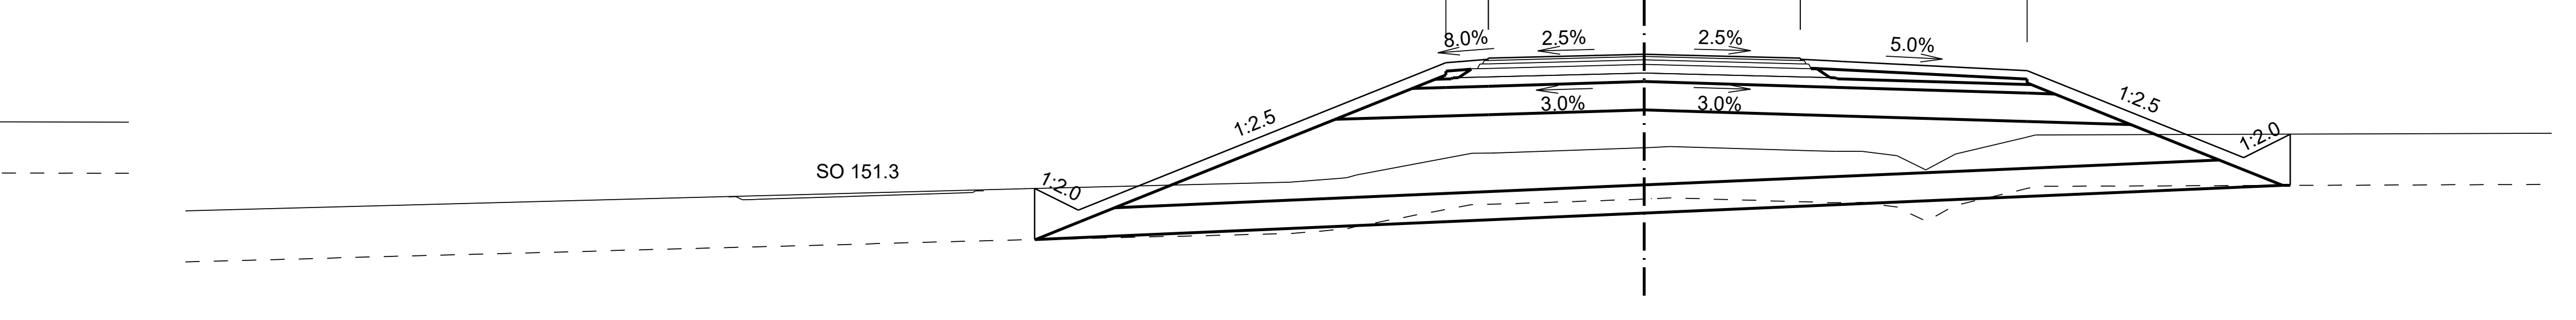

S. R. 216 m

PROJEKTOVANÝ STAV	219.45	218.55	219.06	219.36	219.49	221.66	221.67	221.69	221.72	221.74	221.80	221.74	221.72	221.69	221.69	221.68	221.52	220.39	220.29	219.99	220.40	219.50
ODSAZENÍ OD OSY	-10.75	-10.75	-9.98	-9.23	-8.91	-3.50	-3.27	-2.77	-2.76	-2.75	0.00	2.75	2.76	2.77	3.27	3.50	6.75	9.56	9.82	10.57	11.39	11.39

STÁVAJÍCÍ TERÉN	219.44	219.55	219.63	219.64	219.68	220.06	220.07	220.16	220.17	220.18	220.10	220.10	220.10	220.02	219.77	220.05	220.34	220.38
ODSAZENÍ OD OSY	-10.91	-6.25	-5.36	-5.24	-5.07	-3.04	-2.65	0.00	0.13	0.45	3.02	3.38	3.84	4.45	4.96	5.49	6.71	6.90

km 0 + 580.000

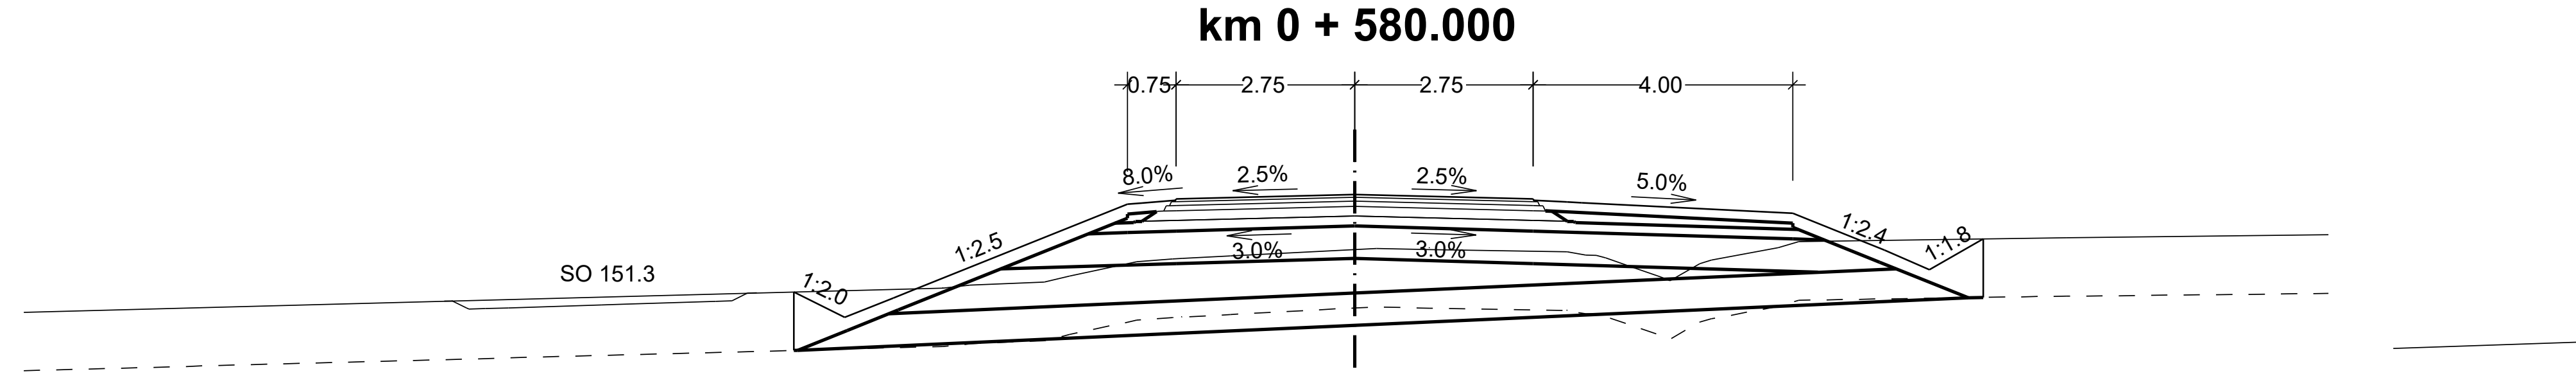

S. R. 216 m

PROJEKTOVANÝ STAV	219.86	218.96	219.46	219.76	219.91	221.20	221.22	221.24	221.26	221.28	221.35	221.28	221.26	221.24	221.24	221.23	221.06	220.64	220.50	220.20	220.67	219.77
ODSAZENÍ OD OSY	-8.64	-8.64	-7.85	-7.10	-6.75	-3.50	-3.27	-2.77	-2.76	-2.75	0.00	2.75	2.76	2.77	3.27	3.50	6.75	7.80	8.16	8.85	9.68	9.68

STÁVAJÍCÍ TERÉN	219.92	219.96	220.01	220.10	220.32	220.36	220.37	220.41	220.51	220.52	220.51	220.47	220.42	220.42	220.38	220.23	220.08	220.03	220.29	220.35	220.54	220.63	220.69
ODSAZENÍ OD OSY	-6.34	-5.92	-4.78	-4.39	-3.35	-2.80	-2.66	-1.92	0.00	0.34	1.15	3.27	3.56	3.72	3.87	4.30	4.72	4.86	5.32	5.50	6.52	6.84	10.97

km 0 + 600.000

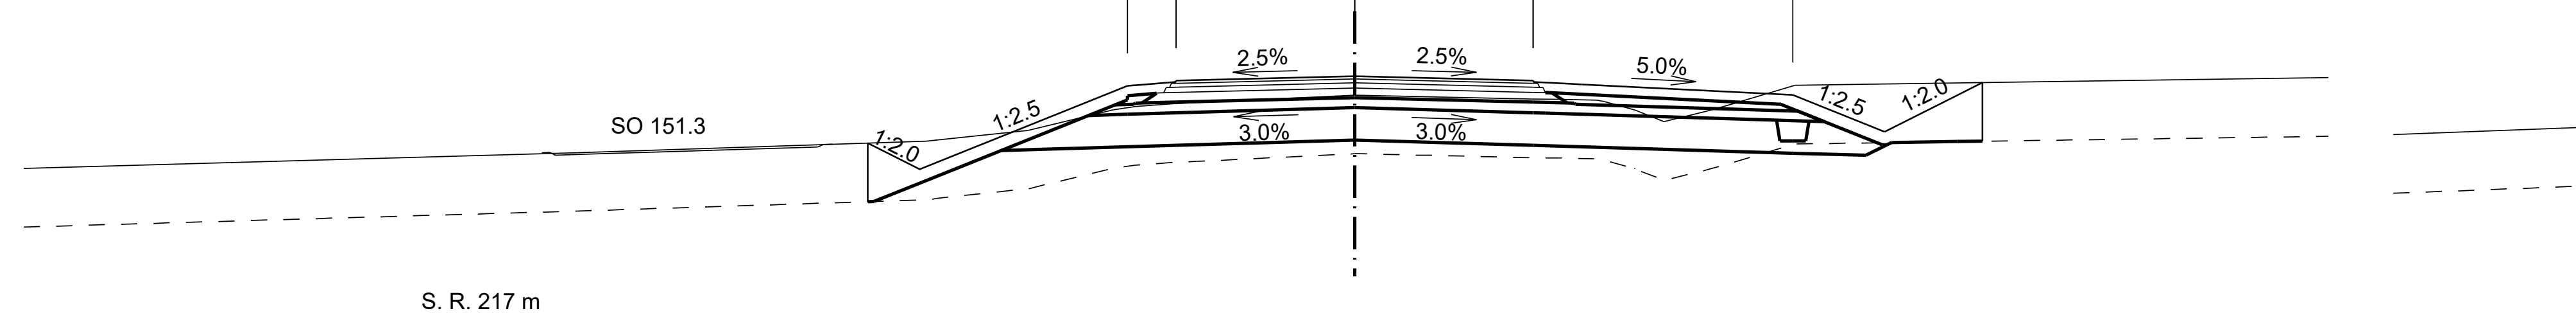

S. R. 217 m

PROJEKTOVANÝ STAV	220.12	219.22	219.72	220.02	220.29	221.00	221.02	221.04	221.06	221.08	221.15	221.08	221.06	221.04	221.04	221.03	220.86	220.30	220.86	221.05	220.15
ODSAZENÍ OD OSY	-7.50	-7.50	-6.70	-5.95	-5.27	-3.50	-3.27	-2.77	-2.76	-2.75	0.00	2.75	2.76	2.77	3.27	3.50	6.75	8.16	9.29	9.67	9.67

STÁVAJÍCÍ TERÉN	219.98	220.15	220.17	220.32	220.64	220.69	220.73	220.74	220.86	220.80	220.79	220.78	220.76	220.63	220.45	220.61	220.70	221.01
ODSAZENÍ OD OSY	-11.98	-6.59	-6.44	-5.03	-3.71	-3.37	-2.80	-2.43	0.00	2.73	3.14	3.73	3.85	4.32	4.76	5.42	5.73	6.78

km 0 + 620.000

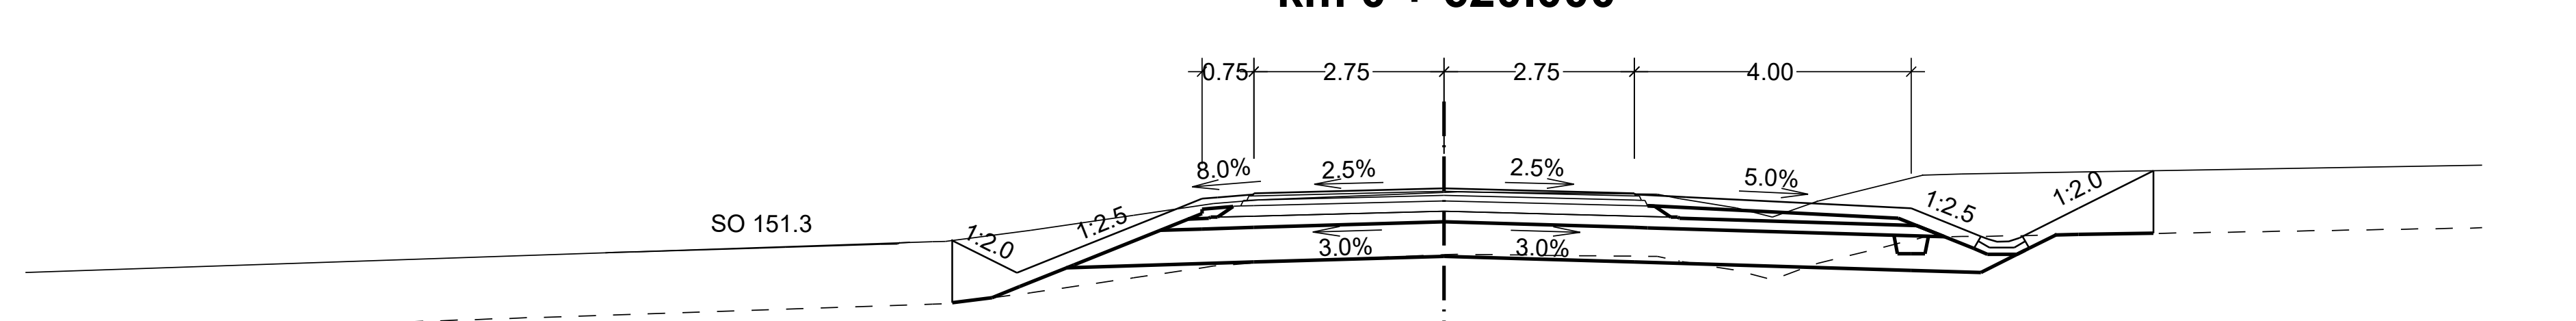

S. R. 217 m

PROJEKTOVANÝ STAV	220.45	219.55	219.98	220.28	220.90	221.05	221.07	221.09	221.11	221.13	221.20	221.13	221.11	221.09	221.09	221.07	220.91	220.51	220.51	220.51	220.91	221.46	220.56
ODSAZENÍ OD OSY	-7.11	-7.11	-6.17	-5.42	-3.88	-3.50	-3.27	-2.77	-2.76	-2.75	0.00	2.75	2.76	2.77	3.27	3.50	6.75	7.76	8.06	8.36	9.17	10.25	10.25

STÁVAJÍCÍ TERÉN	220.43	220.44	220.60	220.81	220.98	221.04	221.14	221.15	221.12	221.05	220.92	220.79	221.02	221.39	221.41
ODSAZENÍ OD OSY	-7.40	-7.21	-5.97	-4.49	-3.34	-2.65	0.00	0.19	3.08	3.40	4.23	4.75	5.40	6.92	7.48

km 0 + 640.000

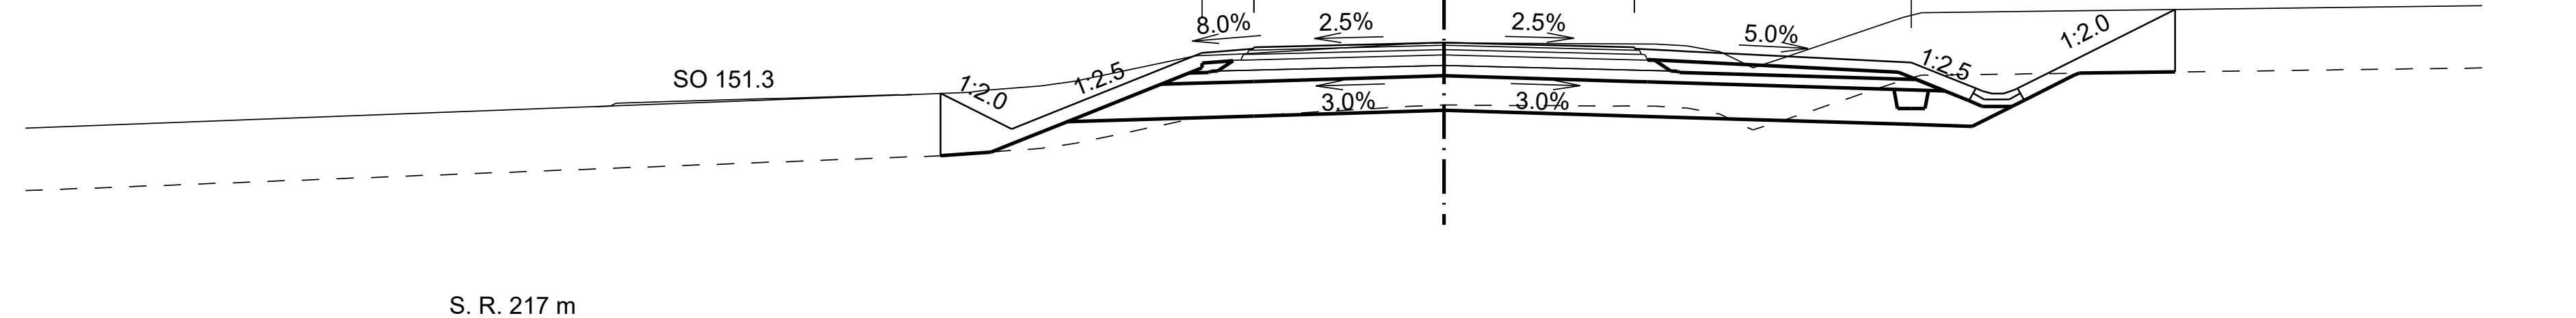

S. R. 217 m

PROJEKTOVANÝ STAV	220.76	219.86	220.24	220.54	221.30	221.34	221.36	221.38	221.40	221.42	221.49	221.42	221.40	221.38	221.38	221.37	221.20	220.83	220.83	220.83	221.20	221.97	221.07
ODSAZENÍ OD OSY	-7.28	-7.28	-6.25	-5.50	-3.62	-3.50	-3.27	-2.77	-2.76	-2.75	0.00	2.75	2.76	2.77	3.27	3.50	6.75	7.69	7.99	8.29	9.03	10.57	10.57

STÁVAJÍCÍ TERÉN	220.77	220.80	220.86	220.93	221.30	221.32	221.33	221.47	221.49	221.48	221.47	221.45	221.38	221.36	221.13	221.28	221.33	221.85	221.92
ODSAZENÍ OD OSY	-6.87	-6.64	-5.83	-5.34	-3.59	-2.93	-2.80	-0.55	-0.03	0.51	3.05	3.50	3.84	3.99	4.46	4.95	5.07	6.63	6.90

Výškový systém: Bpv

SO 121 Přeložka silnice III/2768 v km 2,200

Objednatel:
ŘEDITELSTVÍ SILNIC A DÁLNIC
Ředitelství silnic a dálnic s. p.
Čerčanská 2023/12, Krč, 140 00 Praha 4

Zhotovitel:
Valbek
Valbek, spol. s r.o.
Vaňurova 505/17
460 07 Liberec 3
HIP:
ING. T. KLIMENT

Vypracoval	ING. A. DUMANSKA	Zak. číslo	21-LI13-001
Zodp. projektant	ING. T. KLIMENT	Datum	02/2025
Tech. kontrola	ING. M. HANŽL	Stupeň	PDPS
Akce	I/16 MLADÁ BOLESLAV - MARTINOVICE	Počet formátů	18 x A4
		Měřítko	1 : 100
		Č. přílohy	Paré
Příloha	PŘÍČNÉ ŘEZY km 0,500 - km 0,640	5.3	

Zhotovitel:
Valbek, spol. s r.o.
Vaňurova 505/17
460 07 Liberec 3